Variante E – 12 m und umlaufender Vorbau mit Parken (E1–E4)

VARIANTE E · NICHT FESTGELEGT

Entwurfsstudie Neue Mitte Werlte – Baufeld 3 · überarbeitet 24.10.2026 · keine Variante festgelegt

Ziel: Gebäudehöhe bis 12,00 m planerisch ausnutzen (drei Geschosse, keine zusätzlichen), umlaufender säulengestützter Vorbau, Zufahrt und Stellplätze unter und neben dem Vorbau. Keine Variante ist festgelegt; B3 (Variante A) und alle bestehenden Modelle bleiben unverändert. Alle Flächen sind vorläufig, bis Grundstücksgrenzen und Baugrenzen verlässlich geklärt sind.

	Bestätigt (Quelle)	Annahme / unbestätigt
Grundstück	ca. 960 m² (Projektangabe); amtliche Unterlagen: B-Plan 123, 1. Änderung (Entwurf) mit Baugrenze 3,0 m zu Planstraße/Parkplatz	Zuschnitt 32 × 30 m = Hypothese H1; aus Nutzungskonzept abgeleitete Kandidaten ca. 33 × 25 m / 35 × 27 m (±2 m); Foto-Seiten 13/15/16 fehlen
Höhe / Geschosse	Entwurf B-Plan 123, 1. Änd.: H = 12,00 m über OK Fahrbahn, SH ≤ 0,30 m, TH 6,50 m, zwingend II Vollgeschosse, Dach ≥ 38°; 2–3 Geschosse laut Auftraggeber	Plan nur ENTWURF, Ursprungsplan unbekannt; 12 m gelten erst nach Klärung (Fahrbahnhöhe, Dachform, Vollgeschosse) als eingehalten
Stellplätze Wohnen	KEINE gesetzliche Pflicht seit 01.07.2024 (§ 47 Abs. 1 Satz 3 NBauO; FAQ Land Niedersachsen Stand 11.07.2025)	ob B-Plan/städtebaulicher Vertrag/Kaufvertrag Stellplätze für Wohnungen verlangt: unbekannt
Stellplätze Gastro/Büro	Pflicht besteht; Bemessung bedarfsorientiert (Richtzahlen Erlass: Gaststätte 1 je 8–12 Sitzplätze, Büro 1 je 30–40 m²)	Gaststättenart („örtliche Bedeutung“) und Sitzplatzzahl angenommen
Maße	–	Stellplatz 2,50 × 5,00 m, Fahrgasse 6,00 m, Säule Ø 0,40 m (Vorgaben/Annahmen), Zufahrtslage
Wohnfläche	B3: 846 m², 16 WE (Plan)	übrige Varianten aus Geschosskonturen geschätzt (0,88 × Wohnstreifen)

Grundstück, Baugrenzen und Quellenstatus

VARIANTE E · NICHT FESTGELEGT

Was gesichert ist, was nur aus Beschreibungen stammt und was Hypothese ist


Punkt	Stand	Herkunft / Bemerkung
Grundstücksfläche ca. 960 m²	GESICHERT (Projektangabe)	Projektunterlagen/Auftraggeber; nicht am Liegenschaftsnachweis geprüft
Zuschnitt 32 × 30 m	HYPOTHESE H1	Nur aus 960 m² und B3-Annahme; weder vermessen noch aus einem Plan gemessen
B-Plan Nr. 123 „Ehemalige Grundschule“, 1. Änderung (Entwurf 25.09.2026): MI, GRZ 0,6, II zwingend, TH 6,50 m, H 12,00 m, SH 0,30 m, Baugrenze 3 m	GESICHERT (Entwurf)	amtliche Unterlagen der Stadt Werlte (sgwerlte.de), in quellen_stadt/ abgelegt; nicht rechtskräftig
Foto-Seiten 13/15/16 des Auftraggebers („zwei- bis dreigeschossig“)	FEHLEN	ZIP nicht angekommen; Seite 15/16 entsprechen vermutlich Abb. 2/3 der 1. Änderung (unbestätigt)
Zuordnung „Baufeld 3“ im Nutzungskonzept	UNBEKANNT	ohne Seite 13 nicht bestimmbar; Kandidaten K1/K2 abgeleitet
Baugrenzen / Baulinien, GRZ, Abstandsflächen	UNBEKANNT	keine Maße am Plan abgelesen; alle Konturen in den Plänen sind Hypothese
Erschließungsstraße, Zufahrt, Platzseite	ANNAHME	Platz an der Seite y = 0; Zufahrt von Osten (E) bzw. Süden (F) angenommen
Stellplatz 2,50 × 5,00 m, Fahrgasse 6,00 m	ANNAHME (Auftraggeber, vorläufig)	Abgleich mit Stellplatzsatzung/Garagenverordnung ausstehend

Die ZIP-Datei mit den Fotos der Seiten 13, 15 und 16 ist in dieser Sitzung nicht angekommen; der Ordner quellen_stadt/fotos_stadt_unterlagen/ ist leer. Grundlage sind die amtlichen Planunterlagen der Stadt (Entwurf B-Plan 123, 1. Änderung). Konturen aus den Plänen sind als ABGELEITET (±2 m) gekennzeichnet, gesicherte Maße getrennt.

Planungsrecht: Höhe 12,00 m und ihr Bezugspunkt

GRUNDSTÜCK · TEILWEISE ABGELEITET

B-Plan Nr. 123, 1. Änderung, Entwurf (Textliche Festsetzung 1.2) · Antwort auf: verbindlich festgesetzt? von wo gemessen?

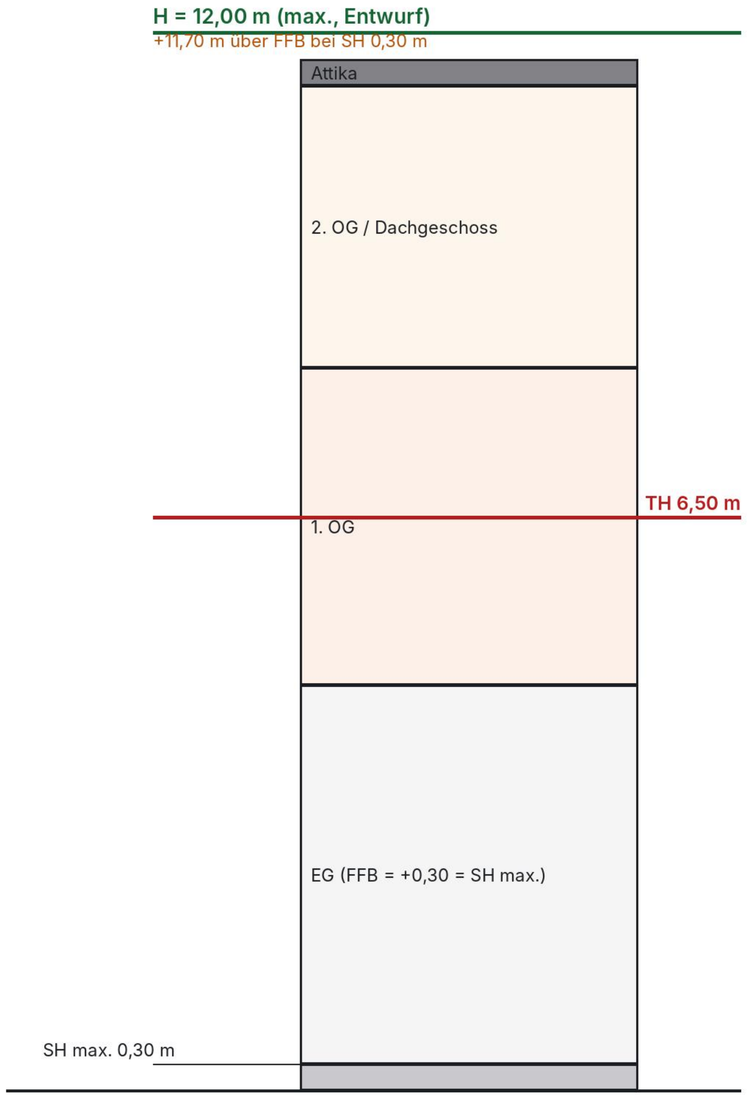


Frage	Antwort
Ist 12 m verbindlich festgesetzt?	Im ENTWURF der 1. Änderung (H = 12,00 m). Satzungsbeschluss steht aus; der rechtskräftige Ursprungsplan 123 (14.04.2023) liegt nicht vor. → Nicht als verbindlich nachgewiesen.
Von wo gemessen?	Unterer Bezugspunkt: Oberkante Fahrbahn der nächstgelegenen ausgebauten Erschließungsstraße in der Mitte vor dem Baukörper (Höhe beim Bauamt erfragbar). Oberer Punkt: Oberkante Baukörper (First, Hauptgesims); untergeordnete Teile (Antennen, Schornsteine) zählen nicht.
Verhältnis zu FFB EG	FFB EG max. 0,30 m über dem Bezugspunkt (SH). Bei SH 0,30 m: Baukörper max. +11,70 m über FFB; E/F zeichnen +12,00 m über FFB → bei SH > 0 überschritten, nur bei FFB = Fahrbahnhöhe möglich.
Traufhöhe	max. 6,50 m (Schnittkante Mauerwerk/Dachhaut): Oberkante 1. OG der Entwürfe (+7,90 / +8,20 m) liegt darüber.
Vollgeschosse / Dach	II zwingend; Hauptdach geneigt ≥ 38° (Flachdach nur Verbindungsbauten, ≥ 1,0 m unter First, bzw. untergeordnete Teile ≤ 70 m²). Dreigeschossige Flachdachbauten (B3, B, C, E, F) passen nicht zum Entwurf.
Fazit	Die 12,00 m bleiben Planungsziel, gelten aber erst als eingehalten, wenn (1) Ursprungsplan/Satzung für Baufeld 3 vorliegt, (2) Fahrbahnhöhe vor dem Baukörper bekannt ist, (3) Traufe/Dachform/Vollgeschosse geklärt sind.

Abgeleitete Grundstückskonturen (Näherung aus dem Nutzungskonzept)

GRUNDSTÜCK · TEILWEISE ABGELEITET

Blau: Kandidat K1, grün: Kandidat K2, orange: Baufenster K1 (3 m Abstand) · Maßstabsabgriff aus Abb. 3, ±2 m · KEINE vermessenen Grenzen

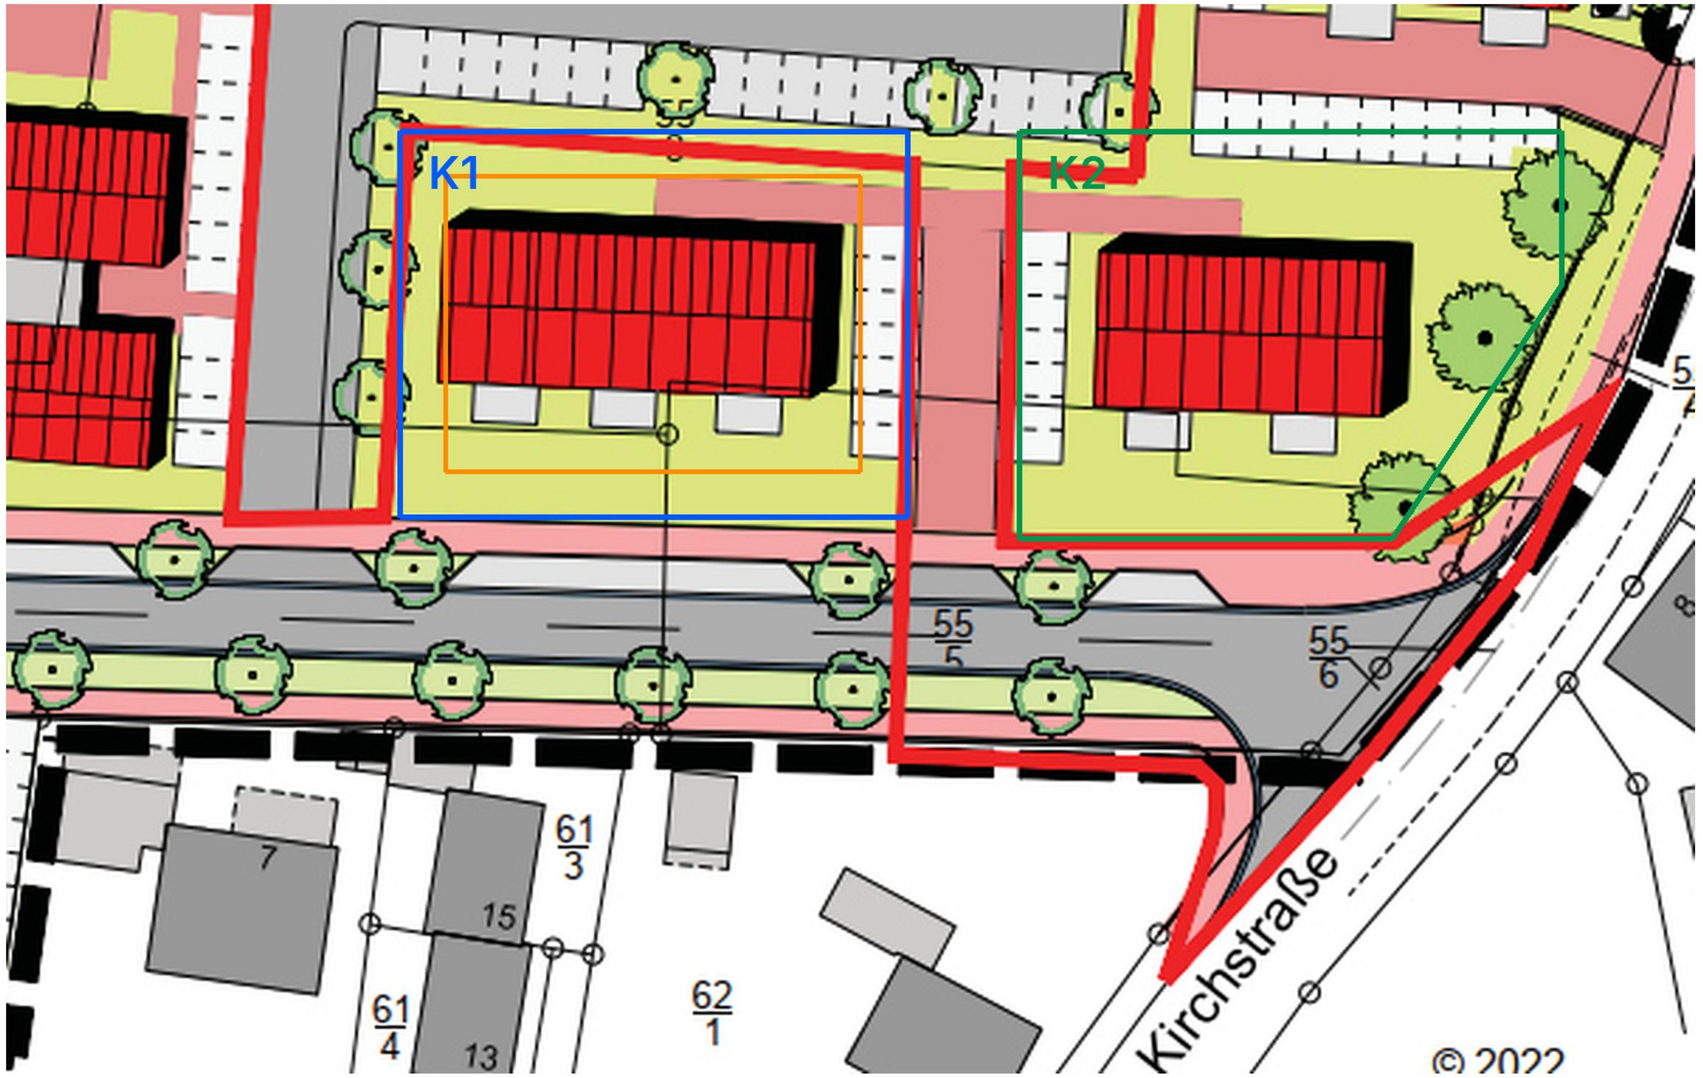

Ableitung: Maßstab 1:1000 der Abbildung; Straßenbreite Planstraße 16 m und Stichstraße/Parkplatz-Arm 11 m dienten als Kontrolle. Die grünen Flächen zwischen Planstraße (Süden), Parkplatz (Norden), Stichstraße (Westen) und Fuß-/Radweg (Osten) sind als Baufelder abgegrenzt; Parzellengrenzen sind in der Abbildung nicht eingezeichnet.


K1: ca. 33 × 25 m ≈ 830 m². K2: ca. 35 × 27 m ≈ 900 m² (Trapez). Die Projektangabe 960 m² passt zu keinem der beiden genau; Baufeld 3 kann also ein anderes Baufeld sein oder Teile der angrenzenden Wege einschließen. Die Zuordnung erfordert Seite 13/15/16 des Auftraggebers.

Baugrenzen (Entwurf): 3,0 m Abstand zu Planstraße und Parkplatz (gesichert); Ost/West angenommen. Baufenster K1 ≈ 27 × 19 m = 513 m².

Lageplan Kandidat K1: Baufenster und Gebäudefußabdrücke

GRUNDSTÜCK · TEILWEISE ABGELEITET

Maße in m, Näherung ±2 m · Baugrenze N/S 3,0 m gesichert, W/O 3,0 m angenommen · Parken auf eigener Fläche nach Fußabdruck

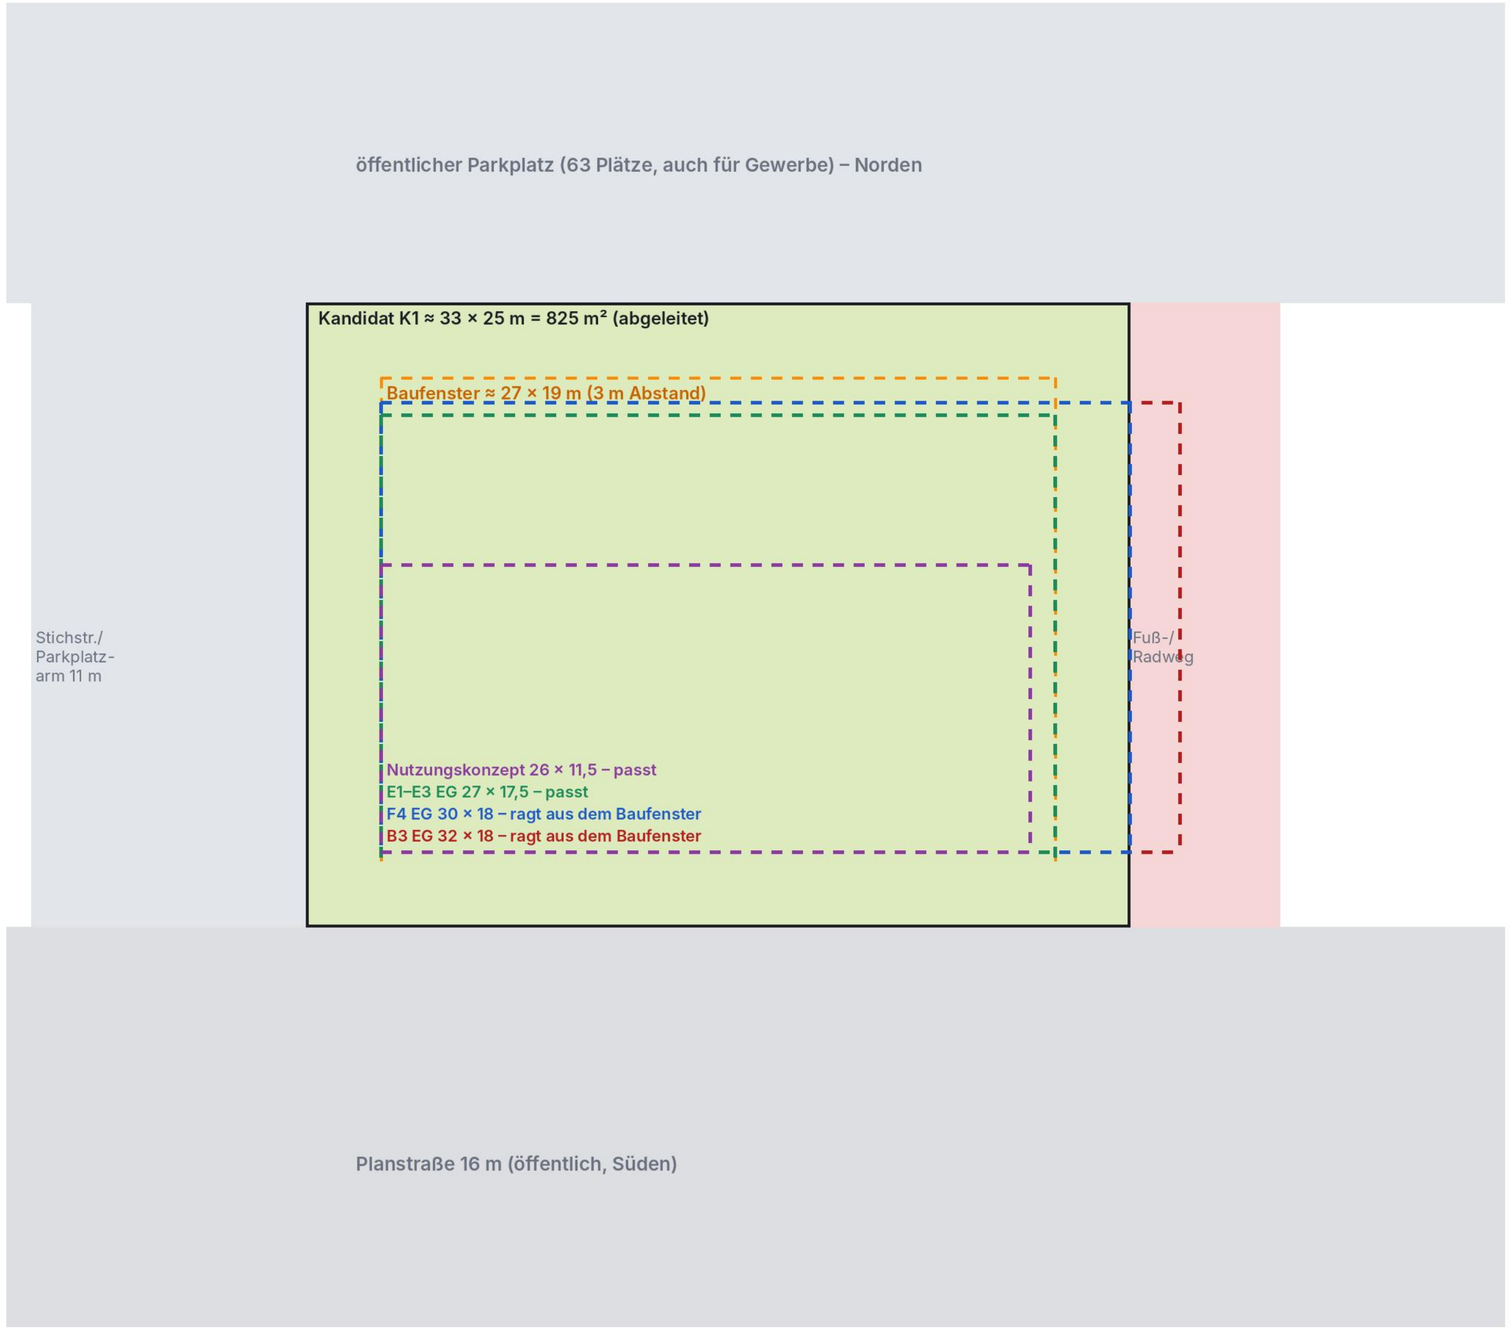

Fußabdruck	Baufenster K1 27 × 19	Baufenster K2 ≈ 29 × 21
B3 / A, B, C, D: EG 32 × 18 m	passt NICHT	passt NICHT
E1–E3: EG 27 × 17,5 m	passt	passt
E4: EG 27 × 12,5 m	passt	passt
F1–F3: EG 18 × 30 m (30 m tief)	passt NICHT	passt NICHT
F4: EG 30 × 18 m	passt NICHT	passt NICHT
Nutzungskonzept (Abb. 3): ca. 26 × 11,5 m	passt	passt


Befund (unter dem Vorbehalt der Kandidatenwahl): Der Entwurf B3 (EG 32 × 18 m, 576 m²) passt in keines der beiden Baufenster. F mit 540 m² passt nur in der gedrehten Lesart (30 × 18 m) und nur bei breiterem Baufenster; die wörtliche Lesart 18 × 30 m (30 m tief) passt nicht. Umlaufender Vorbau über die Baugrenze und Parken unter dem Vorbau auf eigener Fläche sind auf den abgeleiteten Grundstücken nicht möglich. Stellplätze für Gastro/Büro müssten über den öffentlichen Parkplatz (63 Plätze, Baulast/Mitnutzung ungeklärt) oder die vom Nutzungskonzept vorgesehenen privaten Stellplätze neben den Gebäuden nachgewiesen werden.

Parken auf K1: nach Abzug von Baufenster und Baugrenzstreifen (3 m) bleiben ≤ 3–4,5 m Tiefe → keine 5-m-Stellplätze mit Fahrgasse; allenfalls Längsparker im Südstreifen (Ausfahrt über Gehweg ungeklärt).

Höhenrahmen: B3 (+9,90 m) gegen 12,00 m – mit Bezugspunkt nach Entwurf B-Plan 123, 1. Änderung

VARIANTE E · NICHT FESTGELEGT

Schnittschema und Raumhöhen · alle Höhen vorläufig · 12,00 m gelten erst nach Klärung des Bezugspunkts als eingehalten

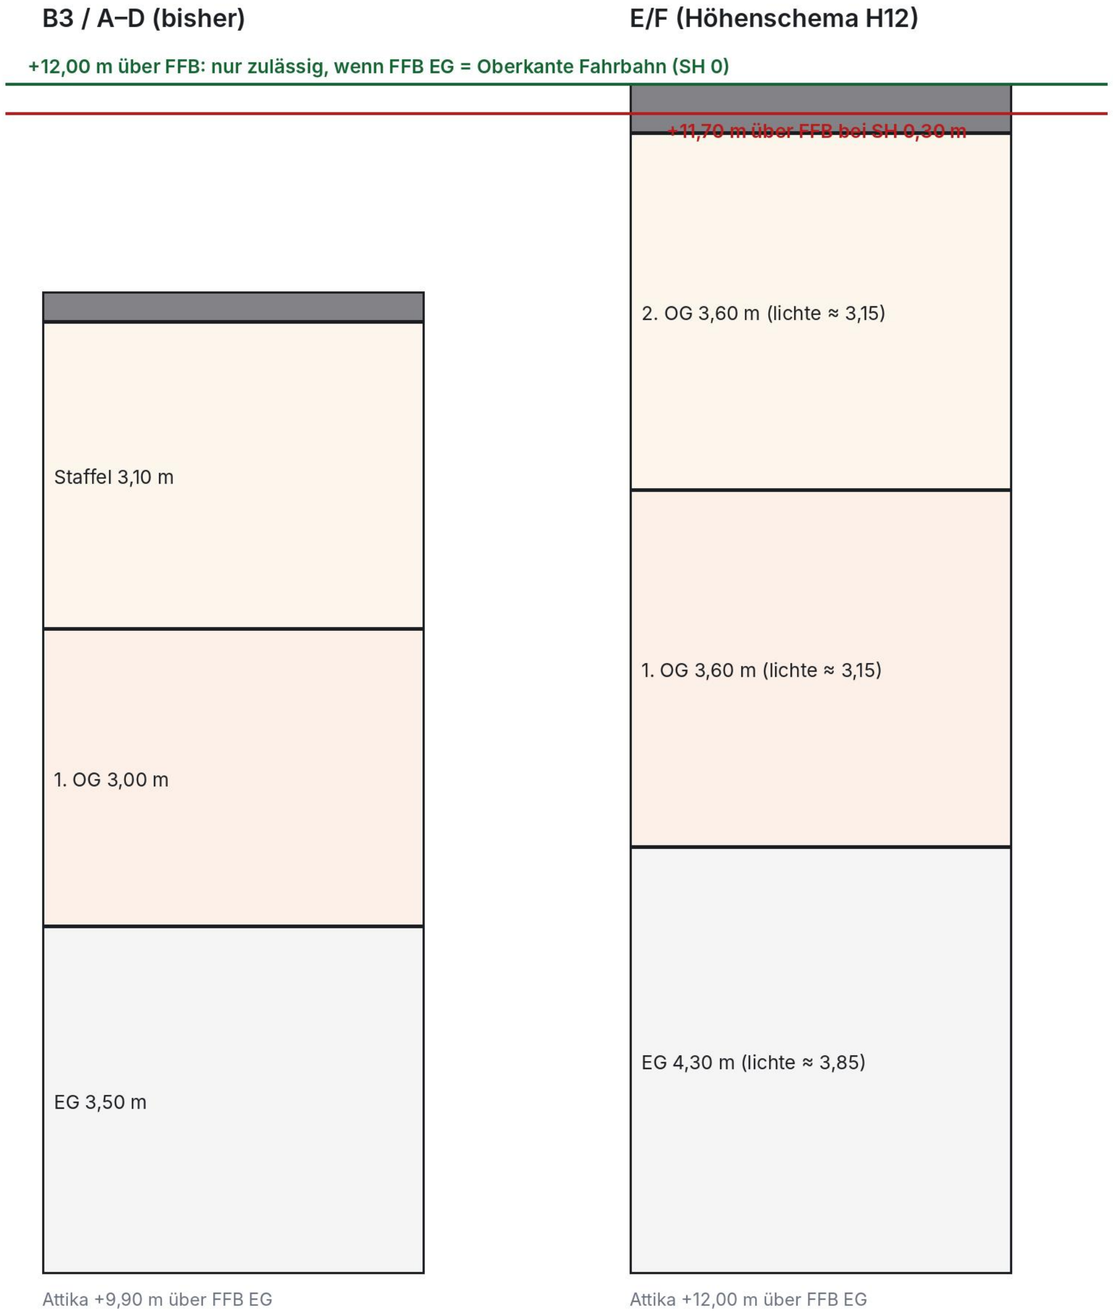

Aspekt	Aussage (Quelle: B-Plan Nr. 123, 1. Änderung, Entwurf 25.09.2026)
Bezugspunkt	H = 12,00 m über Oberkante Fahrbahn der nächstgelegenen ausgebauten Erschließungsstraße in der Mitte vor dem Baukörper (nicht über FFB). FFB EG max. 0,30 m darüber (SH). Fahrbahnhöhe unbekannt.
Rechtsstand	Entwurf; Ursprungsplan 123 (rechtskräftig 14.04.2023) liegt nicht vor. 12 m daher NICHT als verbindlich nachgewiesen.
Folge für E/F	Attika +12,00 m über FFB ist bei SH > 0 zu hoch (+11,70 m max.). Alternative H11,70: EG 4,10 / OG 3,55 / OG 3,55 / Attika 0,50.
Traufhöhe / Dach	TH max. 6,50 m, geneigtes Dach ≥ 38°, zwingend II Vollgeschosse (Entwurf): dreigeschossige Flachdachbauten passen nicht dazu.
Nutzung der Reserve	Statt eines vierten Geschosses (nicht angenommen) fließt die Höhe in Geschosshöhen (lichte ≈ 3,15 m); Wohnfläche steigt dadurch nicht.

Überblick E1–E4

VARIANTE E · NICHT FESTGELEGT


Standardmix · alle Werte vorläufig · Referenz B3 (A)

Kennzahl	A B3	E1 Vorbau bis Attika (Staffel dec	E2 Staffel 1,50 m zurück	E3 Staffel 3,00 m zurück	E4 zweireihiges Parken, kleineres
Staffelrücksprung	0,8 m	0.0 m	1.5 m	3.0 m	1.5 m
Grundfläche EG / 1. OG / 2. OG (m²)	576 / 660 / 539	492 / 768 / 768	492 / 768 / 609	492 / 768 / 468	358 / 608 / 464
Wohnfläche netto (m²)	846	1.084	960	852	727
Δ Wohnfläche gg. A	±0	+238 (+28 %)	+114 (+13 %)	+6 (+1 %)	-119 (-14 %)
Wohnungen	16	18	16	15	16
Gastraum (m²) / Plätze innen	280 / 120	281 / 120	281 / 120	281 / 120	198 / 85
Stellplätze gezeichnet / nutzbar	11 / 11	9 / 9	9 / 9	9 / 9	21 / 21
erforderlich § 47 (Spanne / Mittel)	11,4–16,9 / 13,6	11,4–16,9 / 13,6	11,4–16,9 / 13,6	11,4–16,9 / 13,6	8,5–12,5 / 10,1
optional Wohnen (0,5–1,5 je WE)	8–24	9–27	8–24	8–22	8–24
Säulen	0	22	22	22	20
Höhe Attika	9,90 m	12,00 m (Bezug offen)	12,00 m (Bezug offen)	12,00 m (Bezug offen)	12,00 m (Bezug offen)

E1 – Vorbau bis Attika (Staffel deckungsgleich)

Entwurfsstudie Baufeld 3 · Konzeptvariante, keine Genehmigungsplanung

VARIANTE E · NICHT FESTGELEGT

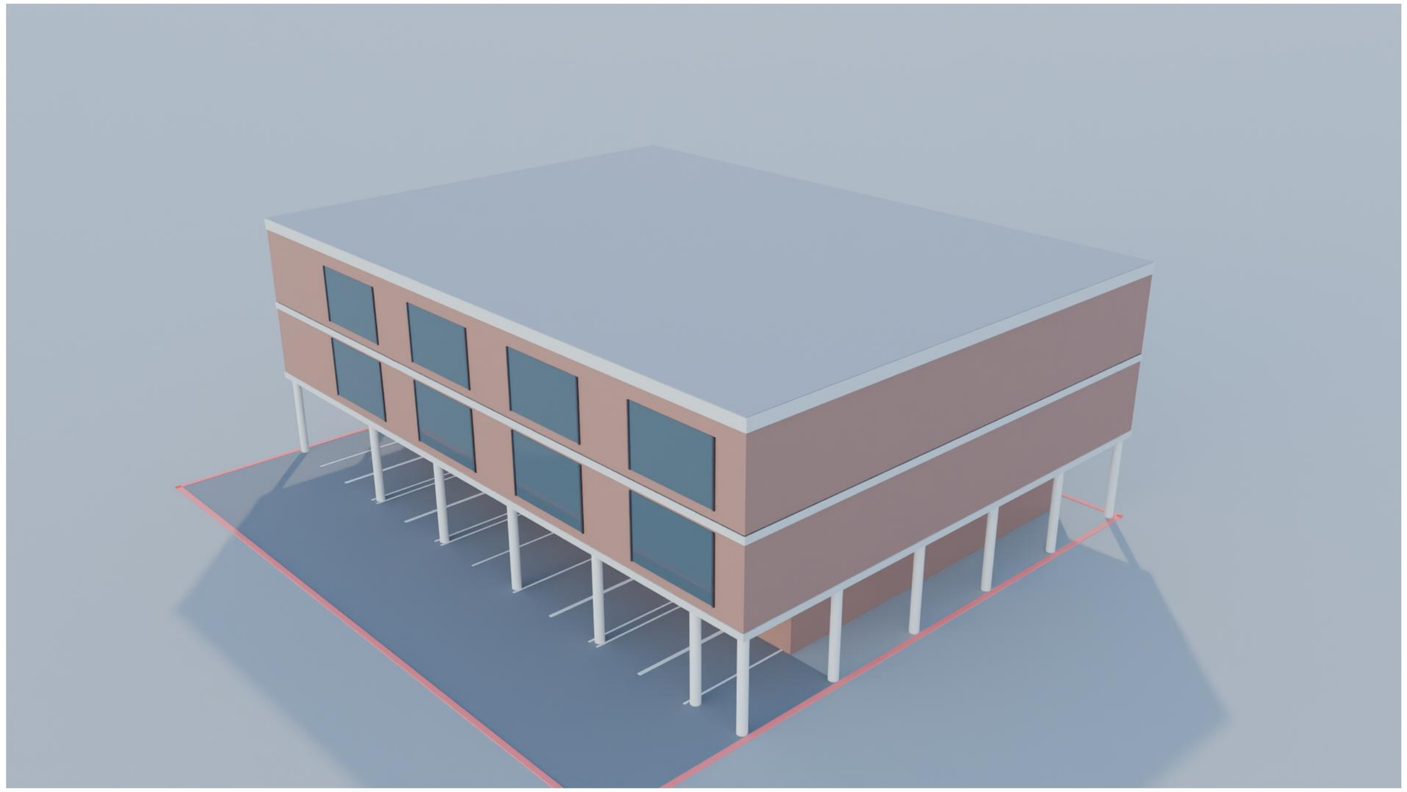

12,00 m Gesamthöhe, drei Geschosse; 1. und 2. OG kragen auf allen vier Seiten über das Erdgeschoss (vorn 1,50 m Arkade, seitlich 2,50 m, hinten 5,00 m über der Stellplatzreihe) und sind deckungsgleich bis zur Attika; Säulen am Rand.

Kennzahl	Wert (vorläufig)
Höhe	12,00 m Attika (EG 4,30 · 1. OG 3,60 · 2. OG 3,60 · Dach/Attika 0,50), 3 Geschosse – Höhenbezug offen
Grundfläche EG / 1. OG / 2. OG	492 / 768 / 768 m²
Außenmaße EG / 1. OG / 2. OG	29.5 × 17.5 / 32.0 × 24.0 / 32.0 × 24.0 m
Wohnfläche netto (geschätzt)	1.084 m²
Wohnungen Standardmix	18 WE (9 + 9), 54–68 m², Ø 60 m²
Gewerbe	EG 492 m²; Gastraum ca. 281 m² (≈ 120 Plätze), Terrasse/Arkade ≈ 28 Plätze, Büro 56 m²
Säulen	22 Säulen Ø 0,40 m; Paare 5,4 m (zwei Stellplätze + Säule)
Stellplätze gezeichnet	9: 9 voll nutzbar, 0 eingeschränkt, 0 Konflikt
Stellplätze erforderlich (§ 47 NBauO)	11,4–16,9, Mittel 13,6 (nur Gastro + Büro; Wohnen 0)
Stellplätze optional (Komfort/Markt)	Wohnen 0,5–1,5 je WE = 9–27; Komfortziel gesamt ≈ 32
Überstand über Grundstück H1	0,00 m

Alle Maße sind Planungsannahmen: Stellplatz 2,50 × 5,00 m, Fahrgasse 6,00 m, Säule Ø 0,40 m, Grundstück 32 × 30 m (Hypothese; die städtischen Unterlagen Seite 13/15/16 liegen nur als Beschreibung vor, nicht als Foto), Zufahrt = Annahme. Wohnfläche = 0,88 × Wohnstreifen, schematisch. Nichts ist genehmigt, bemessen oder abgestimmt.


E1: Lageplan mit Gebäude, Säulen, Zufahrt und Stellplätzen

VARIANTE E · NICHT FESTGELEGT

E1 – Vorbau bis Attika (Staffel deckungsgleich) · grün = Stellplatz funktioniert, orange = eingeschränkt, rot = Konflikt, rosa = nur rechnerisch verbleibende Fläche

Lageplan E1 – Gebäude, Säulen, Zufahrt, Stellplätze

Grundstück H1 32 × 30 m HYPOTHETISCH (Zuschnitt/Baugrenzen nicht belegt) · Stellplatz 2,50 × 5,00 m, Fahrgasse 6,00 m = Planungsannahmen · Zufahrt = Annahme

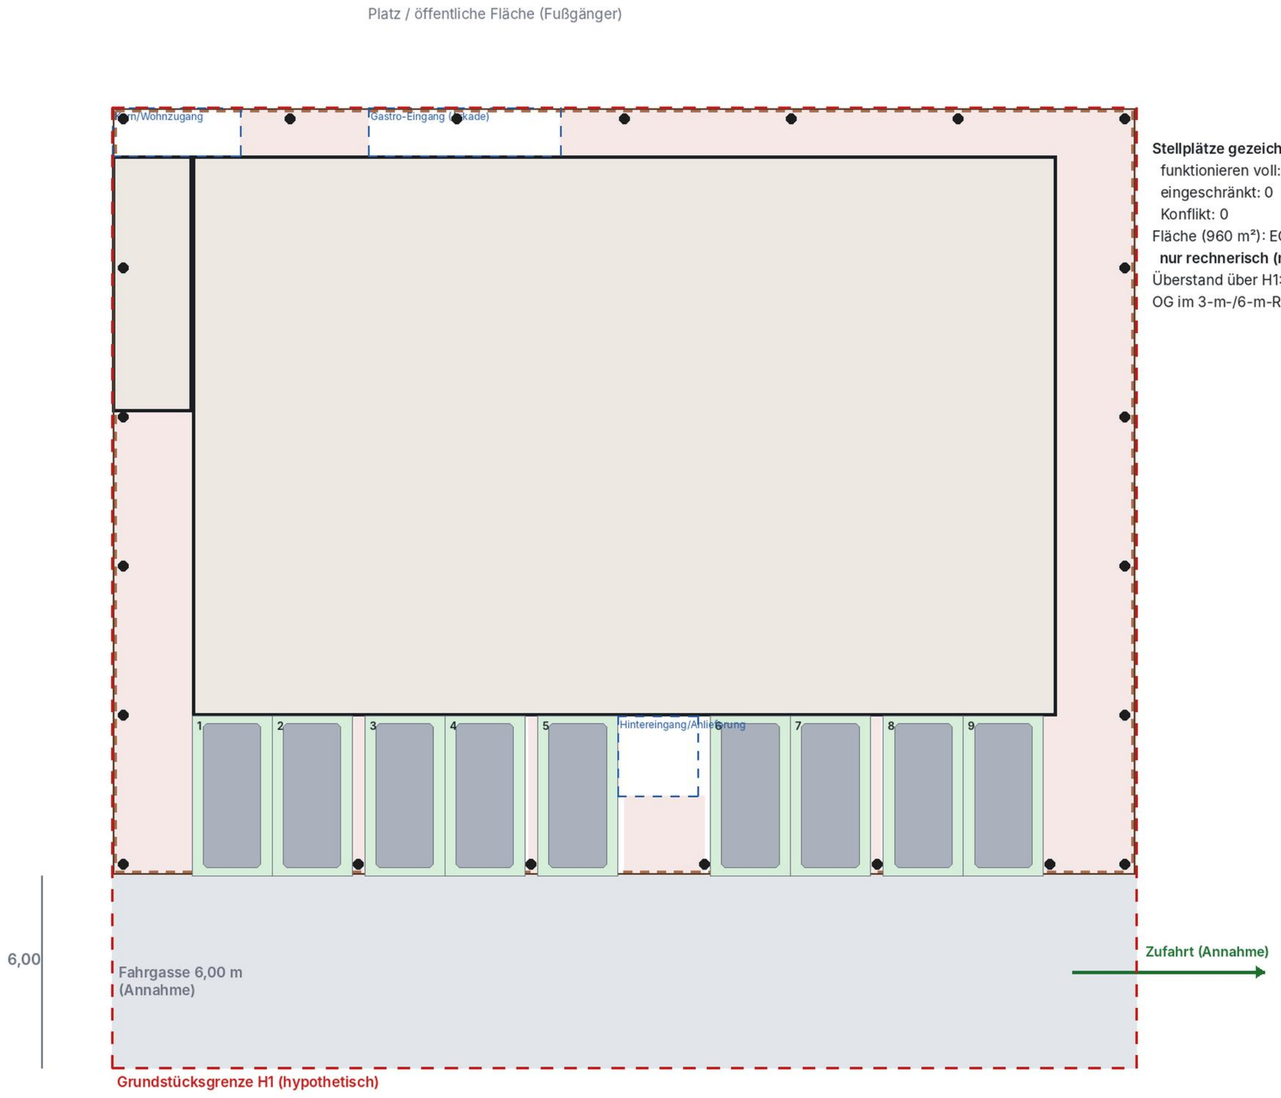

Stellplätze gezeichnet: 9
funktionieren voll: 9
eingeschränkt: 0
Konflikt: 0
Fläche (960 m²): EG 492 · Stellpl. 112 · Fahrgasse 192 · Zugänge 21
nur rechnerisch (nicht nutzbar): 142 m²
Überstand über H1: 0.00 m
OG im 3-m-/6-m-Randstreifen: 222 / 408 m²

Stellplatzprüfung	
Gezeichnet	9
funktionieren voll	9
eingeschränkt	0
Konflikt	0
Min. Nutzbreite 90°	2.50 m
Fahrgasse	6.0 m (frei)
Flächenbilanz 960 m²	
Erdgeschoss	492,5 m²
Stellplätze	112,5 m²
Fahrgasse	192,0 m²
Zugangszonen	21,2 m²
nur rechnerisch	141,8 m²

- Geometrische Prüfung ohne Schleppkurven; 90°-Stellplätze 2,50 × 5,00 m und Fahrgasse 6,00 m sind Planungsannahmen
- Zufahrt (Lage der Straße) ist Annahme
- Feuerwehrzufahrt/Aufstellflächen unter dem Vorbau nicht nachgewiesen (Prüfbedarf)

Stellplatz funktioniert · eingeschränkt · Konflikt · Fahrgasse · nur rechnerisch verbleibend

braun gestrichelt: 1./2. OG über dem EG (Vorbau) · blau gestrichelt: Eingangszonen


E1: Grundrisse EG, 1. OG, 2. OG

E1 – Vorbau bis Attika (Staffel deckungsgleich) · schematisch

VARIANTE E · NICHT FESTGELEGT

Erdgeschoss


E1: Erdgeschoss (schematisch)
Grundriss schematisch · Wohnungsaufteilung = Streifenmodell (Mittelgang 2,0 m), netto = 0,88 × brutto · Säulen Ø 0,40 m · Grundstück H1 hypothetisch

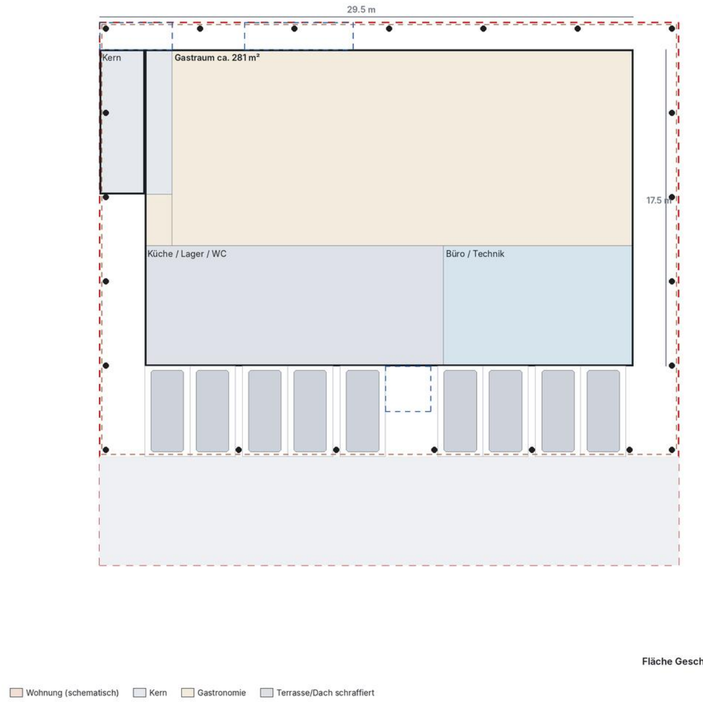

Fläche Geschoss 492 m²

1. Obergeschoss


E1: 1. Obergeschoss (schematisch)
Grundriss schematisch · Wohnungsaufteilung = Streifenmodell (Mittelgang 2,0 m), netto = 0,88 × brutto · Säulen Ø 0,40 m · Grundstück H1 hypothetisch

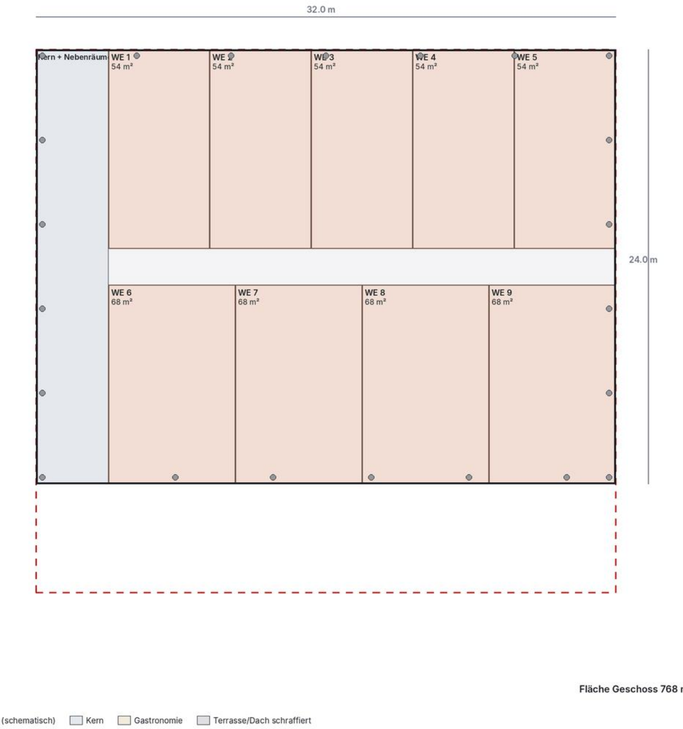

Fläche Geschoss 768 m²

2. Obergeschoss

E1: 2. Obergeschoss (schematisch)
Grundriss schematisch · Wohnungsaufteilung = Streifenmodell (Mittelgang 2,0 m), netto = 0,88 × brutto · Säulen Ø 0,40 m · Grundstück H1 hypothetisch

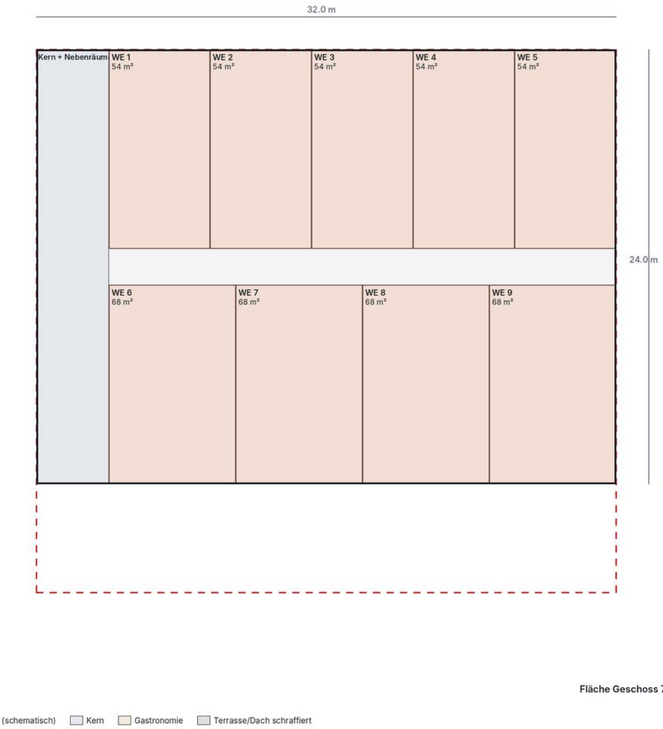

Fläche Geschoss 768 m²

Wohnung (schematisch) Kern Gastronomie Terrasse/Dach schraffiert

E1: vier Fassaden


VARIANTE E · NICHT FESTGELEGT

E1 – Vorbau bis Attika (Staffel deckungsgleich) · orthogonale Ansichten aus dem 3D-Modell

Vorderfassade (Platzseite)



Rückfassade

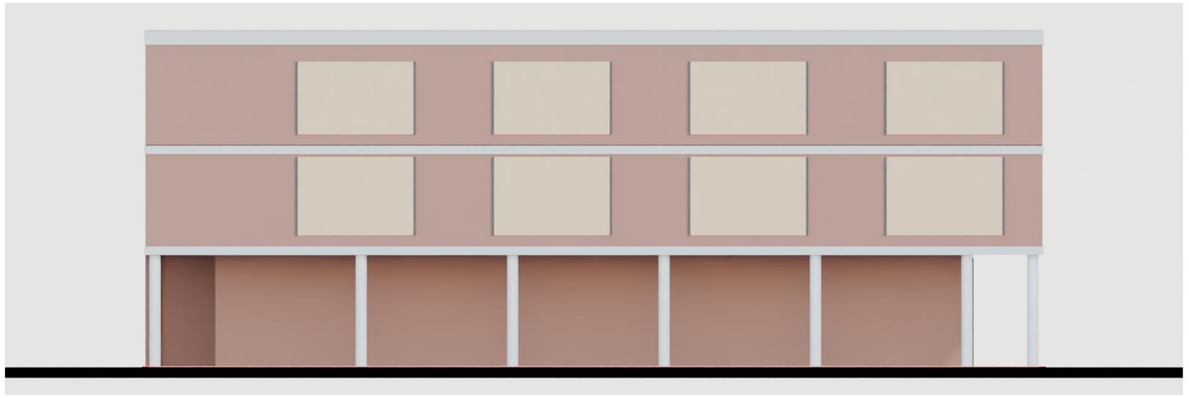

Seitenfassade West



Seitenfassade Ost



E1: Gebäudeschnitt mit Geschosshöhen und 3D-Ansichten

VARIANTE E · NICHT FESTGELEGT


E1 – Vorbau bis Attika (Staffel deckungsgleich)


E1: Gebäudeschnitt mit Geschosshöhen (schematisch)

Platzseite links, Rückseite rechts · Schnitt bei x = 16.25 m · Höhenbezug ±0,00 = OK Fertigfußboden EG (Planbezug Blatt 14) – Bezugspunkt der Stadt für die 12,00 m ist NICHT belegt



Geschosshöhen: EG 4,30 m · 1. OG 3,60 m · 2. OG 3,60 m · Dach/Attika 0,50 m = 12,00 m. Reserve 0,00 m. Die 12,00 m gelten erst als eingehalten, wenn der baurechtliche Höhenbezug geklärt ist.
Säulen im Schnittbereich: 2 · Säulen insgesamt: 22 · Vorbau-Unterkante +4,00 m (Decke 0,30 m)

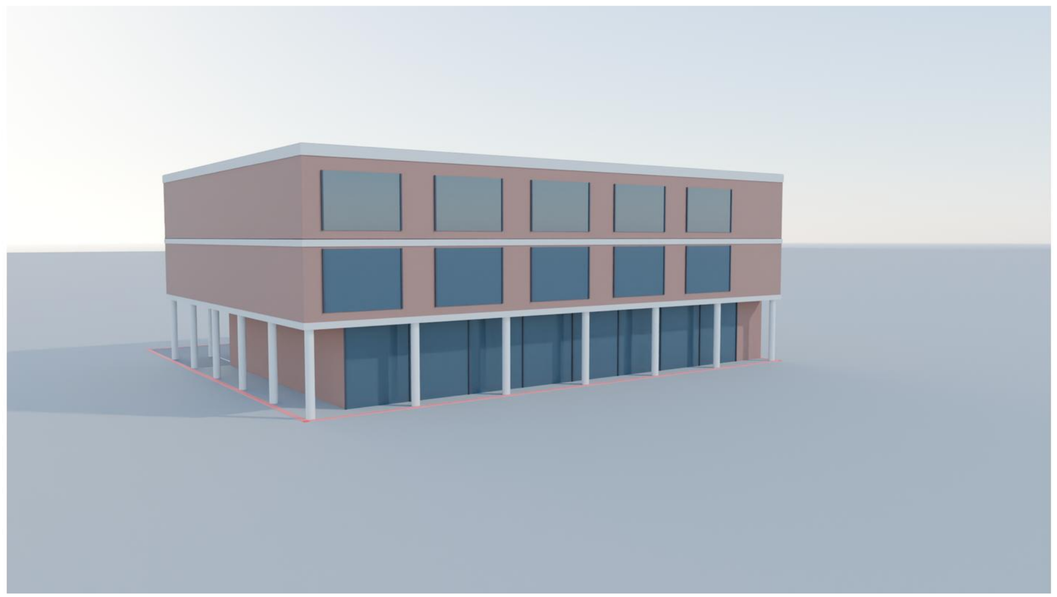


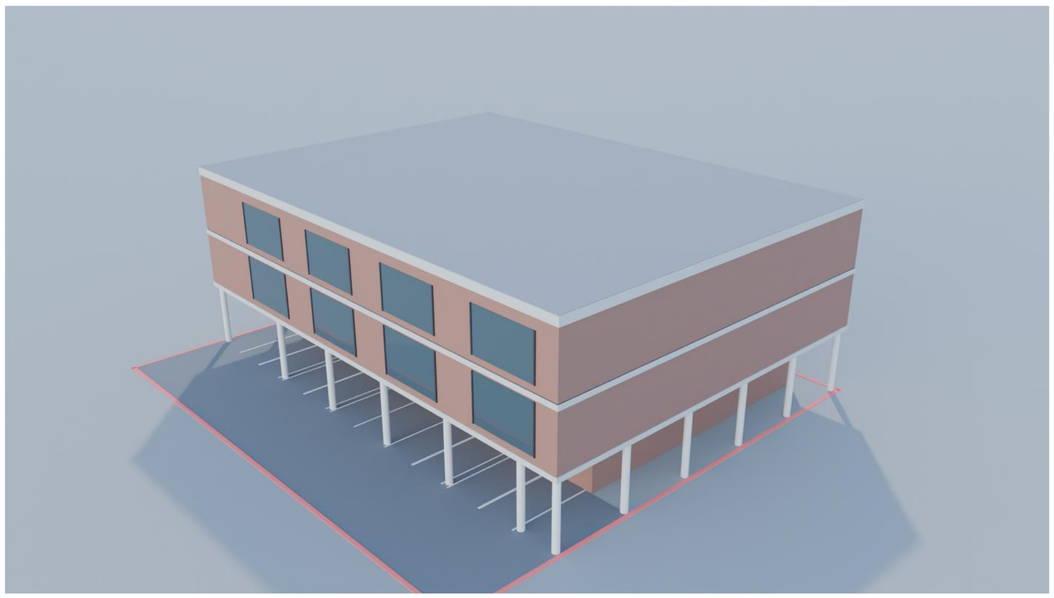

E2 – Staffel 1,50 m zurück

Entwurfsstudie Baufeld 3 · Konzeptvariante, keine Genehmigungsplanung

VARIANTE E · NICHT FESTGELEGT

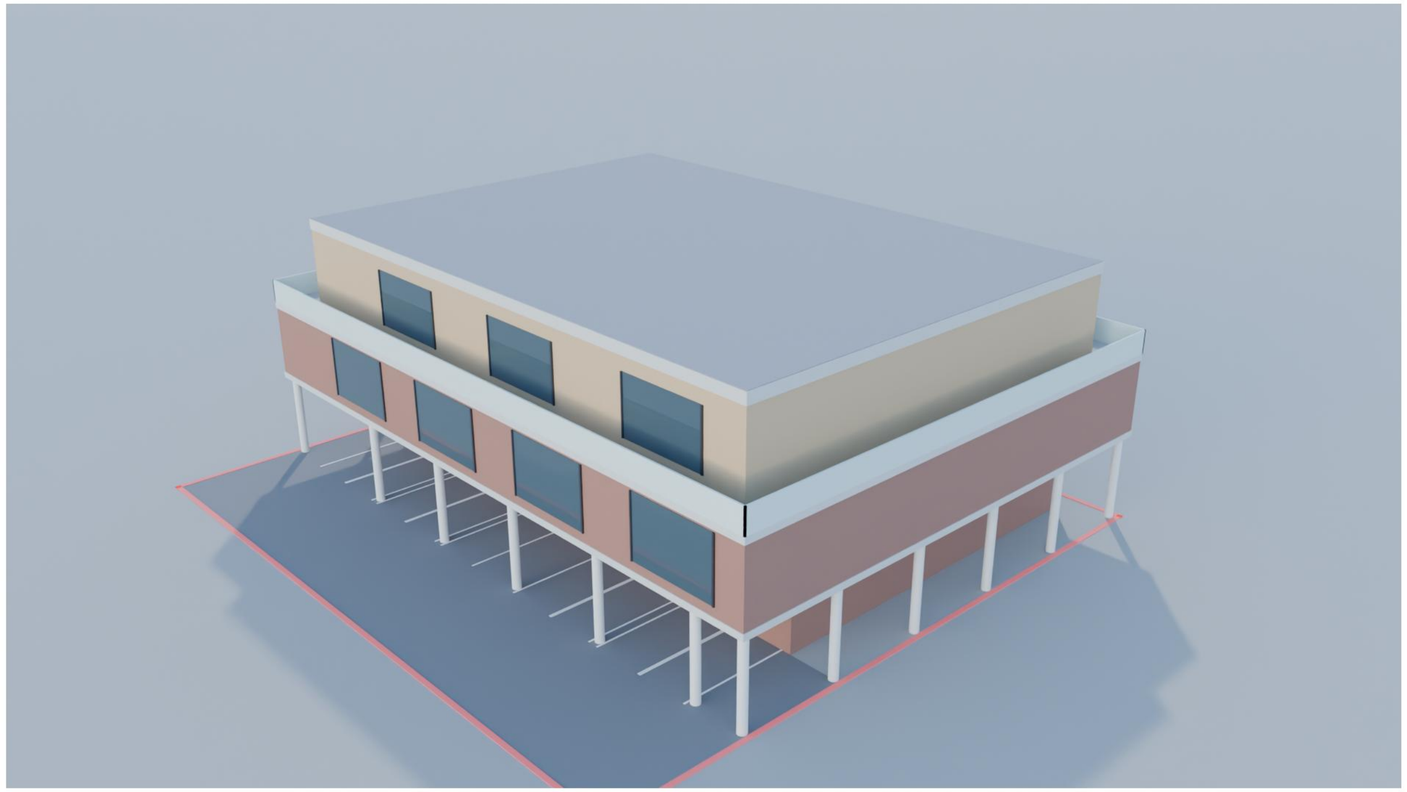

Wie E1, das 2. OG springt rundum 1,50 m hinter die Kante des 1. OG zurück (umlaufende Dachterrasse).

Kennzahl	Wert (vorläufig)
Höhe	12,00 m Attika (EG 4,30 · 1. OG 3,60 · 2. OG 3,60 · Dach/Attika 0,50), 3 Geschosse – Höhenbezug offen
Grundfläche EG / 1. OG / 2. OG	492 / 768 / 609 m²
Außenmaße EG / 1. OG / 2. OG	29.5 × 17.5 / 32.0 × 24.0 / 29.0 × 21.0 m
Wohnfläche netto (geschätzt)	960 m²
Wohnungen Standardmix	16 WE (9 + 7), 52–70 m², Ø 60 m²
Gewerbe	EG 492 m²; Gastraum ca. 281 m² (≈ 120 Plätze), Terrasse/Arkade ≈ 28 Plätze, Büro 56 m²
Säulen	22 Säulen Ø 0,40 m; Paare 5,4 m (zwei Stellplätze + Säule)
Stellplätze gezeichnet	9: 9 voll nutzbar, 0 eingeschränkt, 0 Konflikt
Stellplätze erforderlich (§ 47 NBauO)	11,4–16,9, Mittel 13,6 (nur Gastro + Büro; Wohnen 0)
Stellplätze optional (Komfort/Markt)	Wohnen 0,5–1,5 je WE = 8–24; Komfortziel gesamt ≈ 30
Überstand über Grundstück H1	0,00 m

Alle Maße sind Planungsannahmen: Stellplatz 2,50 × 5,00 m, Fahrgasse 6,00 m, Säule Ø 0,40 m, Grundstück 32 × 30 m (Hypothese; die städtischen Unterlagen Seite 13/15/16 liegen nur als Beschreibung vor, nicht als Foto), Zufahrt = Annahme. Wohnfläche = 0,88 × Wohnstreifen, schematisch. Nichts ist genehmigt, bemessen oder abgestimmt.


E2: Lageplan mit Gebäude, Säulen, Zufahrt und Stellplätzen

VARIANTE E · NICHT FESTGELEGT

E2 – Staffel 1,50 m zurück · grün = Stellplatz funktioniert, orange = eingeschränkt, rot = Konflikt, rosa = nur rechnerisch verbleibende Fläche

Lageplan E2 – Gebäude, Säulen, Zufahrt, Stellplätze

Grundstück H1 32 × 30 m HYPOTHETISCH (Zuschnitt/Baugrenzen nicht belegt) · Stellplatz 2,50 × 5,00 m, Fahrgasse 6,00 m = Planungsannahmen · Zufahrt = Annahme

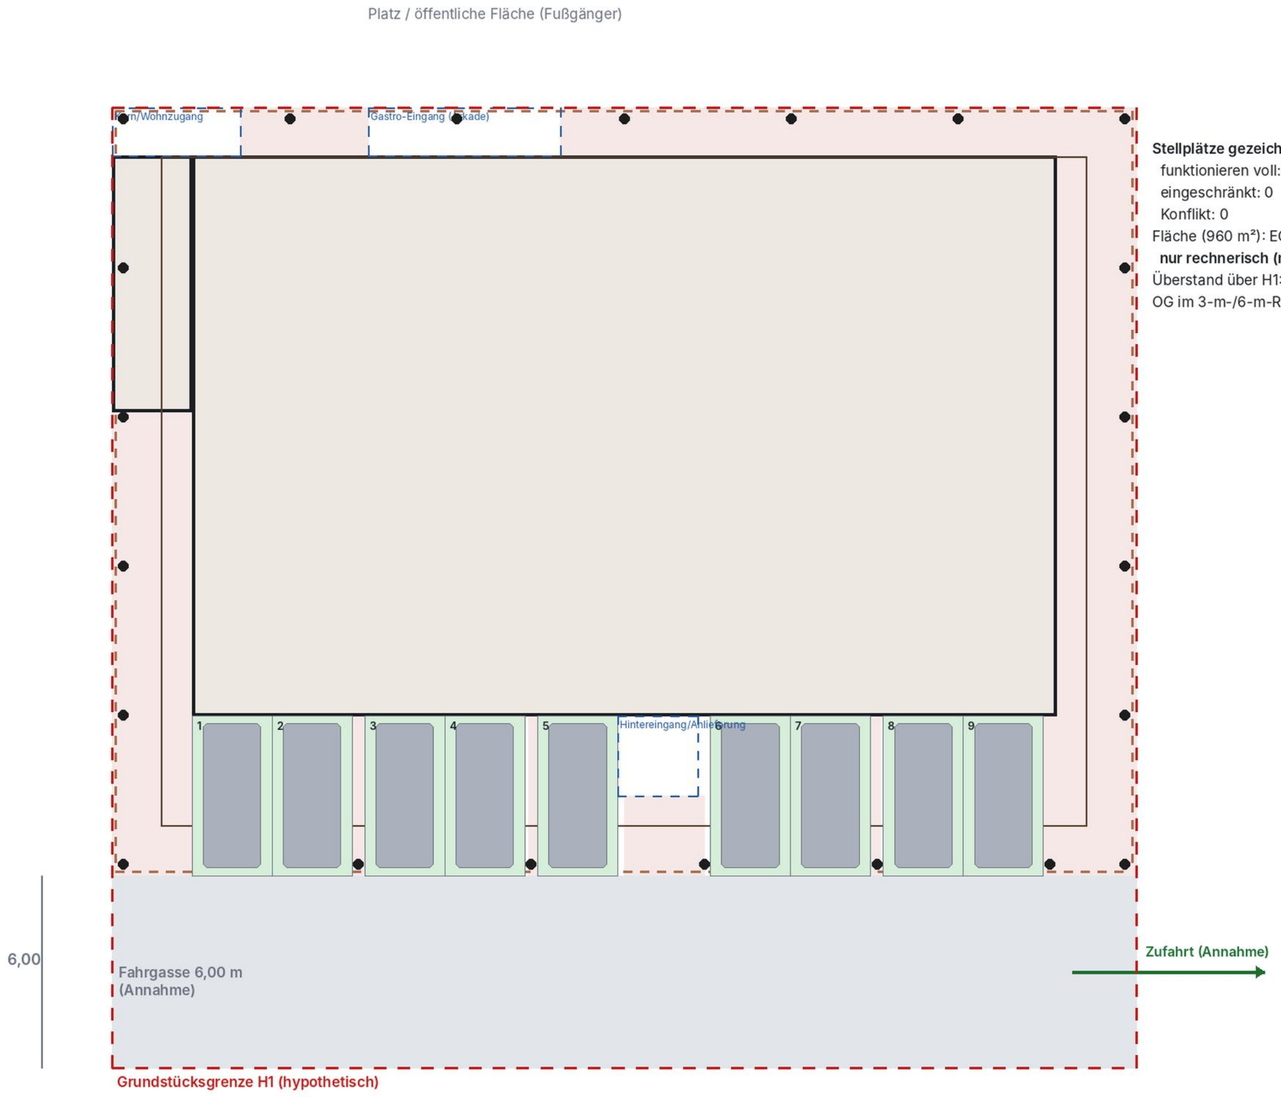

Stellplätze gezeichnet: 9
funktionieren voll: 9
eingeschränkt: 0
Konflikt: 0
Fläche (960 m²): EG 492 · Stellpl. 112 · Fahrgasse 192 · Zugänge 21
nur rechnerisch (nicht nutzbar): 142 m²
Überstand über H1: 0.00 m
OG im 3-m-/6-m-Randstreifen: 222 / 408 m²

braun gestrichelt: 1./2. OG über dem EG (Vorbau) · blau gestrichelt: Eingangszonen

Stellplatz funktioniert · eingeschränkt · Konflikt · Fahrgasse · nur rechnerisch verbleibend

Stellplatzprüfung	
Gezeichnet	9
funktionieren voll	9
eingeschränkt	0
Konflikt	0
Min. Nutzbreite 90°	2.50 m
Fahrgasse	6.0 m (frei)
Flächenbilanz 960 m²	
Erdgeschoss	492,5 m²
Stellplätze	112,5 m²
Fahrgasse	192,0 m²
Zugangszonen	21,2 m²
nur rechnerisch	141,8 m²

- Geometrische Prüfung ohne Schleppkurven; 90°-Stellplätze 2,50 × 5,00 m und Fahrgasse 6,00 m sind Planungsannahmen
- Zufahrt (Lage der Straße) ist Annahme
- Feuerwehrzufahrt/Aufstellflächen unter dem Vorbau nicht nachgewiesen (Prüfbedarf)


E2: Grundrisse EG, 1. OG, 2. OG

E2 – Staffel 1,50 m zurück · schematisch

VARIANTE E · NICHT FESTGELEGT

Erdgeschoss


E2: Erdgeschoss (schematisch)
Grundriss schematisch · Wohnungsaufteilung = Streifenmodell (Mittelgang 2,0 m), netto = 0,88 × brutto · Säulen Ø 0,40 m · Grundstück H1 hypothetisch

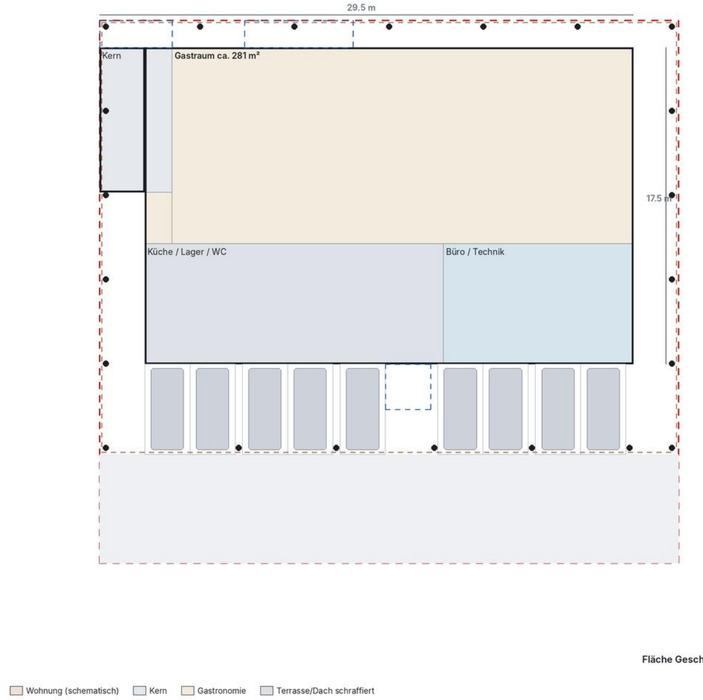

Fläche Geschoss 492 m²

1. Obergeschoss


E2: 1. Obergeschoss (schematisch)
Grundriss schematisch · Wohnungsaufteilung = Streifenmodell (Mittelgang 2,0 m), netto = 0,88 × brutto · Säulen Ø 0,40 m · Grundstück H1 hypothetisch

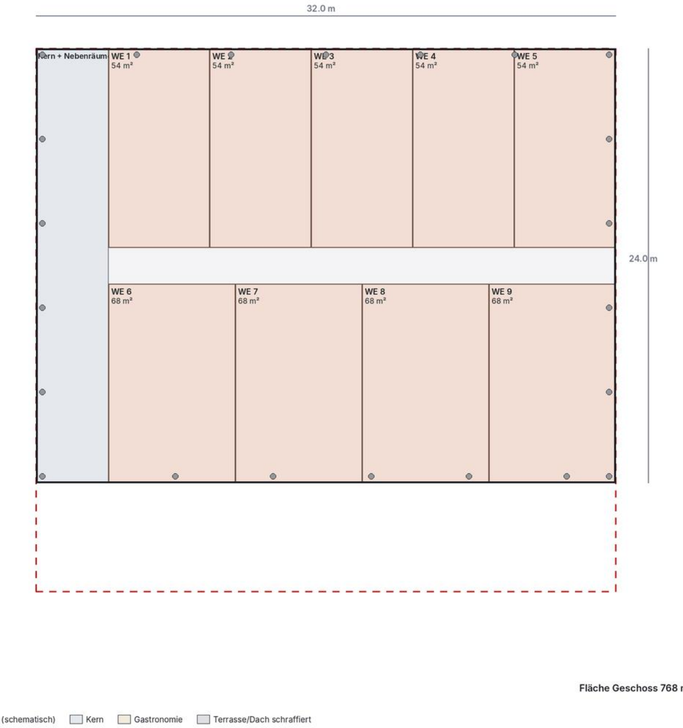

Fläche Geschoss 768 m²

2. Obergeschoss

E2: 2. Obergeschoss (Staffel) (schematisch)
Grundriss schematisch · Wohnungsaufteilung = Streifenmodell (Mittelgang 2,0 m), netto = 0,88 × brutto · Säulen Ø 0,40 m · Grundstück H1 hypothetisch

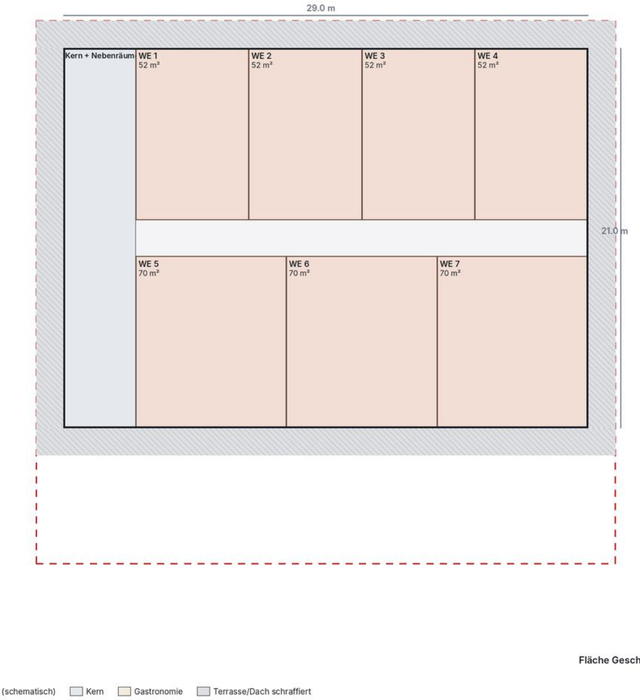

Fläche Geschoss 609 m²

Wohnung (schematisch) Kern Gastronomie Terrasse/Dach schraffiert

E2: vier Fassaden


VARIANTE E · NICHT FESTGELEGT

E2 – Staffel 1,50 m zurück · orthogonale Ansichten aus dem 3D-Modell

Vorderfassade (Platzseite)



Rückfassade

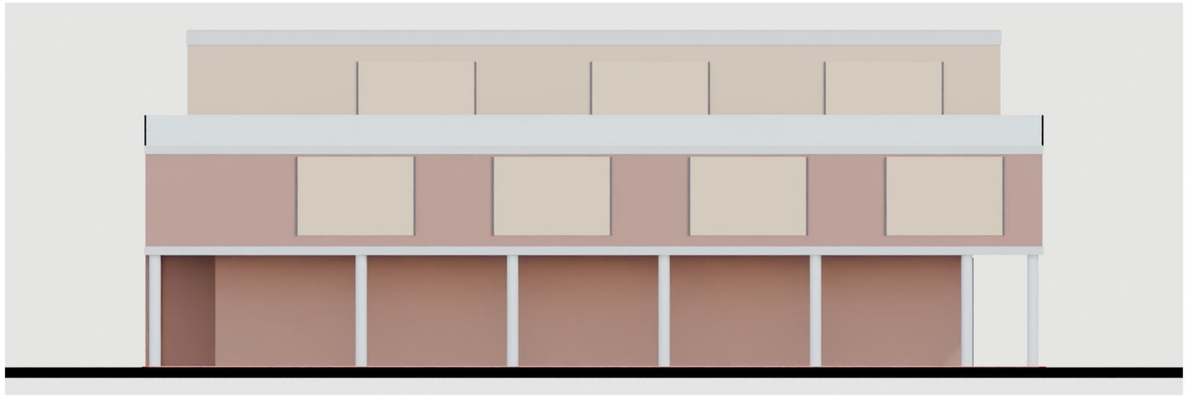

Seitenfassade West



Seitenfassade Ost



E2: Gebäudeschnitt mit Geschosshöhen und 3D-Ansichten

VARIANTE E · NICHT FESTGELEGT


E2 – Staffel 1,50 m zurück


E2: Gebäudeschnitt mit Geschosshöhen (schematisch)

Platzseite links, Rückseite rechts · Schnitt bei x = 16.25 m · Höhenbezug ±0,00 = OK Fertigfußboden EG (Planbezug Blatt 14) – Bezugspunkt der Stadt für die 12,00 m ist NICHT belegt



Geschosshöhen: EG 4,30 m · 1. OG 3,60 m · 2. OG 3,60 m · Dach/Attika 0,50 m = 12,00 m. Reserve 0,00 m. Die 12,00 m gelten erst als eingehalten, wenn der baurechtliche Höhenbezug geklärt ist.
Säulen im Schnittbereich: 2 · Säulen insgesamt: 22 · Vorbau-Unterkante +4,00 m (Decke 0,30 m)

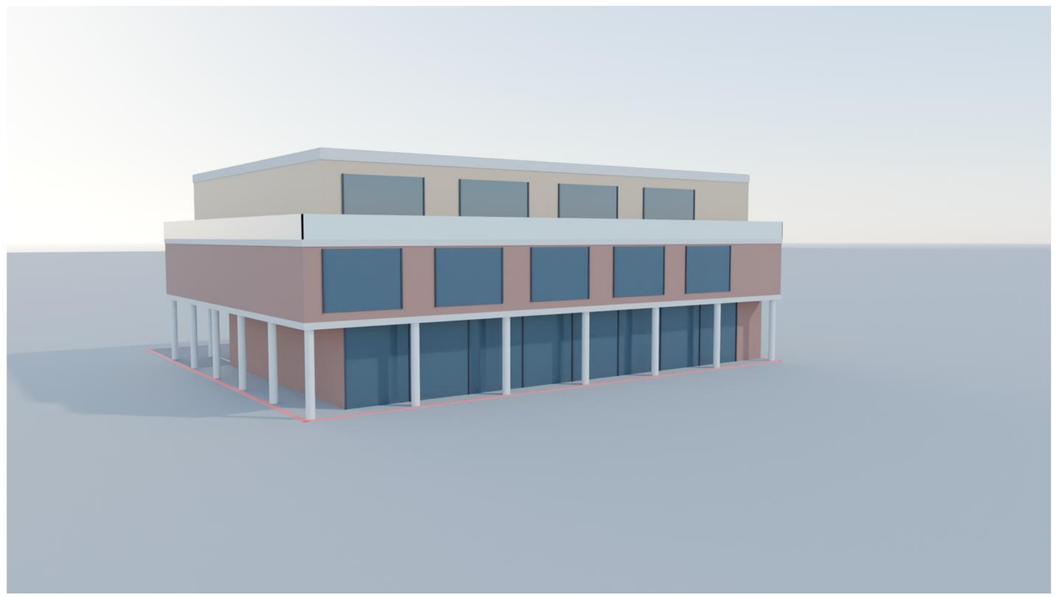


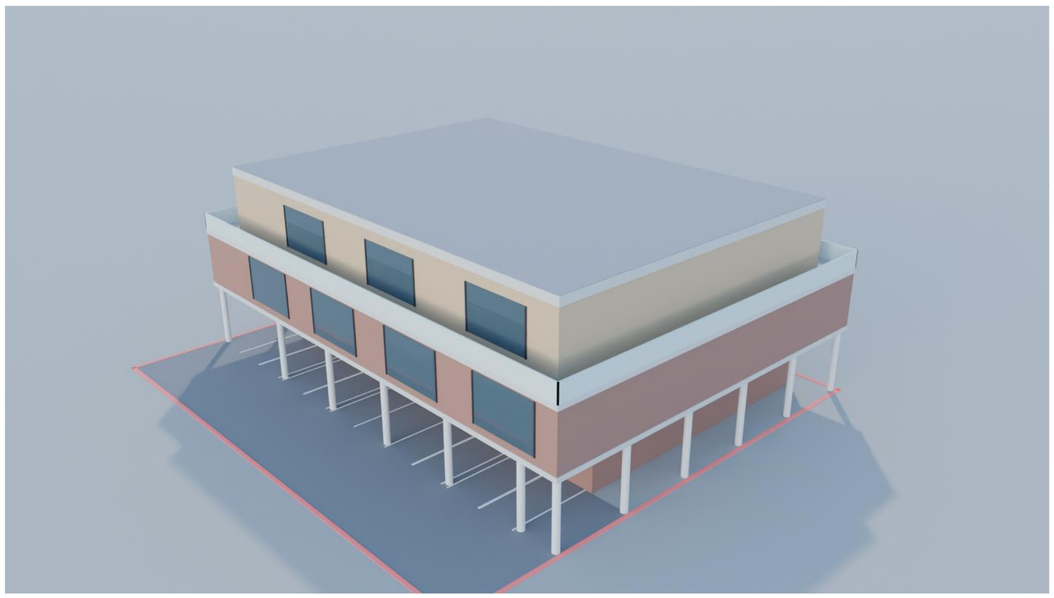

E3 – Staffel 3,00 m zurück

Entwurfsstudie Baufeld 3 · Konzeptvariante, keine Genehmigungsplanung

VARIANTE E · NICHT FESTGELEGT

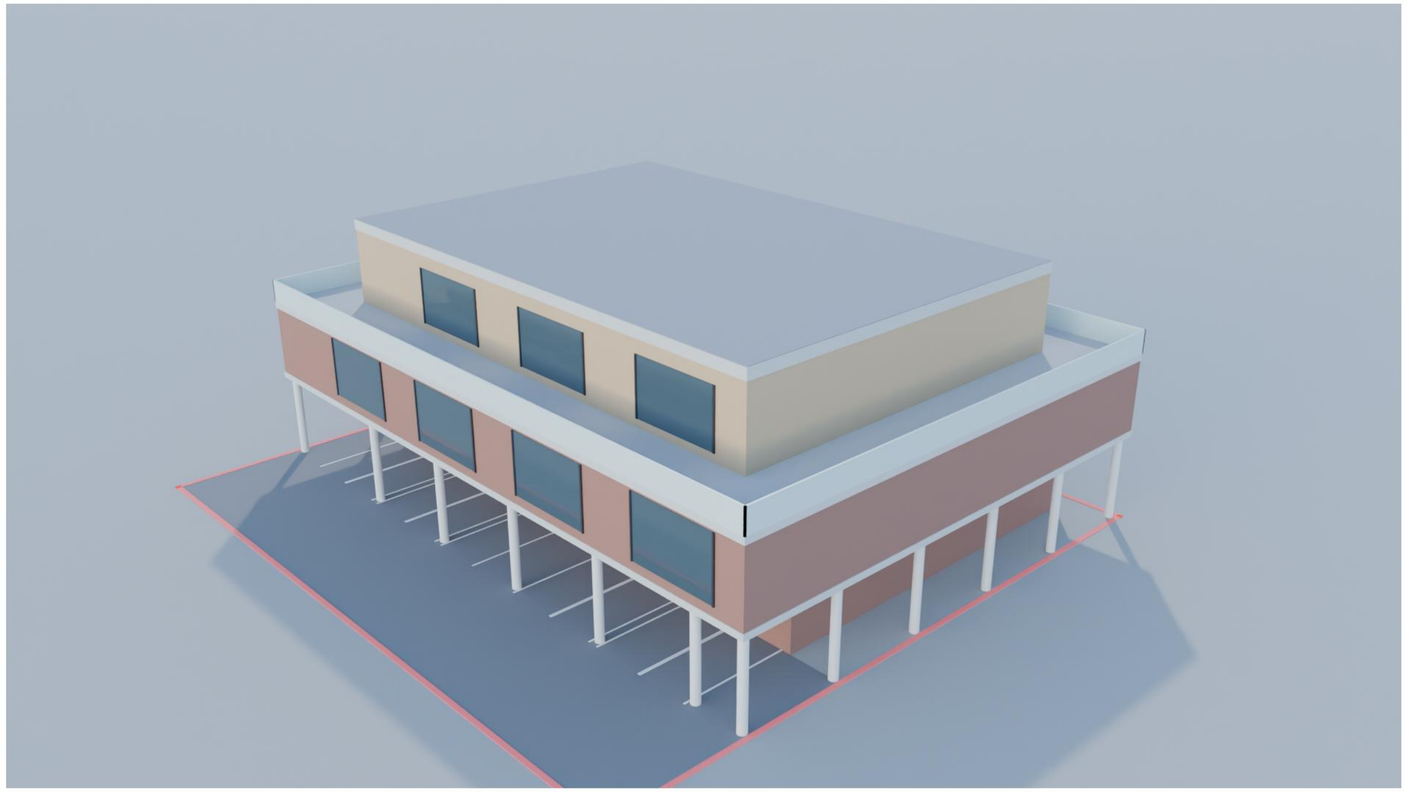

Wie E1, das 2. OG springt rundum 3,00 m zurück (breite umlaufende Dachterrasse, kleineres Staffelgeschoss).

Kennzahl	Wert (vorläufig)
Höhe	12,00 m Attika (EG 4,30 · 1. OG 3,60 · 2. OG 3,60 · Dach/Attika 0,50), 3 Geschosse – Höhenbezug offen
Grundfläche EG / 1. OG / 2. OG	492 / 768 / 468 m²
Außenmaße EG / 1. OG / 2. OG	29.5 × 17.5 / 32.0 × 24.0 / 26.0 × 18.0 m
Wohnfläche netto (geschätzt)	852 m²
Wohnungen Standardmix	15 WE (9 + 6), 52–68 m², Ø 57 m²
Gewerbe	EG 492 m²; Gastraum ca. 281 m² (≈ 120 Plätze), Terrasse/Arkade ≈ 28 Plätze, Büro 56 m²
Säulen	22 Säulen Ø 0,40 m; Paare 5,4 m (zwei Stellplätze + Säule)
Stellplätze gezeichnet	9: 9 voll nutzbar, 0 eingeschränkt, 0 Konflikt
Stellplätze erforderlich (§ 47 NBauO)	11,4–16,9, Mittel 13,6 (nur Gastro + Büro; Wohnen 0)
Stellplätze optional (Komfort/Markt)	Wohnen 0,5–1,5 je WE = 8–22; Komfortziel gesamt ≈ 29
Überstand über Grundstück H1	0,00 m

Alle Maße sind Planungsannahmen: Stellplatz 2,50 × 5,00 m, Fahrgasse 6,00 m, Säule Ø 0,40 m, Grundstück 32 × 30 m (Hypothese; die städtischen Unterlagen Seite 13/15/16 liegen nur als Beschreibung vor, nicht als Foto), Zufahrt = Annahme. Wohnfläche = 0,88 × Wohnstreifen, schematisch. Nichts ist genehmigt, bemessen oder abgestimmt.


E3: Lageplan mit Gebäude, Säulen, Zufahrt und Stellplätzen

VARIANTE E · NICHT FESTGELEGT

E3 – Staffel 3,00 m zurück · grün = Stellplatz funktioniert, orange = eingeschränkt, rot = Konflikt, rosa = nur rechnerisch verbleibende Fläche

Lageplan E3 – Gebäude, Säulen, Zufahrt, Stellplätze

Grundstück H1 32 × 30 m HYPOTHETISCH (Zuschnitt/Baugrenzen nicht belegt) · Stellplatz 2,50 × 5,00 m, Fahrgasse 6,00 m = Planungsannahmen · Zufahrt = Annahme

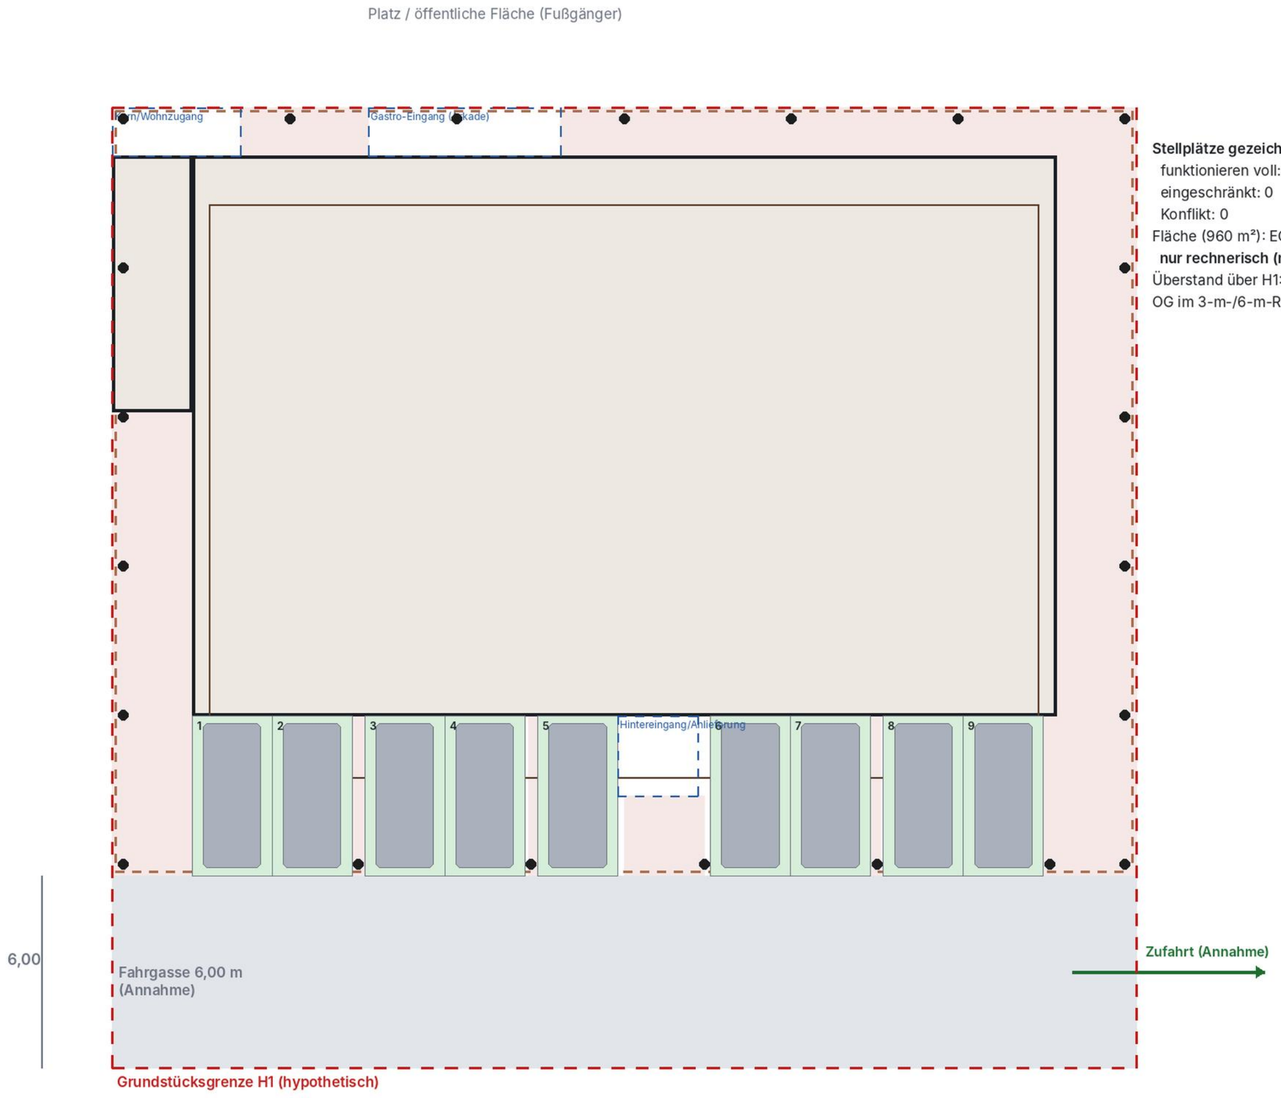

Stellplätze gezeichnet: 9
funktionieren voll: 9
eingeschränkt: 0
Konflikt: 0
Fläche (960 m²): EG 492 · Stellpl. 112 · Fahrgasse 192 · Zugänge 21
nur rechnerisch (nicht nutzbar): 142 m²
Überstand über H1: 0.00 m
OG im 3-m-/6-m-Randstreifen: 222 / 408 m²

Stellplatzprüfung	
Gezeichnet	9
funktionieren voll	9
eingeschränkt	0
Konflikt	0
Min. Nutzbreite 90°	2.50 m
Fahrgasse	6.0 m (frei)
Flächenbilanz 960 m²	
Erdgeschoss	492,5 m²
Stellplätze	112,5 m²
Fahrgasse	192,0 m²
Zugangszonen	21,2 m²
nur rechnerisch	141,8 m²

- Geometrische Prüfung ohne Schleppkurven; 90°-Stellplätze 2,50 × 5,00 m und Fahrgasse 6,00 m sind Planungsannahmen
- Zufahrt (Lage der Straße) ist Annahme
- Feuerwehrzufahrt/Aufstellflächen unter dem Vorbau nicht nachgewiesen (Prüfbedarf)

Stellplatz funktioniert · eingeschränkt · Konflikt · Fahrgasse · nur rechnerisch verbleibend

braun gestrichelt: 1./2. OG über dem EG (Vorbau) · blau gestrichelt: Eingangszonen


E3: Grundrisse EG, 1. OG, 2. OG

E3 – Staffel 3,00 m zurück · schematisch

VARIANTE E · NICHT FESTGELEGT

Erdgeschoss

E3: Erdgeschoss (schematisch)
Grundriss schematisch · Wohnungsaufteilung = Streifenmodell (Mittelgang 2,0 m), netto = 0,88 × brutto · Säulen Ø 0,40 m · Grundstück H1 hypothetisch

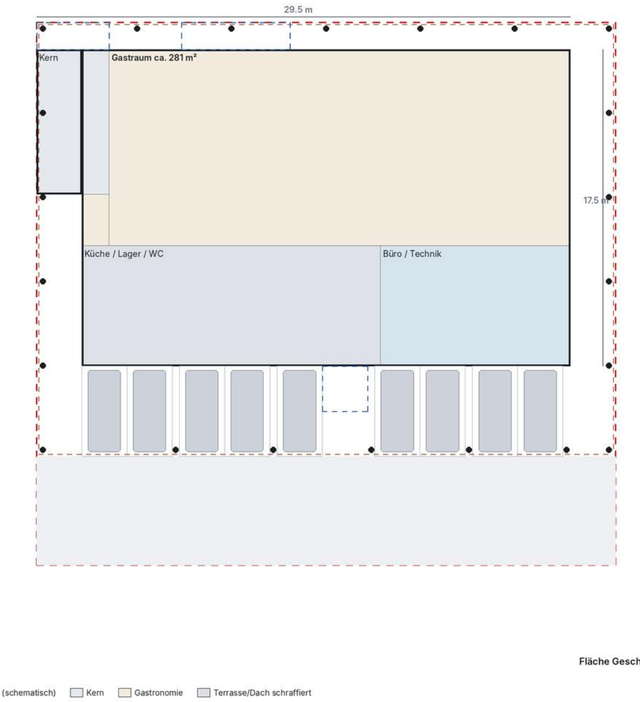


Fläche Geschoss 492 m²

Wohnung (schematisch) Kern Gastronomie Terrasse/Dach schraffiert

1. Obergeschoss

E3: 1. Obergeschoss (schematisch)
Grundriss schematisch · Wohnungsaufteilung = Streifenmodell (Mittelgang 2,0 m), netto = 0,88 × brutto · Säulen Ø 0,40 m · Grundstück H1 hypothetisch

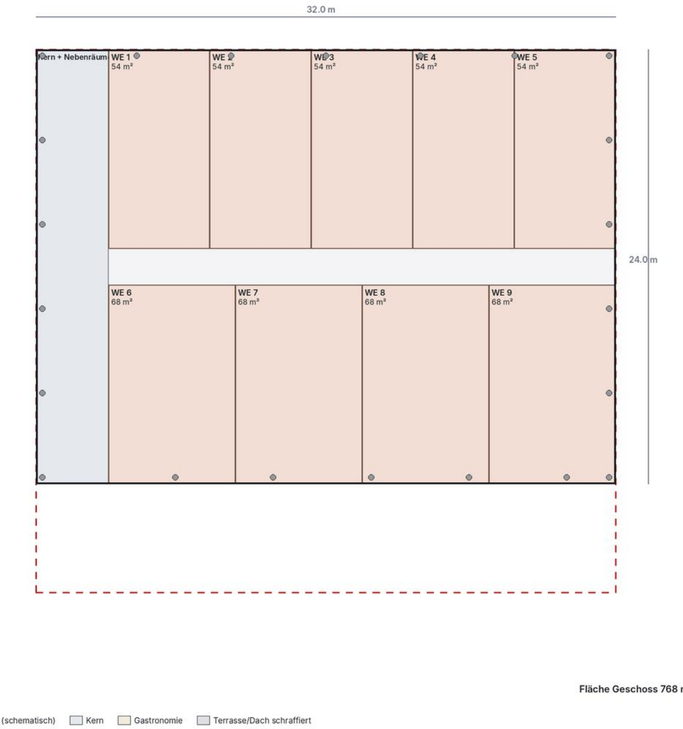


Fläche Geschoss 768 m²

Wohnung (schematisch) Kern Gastronomie Terrasse/Dach schraffiert

2. Obergeschoss

E3: 2. Obergeschoss (Staffel) (schematisch)
Grundriss schematisch · Wohnungsaufteilung = Streifenmodell (Mittelgang 2,0 m), netto = 0,88 × brutto · Säulen Ø 0,40 m · Grundstück H1 hypothetisch

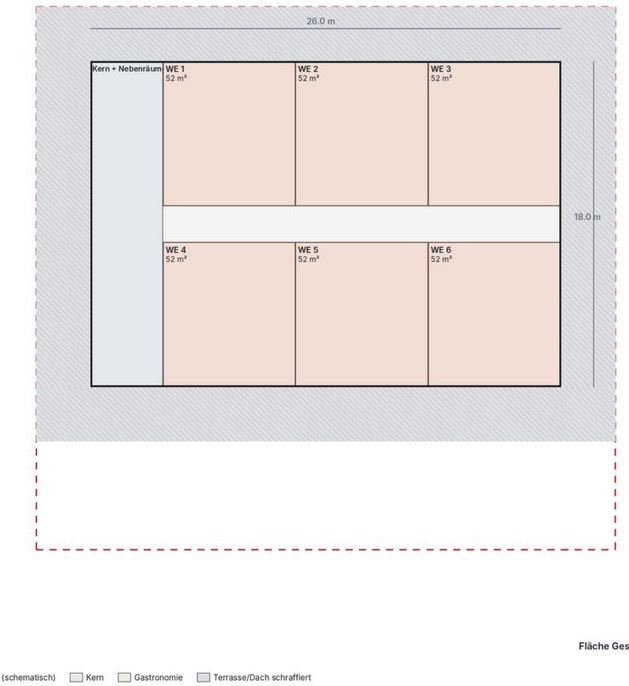

Fläche Geschoss 468 m²

Wohnung (schematisch) Kern Gastronomie Terrasse/Dach schraffiert

E3: vier Fassaden


VARIANTE E · NICHT FESTGELEGT

E3 – Staffel 3,00 m zurück · orthogonale Ansichten aus dem 3D-Modell

Vorderfassade (Platzseite)




Rückfassade

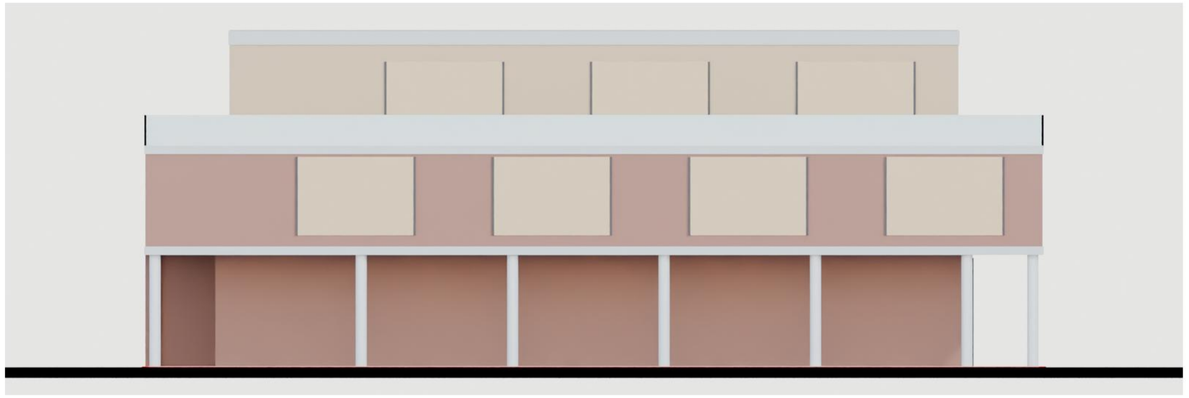

Seitenfassade West



Seitenfassade Ost

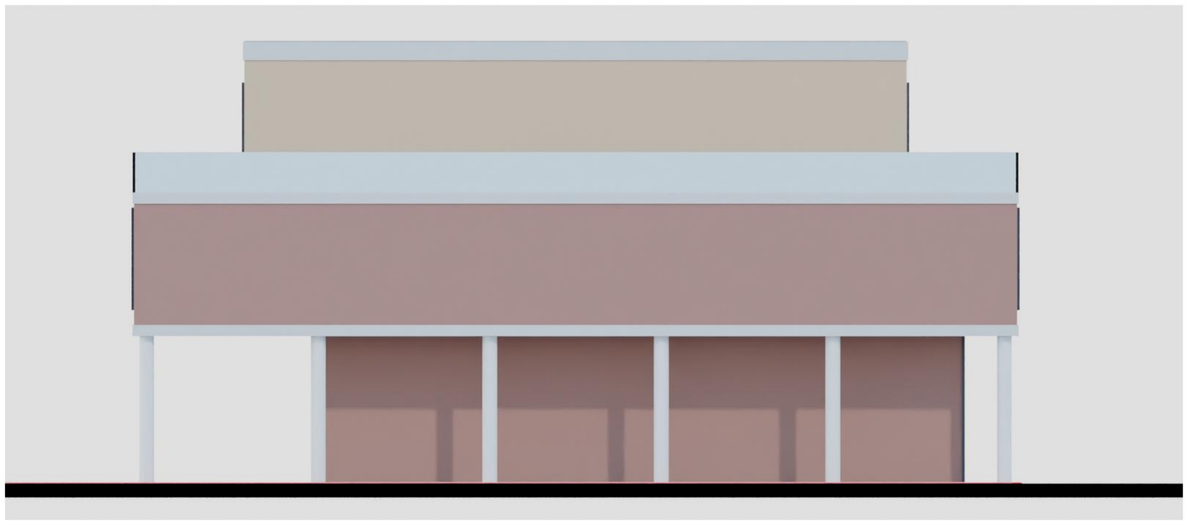


E3: Gebäudeschnitt mit Geschosshöhen und 3D-Ansichten

E3 – Staffel 3,00 m zurück


VARIANTE E · NICHT FESTGELEGT


E3: Gebäudeschnitt mit Geschosshöhen (schematisch)

Platzseite links, Rückseite rechts · Schnitt bei x = 16.25 m · Höhenbezug ±0,00 = OK Fertigfußboden EG (Planbezug Blatt 14) – Bezugspunkt der Stadt für die 12,00 m ist NICHT belegt

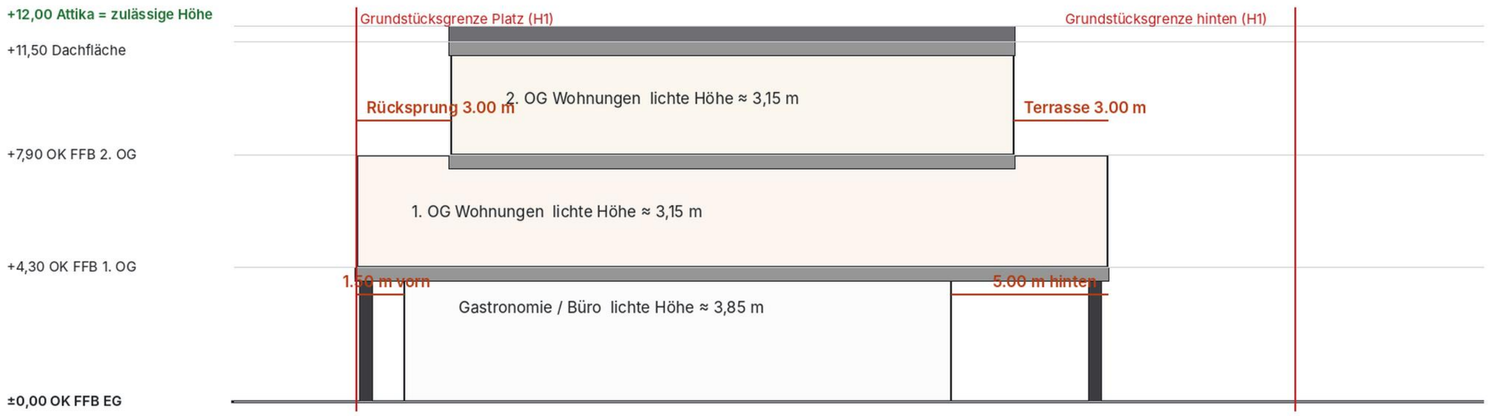

Geschosshöhen: EG 4,30 m · 1. OG 3,60 m · 2. OG 3,60 m · Dach/Attika 0,50 m = 12,00 m. Reserve 0,00 m. Die 12,00 m gelten erst als eingehalten, wenn der baurechtliche Höhenbezug geklärt ist.
Säulen im Schnittbereich: 2 · Säulen insgesamt: 22 · Vorbau-Unterkante +4,00 m (Decke 0,30 m)

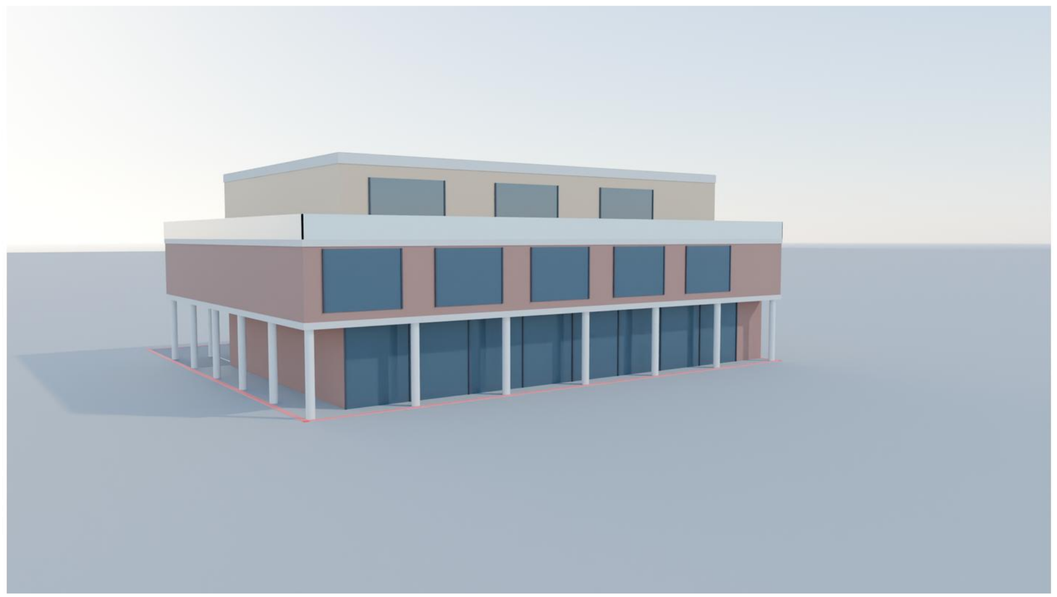


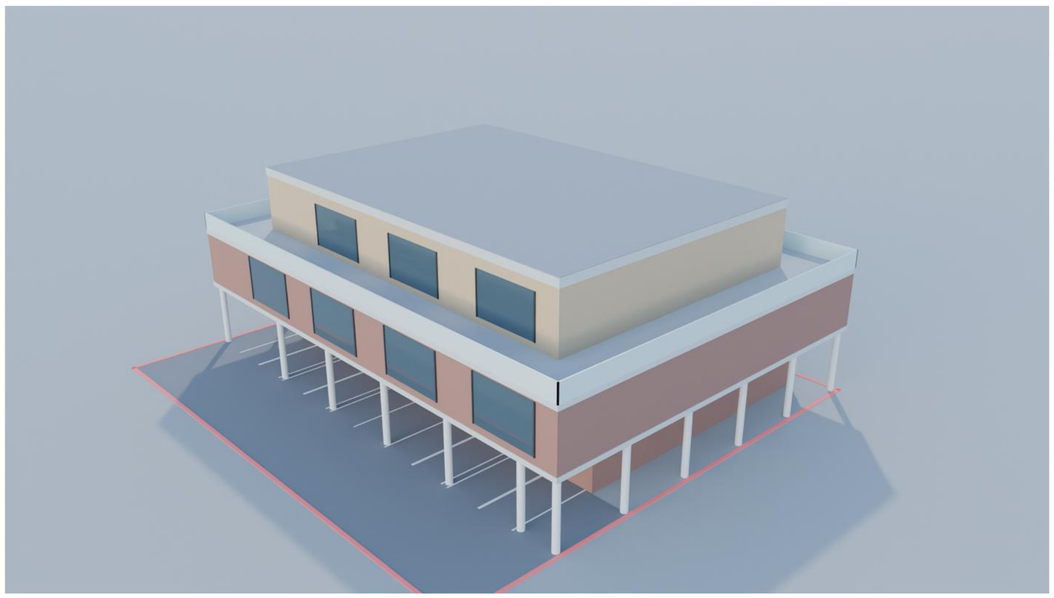

E4 – zweireihiges Parken, kleineres EG

Entwurfsstudie Baufeld 3 · Konzeptvariante, keine Genehmigungsplanung

VARIANTE E · NICHT FESTGELEGT

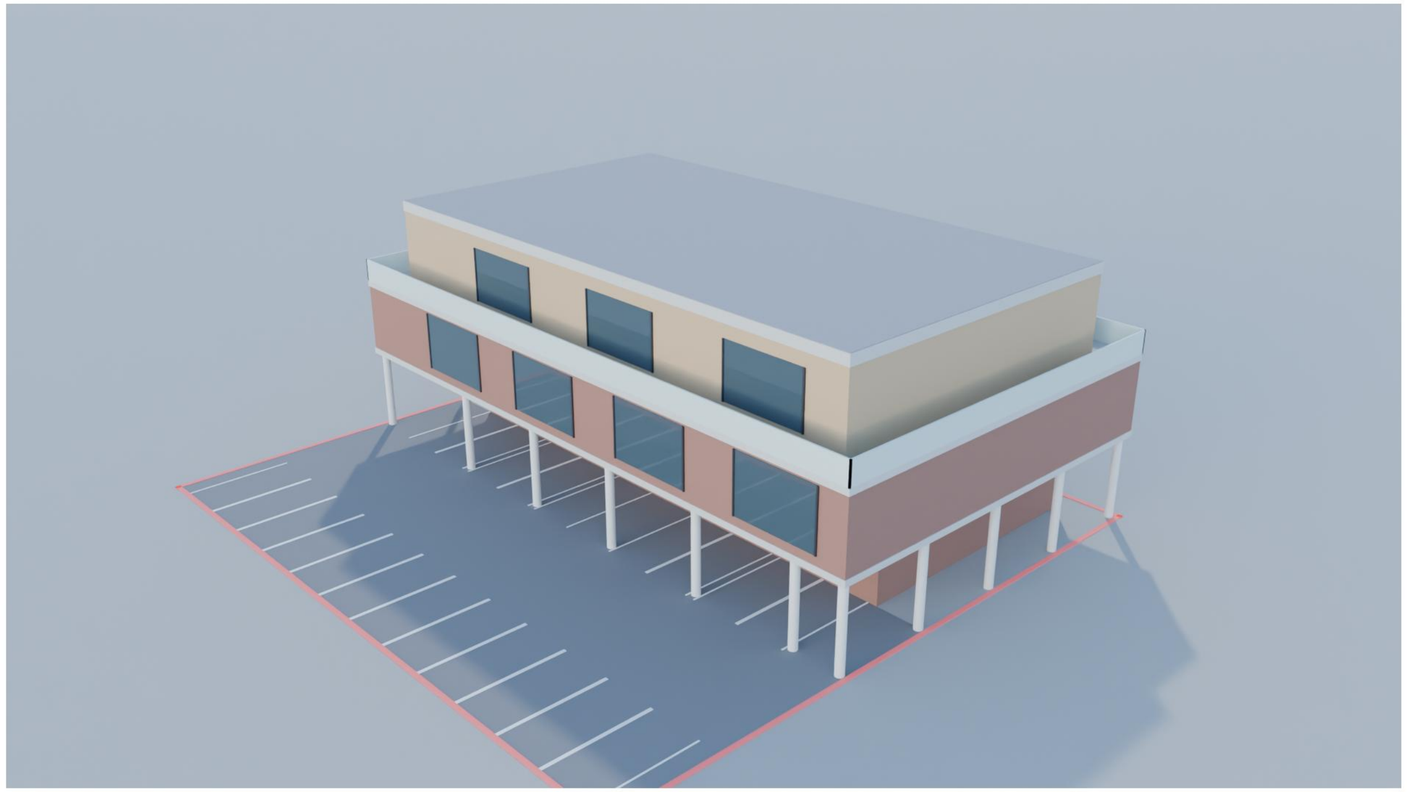

Wie E2, aber Erdgeschoss nur 14 m tief: zwei Stellplatzreihen (eine unter dem 5-m-Vorbau hinten, eine frei) mit 6-m-Fahrgasse dazwischen; dafür weniger Gewerbefläche.

Kennzahl	Wert (vorläufig)
Höhe	12,00 m Attika (EG 4,30 · 1. OG 3,60 · 2. OG 3,60 · Dach/Attika 0,50), 3 Geschosse – Höhenbezug offen
Grundfläche EG / 1. OG / 2. OG	358 / 608 / 464 m²
Außenmaße EG / 1. OG / 2. OG	29.5 × 12.5 / 32.0 × 19.0 / 29.0 × 16.0 m
Wohnfläche netto (geschätzt)	727 m²
Wohnungen Standardmix	16 WE (9 + 7), 38–52 m², Ø 45 m²
Gewerbe	EG 358 m²; Gastraum ca. 198 m² (≈ 85 Plätze), Terrasse/Arkade ≈ 28 Plätze, Büro 56 m²
Säulen	20 Säulen Ø 0,40 m; Paare 5,4 m (zwei Stellplätze + Säule)
Stellplätze gezeichnet	21: 21 voll nutzbar, 0 eingeschränkt, 0 Konflikt
Stellplätze erforderlich (§ 47 NBauO)	8,5–12,5, Mittel 10,1 (nur Gastro + Büro; Wohnen 0)
Stellplätze optional (Komfort/Markt)	Wohnen 0,5–1,5 je WE = 8–24; Komfortziel gesamt ≈ 26
Überstand über Grundstück H1	0,00 m

Alle Maße sind Planungsannahmen: Stellplatz 2,50 × 5,00 m, Fahrgasse 6,00 m, Säule Ø 0,40 m, Grundstück 32 × 30 m (Hypothese; die städtischen Unterlagen Seite 13/15/16 liegen nur als Beschreibung vor, nicht als Foto), Zufahrt = Annahme. Wohnfläche = 0,88 × Wohnstreifen, schematisch. Nichts ist genehmigt, bemessen oder abgestimmt.


E4: Lageplan mit Gebäude, Säulen, Zufahrt und Stellplätzen

VARIANTE E · NICHT FESTGELEGT

E4 – zweireihiges Parken, kleineres EG · grün = Stellplatz funktioniert, orange = eingeschränkt, rot = Konflikt, rosa = nur rechnerisch verbleibende Fläche

Lageplan E4 – Gebäude, Säulen, Zufahrt, Stellplätze

Grundstück H1 32 × 30 m HYPOTHETISCH (Zuschnitt/Baugrenzen nicht belegt) · Stellplatz 2,50 × 5,00 m, Fahrgasse 6,00 m = Planungsannahmen · Zufahrt = Annahme

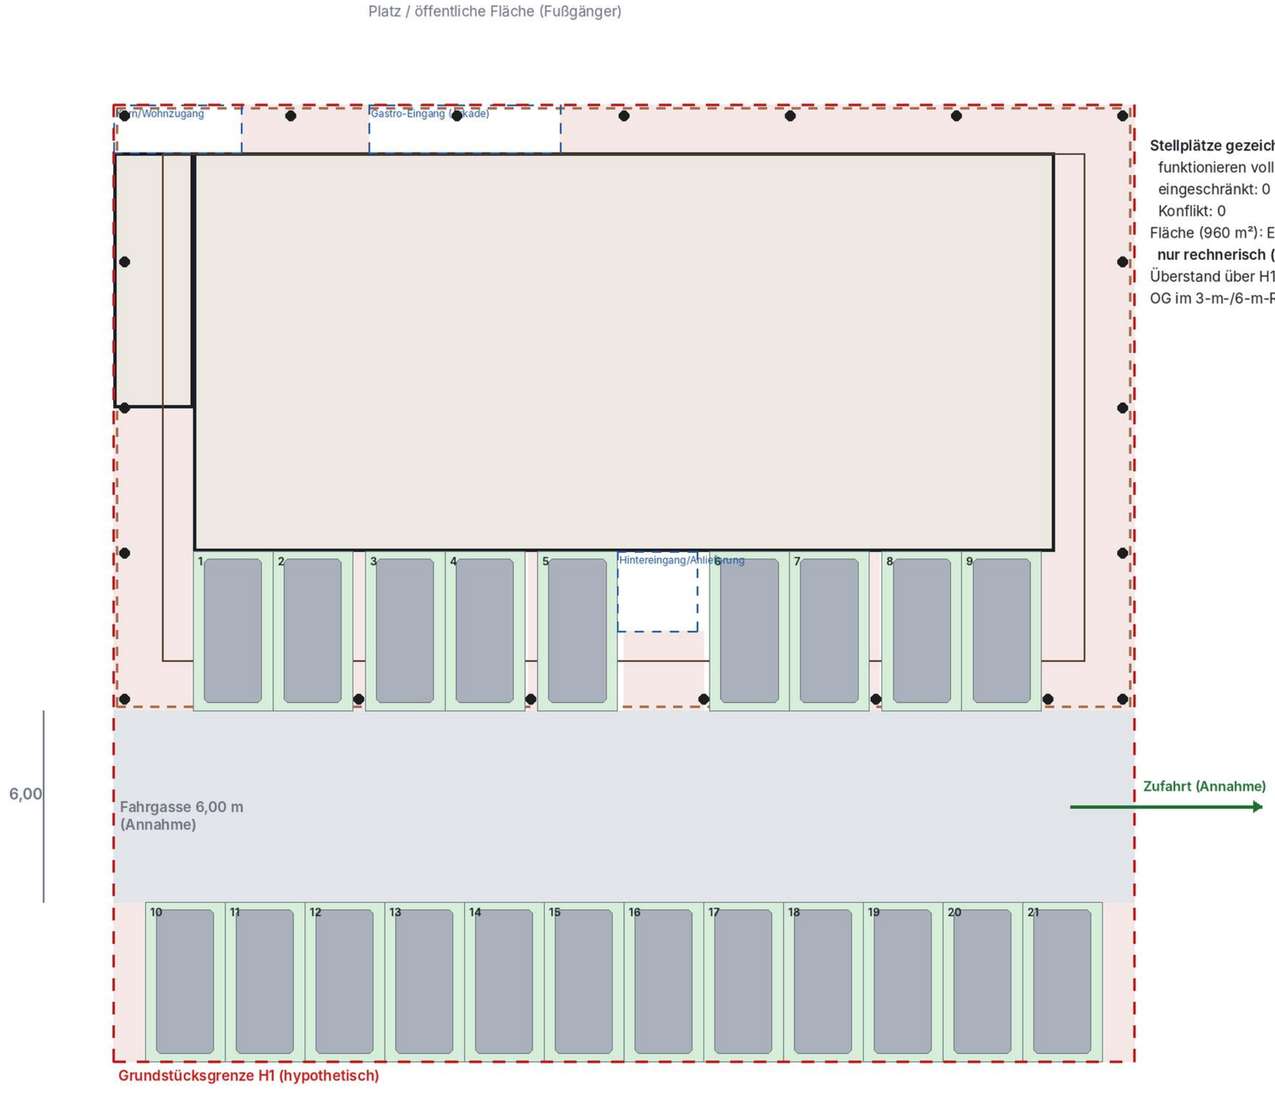

Stellplätze gezeichnet: 21
funktionieren voll: 21
eingeschränkt: 0
Konflikt: 0
Fläche (960 m²): EG 358 · Stellpl. 262 · Fahrgasse 192 · Zugänge 21
nur rechnerisch (nicht nutzbar): 127 m²
Überstand über H1: 0.00 m
OG im 3-m-/6-m-Randstreifen: 192 / 348 m²

Stellplatzprüfung	
Gezeichnet	21
funktionieren voll	21
eingeschränkt	0
Konflikt	0
Min. Nutzbreite 90°	2.50 m
Fahrgasse	6.0 m (frei)
Flächenbilanz 960 m²	
Erdgeschoss	357,5 m²
Stellplätze	262,5 m²
Fahrgasse	192,0 m²
Zugangszonen	21,2 m²
nur rechnerisch	126,8 m²

- Geometrische Prüfung ohne Schleppkurven; 90°-Stellplätze 2,50 × 5,00 m und Fahrgasse 6,00 m sind Planungsannahmen
- Zufahrt (Lage der Straße) ist Annahme
- Feuerwehrzufahrt/Aufstellflächen unter dem Vorbau nicht nachgewiesen (Prüfbedarf)

Stellplatz funktioniert · eingeschränkt · Konflikt · Fahrgasse · nur rechnerisch verbleibend

braun gestrichelt: 1./2. OG über dem EG (Vorbau) · blau gestrichelt: Eingangszonen


E4: Grundrisse EG, 1. OG, 2. OG

E4 – zweireihiges Parken, kleineres EG · schematisch

VARIANTE E · NICHT FESTGELEGT

Erdgeschoss

E4: Erdgeschoss (schematisch)
Grundriss schematisch · Wohnungsaufteilung = Streifenmodell (Mittelgang 2,0 m), netto = 0,88 × brutto · Säulen Ø 0,40 m · Grundstück H1 hypothetisch

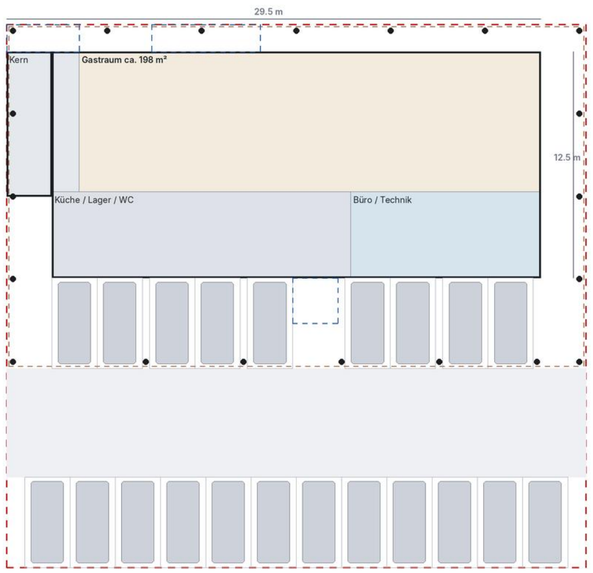


Fläche Geschoss 358 m²

Wohnung (schematisch) Kern Gastronomie Terrasse/Dach schraffiert

1. Obergeschoss

E4: 1. Obergeschoss (schematisch)
Grundriss schematisch · Wohnungsaufteilung = Streifenmodell (Mittelgang 2,0 m), netto = 0,88 × brutto · Säulen Ø 0,40 m · Grundstück H1 hypothetisch

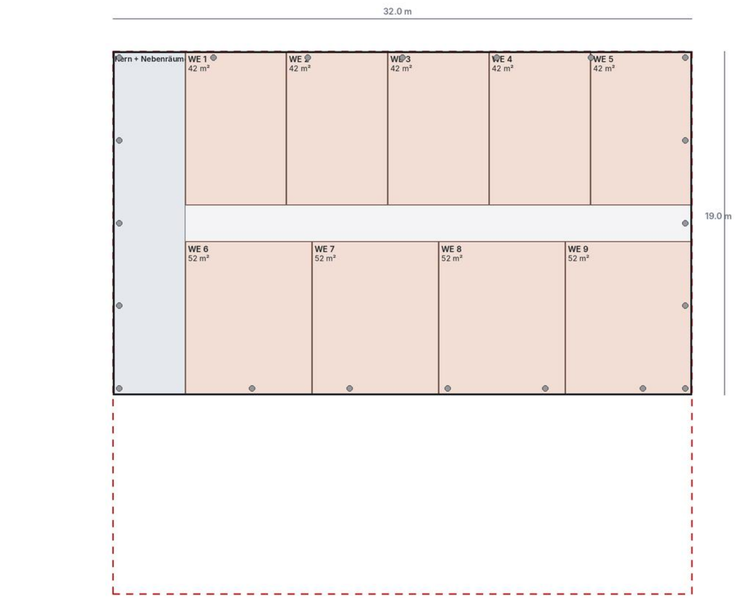


Fläche Geschoss 608 m²

Wohnung (schematisch) Kern Gastronomie Terrasse/Dach schraffiert

2. Obergeschoss

E4: 2. Obergeschoss (Staffel) (schematisch)
Grundriss schematisch · Wohnungsaufteilung = Streifenmodell (Mittelgang 2,0 m), netto = 0,88 × brutto · Säulen Ø 0,40 m · Grundstück H1 hypothetisch

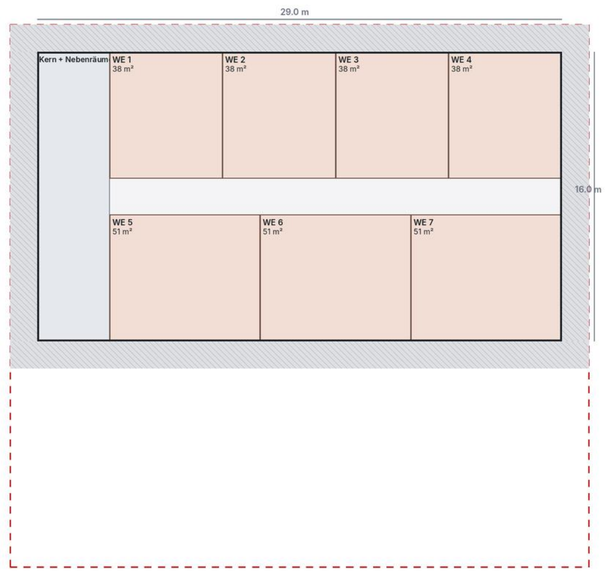

Fläche Geschoss 464 m²

Wohnung (schematisch) Kern Gastronomie Terrasse/Dach schraffiert

E4: vier Fassaden


E4 – zweireihiges Parken, kleineres EG · orthogonale Ansichten aus dem 3D-Modell

VARIANTE E · NICHT FESTGELEGT

Vorderfassade (Platzseite)



Rückfassade

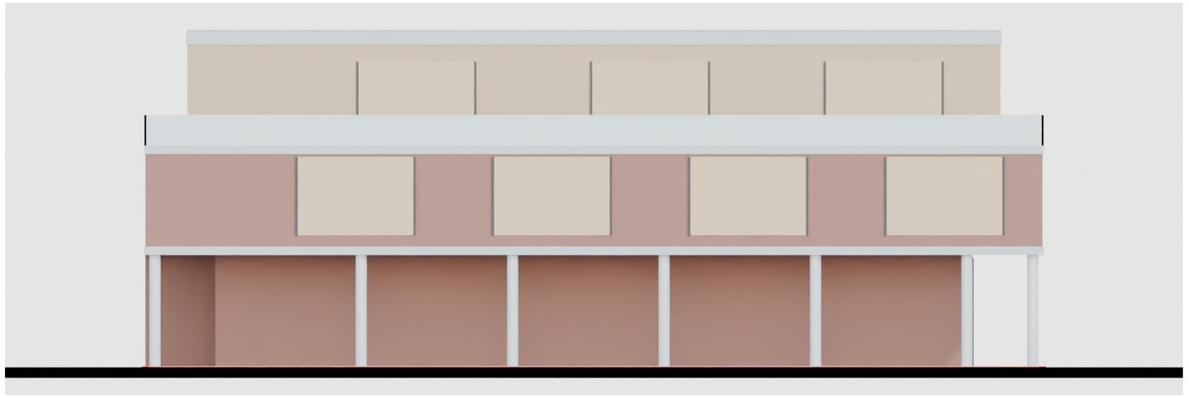

Seitenfassade West



Seitenfassade Ost




E4: Gebäudeschnitt mit Geschosshöhen und 3D-Ansichten

E4 – zweireihiges Parken, kleineres EG


VARIANTE E · NICHT FESTGELEGT


E4: Gebäudeschnitt mit Geschosshöhen (schematisch)

Platzseite links, Rückseite rechts · Schnitt bei x = 16.25 m · Höhenbezug ±0,00 = OK Fertigfußboden EG (Planbezug Blatt 14) – Bezugspunkt der Stadt für die 12,00 m ist NICHT belegt

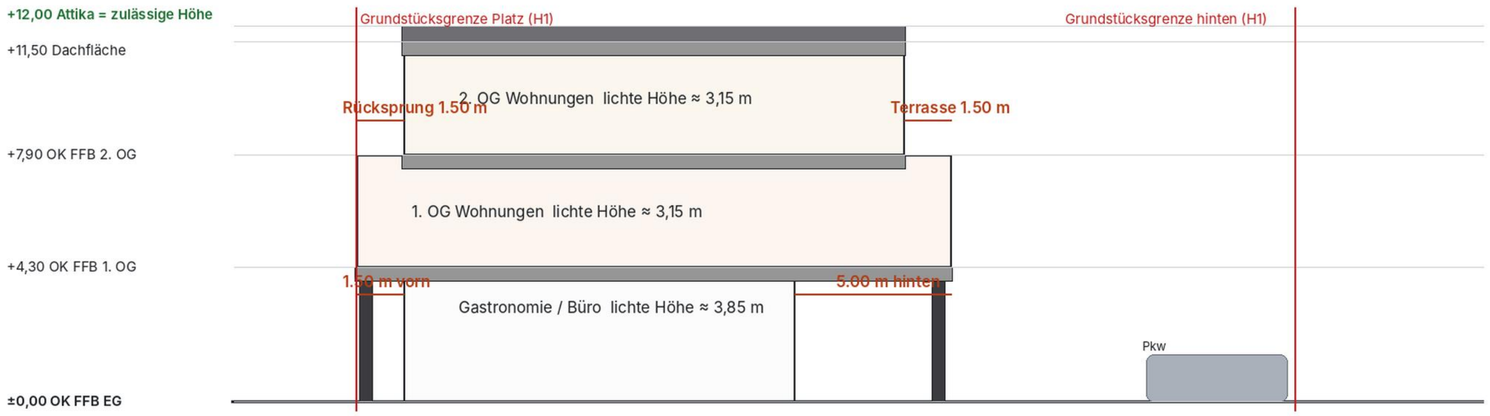

Geschosshöhen: EG 4,30 m · 1. OG 3,60 m · 2. OG 3,60 m · Dach/Attika 0,50 m = 12,00 m. Reserve 0,00 m. Die 12,00 m gelten erst als eingehalten, wenn der baurechtliche Höhenbezug geklärt ist.
Säulen im Schnittbereich: 2 · Säulen insgesamt: 20 · Vorbau-Unterkante +4,00 m (Decke 0,30 m)

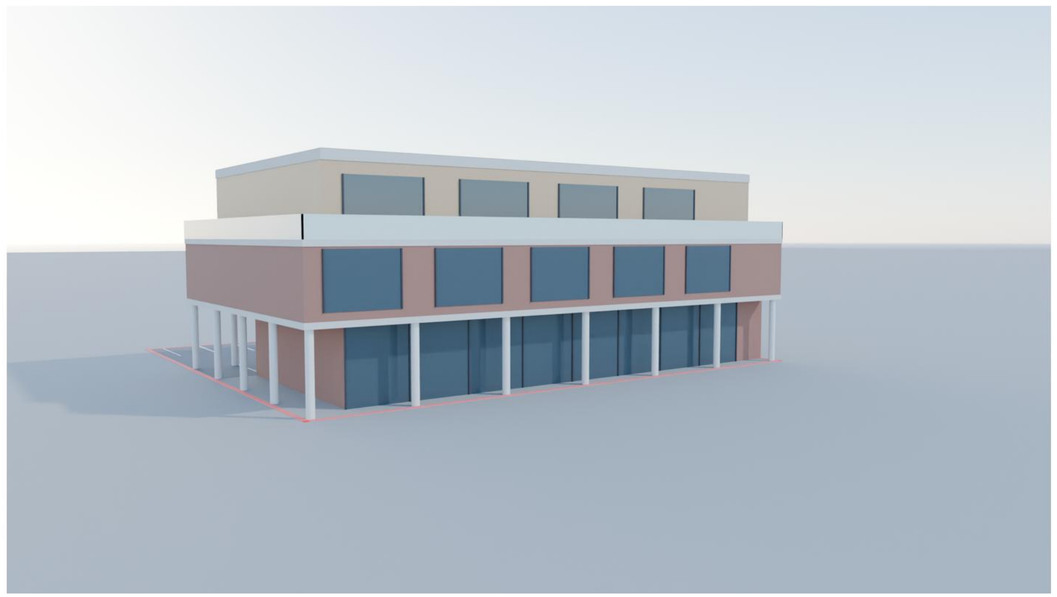

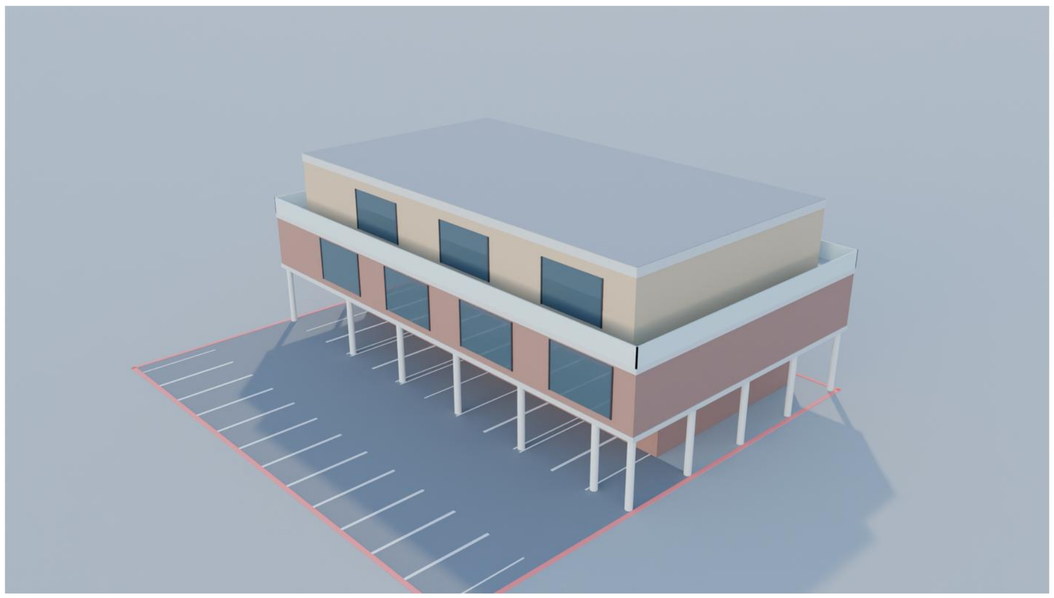

Baurechtliche Ampel (vorläufig)

VARIANTE E · NICHT FESTGELEGT

Keine Rechtsprüfung · bis zur Klärung von Grundstück, Baugrenzen und Satzungen offen

Kriterium	E1	E2	E3	E4
Gebäudehöhe 12,00 m	kritisch / offen: Attika +12,00 m über FFB. Entwurf B-Plan 123: H = 12,00 m über OK Fahrbahn, FFB max. +0,30 m → Baukörper max. +11,70 m über FFB; Fahrbahnhöhe unbekannt, Plan nur Entwurf – NICHT als eingehalten zu werten.	kritisch / offen: Attika +12,00 m über FFB. Entwurf B-Plan 123: H = 12,00 m über OK Fahrbahn, FFB max. +0,30 m → Baukörper max. +11,70 m über FFB; Fahrbahnhöhe unbekannt, Plan nur Entwurf – NICHT als eingehalten zu werten.	kritisch / offen: Attika +12,00 m über FFB. Entwurf B-Plan 123: H = 12,00 m über OK Fahrbahn, FFB max. +0,30 m → Baukörper max. +11,70 m über FFB; Fahrbahnhöhe unbekannt, Plan nur Entwurf – NICHT als eingehalten zu werten.	kritisch / offen: Attika +12,00 m über FFB. Entwurf B-Plan 123: H = 12,00 m über OK Fahrbahn, FFB max. +0,30 m → Baukörper max. +11,70 m über FFB; Fahrbahnhöhe unbekannt, Plan nur Entwurf – NICHT als eingehalten zu werten.
Geschosse / Traufe / Dach	kritisch / offen: Entwurf 1. Änderung: zwingend II Vollgeschosse, TH max. 6,50 m, Hauptdach geneigt ≥ 38° (Flachdach nur untergeordnet). Drei Geschosse mit Flachdach, Oberkante 1. OG +7,90 m und 2. OG = 100 % des 1. OG widersprechen dem Entwurf; Ursprungsplan unbekannt.	kritisch / offen: Entwurf 1. Änderung: zwingend II Vollgeschosse, TH max. 6,50 m, Hauptdach geneigt ≥ 38° (Flachdach nur untergeordnet). Drei Geschosse mit Flachdach, Oberkante 1. OG +7,90 m und 2. OG = 79 % des 1. OG widersprechen dem Entwurf; Ursprungsplan unbekannt.	kritisch / offen: Entwurf 1. Änderung: zwingend II Vollgeschosse, TH max. 6,50 m, Hauptdach geneigt ≥ 38° (Flachdach nur untergeordnet). Drei Geschosse mit Flachdach, Oberkante 1. OG +7,90 m und 2. OG = 61 % des 1. OG widersprechen dem Entwurf; Ursprungsplan unbekannt.	kritisch / offen: Entwurf 1. Änderung: zwingend II Vollgeschosse, TH max. 6,50 m, Hauptdach geneigt ≥ 38° (Flachdach nur untergeordnet). Drei Geschosse mit Flachdach, Oberkante 1. OG +7,90 m und 2. OG = 76 % des 1. OG widersprechen dem Entwurf; Ursprungsplan unbekannt.
GRZ / Überdeckung	zu prüfen: größte Geschossprojektion 768 m² = 80 % von 960 m² (GRZ 0,6 = 576 m² nur Annahme).	zu prüfen: größte Geschossprojektion 768 m² = 80 % von 960 m² (GRZ 0,6 = 576 m² nur Annahme).	zu prüfen: größte Geschossprojektion 768 m² = 80 % von 960 m² (GRZ 0,6 = 576 m² nur Annahme).	zu prüfen: größte Geschossprojektion 608 m² = 63 % von 960 m² (GRZ 0,6 = 576 m² nur Annahme).
Grenzen / Baugrenzen	kritisch / offen: Außenkante OG auf angenommener Grenze (0,00 m). Entwurf: Baugrenze 3,0 m zu Planstraße/Parkplatz – der Vorbau über die Baugrenze ist unzulässig; auf den aus den amtlichen Plänen abgeleiteten Baufeldern (≈ 27 × 19 m Baufenster) passt der Fußabdruck nicht (siehe Grundstücksanalyse).	kritisch / offen: Außenkante OG auf angenommener Grenze (0,00 m). Entwurf: Baugrenze 3,0 m zu Planstraße/Parkplatz – der Vorbau über die Baugrenze ist unzulässig; auf den aus den amtlichen Plänen abgeleiteten Baufeldern (≈ 27 × 19 m Baufenster) passt der Fußabdruck nicht (siehe Grundstücksanalyse).	kritisch / offen: Außenkante OG auf angenommener Grenze (0,00 m). Entwurf: Baugrenze 3,0 m zu Planstraße/Parkplatz – der Vorbau über die Baugrenze ist unzulässig; auf den aus den amtlichen Plänen abgeleiteten Baufeldern (≈ 27 × 19 m Baufenster) passt der Fußabdruck nicht (siehe Grundstücksanalyse).	kritisch / offen: Außenkante OG auf angenommener Grenze (0,00 m). Entwurf: Baugrenze 3,0 m zu Planstraße/Parkplatz – der Vorbau über die Baugrenze ist unzulässig; auf den aus den amtlichen Plänen abgeleiteten Baufeldern (≈ 27 × 19 m Baufenster) passt der Fußabdruck nicht (siehe Grundstücksanalyse).
Stellplätze (gesetzlich)	kritisch / offen: 9 nutzbar < erforderlich Mittel 13,6 (11,4–16,9): Ablöse/Mitbenutzung nötig	kritisch / offen: 9 nutzbar < erforderlich Mittel 13,6 (11,4–16,9): Ablöse/Mitbenutzung nötig	kritisch / offen: 9 nutzbar < erforderlich Mittel 13,6 (11,4–16,9): Ablöse/Mitbenutzung nötig	voraussichtlich ok: 21 nutzbar ≥ erforderlich bis 12,5
Gewerbe im EG	zu prüfen: EG 492 m² (B3: 576 m²); Gastraum ca. 281 m².	zu prüfen: EG 492 m² (B3: 576 m²); Gastraum ca. 281 m².	zu prüfen: EG 492 m² (B3: 576 m²); Gastraum ca. 281 m².	zu prüfen: EG 358 m² (B3: 576 m²); Gastraum ca. 198 m².
Brandschutz / Feuerwehr	zu prüfen: Vorbau über Stellplätzen/Fahrgasse, Aufstellflächen und Feuerwehrzufahrt, Rettungswege – Konzept erforderlich.	zu prüfen: Vorbau über Stellplätzen/Fahrgasse, Aufstellflächen und Feuerwehrzufahrt, Rettungswege – Konzept erforderlich.	zu prüfen: Vorbau über Stellplätzen/Fahrgasse, Aufstellflächen und Feuerwehrzufahrt, Rettungswege – Konzept erforderlich.	zu prüfen: Vorbau über Stellplätzen/Fahrgasse, Aufstellflächen und Feuerwehrzufahrt, Rettungswege – Konzept erforderlich.

Offene Fragen und Prüfbedarf

VARIANTE E · NICHT FESTGELEGT

Vor jeder Weiterentwicklung zu klären

• Fotos der städtischen Unterlagen (S. 13, 15, 16) in den Projektordner; daraus Grundstückszuschnitt, Baugrenzen, GRZ, Höhenbezugspunkt, Traufhöhe, Dachform, Abstände, Festsetzungen zu Stellplätzen/Zufahrten.
• Bebauungsplan-Stand: Entwurf (S. 15) – rechtskräftige Fassung; örtliche Bauvorschrift/Stellplatzsatzung für Nicht-Wohnungen; städtebaulicher Vertrag/Kaufvertrag (Stellplätze auch für Wohnungen möglich).
• Einstufung der Gaststätte („örtliche“ oder „überörtliche Bedeutung“), Sitzplatzzahl innen/außen, Büro mit/ohne Besucherverkehr.
• Höhenbezug der 12,00 m; Vollgeschoss-Definition für das 2. OG; Traufhöhe 6,50 m.
• Überbauung des Platzes (F1–F3: 1,5 m), Grenz- und Abstandsflächen, GRZ-Anrechnung überdeckter Stellplätze.
• Zufahrt: Straße, Gefälle, Sichtdreiecke; Feuerwehrzufahrt/Aufstellflächen unter dem Vorbau; Wendemöglichkeit in der Sackgasse (F1–F3).
• Stellplatzmaße/Garagenverordnung für Stellplätze neben Säulen und Parallelparker; Schleppkurven.
• Statik: Kragarme 1,0–5,0 m, Säulenraster 5,4 m, Fundamente; Brandschutz Vorbau.

Keine Variante ist ausgewählt.