Variante F – Erdgeschoss 540 m² (18 × 30 m) mit umlaufendem Vorbau und Parke[illegible]

VARIANTE F · NICHT FESTGELEGT

Entwurfsstudie Neue Mitte Werlte – Baufeld 3 · Planungsziel 540 m² Gebäude + 420 m² Restfläche · keine Variante festgelegt

Ziel: Gebäudehöhe bis 12,00 m planerisch ausnutzen (drei Geschosse, keine zusätzlichen), umlaufender säulengestützter Vorbau, Zufahrt und Stellplätze unter und neben dem Vorbau. Keine Variante ist festgelegt; B3 (Variante A) und alle bestehenden Modelle bleiben unverändert. Alle Flächen sind vorläufig, bis Grundstücksgrenzen und Baugrenzen verlässlich geklärt sind.

	Bestätigt (Quelle)	Annahme / unbestätigt
Grundstück	ca. 960 m² (Projektangabe); amtliche Unterlagen: B-Plan 123, 1. Änderung (Entwurf) mit Baugrenze 3,0 m zu Planstraße/Parkplatz	Zuschnitt 32 × 30 m = Hypothese H1; aus Nutzungskonzept abgeleitete Kandidaten ca. 33 × 25 m / 35 × 27 m (±2 m); Foto-Seiten 13/15/16 fehlen
Höhe / Geschosse	Entwurf B-Plan 123, 1. Änd.: H = 12,00 m über OK Fahrbahn, SH ≤ 0,30 m, TH 6,50 m, zwingend II Vollgeschosse, Dach ≥ 38°; 2–3 Geschosse laut Auftraggeber	Plan nur ENTWURF, Ursprungsplan unbekannt; 12 m gelten erst nach Klärung (Fahrbahnhöhe, Dachform, Vollgeschosse) als eingehalten
Stellplätze Wohnen	KEINE gesetzliche Pflicht seit 01.07.2024 (§ 47 Abs. 1 Satz 3 NBauO; FAQ Land Niedersachsen Stand 11.07.2025)	ob B-Plan/städtebaulicher Vertrag/Kaufvertrag Stellplätze für Wohnungen verlangt: unbekannt
Stellplätze Gastro/Büro	Pflicht besteht; Bemessung bedarfsorientiert (Richtzahlen Erlass: Gaststätte 1 je 8–12 Sitzplätze, Büro 1 je 30–40 m²)	Gaststättenart („örtliche Bedeutung“) und Sitzplatzzahl angenommen
Maße	–	Stellplatz 2,50 × 5,00 m, Fahrgasse 6,00 m, Säule Ø 0,40 m (Vorgaben/Annahmen), Zufahrtslage
Wohnfläche	B3: 846 m², 16 WE (Plan)	übrige Varianten aus Geschosskonturen geschätzt (0,88 × Wohnstreifen)

Grundstück, Baugrenzen und Quellenstatus

VARIANTE F · NICHT FESTGELEGT

Was gesichert ist, was nur aus Beschreibungen stammt und was Hypothese ist


Punkt	Stand	Herkunft / Bemerkung
Grundstücksfläche ca. 960 m²	GESICHERT (Projektangabe)	Projektunterlagen/Auftraggeber; nicht am Liegenschaftsnachweis geprüft
Zuschnitt 32 × 30 m	HYPOTHESE H1	Nur aus 960 m² und B3-Annahme; weder vermessen noch aus einem Plan gemessen
B-Plan Nr. 123 „Ehemalige Grundschule“, 1. Änderung (Entwurf 25.09.2026): MI, GRZ 0,6, II zwingend, TH 6,50 m, H 12,00 m, SH 0,30 m, Baugrenze 3 m	GESICHERT (Entwurf)	amtliche Unterlagen der Stadt Werlte (sgwerlte.de), in quellen_stadt/ abgelegt; nicht rechtskräftig
Foto-Seiten 13/15/16 des Auftraggebers („zwei- bis dreigeschossig“)	FEHLEN	ZIP nicht angekommen; Seite 15/16 entsprechen vermutlich Abb. 2/3 der 1. Änderung (unbestätigt)
Zuordnung „Baufeld 3“ im Nutzungskonzept	UNBEKANNT	ohne Seite 13 nicht bestimmbar; Kandidaten K1/K2 abgeleitet
Baugrenzen / Baulinien, GRZ, Abstandsflächen	UNBEKANNT	keine Maße am Plan abgelesen; alle Konturen in den Plänen sind Hypothese
Erschließungsstraße, Zufahrt, Platzseite	ANNAHME	Platz an der Seite y = 0; Zufahrt von Osten (E) bzw. Süden (F) angenommen
Stellplatz 2,50 × 5,00 m, Fahrgasse 6,00 m	ANNAHME (Auftraggeber, vorläufig)	Abgleich mit Stellplatzsatzung/Garagenverordnung ausstehend

Die ZIP-Datei mit den Fotos der Seiten 13, 15 und 16 ist in dieser Sitzung nicht angekommen; der Ordner quellen_stadt/fotos_stadt_unterlagen/ ist leer. Grundlage sind die amtlichen Planunterlagen der Stadt (Entwurf B-Plan 123, 1. Änderung). Konturen aus den Plänen sind als ABGELEITET (±2 m) gekennzeichnet, gesicherte Maße getrennt.

Planungsrecht: Höhe 12,00 m und ihr Bezugspunkt

GRUNDSTÜCK · TEILWEISE ABGELEITET

B-Plan Nr. 123, 1. Änderung, Entwurf (Textliche Festsetzung 1.2) · Antwort auf: verbindlich festgesetzt? von wo gemessen?

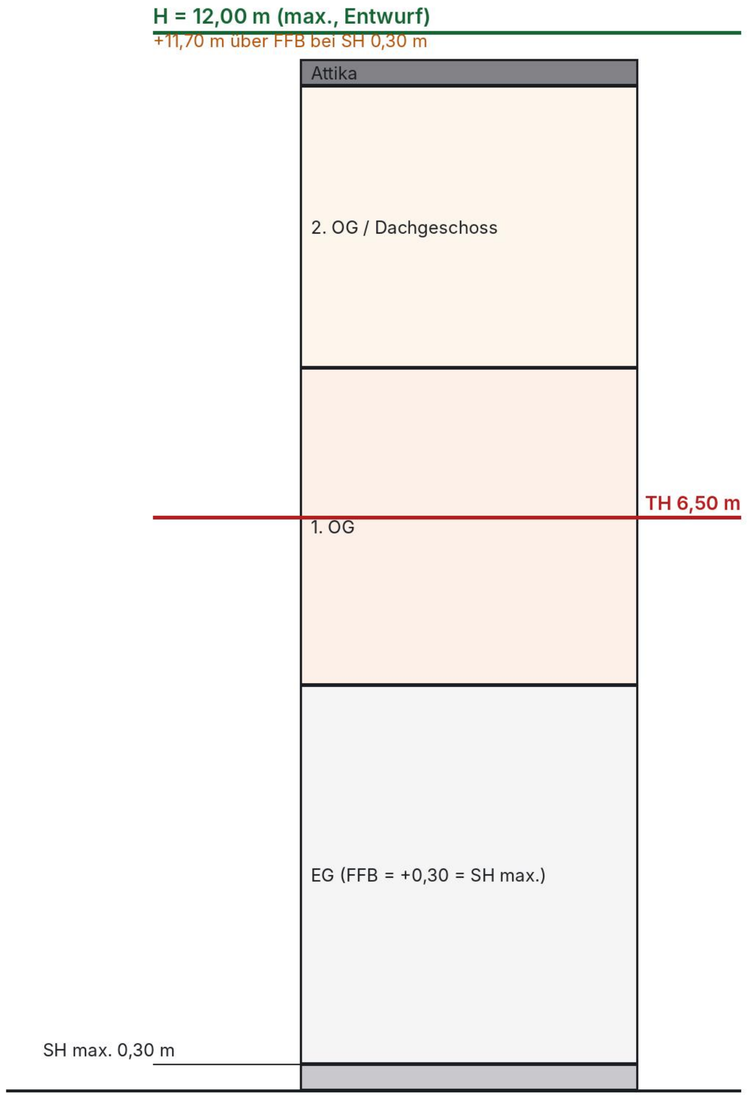


Frage	Antwort
Ist 12 m verbindlich festgesetzt?	Im ENTWURF der 1. Änderung (H = 12,00 m). Satzungsbeschluss steht aus; der rechtskräftige Ursprungsplan 123 (14.04.2023) liegt nicht vor. → Nicht als verbindlich nachgewiesen.
Von wo gemessen?	Unterer Bezugspunkt: Oberkante Fahrbahn der nächstgelegenen ausgebauten Erschließungsstraße in der Mitte vor dem Baukörper (Höhe beim Bauamt erfragbar). Oberer Punkt: Oberkante Baukörper (First, Hauptgesims); untergeordnete Teile (Antennen, Schornsteine) zählen nicht.
Verhältnis zu FFB EG	FFB EG max. 0,30 m über dem Bezugspunkt (SH). Bei SH 0,30 m: Baukörper max. +11,70 m über FFB; E/F zeichnen +12,00 m über FFB → bei SH > 0 überschritten, nur bei FFB = Fahrbahnhöhe möglich.
Traufhöhe	max. 6,50 m (Schnittkante Mauerwerk/Dachhaut): Oberkante 1. OG der Entwürfe (+7,90 / +8,20 m) liegt darüber.
Vollgeschosse / Dach	II zwingend; Hauptdach geneigt ≥ 38° (Flachdach nur Verbindungsbauten, ≥ 1,0 m unter First, bzw. untergeordnete Teile ≤ 70 m²). Dreigeschossige Flachdachbauten (B3, B, C, E, F) passen nicht zum Entwurf.
Fazit	Die 12,00 m bleiben Planungsziel, gelten aber erst als eingehalten, wenn (1) Ursprungsplan/Satzung für Baufeld 3 vorliegt, (2) Fahrbahnhöhe vor dem Baukörper bekannt ist, (3) Traufe/Dachform/Vollgeschosse geklärt sind.

Abgeleitete Grundstückskonturen (Näherung aus dem Nutzungskonzept)

GRUNDSTÜCK · TEILWEISE ABGELEITET

Blau: Kandidat K1, grün: Kandidat K2, orange: Baufenster K1 (3 m Abstand) · Maßstabsabgriff aus Abb. 3, ±2 m · KEINE vermessenen Grenzen

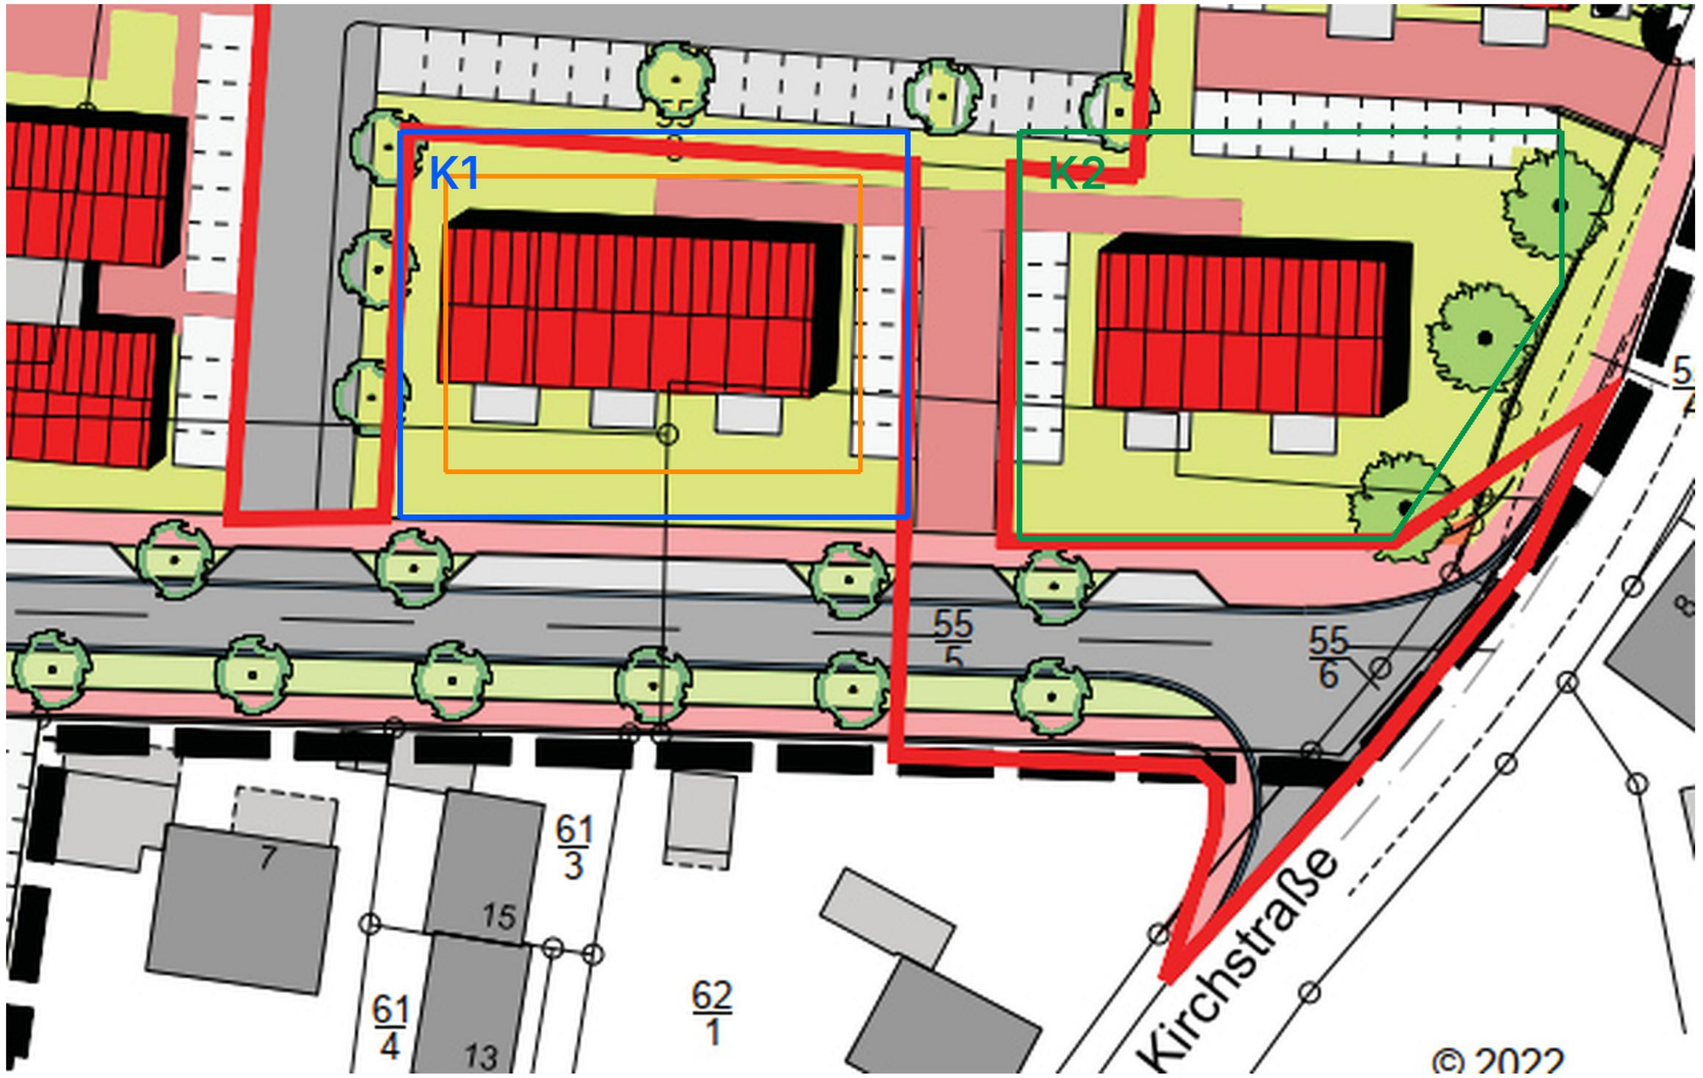

Ableitung: Maßstab 1:1000 der Abbildung; Straßenbreite Planstraße 16 m und Stichstraße/Parkplatz-Arm 11 m dienten als Kontrolle. Die grünen Flächen zwischen Planstraße (Süden), Parkplatz (Norden), Stichstraße (Westen) und Fuß-/Radweg (Osten) sind als Baufelder abgegrenzt; Parzellengrenzen sind in der Abbildung nicht eingezeichnet.


K1: ca. 33 × 25 m ≈ 830 m². K2: ca. 35 × 27 m ≈ 900 m² (Trapez). Die Projektangabe 960 m² passt zu keinem der beiden genau; Baufeld 3 kann also ein anderes Baufeld sein oder Teile der angrenzenden Wege einschließen. Die Zuordnung erfordert Seite 13/15/16 des Auftraggebers.

Baugrenzen (Entwurf): 3,0 m Abstand zu Planstraße und Parkplatz (gesichert); Ost/West angenommen. Baufenster K1 ≈ 27 × 19 m = 513 m².

Lageplan Kandidat K1: Baufenster und Gebäudefußabdrücke

GRUNDSTÜCK · TEILWEISE ABGELEITET

Maße in m, Näherung ±2 m · Baugrenze N/S 3,0 m gesichert, W/O 3,0 m angenommen · Parken auf eigener Fläche nach Fußabdruck

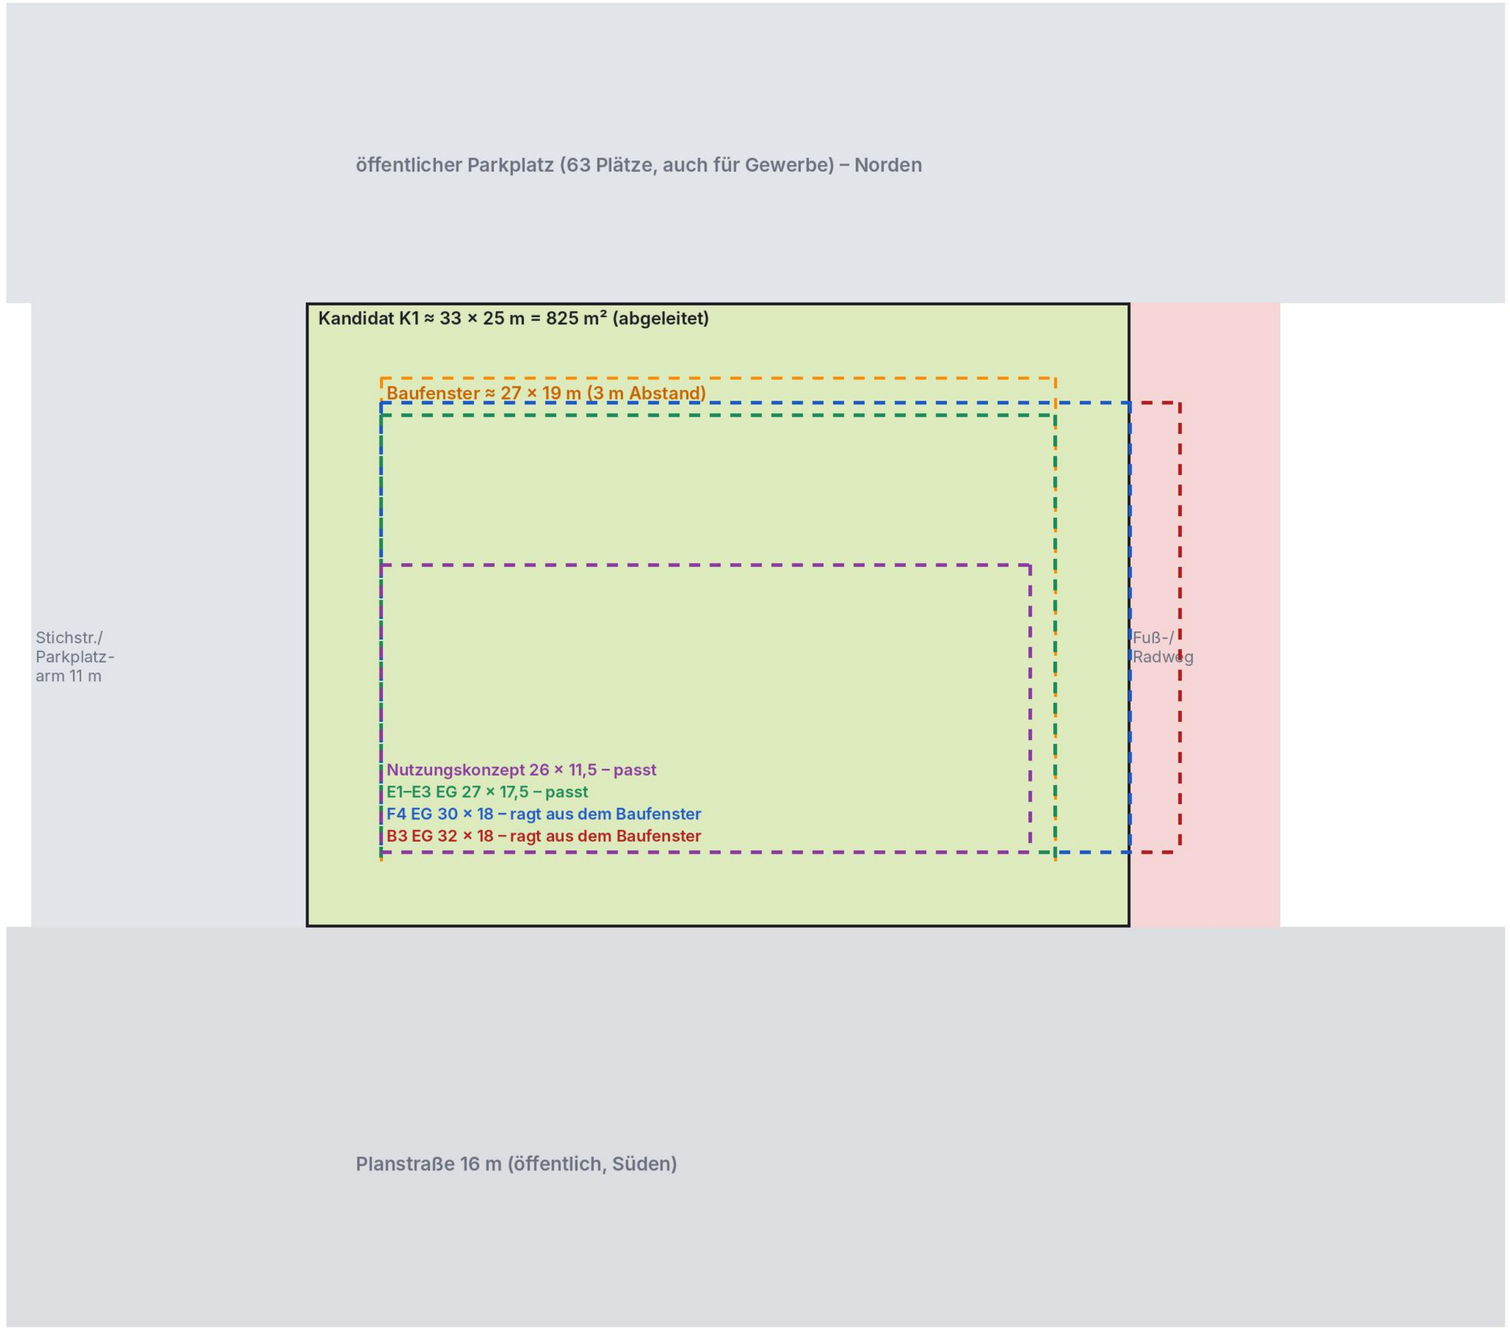

Fußabdruck	Baufenster K1 27 × 19	Baufenster K2 ≈ 29 × 21
B3 / A, B, C, D: EG 32 × 18 m	passt NICHT	passt NICHT
E1–E3: EG 27 × 17,5 m	passt	passt
E4: EG 27 × 12,5 m	passt	passt
F1–F3: EG 18 × 30 m (30 m tief)	passt NICHT	passt NICHT
F4: EG 30 × 18 m	passt NICHT	passt NICHT
Nutzungskonzept (Abb. 3): ca. 26 × 11,5 m	passt	passt


Befund (unter dem Vorbehalt der Kandidatenwahl): Der Entwurf B3 (EG 32 × 18 m, 576 m²) passt in keines der beiden Baufenster. F mit 540 m² passt nur in der gedrehten Lesart (30 × 18 m) und nur bei breiterem Baufenster; die wörtliche Lesart 18 × 30 m (30 m tief) passt nicht. Umlaufender Vorbau über die Baugrenze und Parken unter dem Vorbau auf eigener Fläche sind auf den abgeleiteten Grundstücken nicht möglich. Stellplätze für Gastro/Büro müssten über den öffentlichen Parkplatz (63 Plätze, Baulast/Mitnutzung ungeklärt) oder die vom Nutzungskonzept vorgesehenen privaten Stellplätze neben den Gebäuden nachgewiesen werden.

Parken auf K1: nach Abzug von Baufenster und Baugrenzstreifen (3 m) bleiben ≤ 3–4,5 m Tiefe → keine 5-m-Stellplätze mit Fahrgasse; allenfalls Längsparker im Südstreifen (Ausfahrt über Gehweg ungeklärt).

Höhenrahmen: B3 (+9,90 m) gegen 12,00 m – mit Bezugspunkt nach Entwurf B-Plan 123, 1. Änderung

VARIANTE F · NICHT FESTGELEGT

Schnittschema und Raumhöhen · alle Höhen vorläufig · 12,00 m gelten erst nach Klärung des Bezugspunkts als eingehalten

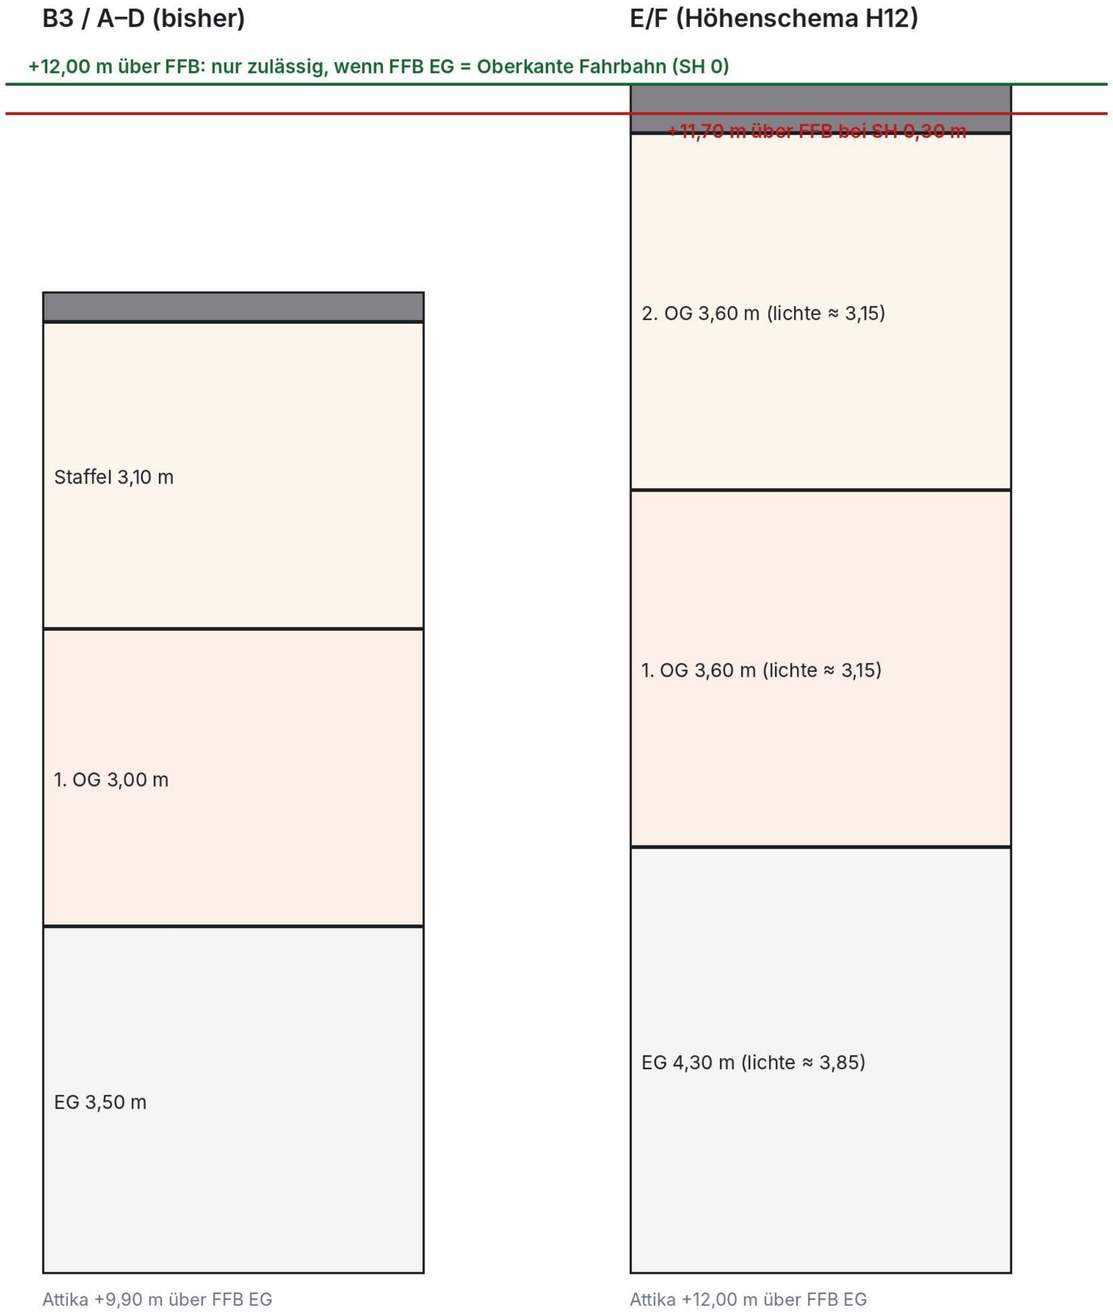

Aspekt	Aussage (Quelle: B-Plan Nr. 123, 1. Änderung, Entwurf 25.09.2026)
Bezugspunkt	H = 12,00 m über Oberkante Fahrbahn der nächstgelegenen ausgebauten Erschließungsstraße in der Mitte vor dem Baukörper (nicht über FFB). FFB EG max. 0,30 m darüber (SH). Fahrbahnhöhe unbekannt.
Rechtsstand	Entwurf; Ursprungsplan 123 (rechtskräftig 14.04.2023) liegt nicht vor. 12 m daher NICHT als verbindlich nachgewiesen.
Folge für E/F	Attika +12,00 m über FFB ist bei SH > 0 zu hoch (+11,70 m max.). Alternative H11,70: EG 4,10 / OG 3,55 / OG 3,55 / Attika 0,50.
Traufhöhe / Dach	TH max. 6,50 m, geneigtes Dach ≥ 38°, zwingend II Vollgeschosse (Entwurf): dreigeschossige Flachdachbauten passen nicht dazu.
Nutzung der Reserve	Statt eines vierten Geschosses (nicht angenommen) fließt die Höhe in Geschosshöhen (lichte ≈ 3,15 m); Wohnfläche steigt dadurch nicht.

Planungsziel EG 540 m² + 420 m² Restfläche: Prüfung gegen die Hypothese

VARIANTE F · NICHT FESTGELEGT

18 m × 30 m = 540 m² Gebäude, 960 − 540 = 420 m² für Zufahrt, Fahrgasse, Stellplätze, Freiflächen

Lesart	Anordnung auf H1 (32 × 30 m)	Vereinbar?	Bemerkung
F1–F3 wörtlich: 18 m Platzseite × 30 m Tiefe	EG x 1–19, y 0–30; Restfläche = Streifen 14 × 30 m (+1 m Westrand)	geometrisch ja, mit Abweichung	EG füllt die ganze Grundstückstiefe: rückseitig KEIN Vorbau und keine Rückfahrfläche; Vorbau vorn ragt 1,5 m in den Platz (Überstand!); Zufahrt nur von Süden
F4 gedreht: 30 m Platzseite × 18 m Tiefe	EG x 1–31, y 1–19; Restfläche = hinterer Streifen 32 × 11 m + Ränder	ja	Vorbau rundum innerhalb H1 (vorn/seitlich 1,0 m, hinten 5,0 m über der Stellplatzreihe); eine Stellplatzreihe + 6-m-Fahrgasse
Baugrenzen/Abstände	unbekannt	NICHT PRÜFBAR	Baufenster geschätzt 400–460 m² (project_brief, nicht gemessen) läge unter 540 m²; ohne Planfoto keine Aussage

Restfläche 420 m² (EG 540 m²)	F1–F3	F4
Stellplätze (funktionierend)	155,0 m²	112,5 m²
Fahrgasse 6,00 m	180,0 m²	192,0 m²
Zugangszonen (Eingänge)	12,5 m²	16,2 m²
nur rechnerisch verbleibend (nicht nutzbar)	72,5 m²	99,2 m²
Summe Restfläche	420,0 m²	420,0 m²

Ergebnis: Die 420 m² sind nicht vollständig Stellplatzfläche. Nach Abzug von Fahrgasse (180–192 m²), Zugängen und Randstreifen bleiben rund 100–155 m² für Stellplätze = 8–13 Plätze (F1–F3: 8 Plätze 90° + 5 Parallelparker; F4: 9). Der verbleibende Rest ist nur rechnerisch vorhanden.

Überblick F1–F4

VARIANTE F · NICHT FESTGELEGT


Standardmix · alle Werte vorläufig · Referenz B3 (A)

Kennzahl	A B3	F1 EG 18×30 m, Vorbau bis Attika	F2 EG 18×30 m, Staffel 1,50 m	F3 EG 18×30 m, Staffel 3,00 m	F4 EG 30×18 m (gedreht), Staffel
Staffelrücksprung	0,8 m	0.0 m	1.5 m	3.0 m	1.5 m
Grundfläche EG / 1. OG / 2. OG (m²)	576 / 660 / 539	540 / 756 / 756	540 / 756 / 598	540 / 756 / 459	540 / 768 / 609
Wohnfläche netto (m²)	846	1.065	942	835	960
Δ Wohnfläche gg. A	±0	+219 (+26 %)	+96 (+11 %)	-11 (-1 %)	+114 (+13 %)
Wohnungen	16	14	14	13	16
Gastraum (m²) / Plätze innen	280 / 120	232 / 99	232 / 99	232 / 99	307 / 132
Stellplätze gezeichnet / nutzbar	11 / 11	13 / 13	13 / 13	13 / 13	9 / 9
erforderlich § 47 (Spanne / Mittel)	11,4–16,9 / 13,6	9,7–14,3 / 11,6	9,7–14,3 / 11,6	9,7–14,3 / 11,6	12,4–18,3 / 14,8
optional Wohnen (0,5–1,5 je WE)	8–24	7–21	7–21	6–20	8–24
Säulen	0	18	18	18	22
Höhe Attika	9,90 m	12,00 m (Bezug offen)	12,00 m (Bezug offen)	12,00 m (Bezug offen)	12,00 m (Bezug offen)

F1 – EG 18×30 m, Vorbau bis Attika

Entwurfsstudie Baufeld 3 · Konzeptvariante, keine Genehmigungsplanung

VARIANTE F · NICHT FESTGELEGT

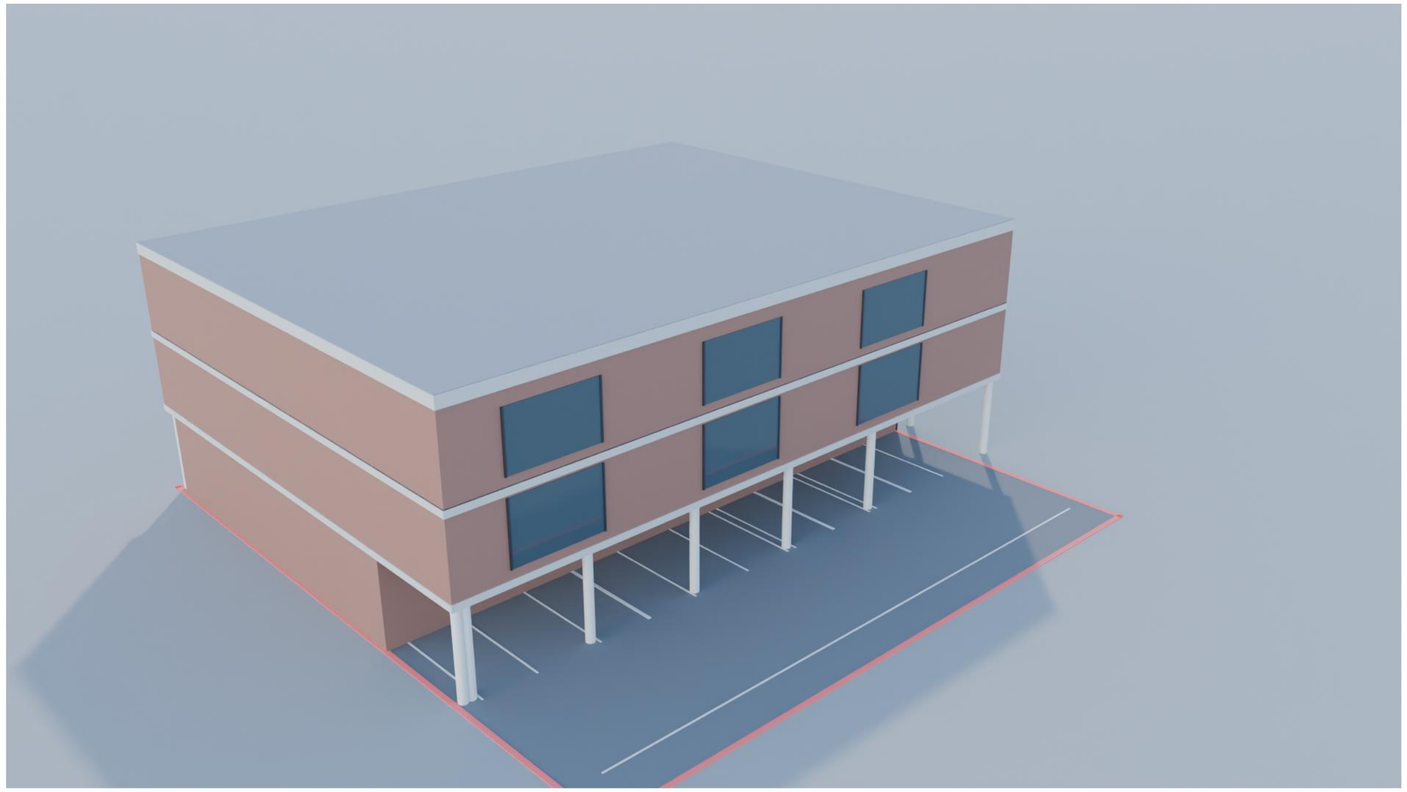

Erdgeschoss 18 × 30 m = 540 m² (Platzseite 18 m, Tiefe 30 m = volle Grundstückstiefe); 1. und 2. OG kragen 1,0 m nach Westen, 5,0 m nach Osten (über die Stellplatzreihe) und 1,5 m zum Platz aus und sind deckungsgleich bis zur Attika +12,00 m. Rückseite ohne Vorbau (Grundstücksgrenze).

Kennzahl	Wert (vorläufig)
Höhe	12,00 m Attika (EG 4,30 · 1. OG 3,60 · 2. OG 3,60 · Dach/Attika 0,50), 3 Geschosse – Höhenbezug offen
Grundfläche EG / 1. OG / 2. OG	540 / 756 / 756 m²
Außenmaße EG / 1. OG / 2. OG	18.0 × 30.0 / 24.0 × 31.5 / 24.0 × 31.5 m
Wohnfläche netto (geschätzt)	1.065 m²
Wohnungen Standardmix	14 WE (7 + 7), 66–89 m², Ø 76 m²
Gewerbe	EG 540 m²; Gastraum ca. 232 m² (≈ 99 Plätze), Terrasse/Arkade ≈ 25 Plätze, Büro 56 m²
Säulen	18 Säulen Ø 0,40 m; Paare 5,4 m (zwei Stellplätze + Säule)
Stellplätze gezeichnet	13: 8 voll nutzbar, 5 eingeschränkt, 0 Konflikt
Stellplätze erforderlich (§ 47 NBauO)	9,7–14,3, Mittel 11,6 (nur Gastro + Büro; Wohnen 0)
Stellplätze optional (Komfort/Markt)	Wohnen 0,5–1,5 je WE = 7–21; Komfortziel gesamt ≈ 26
Überstand über Grundstück H1	1,50 m

Alle Maße sind Planungsannahmen: Stellplatz 2,50 × 5,00 m, Fahrgasse 6,00 m, Säule Ø 0,40 m, Grundstück 32 × 30 m (Hypothese; die städtischen Unterlagen Seite 13/15/16 liegen nur als Beschreibung vor, nicht als Foto), Zufahrt = Annahme. Wohnfläche = 0,88 × Wohnstreifen, schematisch. Nichts ist genehmigt, bemessen oder abgestimmt.


F1: Lageplan mit Gebäude, Säulen, Zufahrt und Stellplätzen

F1 – EG 18×30 m, Vorbau bis Attika · grün = Stellplatz funktioniert, orange = eingeschränkt, rot = Konflikt, rosa = nur rechnerisch verbleibende Fläche

VARIANTE F · NICHT FESTGELEGT

Lageplan F1 – Gebäude, Säulen, Zufahrt, Stellplätze

Grundstück H1 32 × 30 m HYPOTHETISCH (Zuschnitt/Baugrenzen nicht belegt) · Stellplatz 2,50 × 5,00 m, Fahrgasse 6,00 m = Planungsannahmen · Zufahrt = Annahme

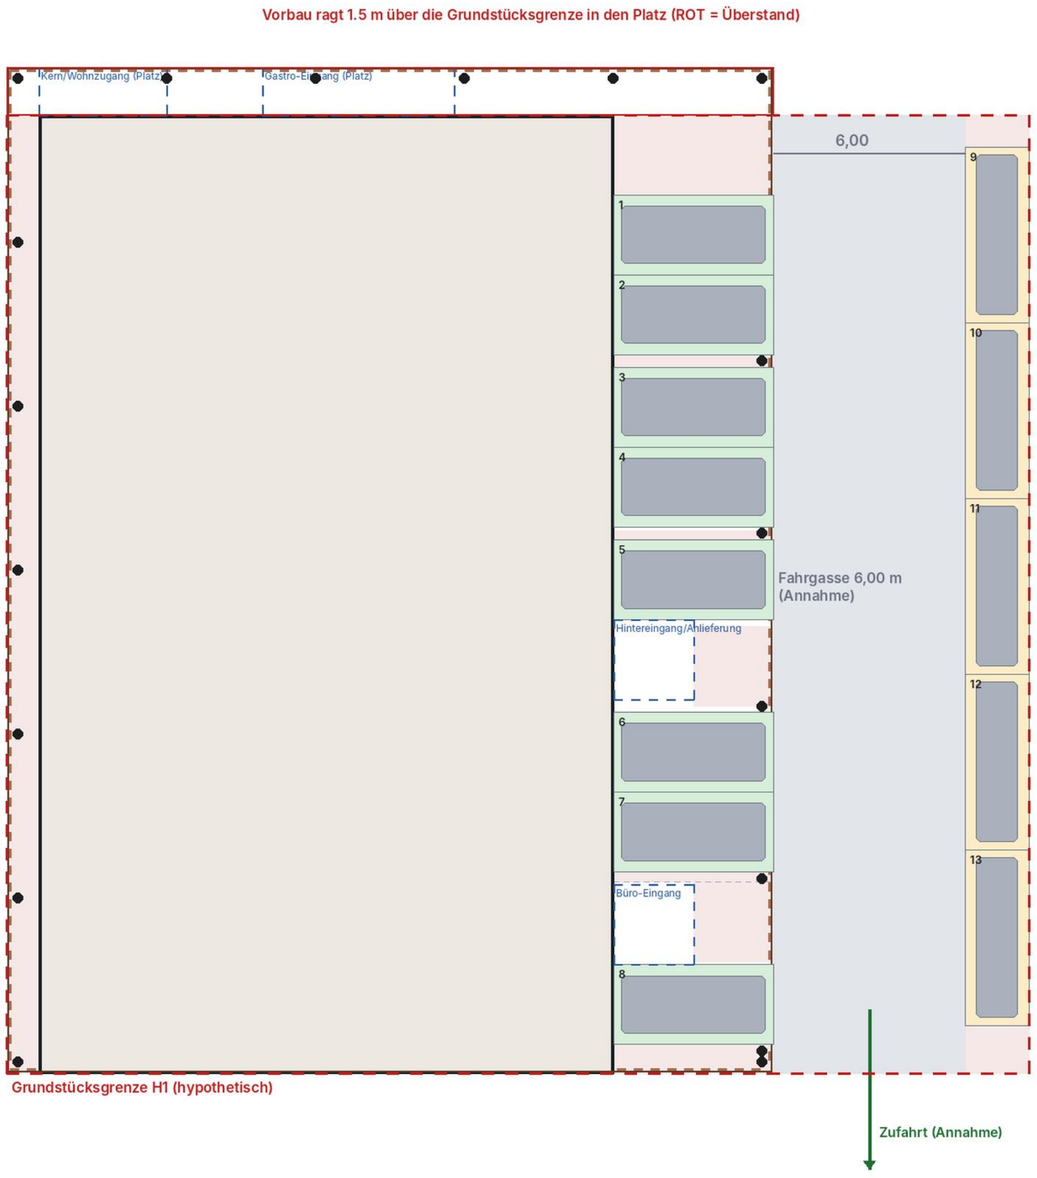

Stellplätze gezeichnet: 13
funktionieren voll: 8
eingeschränkt: 5
Konflikt: 0
Fläche (960 m²): EG 540 · Stellpl. 155 · Fahrgasse 180 · Zugänge 12
nur rechnerisch (nicht nutzbar): 72 m²
Überstand über H1: 1.50 m
OG im 3-m-/6-m-Randstreifen: 252 / 432 m²

Stellplatz funktioniert · eingeschränkt · Konflikt · Fahrgasse · nur rechnerisch verbleibend

braun gestrichelt: 1./2. OG über dem EG (Vorbau) · blau gestrichelt: Eingangszonen

Stellplatzprüfung	
Gezeichnet	13
funktionieren voll	8
eingeschränkt	5
Konflikt	0
Min. Nutzbreite 90°	2.50 m
Fahrgasse	6.0 m (frei)
Flächenbilanz 960 m²	
Erdgeschoss	540,0 m²
Stellplätze	155,0 m²
Fahrgasse	180,0 m²
Zugangszonen	12,5 m²
nur rechnerisch	72,5 m²

- Fahrgasse ist Sackgasse zum Platz hin: Wenden im Gassenende (Dreipunktwende) nötig – Schleppkurve prüfen
- Geometrische Prüfung ohne Schleppkurven; 90°-Stellplätze 2,50 × 5,00 m und Fahrgasse 6,00 m sind Planungsannahmen
- Zufahrt (Lage der Straße) ist Annahme
- Feuerwehrzufahrt/Aufstellflächen unter dem Vorbau nicht nachgewiesen (Prüfbedarf)

F1: Grundrisse EG, 1. OG, 2. OG


F1 – EG 18×30 m, Vorbau bis Attika · schematisch

VARIANTE F · NICHT FESTGELEGT

Erdgeschoss

F1: Erdgeschoss (schematisch)

Grundriss schematisch · Wohnungsaufteilung = Streifenmodell (Mittelgang 2,0 m), netto = 0,88 × brutto · Säulen Ø 0,40 m · Grundstück H1 hypothetisch

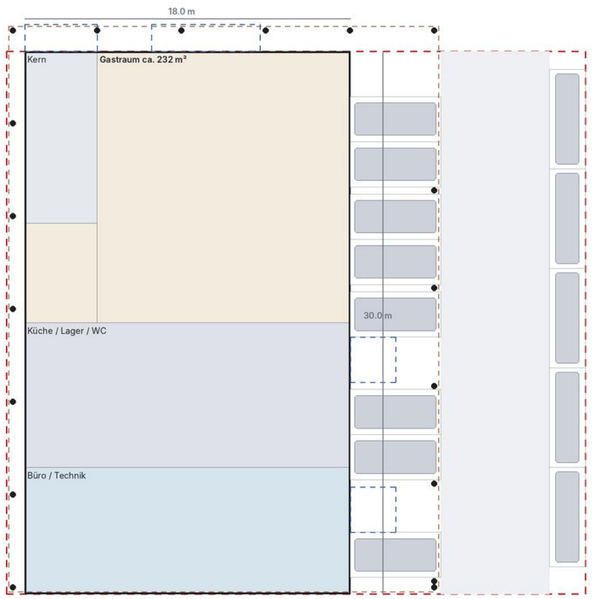


Fläche Geschoss 540 m²

Wohnung (schematisch) Kern Gastronomie Terrasse/Dach schraffiert

1. Obergeschoss

F1: 1. Obergeschoss (schematisch)

Grundriss schematisch · Wohnungsaufteilung = Streifenmodell (Mittelgang 2,0 m), netto = 0,88 × brutto · Säulen Ø 0,40 m · Grundstück H1 hypothetisch

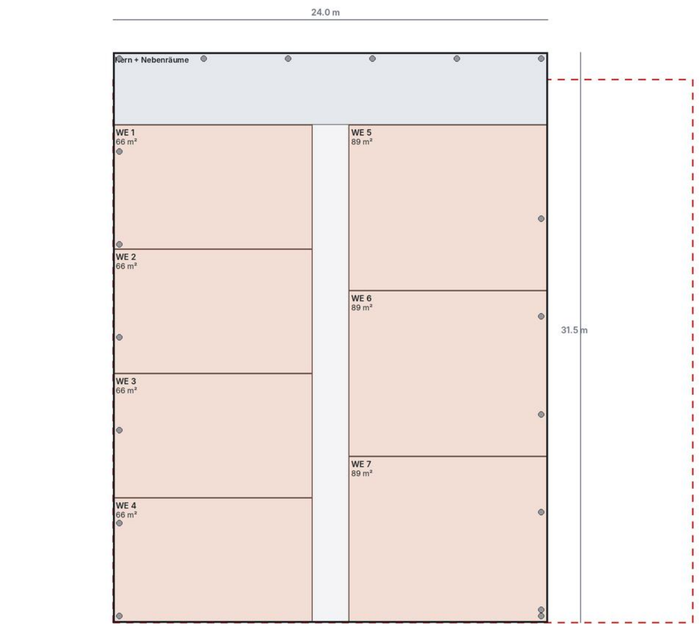


Fläche Geschoss 756 m²

Wohnung (schematisch) Kern Gastronomie Terrasse/Dach schraffiert

2. Obergeschoss

F1: 2. Obergeschoss (schematisch)

Grundriss schematisch · Wohnungsaufteilung = Streifenmodell (Mittelgang 2,0 m), netto = 0,88 × brutto · Säulen Ø 0,40 m · Grundstück H1 hypothetisch

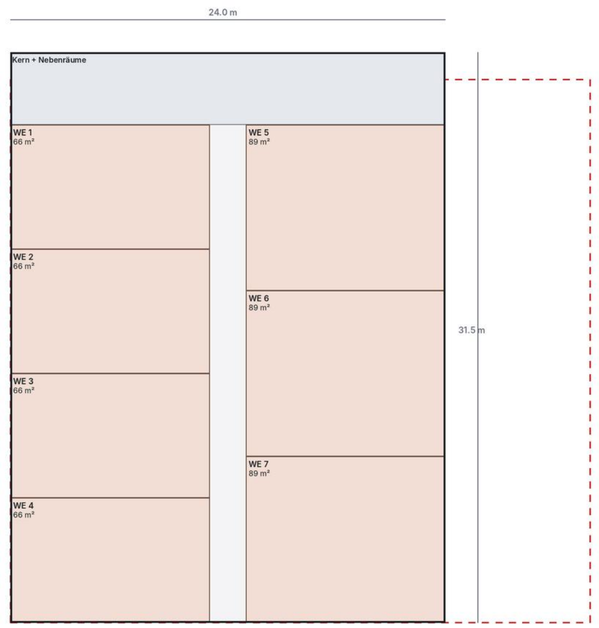

Fläche Geschoss 756 m²

Wohnung (schematisch) Kern Gastronomie Terrasse/Dach schraffiert

F1: vier Fassaden

VARIANTE F · NICHT FESTGELEGT

F1 – EG 18×30 m, Vorbau bis Attika · orthogonale Ansichten aus dem 3D-Modell


Vorderfassade (Platzseite)




Rückfassade



Seitenfassade West

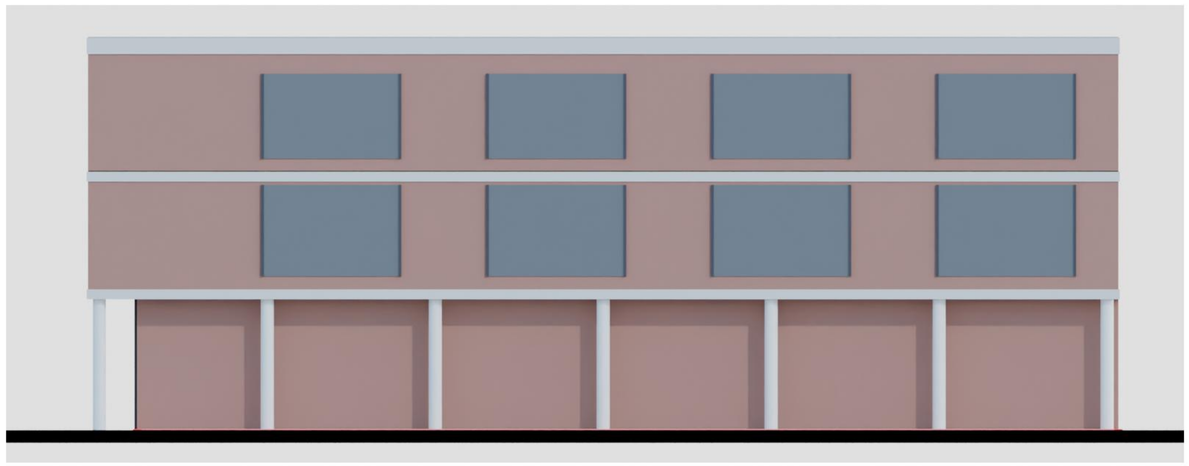

Seitenfassade Ost

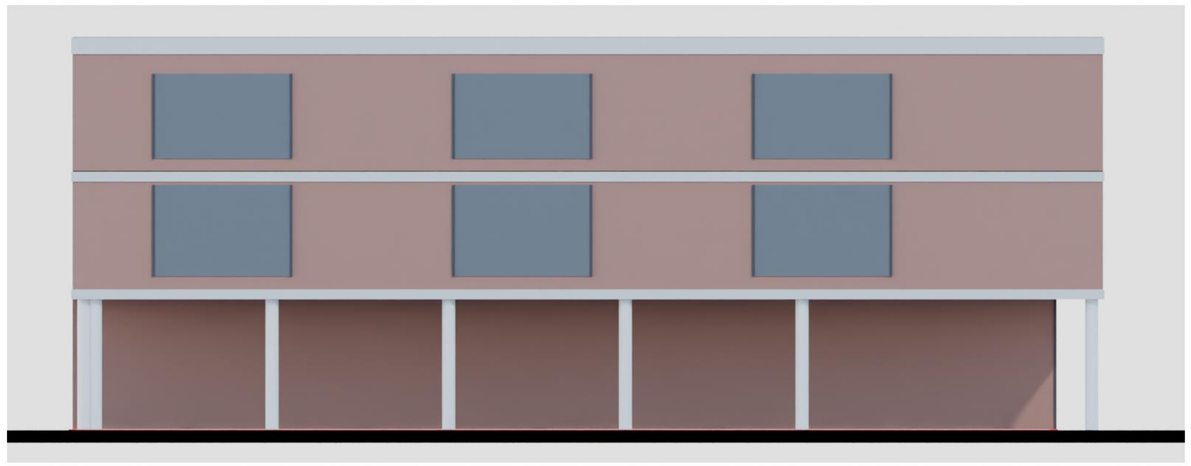

F1: Gebäudeschnitt mit Geschosshöhen und 3D-Ansichten

F1 – EG 18×30 m, Vorbau bis Attika


VARIANTE F · NICHT FESTGELEGT


F1: Gebäudeschnitt mit Geschosshöhen (schematisch)

Westseite links, Ostseite rechts · Schnitt bei y = 15.0 m · Höhenbezug ±0,00 = OK Fertigfußboden EG (Planbezug Blatt 14) – Bezugspunkt der Stadt für die 12,00 m ist NICHT belegt



Geschosshöhen: EG 4,30 m · 1. OG 3,60 m · 2. OG 3,60 m · Dach/Attika 0,50 m = 12,00 m. Reserve 0,00 m. Die 12,00 m gelten erst als eingehalten, wenn der baurechtliche Höhenbezug geklärt ist.
Säulen im Schnittbereich: 2 · Säulen insgesamt: 18 · Vorbau-Unterkante +4,00 m (Decke 0,30 m)

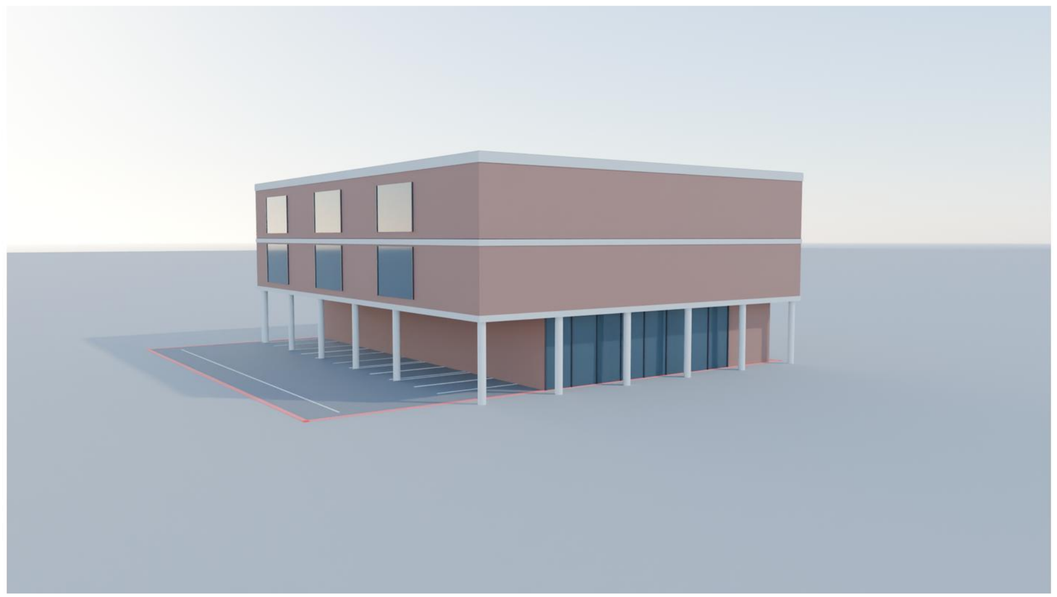


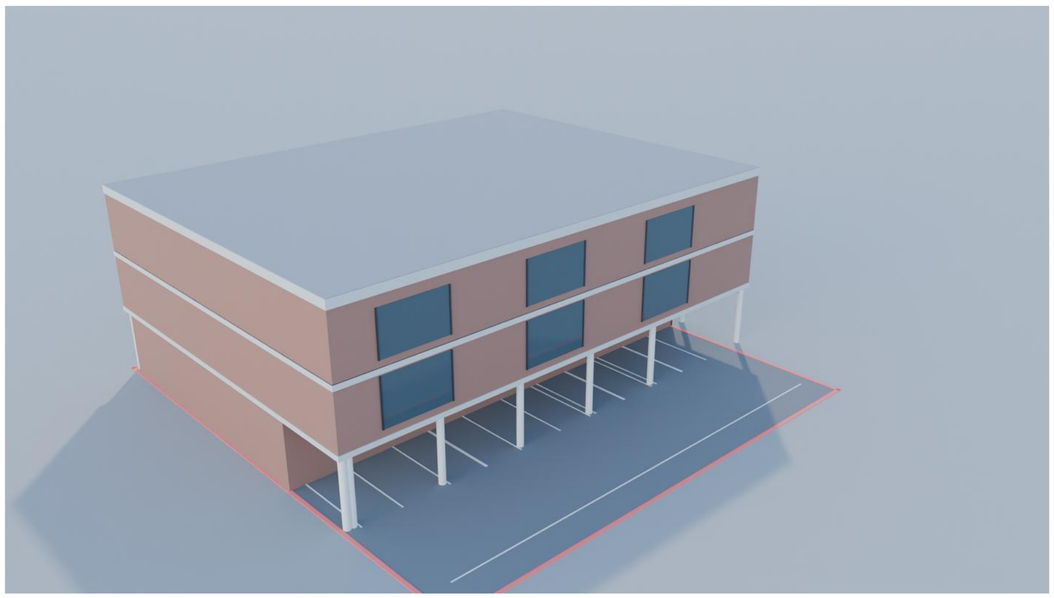

F2 – EG 18×30 m, Staffel 1,50 m

Entwurfsstudie Baufeld 3 · Konzeptvariante, keine Genehmigungsplanung

VARIANTE F · NICHT FESTGELEGT

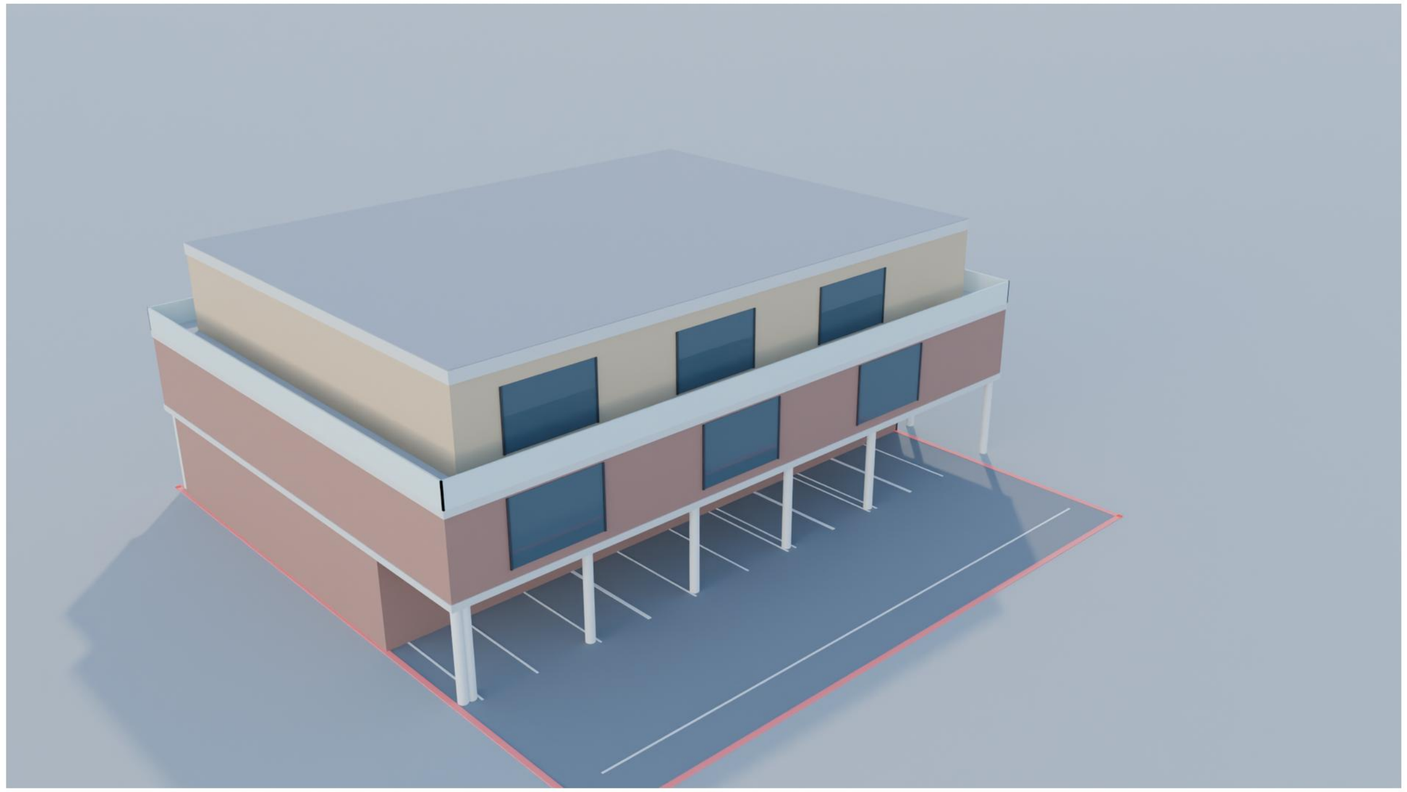

Alle Maße sind Planungsannahmen: Stellplatz 2,50 × 5,00 m, Fahrgasse 6,00 m, Säule Ø 0,40 m, Grundstück 32 × 30 m (Hypothese; die städtischen Unterlagen Seite 13/15/16 liegen nur als Beschreibung vor, nicht als Foto), Zufahrt = Annahme. Wohnfläche = 0,88 × Wohnstreifen, schematisch. Nichts ist genehmigt, bemessen oder abgestimmt.

Wie F1, das 2. OG springt rundum 1,50 m zurück (umlaufende Dachterrasse).

Kennzahl	Wert (vorläufig)
Höhe	12,00 m Attika (EG 4,30 · 1. OG 3,60 · 2. OG 3,60 · Dach/Attika 0,50), 3 Geschosse – Höhenbezug offen
Grundfläche EG / 1. OG / 2. OG	540 / 756 / 598 m²
Außenmaße EG / 1. OG / 2. OG	18.0 × 30.0 / 24.0 × 31.5 / 21.0 × 28.5 m
Wohnfläche netto (geschätzt)	942 m²
Wohnungen Standardmix	14 WE (7 + 7), 51–89 m², Ø 67 m²
Gewerbe	EG 540 m²; Gastraum ca. 232 m² (≈ 99 Plätze), Terrasse/Arkade ≈ 25 Plätze, Büro 56 m²
Säulen	18 Säulen Ø 0,40 m; Paare 5,4 m (zwei Stellplätze + Säule)
Stellplätze gezeichnet	13: 8 voll nutzbar, 5 eingeschränkt, 0 Konflikt
Stellplätze erforderlich (§ 47 NBauO)	9,7–14,3, Mittel 11,6 (nur Gastro + Büro; Wohnen 0)
Stellplätze optional (Komfort/Markt)	Wohnen 0,5–1,5 je WE = 7–21; Komfortziel gesamt ≈ 26
Überstand über Grundstück H1	1,50 m


F2: Lageplan mit Gebäude, Säulen, Zufahrt und Stellplätzen

F2 – EG 18×30 m, Staffel 1,50 m · grün = Stellplatz funktioniert, orange = eingeschränkt, rot = Konflikt, rosa = nur rechnerisch verbleibende Fläche

VARIANTE F · NICHT FESTGELEGT

Lageplan F2 – Gebäude, Säulen, Zufahrt, Stellplätze

Grundstück H1 32 × 30 m HYPOTHETISCH (Zuschnitt/Baugrenzen nicht belegt) · Stellplatz 2,50 × 5,00 m, Fahrgasse 6,00 m = Planungsannahmen · Zufahrt = Annahme

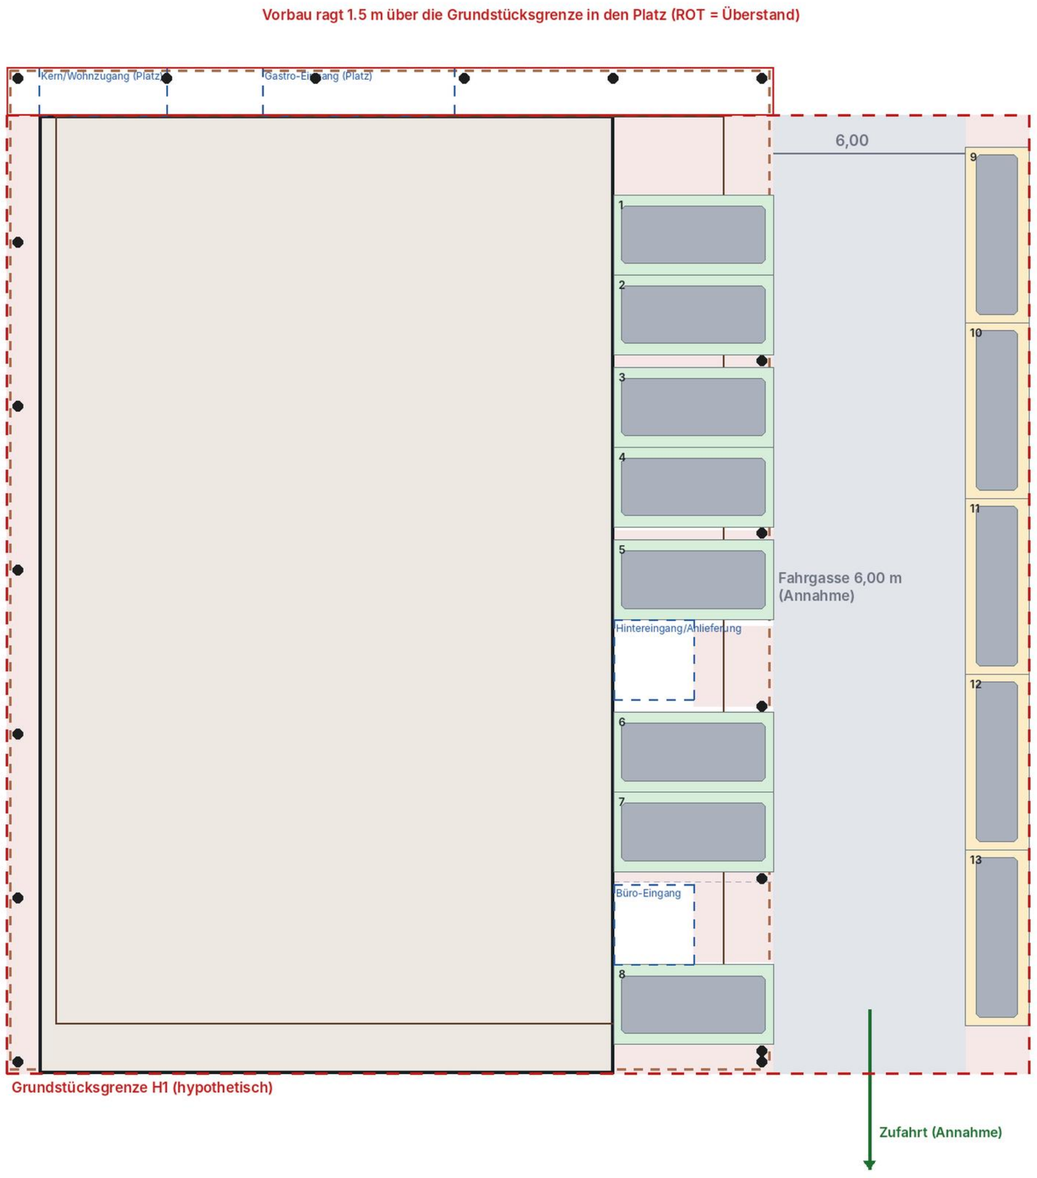

Stellplätze gezeichnet: 13
funktionieren voll: 8
eingeschränkt: 5
Konflikt: 0
Fläche (960 m²): EG 540 · Stellpl. 155 · Fahrgasse 180 · Zugänge 12
nur rechnerisch (nicht nutzbar): 72 m²
Überstand über H1: 1.50 m
OG im 3-m-/6-m-Randstreifen: 252 / 432 m²

Stellplatzprüfung	
Gezeichnet	13
funktionieren voll	8
eingeschränkt	5
Konflikt	0
Min. Nutzbreite 90°	2.50 m
Fahrgasse	6.0 m (frei)
Flächenbilanz 960 m²	
Erdgeschoss	540,0 m²
Stellplätze	155,0 m²
Fahrgasse	180,0 m²
Zugangszonen	12,5 m²
nur rechnerisch	72,5 m²

- Fahrgasse ist Sackgasse zum Platz hin: Wenden im Gassenende (Dreipunktwende) nötig – Schleppkurve prüfen
- Geometrische Prüfung ohne Schleppkurven; 90°-Stellplätze 2,50 × 5,00 m und Fahrgasse 6,00 m sind Planungsannahmen
- Zufahrt (Lage der Straße) ist Annahme
- Feuerwehrzufahrt/Aufstellflächen unter dem Vorbau nicht nachgewiesen (Prüfbedarf)

Stellplatz funktioniert · eingeschränkt · Konflikt · Fahrgasse · nur rechnerisch verbleibend

braun gestrichelt: 1./2. OG über dem EG (Vorbau) · blau gestrichelt: Eingangszonen


F2: Grundrisse EG, 1. OG, 2. OG

F2 – EG 18×30 m, Staffel 1,50 m · schematisch

VARIANTE F · NICHT FESTGELEGT

Erdgeschoss

F2: Erdgeschoss (schematisch)
Grundriss schematisch · Wohnungsaufteilung = Streifenmodell (Mittelgang 2,0 m), netto = 0,88 × brutto · Säulen Ø 0,40 m · Grundstück H1 hypothetisch

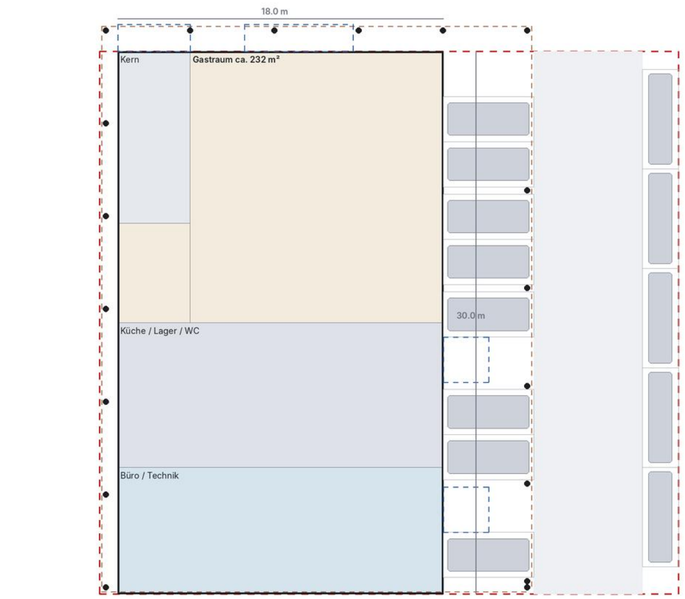


Fläche Geschoss 540 m²

Wohnung (schematisch) Kern Gastronomie Terrasse/Dach schraffiert

1. Obergeschoss

F2: 1. Obergeschoss (schematisch)
Grundriss schematisch · Wohnungsaufteilung = Streifenmodell (Mittelgang 2,0 m), netto = 0,88 × brutto · Säulen Ø 0,40 m · Grundstück H1 hypothetisch

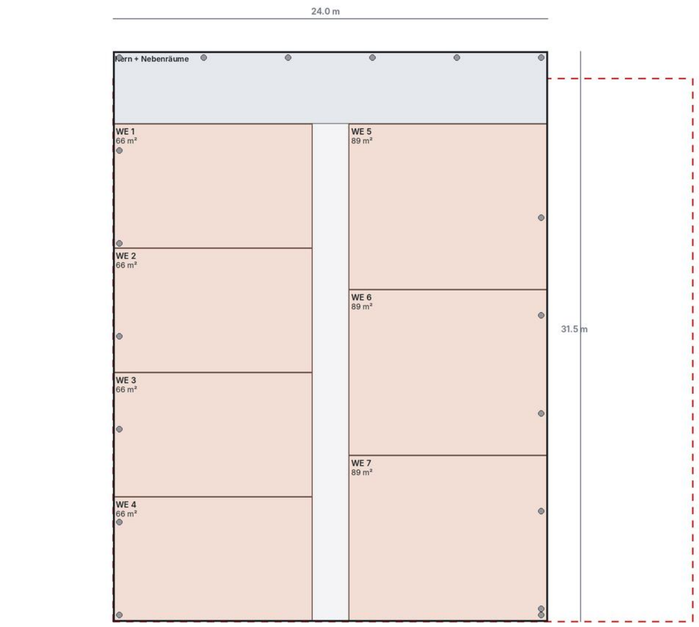


Fläche Geschoss 756 m²

Wohnung (schematisch) Kern Gastronomie Terrasse/Dach schraffiert

2. Obergeschoss

F2: 2. Obergeschoss (Staffel) (schematisch)
Grundriss schematisch · Wohnungsaufteilung = Streifenmodell (Mittelgang 2,0 m), netto = 0,88 × brutto · Säulen Ø 0,40 m · Grundstück H1 hypothetisch

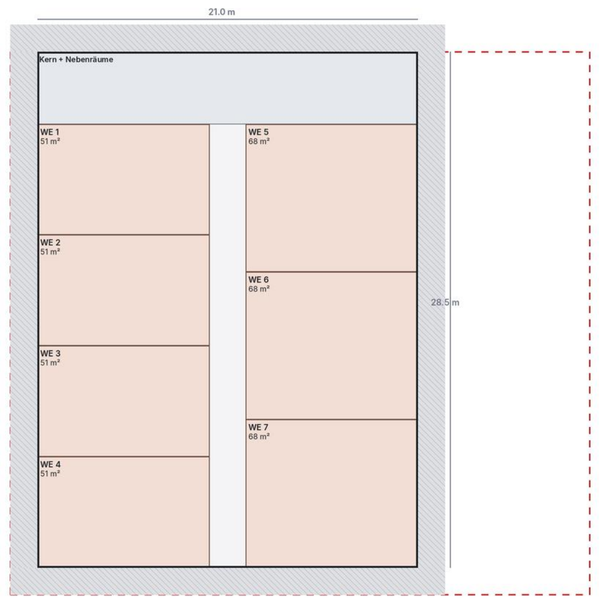

Fläche Geschoss 598 m²

Wohnung (schematisch) Kern Gastronomie Terrasse/Dach schraffiert

F2: vier Fassaden


F2 – EG 18×30 m, Staffel 1,50 m · orthogonale Ansichten aus dem 3D-Modell

VARIANTE F · NICHT FESTGELEGT


Vorderfassade (Platzseite)




Rückfassade

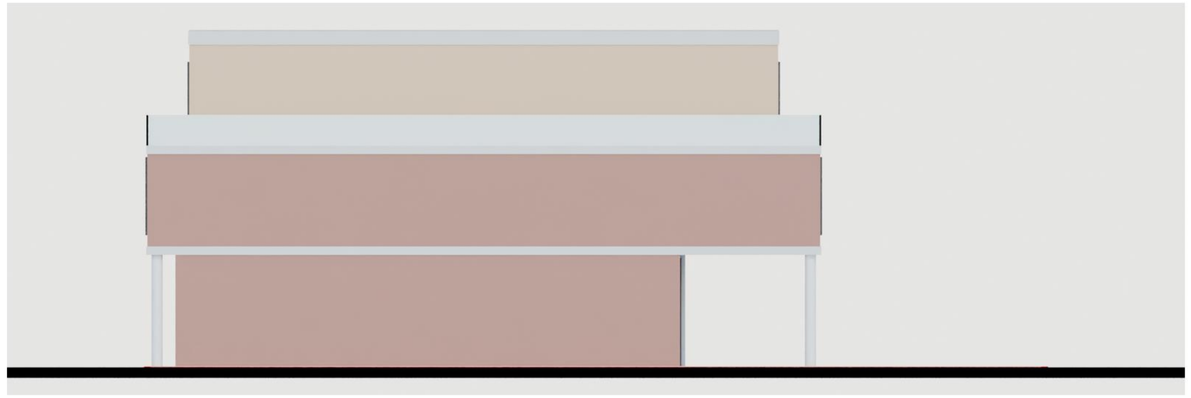

Seitenfassade West

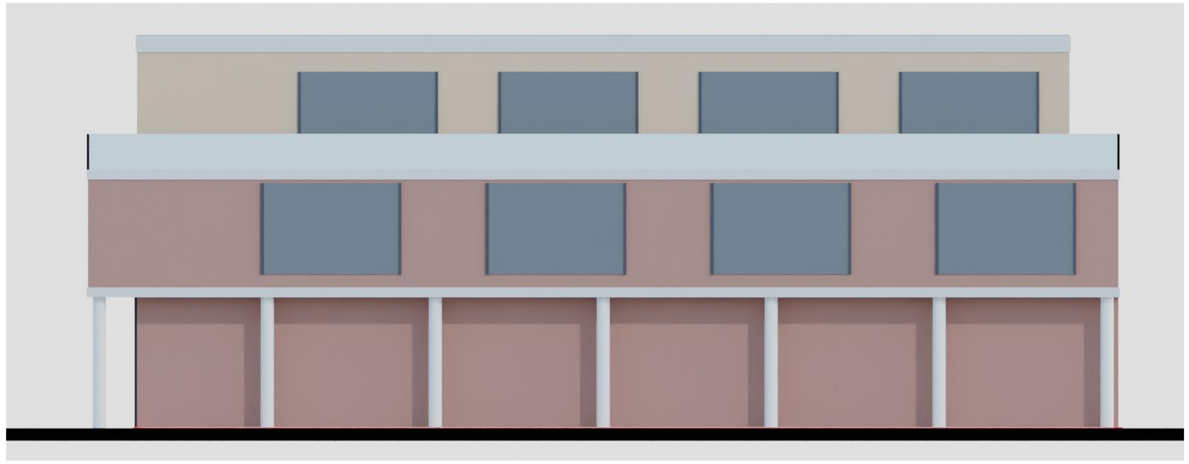

Seitenfassade Ost

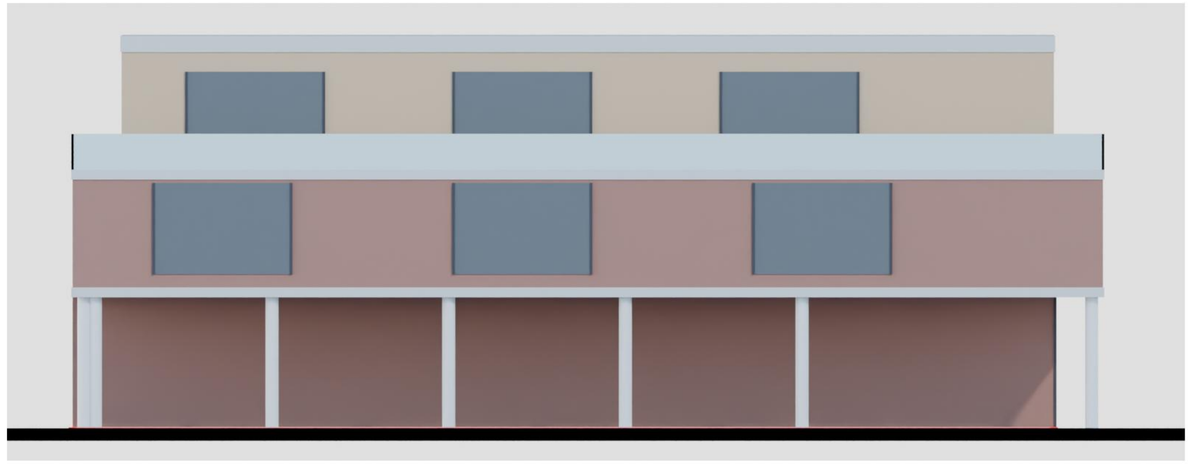

F2: Gebäudeschnitt mit Geschosshöhen und 3D-Ansichten

F2 – EG 18×30 m, Staffel 1,50 m


VARIANTE F · NICHT FESTGELEGT


F2: Gebäudeschnitt mit Geschosshöhen (schematisch)

Westseite links, Ostseite rechts · Schnitt bei y = 15.0 m · Höhenbezug ±0,00 = OK Fertigfußboden EG (Planbezug Blatt 14) – Bezugspunkt der Stadt für die 12,00 m ist NICHT belegt



Geschosshöhen: EG 4,30 m · 1. OG 3,60 m · 2. OG 3,60 m · Dach/Attika 0,50 m = 12,00 m. Reserve 0,00 m. Die 12,00 m gelten erst als eingehalten, wenn der baurechtliche Höhenbezug geklärt ist.
Säulen im Schnittbereich: 2 · Säulen insgesamt: 18 · Vorbau-Unterkante +4,00 m (Decke 0,30 m)

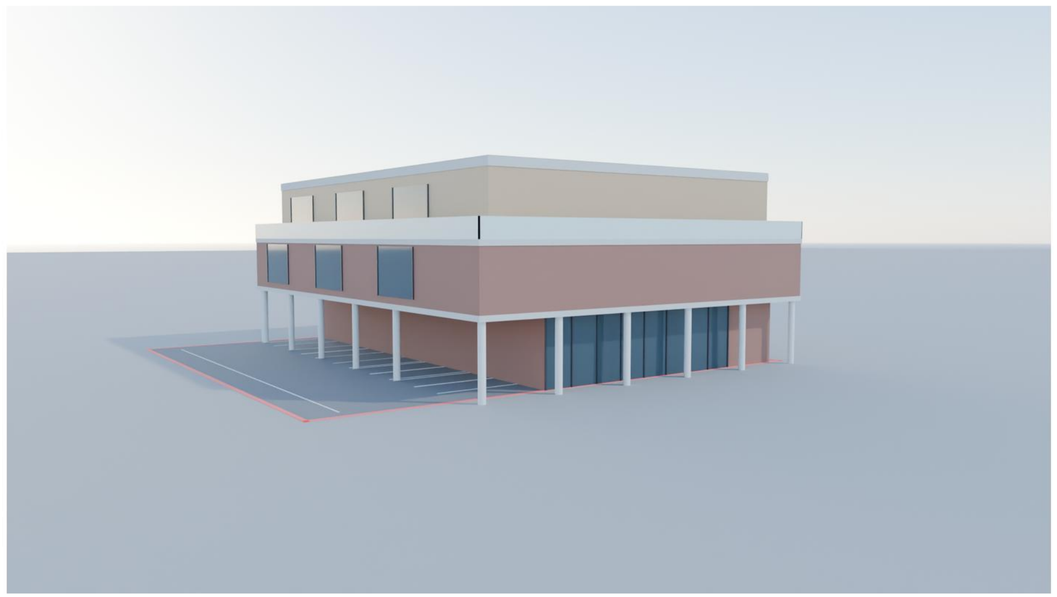


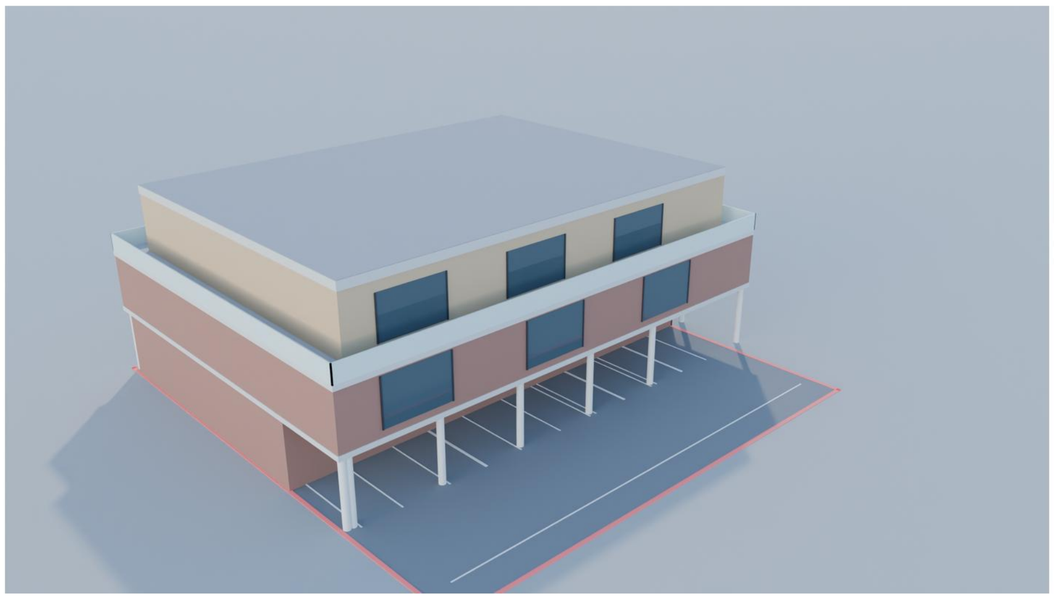

F3 – EG 18×30 m, Staffel 3,00 m

Entwurfsstudie Baufeld 3 · Konzeptvariante, keine Genehmigungsplanung

VARIANTE F · NICHT FESTGELEGT

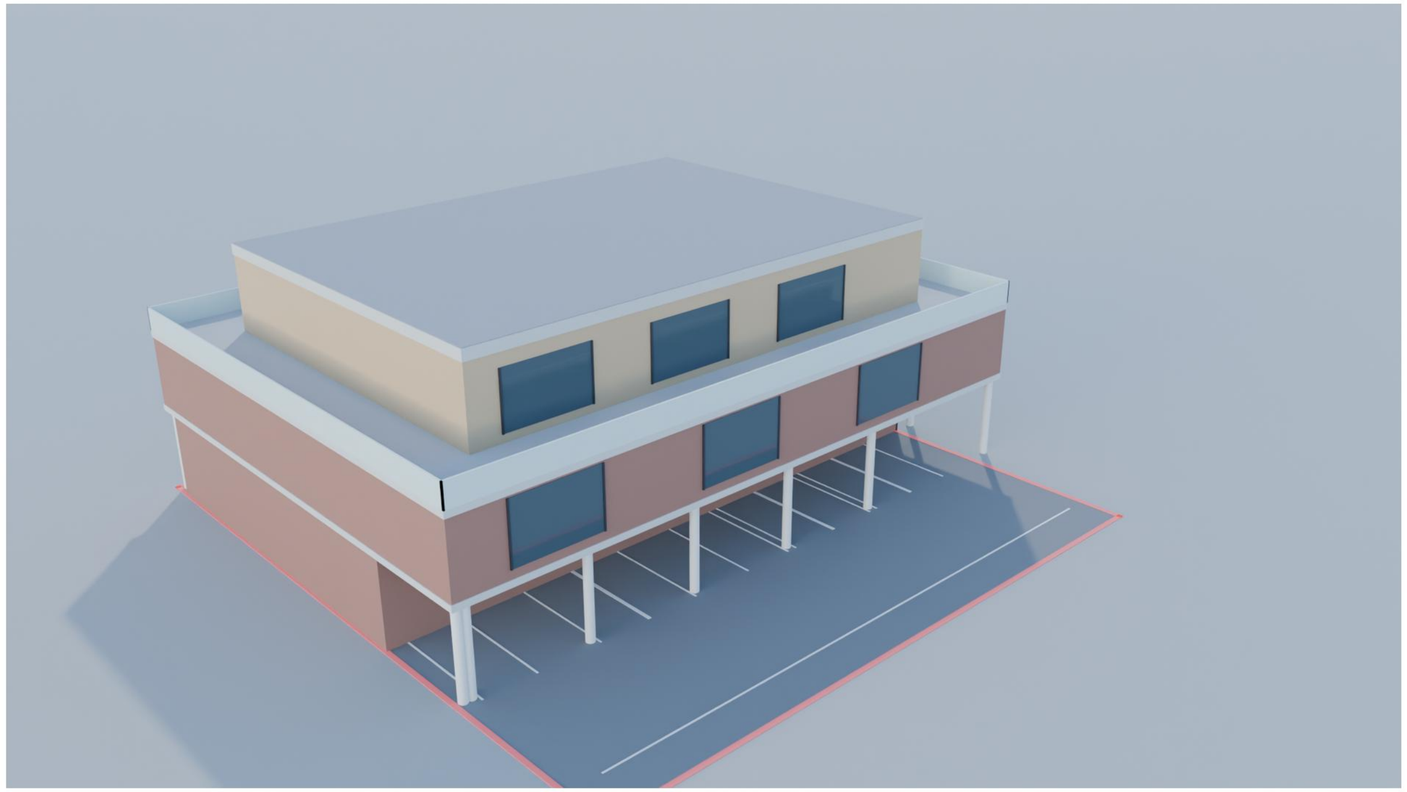

Alle Maße sind Planungsannahmen: Stellplatz 2,50 × 5,00 m, Fahrgasse 6,00 m, Säule Ø 0,40 m, Grundstück 32 × 30 m (Hypothese; die städtischen Unterlagen Seite 13/15/16 liegen nur als Beschreibung vor, nicht als Foto), Zufahrt = Annahme. Wohnfläche = 0,88 × Wohnstreifen, schematisch. Nichts ist genehmigt, bemessen oder abgestimmt.

Wie F1, das 2. OG springt rundum 3,00 m zurück (breite Dachterrasse, kleineres 2. OG).

Kennzahl	Wert (vorläufig)
Höhe	12,00 m Attika (EG 4,30 · 1. OG 3,60 · 2. OG 3,60 · Dach/Attika 0,50), 3 Geschosse – Höhenbezug offen
Grundfläche EG / 1. OG / 2. OG	540 / 756 / 459 m²
Außenmaße EG / 1. OG / 2. OG	18.0 × 30.0 / 24.0 × 31.5 / 18.0 × 25.5 m
Wohnfläche netto (geschätzt)	835 m²
Wohnungen Standardmix	13 WE (7 + 6), 50–89 m², Ø 64 m²
Gewerbe	EG 540 m²; Gastraum ca. 232 m² (≈ 99 Plätze), Terrasse/Arkade ≈ 25 Plätze, Büro 56 m²
Säulen	18 Säulen Ø 0,40 m; Paare 5,4 m (zwei Stellplätze + Säule)
Stellplätze gezeichnet	13: 8 voll nutzbar, 5 eingeschränkt, 0 Konflikt
Stellplätze erforderlich (§ 47 NBauO)	9,7–14,3, Mittel 11,6 (nur Gastro + Büro; Wohnen 0)
Stellplätze optional (Komfort/Markt)	Wohnen 0,5–1,5 je WE = 6–20; Komfortziel gesamt ≈ 25
Überstand über Grundstück H1	1,50 m


F3: Lageplan mit Gebäude, Säulen, Zufahrt und Stellplätzen

F3 – EG 18×30 m, Staffel 3,00 m · grün = Stellplatz funktioniert, orange = eingeschränkt, rot = Konflikt, rosa = nur rechnerisch verbleibende Fläche

VARIANTE F · NICHT FESTGELEGT

Lageplan F3 – Gebäude, Säulen, Zufahrt, Stellplätze

Grundstück H1 32 × 30 m HYPOTHETISCH (Zuschnitt/Baugrenzen nicht belegt) · Stellplatz 2,50 × 5,00 m, Fahrgasse 6,00 m = Planungsannahmen · Zufahrt = Annahme

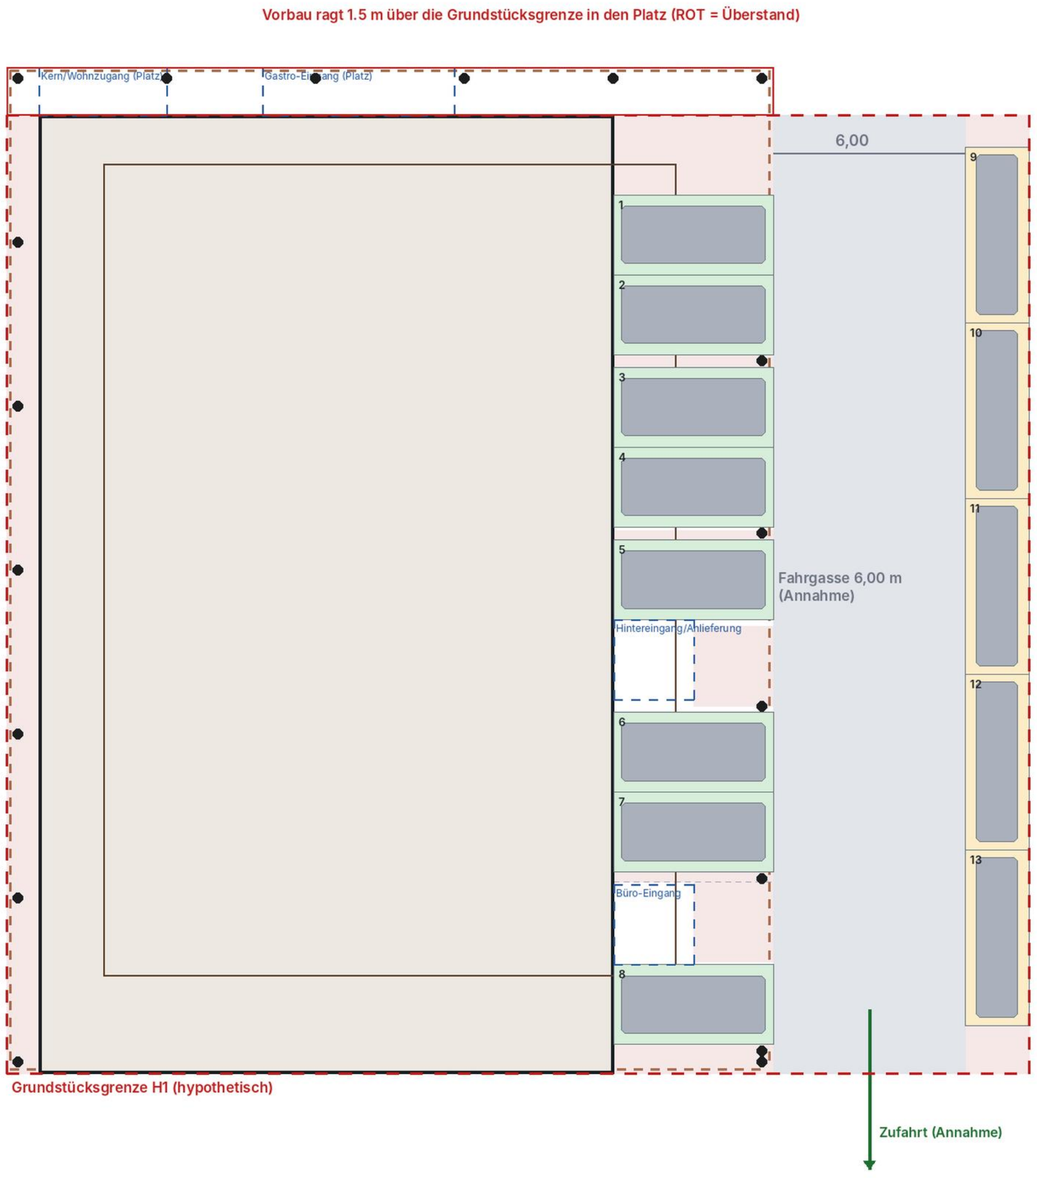

Stellplätze gezeichnet: 13
funktionieren voll: 8
eingeschränkt: 5
Konflikt: 0
Fläche (960 m²): EG 540 · Stellpl. 155 · Fahrgasse 180 · Zugänge 12
nur rechnerisch (nicht nutzbar): 72 m²
Überstand über H1: 1.50 m
OG im 3-m-/6-m-Randstreifen: 252 / 432 m²

braun gestrichelt: 1./2. OG über dem EG (Vorbau) · blau gestrichelt: Eingangszonen

Stellplatz funktioniert · eingeschränkt · Konflikt · Fahrgasse · nur rechnerisch verbleibend

Stellplatzprüfung	
Gezeichnet	13
funktionieren voll	8
eingeschränkt	5
Konflikt	0
Min. Nutzbreite 90°	2.50 m
Fahrgasse	6.0 m (frei)
Flächenbilanz 960 m²	
Erdgeschoss	540,0 m²
Stellplätze	155,0 m²
Fahrgasse	180,0 m²
Zugangszonen	12,5 m²
nur rechnerisch	72,5 m²

- Fahrgasse ist Sackgasse zum Platz hin: Wenden im Gassenende (Dreipunktwende) nötig – Schleppkurve prüfen
- Geometrische Prüfung ohne Schleppkurven; 90°-Stellplätze 2,50 × 5,00 m und Fahrgasse 6,00 m sind Planungsannahmen
- Zufahrt (Lage der Straße) ist Annahme
- Feuerwehrzufahrt/Aufstellflächen unter dem Vorbau nicht nachgewiesen (Prüfbedarf)


F3: Grundrisse EG, 1. OG, 2. OG

F3 – EG 18×30 m, Staffel 3,00 m · schematisch

VARIANTE F · NICHT FESTGELEGT

Erdgeschoss

F3: Erdgeschoss (schematisch)
Grundriss schematisch · Wohnungsaufteilung = Streifenmodell (Mittelgang 2,0 m), netto = 0,88 × brutto · Säulen Ø 0,40 m · Grundstück H1 hypothetisch

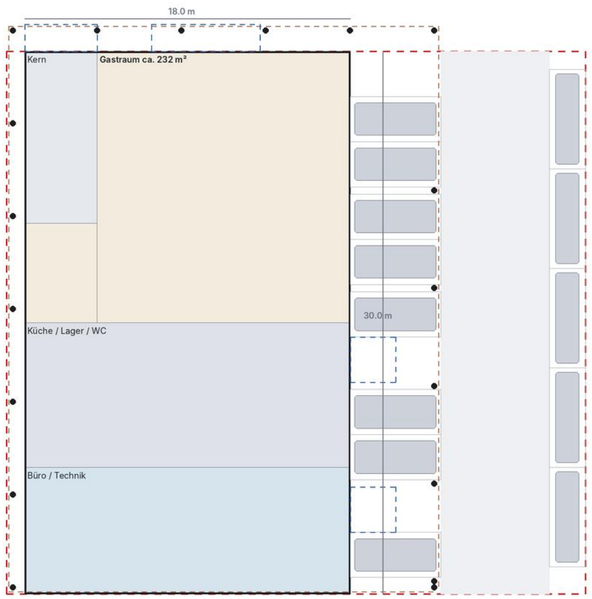


Fläche Geschoss 540 m²

Wohnung (schematisch) Kern Gastronomie Terrasse/Dach schraffiert

1. Obergeschoss

F3: 1. Obergeschoss (schematisch)
Grundriss schematisch · Wohnungsaufteilung = Streifenmodell (Mittelgang 2,0 m), netto = 0,88 × brutto · Säulen Ø 0,40 m · Grundstück H1 hypothetisch

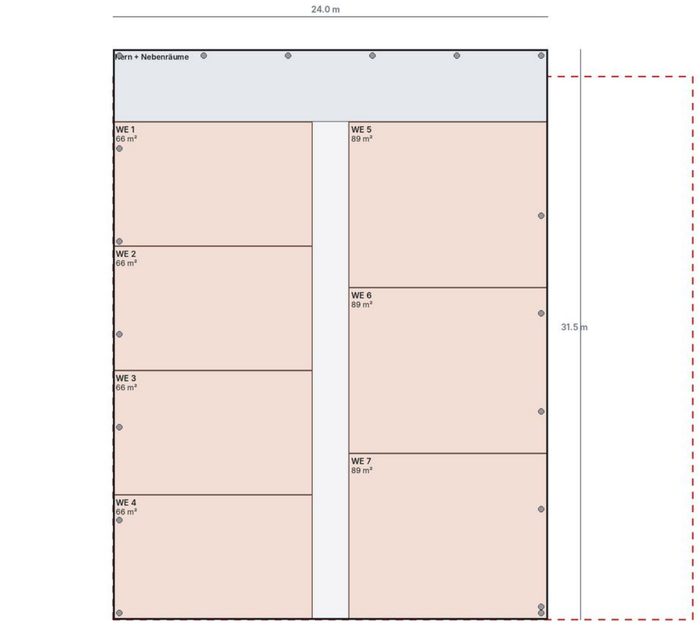


Fläche Geschoss 756 m²

Wohnung (schematisch) Kern Gastronomie Terrasse/Dach schraffiert

2. Obergeschoss

F3: 2. Obergeschoss (Staffel) (schematisch)
Grundriss schematisch · Wohnungsaufteilung = Streifenmodell (Mittelgang 2,0 m), netto = 0,88 × brutto · Säulen Ø 0,40 m · Grundstück H1 hypothetisch

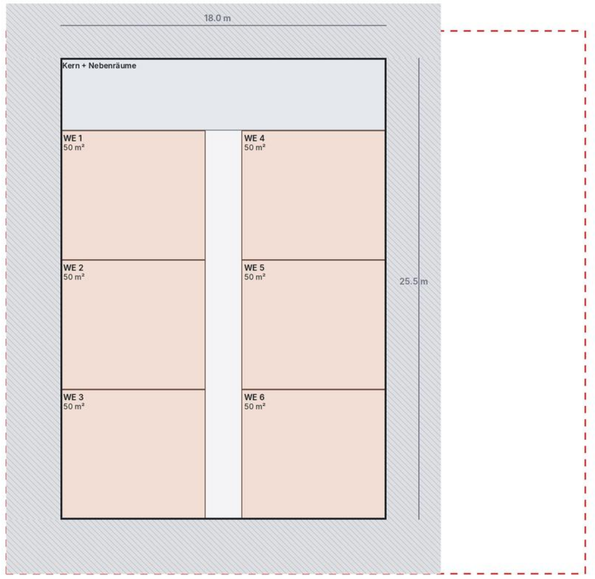

Fläche Geschoss 459 m²

Wohnung (schematisch) Kern Gastronomie Terrasse/Dach schraffiert

F3: vier Fassaden


VARIANTE F · NICHT FESTGELEGT

F3 – EG 18×30 m, Staffel 3,00 m · orthogonale Ansichten aus dem 3D-Modell


Vorderfassade (Platzseite)




Rückfassade

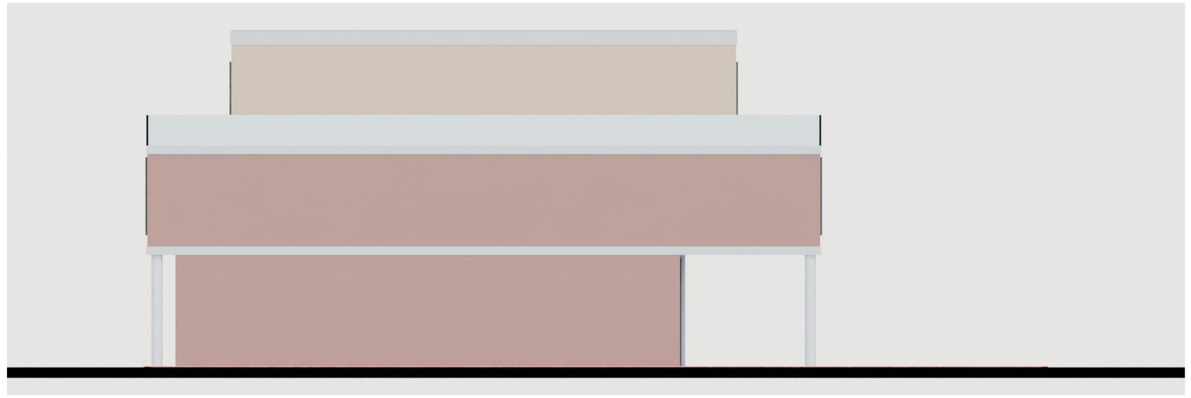

Seitenfassade West

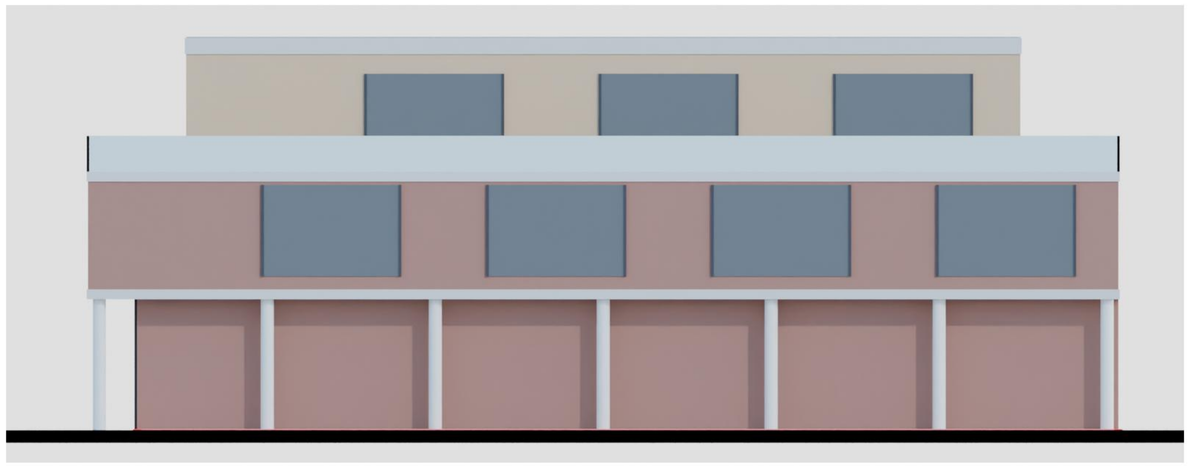

Seitenfassade Ost

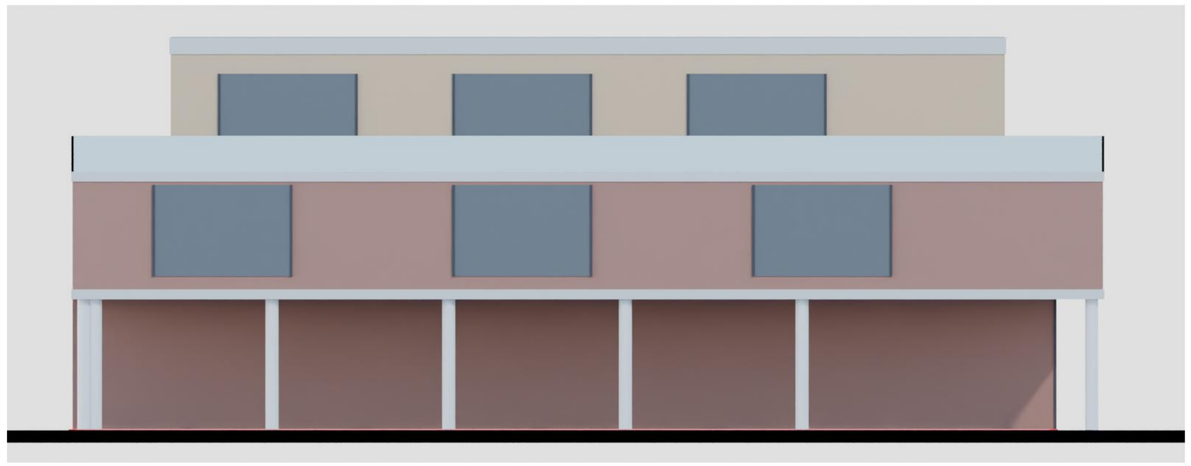


F3: Gebäudeschnitt mit Geschosshöhen und 3D-Ansichten

F3 – EG 18×30 m, Staffel 3,00 m


VARIANTE F · NICHT FESTGELEGT


F3: Gebäudeschnitt mit Geschosshöhen (schematisch)

Westseite links, Ostseite rechts · Schnitt bei y = 15.0 m · Höhenbezug ±0,00 = OK Fertigfußboden EG (Planbezug Blatt 14) – Bezugspunkt der Stadt für die 12,00 m ist NICHT belegt

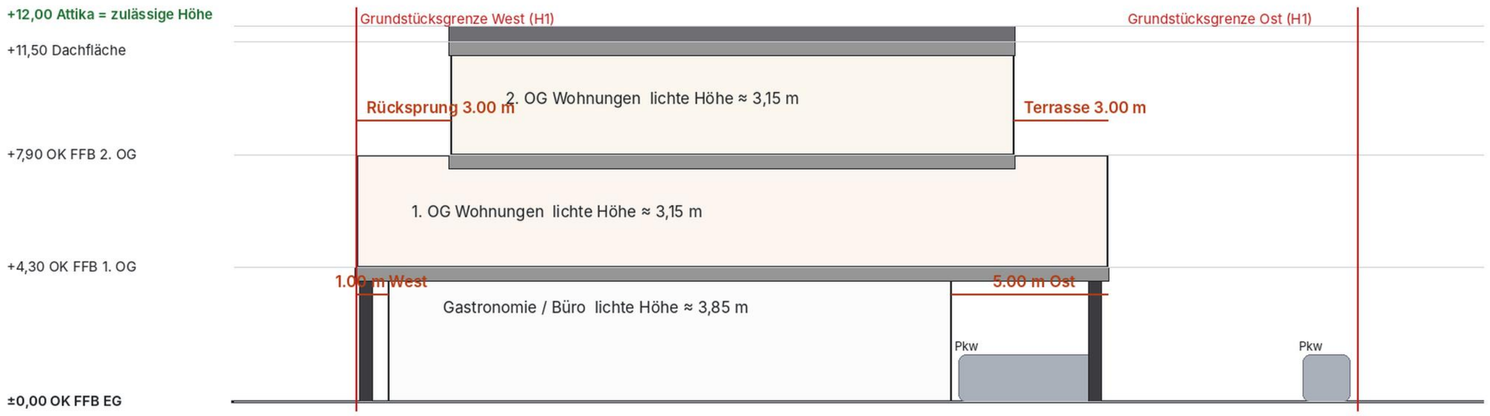

Geschosshöhen: EG 4,30 m · 1. OG 3,60 m · 2. OG 3,60 m · Dach/Attika 0,50 m = 12,00 m. Reserve 0,00 m. Die 12,00 m gelten erst als eingehalten, wenn der baurechtliche Höhenbezug geklärt ist.
Säulen im Schnittbereich: 2 · Säulen insgesamt: 18 · Vorbau-Unterkante +4,00 m (Decke 0,30 m)

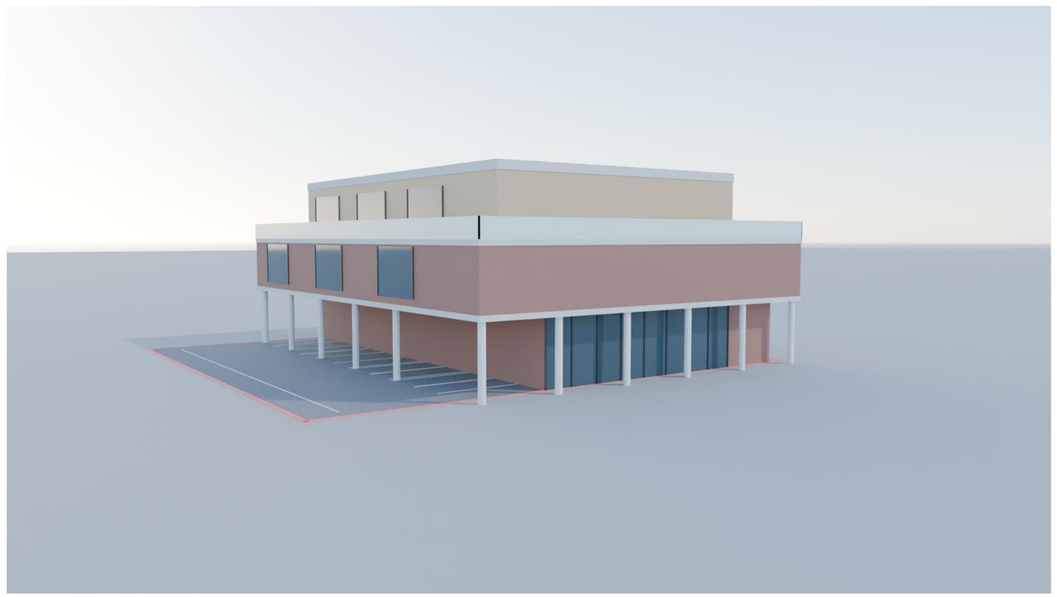


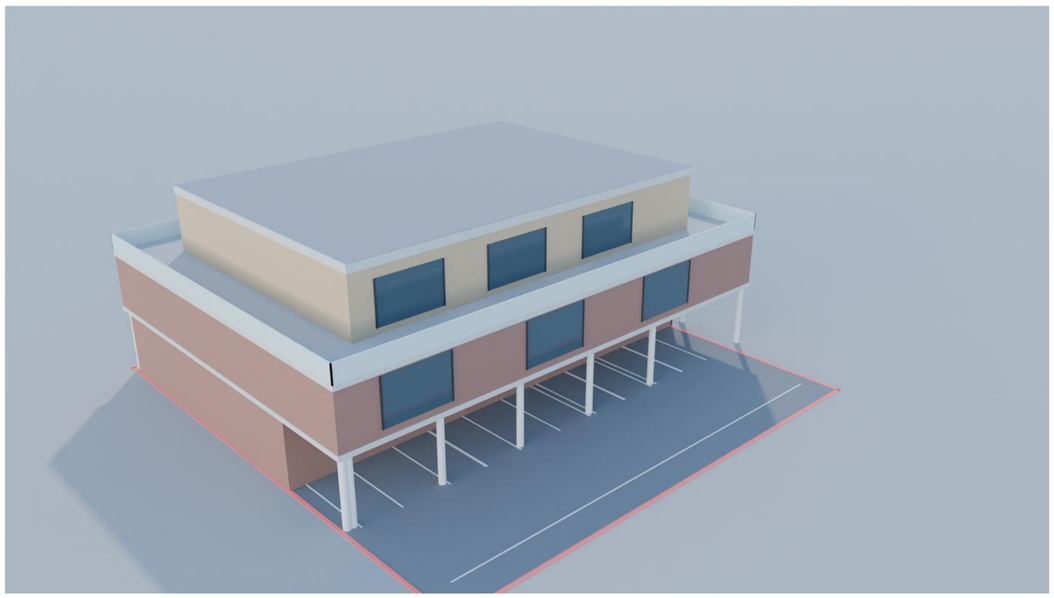

F4 – EG 30×18 m (gedreht), Staffel 1,50 m

Entwurfsstudie Baufeld 3 · Konzeptvariante, keine Genehmigungsplanung

VARIANTE F · NICHT FESTGELEGT

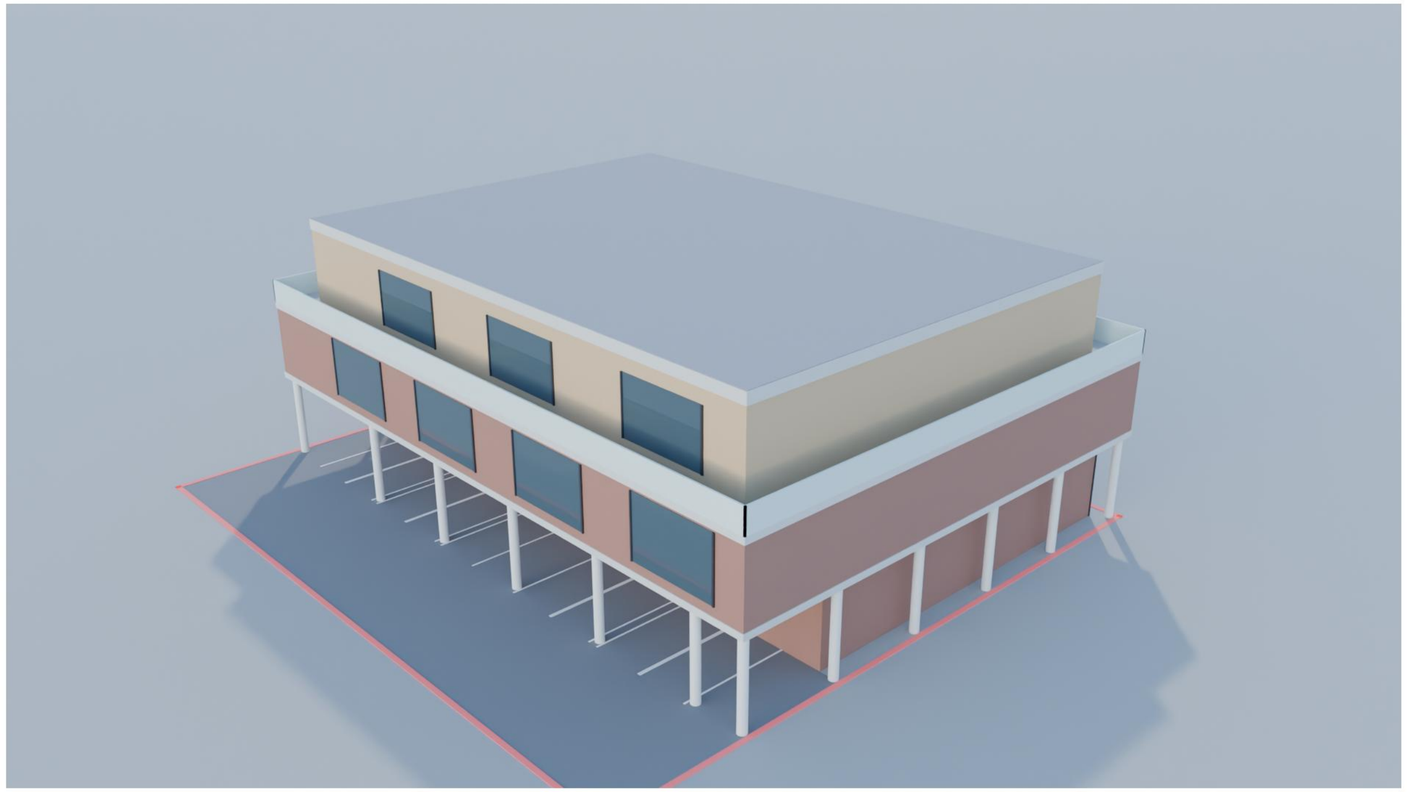

Gedrehte Lesart der 540 m²: 30 m Platzseite × 18 m Tiefe, Vorbau rundum (vorn 1,0 / seitlich 1,0 / hinten 5,0 m über der Stellplatzreihe), Staffel 1,50 m; wie E2, aber EG 540 statt 492 m².

Kennzahl	Wert (vorläufig)
Höhe	12,00 m Attika (EG 4,30 · 1. OG 3,60 · 2. OG 3,60 · Dach/Attika 0,50), 3 Geschosse – Höhenbezug offen
Grundfläche EG / 1. OG / 2. OG	540 / 768 / 609 m²
Außenmaße EG / 1. OG / 2. OG	30.0 × 18.0 / 32.0 × 24.0 / 29.0 × 21.0 m
Wohnfläche netto (geschätzt)	960 m²
Wohnungen Standardmix	16 WE (9 + 7), 52–70 m², Ø 60 m²
Gewerbe	EG 540 m²; Gastraum ca. 307 m² (≈ 132 Plätze), Terrasse/Arkade ≈ 20 Plätze, Büro 56 m²
Säulen	22 Säulen Ø 0,40 m; Paare 5,4 m (zwei Stellplätze + Säule)
Stellplätze gezeichnet	9: 9 voll nutzbar, 0 eingeschränkt, 0 Konflikt
Stellplätze erforderlich (§ 47 NBauO)	12,4–18,3, Mittel 14,8 (nur Gastro + Büro; Wohnen 0)
Stellplätze optional (Komfort/Markt)	Wohnen 0,5–1,5 je WE = 8–24; Komfortziel gesamt ≈ 31
Überstand über Grundstück H1	0,00 m

Alle Maße sind Planungsannahmen: Stellplatz 2,50 × 5,00 m, Fahrgasse 6,00 m, Säule Ø 0,40 m, Grundstück 32 × 30 m (Hypothese; die städtischen Unterlagen Seite 13/15/16 liegen nur als Beschreibung vor, nicht als Foto), Zufahrt = Annahme. Wohnfläche = 0,88 × Wohnstreifen, schematisch. Nichts ist genehmigt, bemessen oder abgestimmt.


F4: Lageplan mit Gebäude, Säulen, Zufahrt und Stellplätzen

VARIANTE F · NICHT FESTGELEGT

F4 – EG 30×18 m (gedreht), Staffel 1,50 m · grün = Stellplatz funktioniert, orange = eingeschränkt, rot = Konflikt, rosa = nur rechnerisch verbleibende Fläche

Lageplan F4 – Gebäude, Säulen, Zufahrt, Stellplätze

Grundstück H1 32 × 30 m HYPOTHETISCH (Zuschnitt/Baugrenzen nicht belegt) · Stellplatz 2,50 × 5,00 m, Fahrgasse 6,00 m = Planungsannahmen · Zufahrt = Annahme

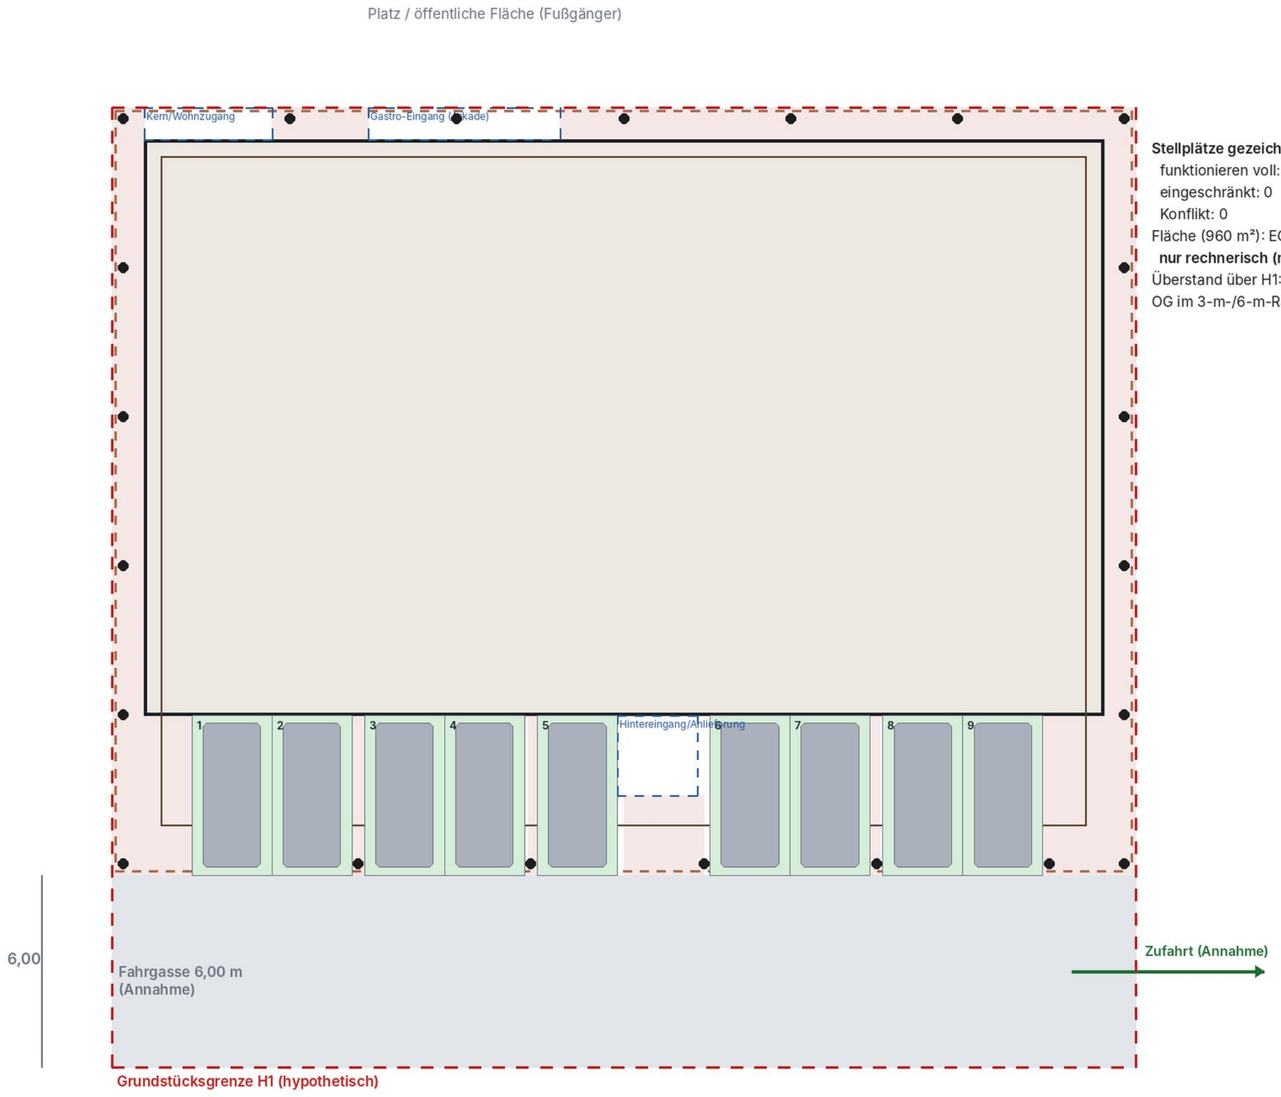

Stellplätze gezeichnet: 9
funktionieren voll: 9
eingeschränkt: 0
Konflikt: 0
Fläche (960 m²): EG 540 · Stellpl. 112 · Fahrgasse 192 · Zugänge 16
nur rechnerisch (nicht nutzbar): 99 m²
Überstand über H1: 0.00 m
OG im 3-m-/6-m-Randstreifen: 222 / 408 m²

Stellplatzprüfung	
Gezeichnet	9
funktionieren voll	9
eingeschränkt	0
Konflikt	0
Min. Nutzbreite 90°	2.50 m
Fahrgasse	6.0 m (frei)
Flächenbilanz 960 m²	
Erdgeschoss	540,0 m²
Stellplätze	112,5 m²
Fahrgasse	192,0 m²
Zugangszonen	16,2 m²
nur rechnerisch	99,2 m²

- Geometrische Prüfung ohne Schleppkurven; 90°-Stellplätze 2,50 × 5,00 m und Fahrgasse 6,00 m sind Planungsannahmen
- Zufahrt (Lage der Straße) ist Annahme
- Feuerwehrzufahrt/Aufstellflächen unter dem Vorbau nicht nachgewiesen (Prüfbedarf)

Stellplatz funktioniert · eingeschränkt · Konflikt · Fahrgasse · nur rechnerisch verbleibend

braun gestrichelt: 1./2. OG über dem EG (Vorbau) · blau gestrichelt: Eingangszonen


F4: Grundrisse EG, 1. OG, 2. OG

F4 – EG 30×18 m (gedreht), Staffel 1,50 m · schematisch

VARIANTE F · NICHT FESTGELEGT

Erdgeschoss


F4: Erdgeschoss (schematisch)
Grundriss schematisch · Wohnungsaufteilung = Streifenmodell (Mittelgang 2,0 m), netto = 0,88 × brutto · Säulen Ø 0,40 m · Grundstück H1 hypothetisch

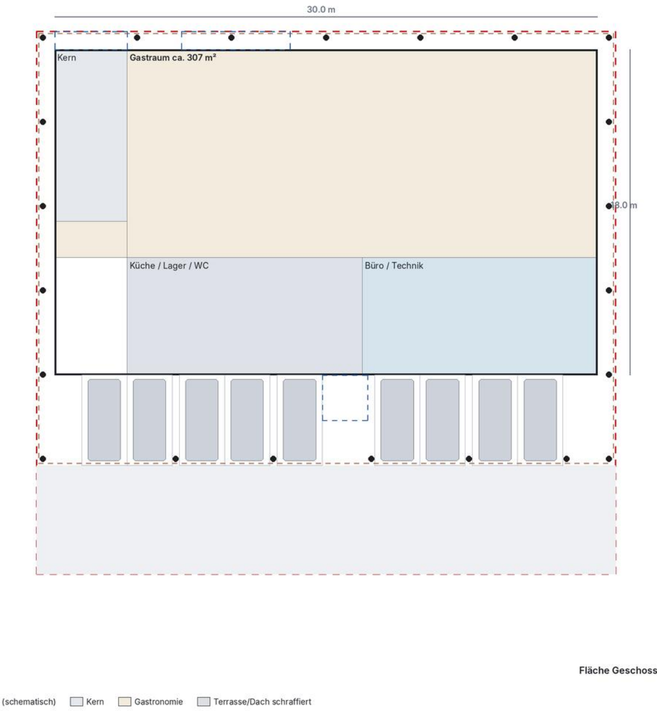

Fläche Geschoss 540 m²

1. Obergeschoss


F4: 1. Obergeschoss (schematisch)
Grundriss schematisch · Wohnungsaufteilung = Streifenmodell (Mittelgang 2,0 m), netto = 0,88 × brutto · Säulen Ø 0,40 m · Grundstück H1 hypothetisch

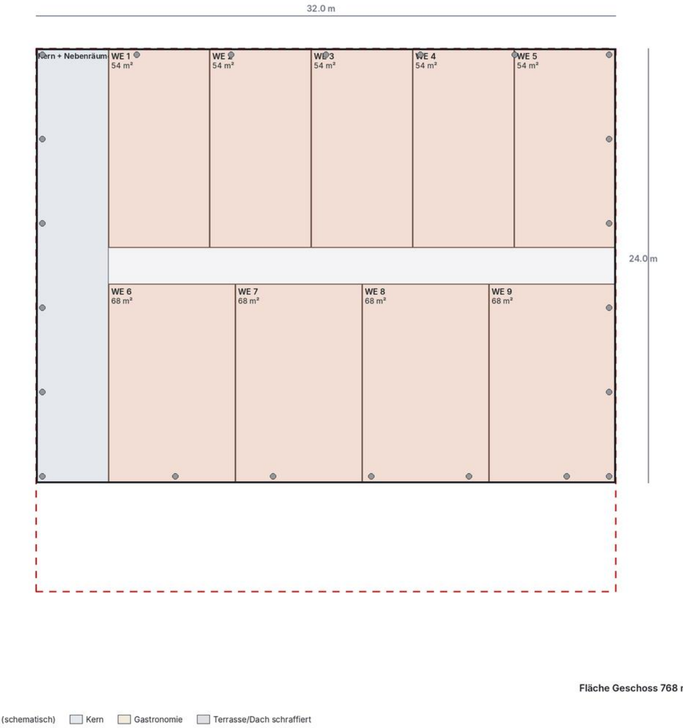

Fläche Geschoss 768 m²

2. Obergeschoss

F4: 2. Obergeschoss (Staffel) (schematisch)
Grundriss schematisch · Wohnungsaufteilung = Streifenmodell (Mittelgang 2,0 m), netto = 0,88 × brutto · Säulen Ø 0,40 m · Grundstück H1 hypothetisch

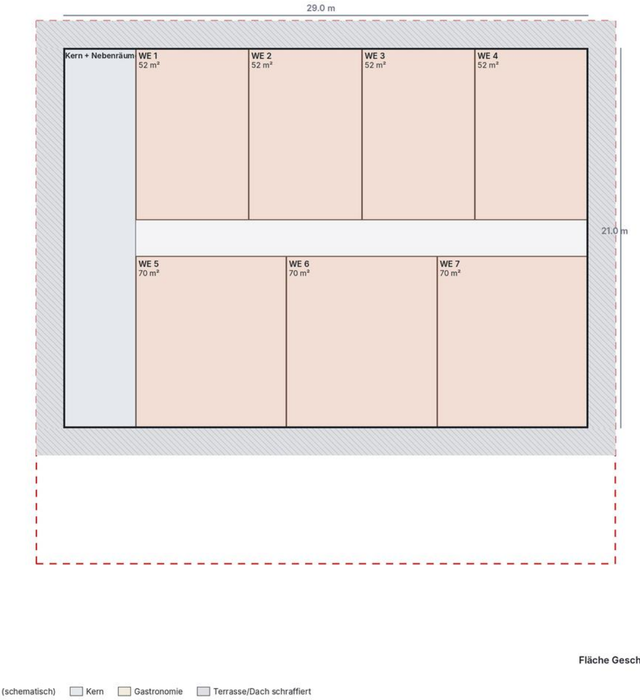

Fläche Geschoss 609 m²

Wohnung (schematisch) Kern Gastronomie Terrasse/Dach schraffiert

F4: vier Fassaden


VARIANTE F · NICHT FESTGELEGT

F4 – EG 30×18 m (gedreht), Staffel 1,50 m · orthogonale Ansichten aus dem 3D-Modell


Vorderfassade (Platzseite)



Rückfassade

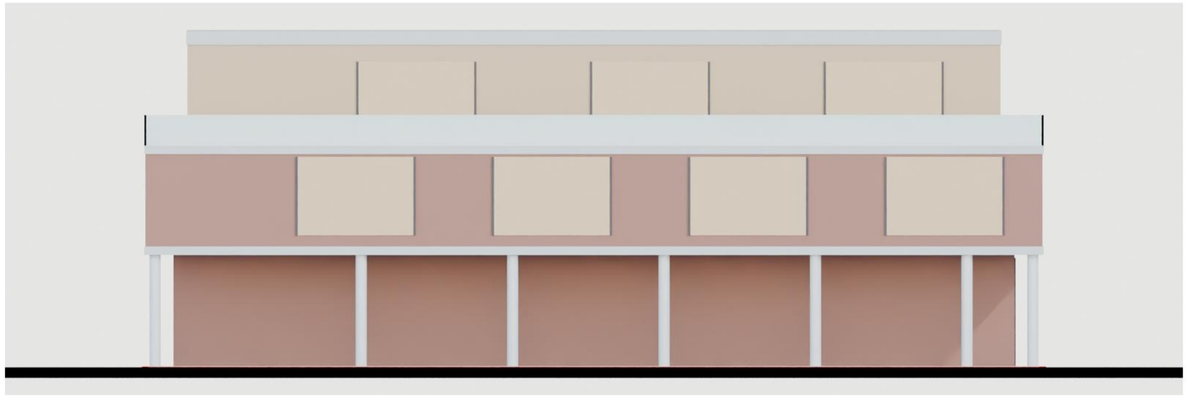

Seitenfassade West

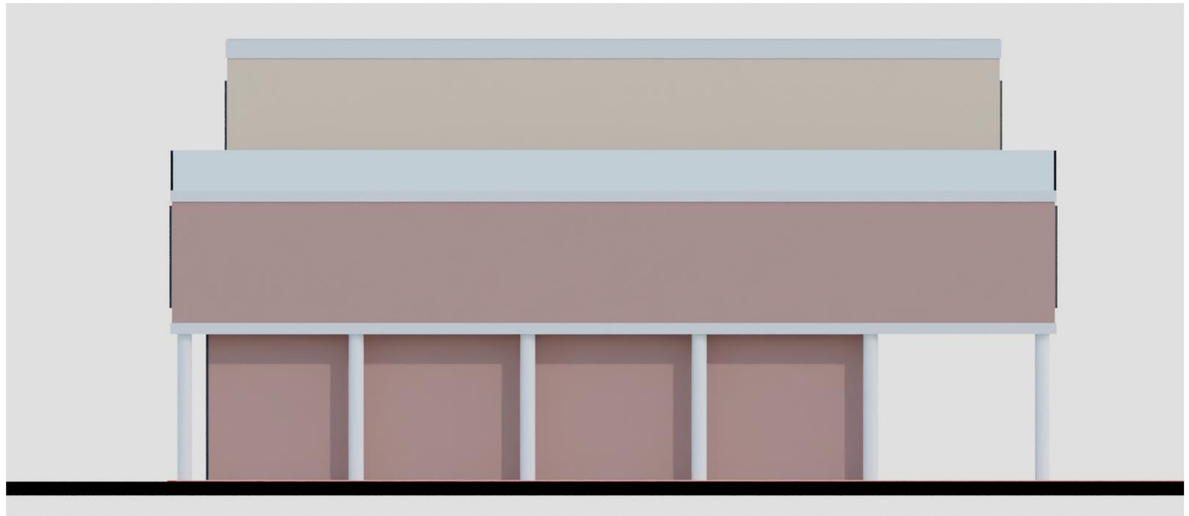

Seitenfassade Ost



F4: Gebäudeschnitt mit Geschosshöhen und 3D-Ansichten

F4 – EG 30×18 m (gedreht), Staffel 1,50 m


VARIANTE F · NICHT FESTGELEGT


F4: Gebäudeschnitt mit Geschosshöhen (schematisch)

Platzseite links, Rückseite rechts · Schnitt bei x = 16.25 m · Höhenbezug ±0,00 = OK Fertigfußboden EG (Planbezug Blatt 14) – Bezugspunkt der Stadt für die 12,00 m ist NICHT belegt



Geschosshöhen: EG 4,30 m · 1. OG 3,60 m · 2. OG 3,60 m · Dach/Attika 0,50 m = 12,00 m. Reserve 0,00 m. Die 12,00 m gelten erst als eingehalten, wenn der baurechtliche Höhenbezug geklärt ist.
Säulen im Schnittbereich: 2 · Säulen insgesamt: 22 · Vorbau-Unterkante +4,00 m (Decke 0,30 m)

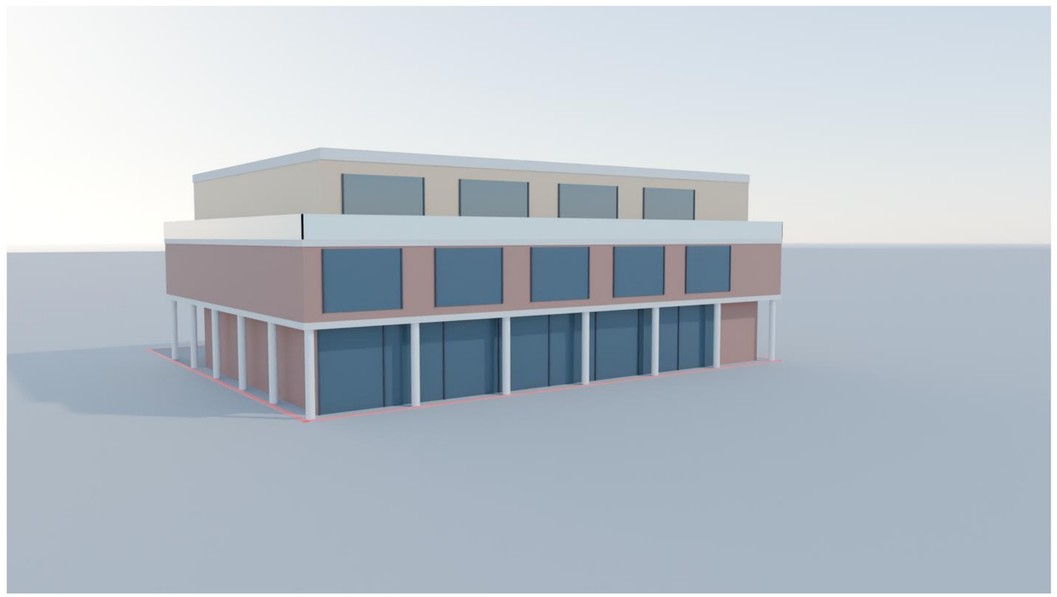

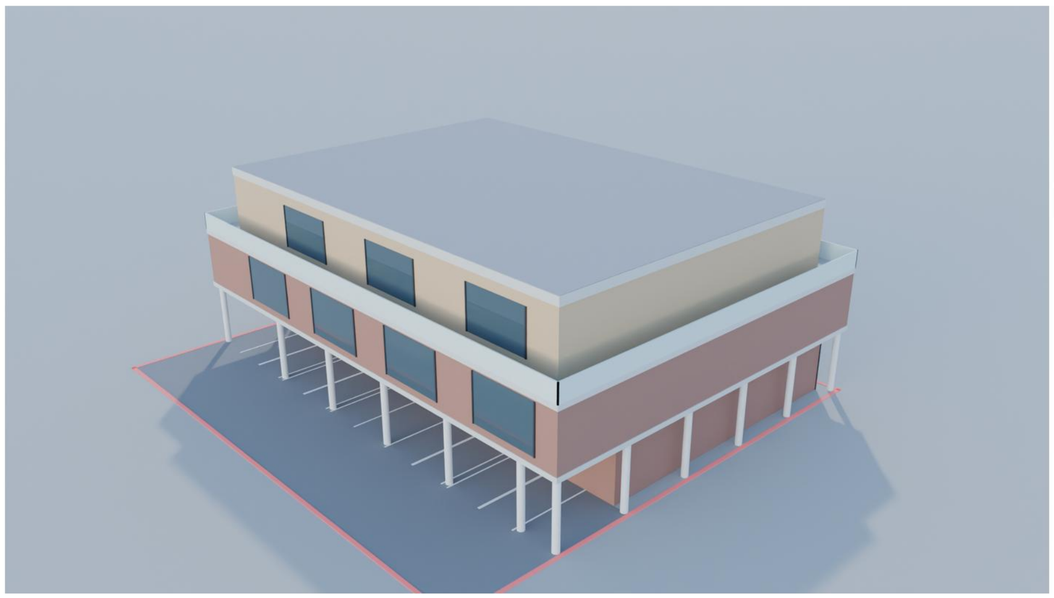

Baurechtliche Ampel (vorläufig)

VARIANTE F · NICHT FESTGELEGT

Keine Rechtsprüfung · bis zur Klärung von Grundstück, Baugrenzen und Satzungen offen

Kriterium	F1	F2	F3	F4
Gebäudehöhe 12,00 m	kritisch / offen: Attika +12,00 m über FFB. Entwurf B-Plan 123: H = 12,00 m über OK Fahrbahn, FFB max. +0,30 m → Baukörper max. +11,70 m über FFB; Fahrbahnhöhe unbekannt, Plan nur Entwurf – NICHT als eingehalten zu werten.	kritisch / offen: Attika +12,00 m über FFB. Entwurf B-Plan 123: H = 12,00 m über OK Fahrbahn, FFB max. +0,30 m → Baukörper max. +11,70 m über FFB; Fahrbahnhöhe unbekannt, Plan nur Entwurf – NICHT als eingehalten zu werten.	kritisch / offen: Attika +12,00 m über FFB. Entwurf B-Plan 123: H = 12,00 m über OK Fahrbahn, FFB max. +0,30 m → Baukörper max. +11,70 m über FFB; Fahrbahnhöhe unbekannt, Plan nur Entwurf – NICHT als eingehalten zu werten.	kritisch / offen: Attika +12,00 m über FFB. Entwurf B-Plan 123: H = 12,00 m über OK Fahrbahn, FFB max. +0,30 m → Baukörper max. +11,70 m über FFB; Fahrbahnhöhe unbekannt, Plan nur Entwurf – NICHT als eingehalten zu werten.
Geschosse / Traufe / Dach	kritisch / offen: Entwurf 1. Änderung: zwingend II Vollgeschosse, TH max. 6,50 m, Hauptdach geneigt ≥ 38° (Flachdach nur untergeordnet). Drei Geschosse mit Flachdach, Oberkante 1. OG +7,90 m und 2. OG = 100 % des 1. OG widersprechen dem Entwurf; Ursprungsplan unbekannt.	kritisch / offen: Entwurf 1. Änderung: zwingend II Vollgeschosse, TH max. 6,50 m, Hauptdach geneigt ≥ 38° (Flachdach nur untergeordnet). Drei Geschosse mit Flachdach, Oberkante 1. OG +7,90 m und 2. OG = 79 % des 1. OG widersprechen dem Entwurf; Ursprungsplan unbekannt.	kritisch / offen: Entwurf 1. Änderung: zwingend II Vollgeschosse, TH max. 6,50 m, Hauptdach geneigt ≥ 38° (Flachdach nur untergeordnet). Drei Geschosse mit Flachdach, Oberkante 1. OG +7,90 m und 2. OG = 61 % des 1. OG widersprechen dem Entwurf; Ursprungsplan unbekannt.	kritisch / offen: Entwurf 1. Änderung: zwingend II Vollgeschosse, TH max. 6,50 m, Hauptdach geneigt ≥ 38° (Flachdach nur untergeordnet). Drei Geschosse mit Flachdach, Oberkante 1. OG +7,90 m und 2. OG = 79 % des 1. OG widersprechen dem Entwurf; Ursprungsplan unbekannt.
GRZ / Überdeckung	zu prüfen: größte Geschossprojektion 756 m² = 79 % von 960 m² (GRZ 0,6 = 576 m² nur Annahme).	zu prüfen: größte Geschossprojektion 756 m² = 79 % von 960 m² (GRZ 0,6 = 576 m² nur Annahme).	zu prüfen: größte Geschossprojektion 756 m² = 79 % von 960 m² (GRZ 0,6 = 576 m² nur Annahme).	zu prüfen: größte Geschossprojektion 768 m² = 80 % von 960 m² (GRZ 0,6 = 576 m² nur Annahme).
Grenzen / Baugrenzen	kritisch / offen: Überstand 1,50 m über H1 (Platzseite); Außenkante sonst auf der Grenze.	kritisch / offen: Überstand 1,50 m über H1 (Platzseite); Außenkante sonst auf der Grenze.	kritisch / offen: Überstand 1,50 m über H1 (Platzseite); Außenkante sonst auf der Grenze.	kritisch / offen: Außenkante OG auf angenommener Grenze (0,00 m). Entwurf: Baugrenze 3,0 m zu Planstraße/Parkplatz – der Vorbau über die Baugrenze ist unzulässig; auf den aus den amtlichen Plänen abgeleiteten Baufeldern (≈ 27 × 19 m Baufenster) passt der Fußabdruck nicht (siehe Grundstücksanalyse).
Stellplätze (gesetzlich)	zu prüfen: 13 nutzbar, erforderlich 9,7–14,3 (Mittel 11,6): Spanne der Bauaufsicht entscheidet	zu prüfen: 13 nutzbar, erforderlich 9,7–14,3 (Mittel 11,6): Spanne der Bauaufsicht entscheidet	zu prüfen: 13 nutzbar, erforderlich 9,7–14,3 (Mittel 11,6): Spanne der Bauaufsicht entscheidet	kritisch / offen: 9 nutzbar < erforderlich Mittel 14,8 (12,4–18,3): Ablöse/Mitbenutzung nötig
Gewerbe im EG	zu prüfen: EG 540 m² (B3: 576 m²); Gastraum ca. 232 m².	zu prüfen: EG 540 m² (B3: 576 m²); Gastraum ca. 232 m².	zu prüfen: EG 540 m² (B3: 576 m²); Gastraum ca. 232 m².	zu prüfen: EG 540 m² (B3: 576 m²); Gastraum ca. 307 m².
Brandschutz / Feuerwehr	zu prüfen: Vorbau über Stellplätzen/Fahrgasse, Aufstellflächen und Feuerwehrzufahrt, Rettungswege – Konzept erforderlich.	zu prüfen: Vorbau über Stellplätzen/Fahrgasse, Aufstellflächen und Feuerwehrzufahrt, Rettungswege – Konzept erforderlich.	zu prüfen: Vorbau über Stellplätzen/Fahrgasse, Aufstellflächen und Feuerwehrzufahrt, Rettungswege – Konzept erforderlich.	zu prüfen: Vorbau über Stellplätzen/Fahrgasse, Aufstellflächen und Feuerwehrzufahrt, Rettungswege – Konzept erforderlich.

Offene Fragen und Prüfbedarf

VARIANTE F · NICHT FESTGELEGT

Vor jeder Weiterentwicklung zu klären

• Fotos der städtischen Unterlagen (S. 13, 15, 16) in den Projektordner; daraus Grundstückszuschnitt, Baugrenzen, GRZ, Höhenbezugspunkt, Traufhöhe, Dachform, Abstände, Festsetzungen zu Stellplätzen/Zufahrten.
• Bebauungsplan-Stand: Entwurf (S. 15) – rechtskräftige Fassung; örtliche Bauvorschrift/Stellplatzsatzung für Nicht-Wohnungen; städtebaulicher Vertrag/Kaufvertrag (Stellplätze auch für Wohnungen möglich).
• Einstufung der Gaststätte („örtliche“ oder „überörtliche Bedeutung“), Sitzplatzzahl innen/außen, Büro mit/ohne Besucherverkehr.
• Höhenbezug der 12,00 m; Vollgeschoss-Definition für das 2. OG; Traufhöhe 6,50 m.
• Überbauung des Platzes (F1–F3: 1,5 m), Grenz- und Abstandsflächen, GRZ-Anrechnung überdeckter Stellplätze.
• Zufahrt: Straße, Gefälle, Sichtdreiecke; Feuerwehrzufahrt/Aufstellflächen unter dem Vorbau; Wendemöglichkeit in der Sackgasse (F1–F3).
• Stellplatzmaße/Garagenverordnung für Stellplätze neben Säulen und Parallelparker; Schleppkurven.
• Statik: Kragarme 1,0–5,0 m, Säulenraster 5,4 m, Fundamente; Brandschutz Vorbau.

Keine Variante ist ausgewählt.