# Grundstück Baufeld 3: Quellen, Planungsrecht, Zuschnitt

GRUNDSTÜCK · TEILWEISE ABGELEITET

Auswertung der amtlichen Unterlagen der Stadt Werlte · Stand 24.10.2026

Wichtig vorab: Die ZIP-Datei mit den Fotos der Seiten 13/15/16 ist in dieser Sitzung nicht angekommen (kein Anhang, Upload-Ordner leer, nichts im Repository). Der Ordner fotos_stadt_unterlagen/ ist leer.

Stattdessen habe ich die amtlichen Planunterlagen von der Website der Samtgemeinde Werlte geladen: B-Plan Nr. 123 „Ehemalige Grundschule“, 1. Änderung (Entwurf 25.09.2026, mit Begründung, Planzeichnung, Nutzungskonzept, Schallgutachten) und B-Plan Nr. 122 „Neue Mitte“ (Entwurf, Offenlage 02.10.–02.11.2026). Sie liegen in quellen_stadt/amtliche_unterlagen_sgwerlte/.

Kernergebnisse:
• Die 12,00 m sind NUR im Entwurf der 1. Änderung festgesetzt (H = 12,00 m); Rechtskraft liegt nur für den Ursprungsplan 123 vor (14.04.2023), dessen Text nicht vorliegt.
• Bezugspunkt: Oberkante Fahrbahn der nächstgelegenen ausgebauten Erschließungsstraße in der Mitte vor dem Baukörper; EG-Fußboden max. 0,30 m darüber. Bei SH 0,30 m bleiben nur +11,70 m über FFB; die in E/F gezeichneten +12,00 m über FFB sind zu hoch bzw. nicht nachgewiesen.
• Im Entwurf gilt für den Änderungsbereich: Mischgebiet, GRZ 0,6, zwingend zwei Vollgeschosse, Traufhöhe 6,50 m, geneigtes Dach mind. 38°, Baugrenze 3,0 m zu Planstraße und Parkplatz. Das passt nicht zu dreigeschossigen Flachdachbauten mit Vorbau über die Baugrenze.
• Welches Baufeld „Baufeld 3“ ist, lässt sich ohne Seite 13 nicht sicher bestimmen. Aus dem Nutzungskonzept habe ich zwei Kandidaten abgegriffen (ca. 33 × 25 m und 35 × 27 m, Näherung ±2 m). Auf beiden passt weder B3 (EG 32 × 18 m) noch F (540 m²) in das Baufenster.

# Gesicherte Maße, Ableitungen, Annahmen

GRUNDSTÜCK · TEILWEISE ABGELEITET


Trennung nach Herkunft

| Angabe | Wert | Status | Fundstelle / Bemerkung |
|---|---|---|---|
| **Plangebiet 1. Änderung** | ca. 3.874 m² (0,39 ha) | GESICHERT | Begründung Nr. 1; Bekanntmachung 24.09.2026 |
| **Baugrenze zu Planstraße und Parkplatz** | 3,0 m | GESICHERT | Begründung Nr. 3.3 |
| **Planstraße Querschnitt** | 16,0 m | GESICHERT | Begründung Nr. 3.3; Abb. 2 (15,8 m) |
| **Parkplatz öffentlich** | 63 Einstellplätze | GESICHERT | Begründung 2.5, Schallgutachten (Nutzungskonzept) |
| **Höhen (SH 0,30 / TH 6,50 / H 12,00 m), II zwingend, GRZ 0,6, MI** | siehe Planzeichnung | GESICHERT (Entwurf) | Planzeichnung, Textliche Festsetzungen 1.2; nicht rechtskräftig |
| **Flurstücks- und Baufeldgrenzen der Baufelder** | nicht dargestellt | UNBEKANNT | Abb. 3 zeigt keine Grundstücksgrenzen, nur Nutzungen |
| **Kandidat K1: 33 × 25 m (≈ 830 m²)** | Näherung | ABGELEITET (±2 m) | aus Abb. 3, Maßstab 1:1000, Straßen-/Wegkanten |
| **Kandidat K2: 35 × 27 m (≈ 900 m²)** | Näherung | ABGELEITET (±2 m) | wie oben; Trapezform vereinfacht |
| **Fläche Baufeld 3 ≈ 960 m²** | ca. 960 m² | Projektangabe, nicht am Plan belegt | weder K1 (−12 %) noch K2 (−6 %) deckungsgleich |
| **Baufenster W/O (Abstand 3 m)** | 27 × 19 m (K1) | ANNAHME | nur N/S aus Begründung; Ost/West nicht belegt |
| **Ursprungsplan 123 (rechtskräftig seit 14.04.2023)** | – | UNBEKANNT | Text/Plan liegt nicht vor; „2–3 Geschosse“ (Seite 13) ungeprüft |
| **Lage der Platzseite / Zufahrt** | – | UNBEKANNT | Planstraße im Süden, Parkplatz im Norden der Kandidaten; Zufahrt Annahme |

# Planungsrecht: Höhe 12,00 m und ihr Bezugspunkt

GRUNDSTÜCK · TEILWEISE ABGELEITET

B-Plan Nr. 123, 1. Änderung, Entwurf (Textliche Festsetzung 1.2) · Antwort auf: verbindlich festgesetzt? von wo gemessen?

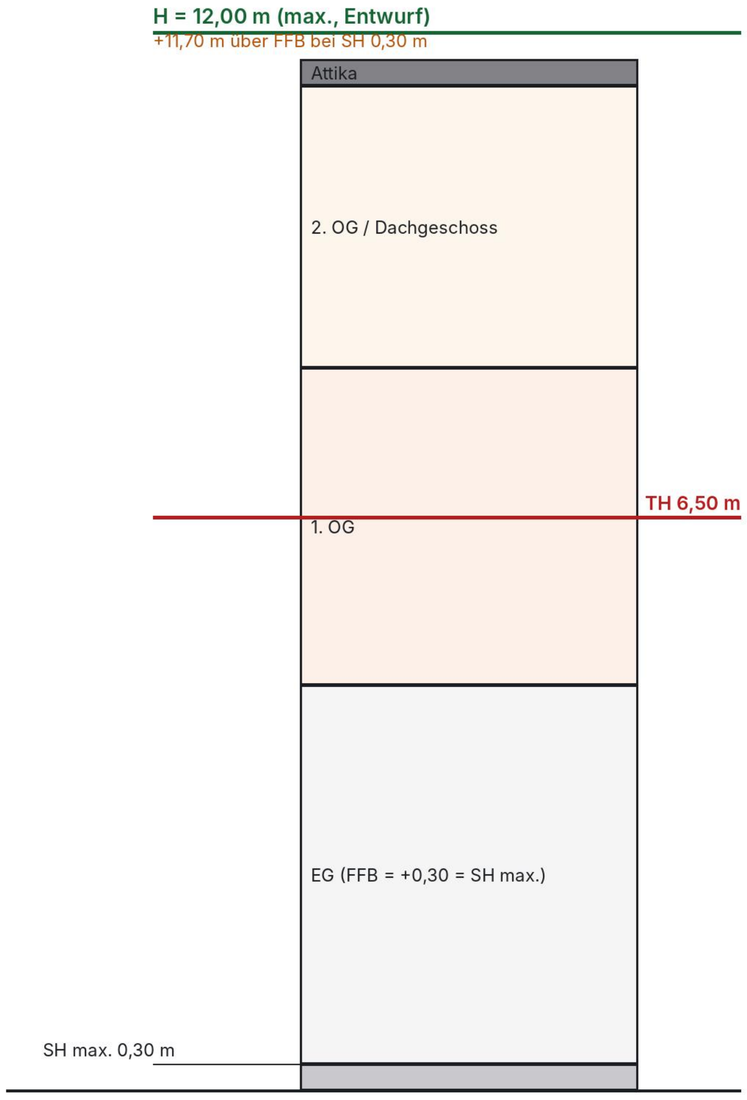




| Frage | Antwort |
|---|---|
| **Ist 12 m verbindlich festgesetzt?** | Im ENTWURF der 1. Änderung (H = 12,00 m). Satzungsbeschluss steht aus; der rechtskräftige Ursprungsplan 123 (14.04.2023) liegt nicht vor. → Nicht als verbindlich nachgewiesen. |
| **Von wo gemessen?** | Unterer Bezugspunkt: Oberkante Fahrbahn der nächstgelegenen ausgebauten Erschließungsstraße in der Mitte vor dem Baukörper (Höhe beim Bauamt erfragbar). Oberer Punkt: Oberkante Baukörper (First, Hauptgesims); untergeordnete Teile (Antennen, Schornsteine) zählen nicht. |
| **Verhältnis zu FFB EG** | FFB EG max. 0,30 m über dem Bezugspunkt (SH). Bei SH 0,30 m: Baukörper max. +11,70 m über FFB; E/F zeichnen +12,00 m über FFB → bei SH > 0 überschritten, nur bei FFB = Fahrbahnhöhe möglich. |
| **Traufhöhe** | max. 6,50 m (Schnittkante Mauerwerk/Dachhaut): Oberkante 1. OG der Entwürfe (+7,90 / +8,20 m) liegt darüber. |
| **Vollgeschosse / Dach** | II zwingend; Hauptdach geneigt ≥ 38° (Flachdach nur Verbindungsbauten, ≥ 1,0 m unter First, bzw. untergeordnete Teile ≤ 70 m²). Dreigeschossige Flachdachbauten (B3, B, C, E, F) passen nicht zum Entwurf. |
| **Fazit** | Die 12,00 m bleiben Planungsziel, gelten aber erst als eingehalten, wenn (1) Ursprungsplan/Satzung für Baufeld 3 vorliegt, (2) Fahrbahnhöhe vor dem Baukörper bekannt ist, (3) Traufe/Dachform/Vollgeschosse geklärt sind. |

# Planauszüge der Stadt (Entwurf 1. Änderung)

GRUNDSTÜCK · TEILWEISE ABGELEITET

links Entwurfszeichnung (Abb. 2, Stand 25.08.2026), rechts Nutzungskonzept (Abb. 3, Stand 14.08.2026) · Quelle: Schallgutachten Bericht 476-26-a-hi, Büro Gieselmann und Müller

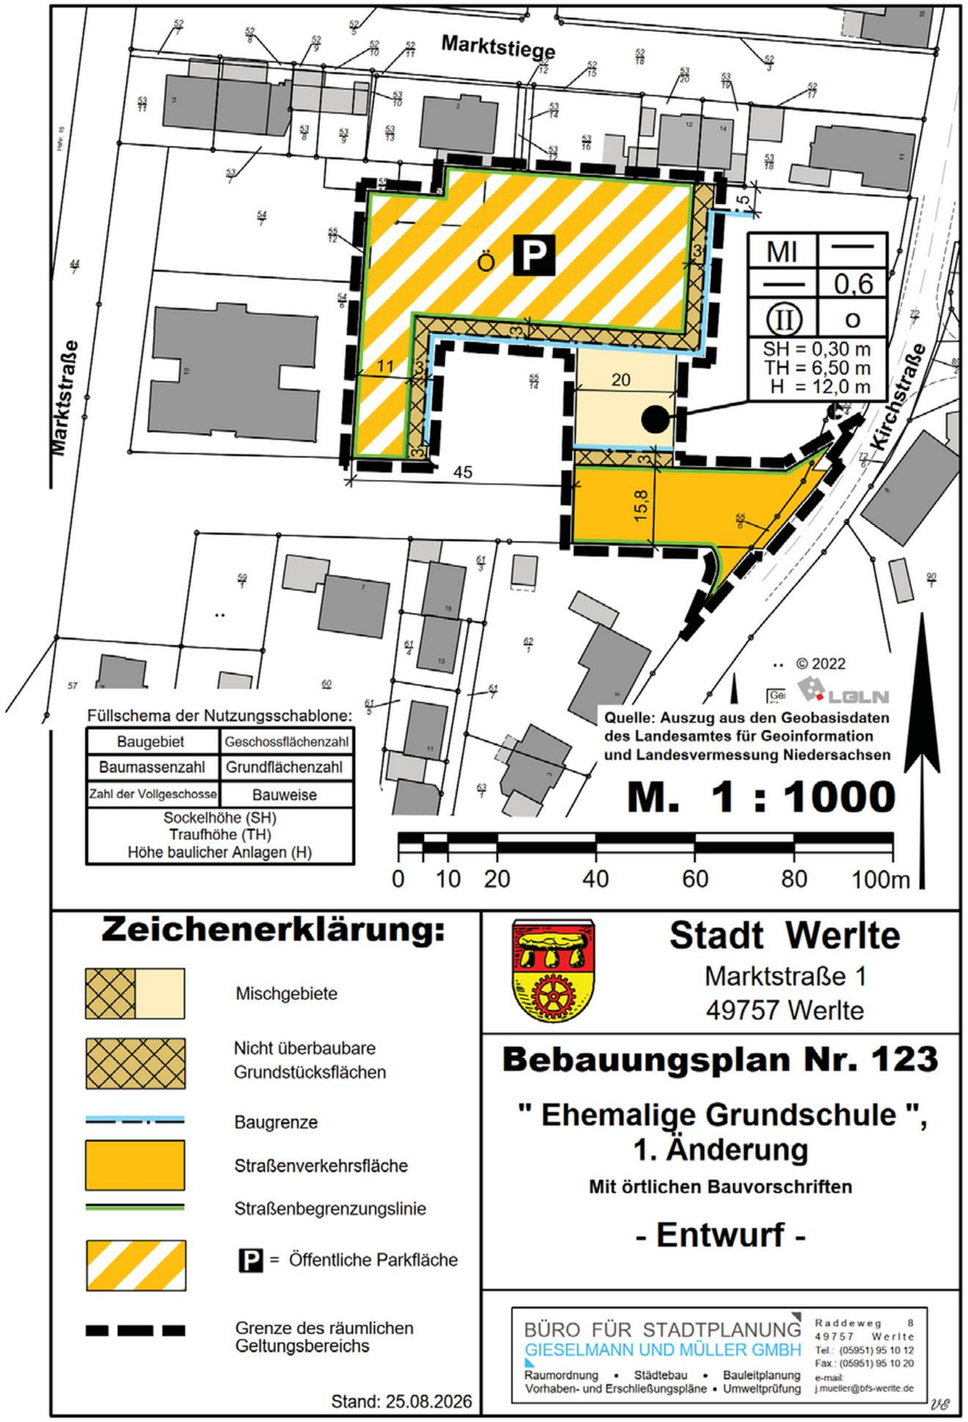

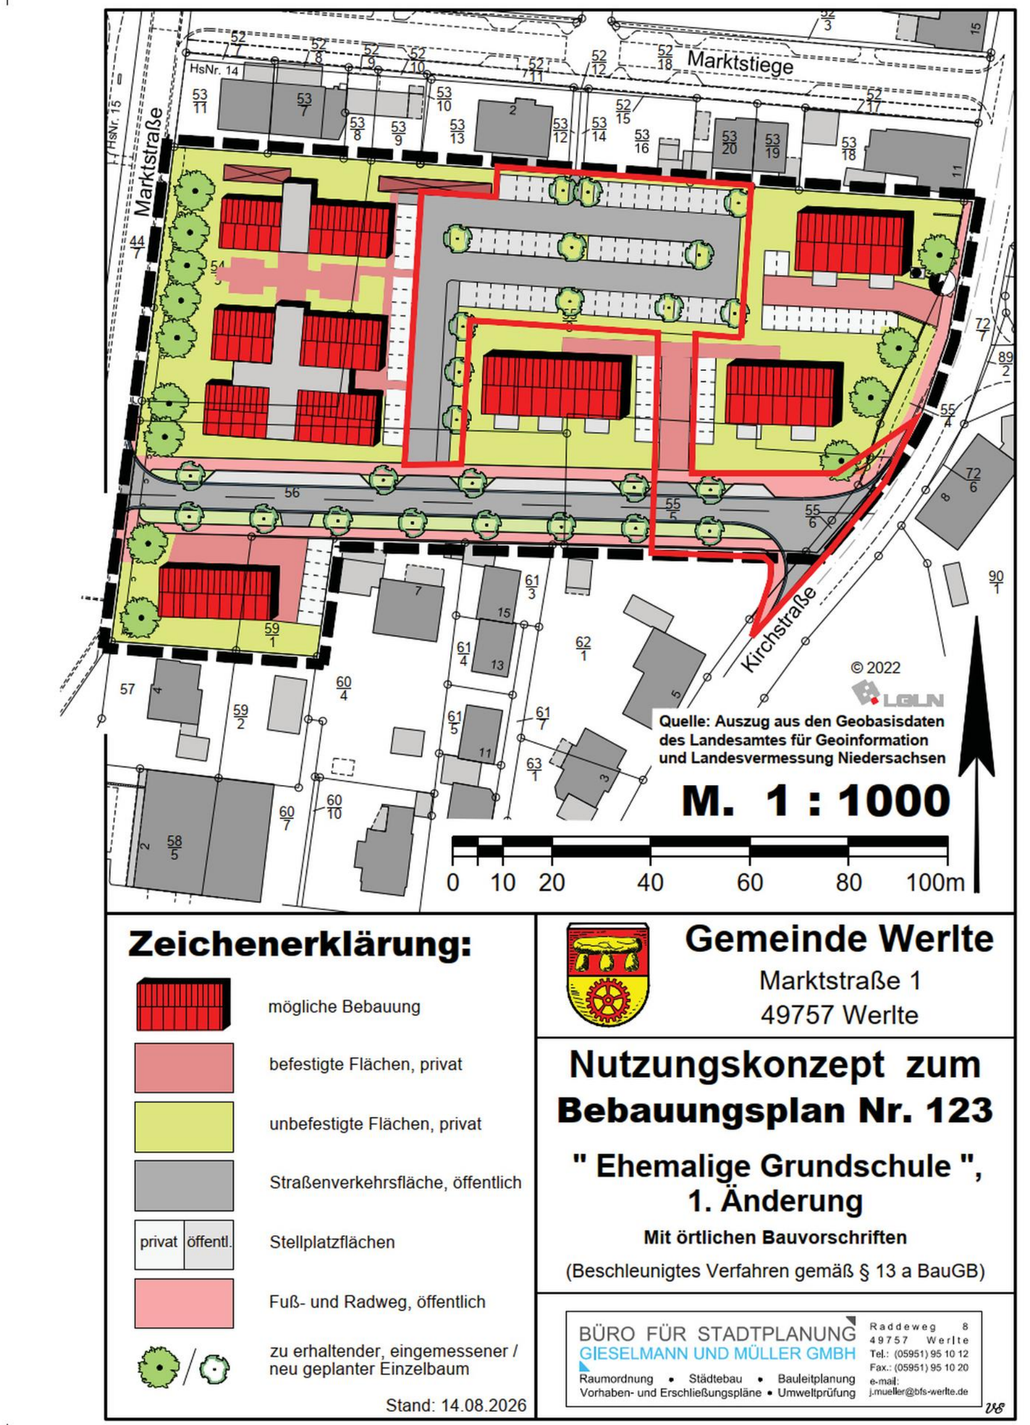
# Abgeleitete Grundstückskonturen (Näherung aus dem Nutzungskonzept)

GRUNDSTÜCK · TEILWEISE ABGELEITET

Blau: Kandidat K1, grün: Kandidat K2, orange: Baufenster K1 (3 m Abstand) · Maßstabsabgriff aus Abb. 3, ±2 m · KEINE vermessenen Grenzen

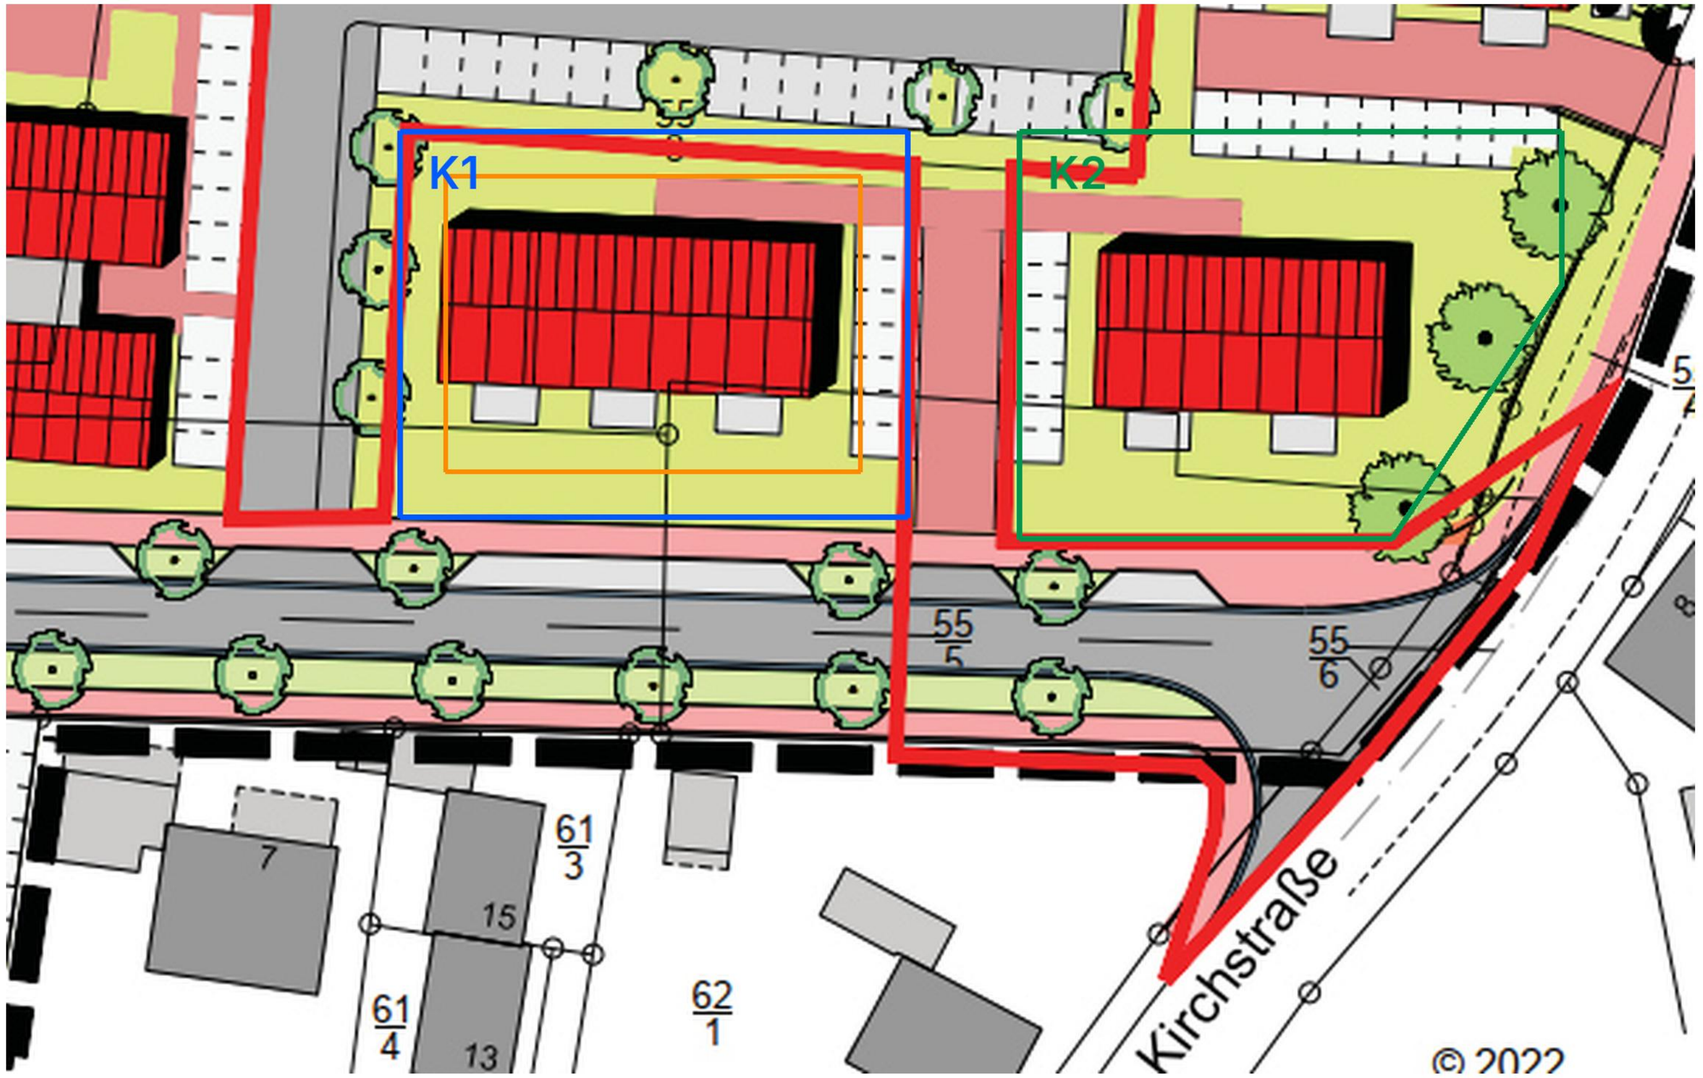


Ableitung: Maßstab 1:1000 der Abbildung; Straßenbreite Planstraße 16 m und Stichstraße/Parkplatz-Arm 11 m dienten als Kontrolle. Die grünen Flächen zwischen Planstraße (Süden), Parkplatz (Norden), Stichstraße (Westen) und Fuß-/Radweg (Osten) sind als Baufelder abgegrenzt; Parzellengrenzen sind in der Abbildung nicht eingezeichnet.


K1: ca. 33 × 25 m ≈ 830 m². K2: ca. 35 × 27 m ≈ 900 m² (Trapez). Die Projektangabe 960 m² passt zu keinem der beiden genau; Baufeld 3 kann also ein anderes Baufeld sein oder Teile der angrenzenden Wege einschließen. Die Zuordnung erfordert Seite 13/15/16 des Auftraggebers.

Baugrenzen (Entwurf): 3,0 m Abstand zu Planstraße und Parkplatz (gesichert); Ost/West angenommen. Baufenster K1 ≈ 27 × 19 m = 513 m².

# Realistischster Lageplan: Kandidat K1 mit Baufenster und Gebäudefußabdrücken

GRUNDSTÜCK · TEILWEISE ABGELEITET

Maße in m, Näherung ±2 m · Baugrenze N/S 3,0 m gesichert, W/O 3,0 m angenommen · Parken auf eigener Fläche nach Fußabdruck

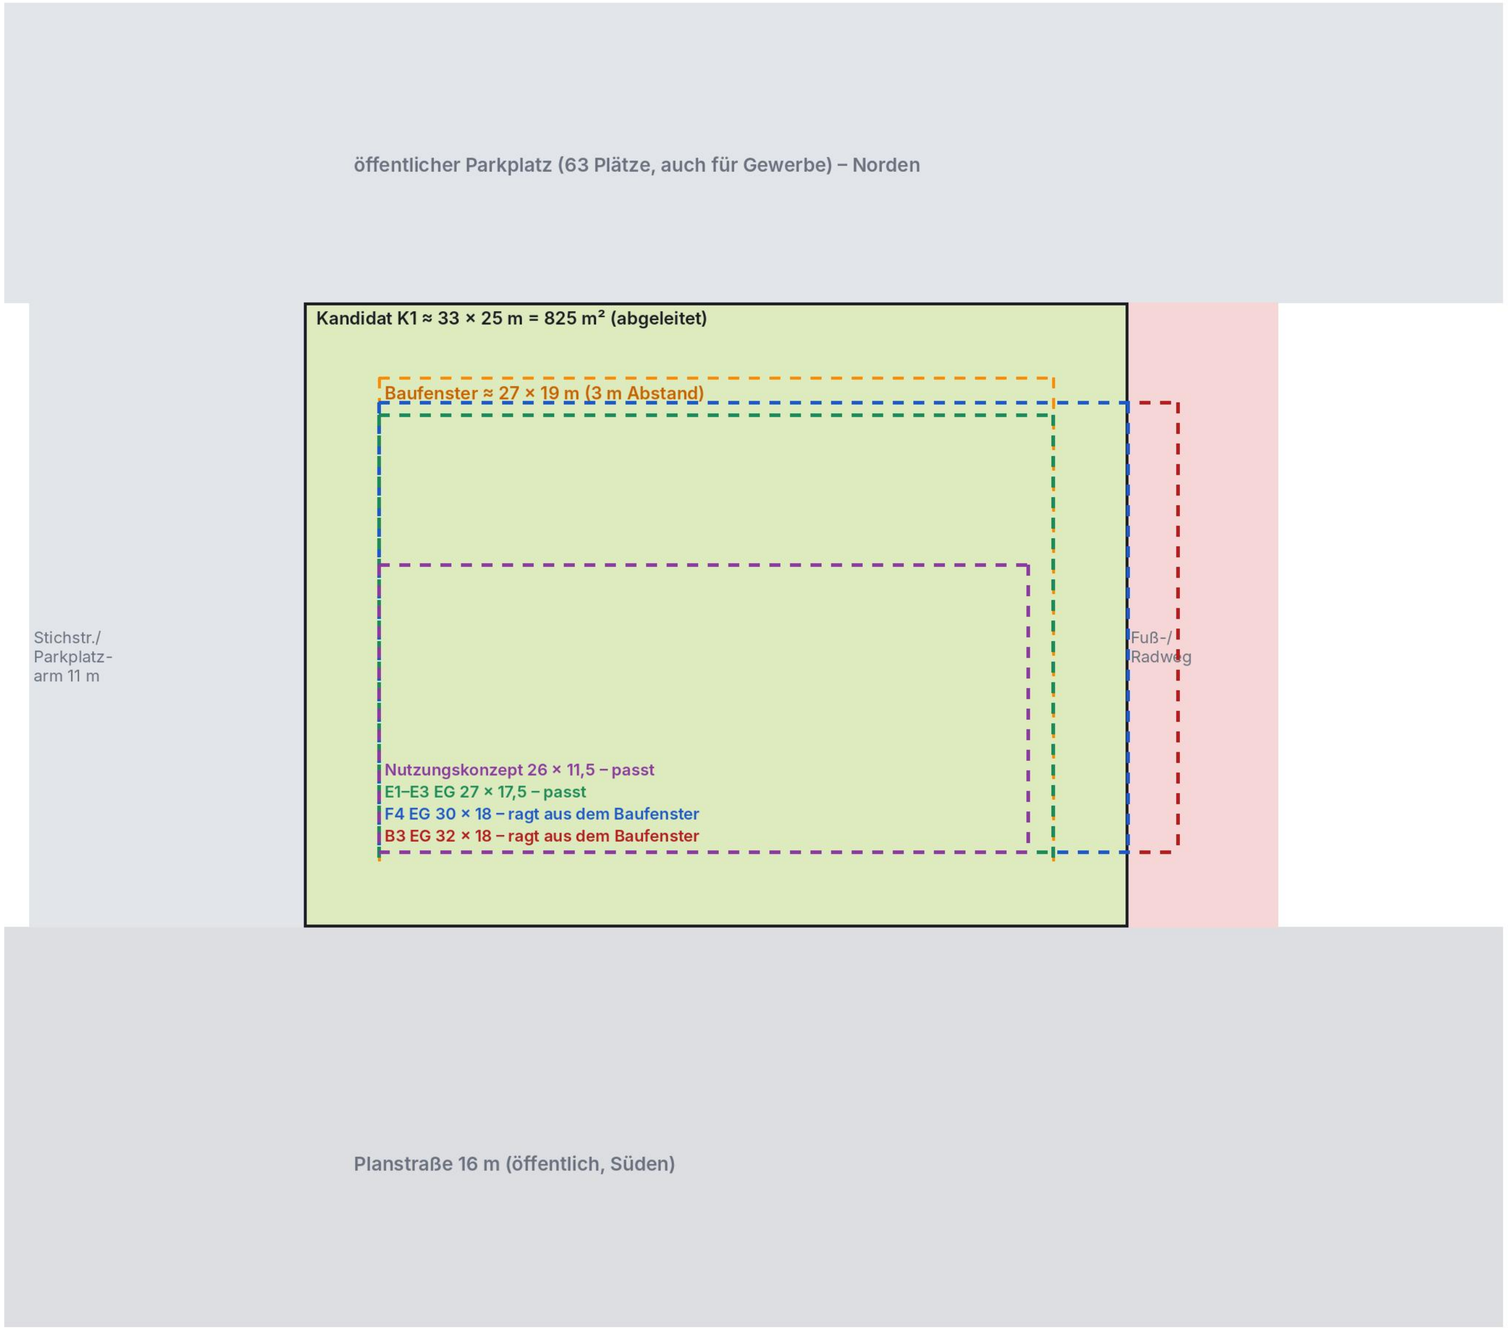


| Fußabdruck | Baufenster K1 27 × 19 | Baufenster K2 ≈ 29 × 21 |
|---|---|---|
| B3 / A, B, C, D: EG 32 × 18 m | passt NICHT | passt NICHT |
| E1–E3: EG 27 × 17,5 m | passt | passt |
| E4: EG 27 × 12,5 m | passt | passt |
| F1–F3: EG 18 × 30 m (30 m tief) | passt NICHT | passt NICHT |
| F4: EG 30 × 18 m | passt NICHT | passt NICHT |
| Nutzungskonzept (Abb. 3): ca. 26 × 11,5 m | passt | passt |

Befund (unter dem Vorbehalt der Kandidatenwahl): Der Entwurf B3 (EG 32 × 18 m, 576 m²) passt in keines der beiden Baufenster. F mit 540 m² passt nur in der gedrehten Lesart (30 × 18 m) und nur bei breiterem Baufenster; die wörtliche Lesart 18 × 30 m (30 m tief) passt nicht. Umlaufender Vorbau über die Baugrenze und Parken unter dem Vorbau auf eigener Fläche sind auf den abgeleiteten Grundstücken nicht möglich. Stellplätze für Gastro/Büro müssten über den öffentlichen Parkplatz (63 Plätze, Baulast/Mitnutzung ungeklärt) oder die vom Nutzungskonzept vorgesehenen privaten Stellplätze neben den Gebäuden nachgewiesen werden.

Parken auf K1: nach Abzug von Baufenster und Baugrenzstreifen (3 m) bleiben ≤ 3–4,5 m Tiefe → keine 5-m-Stellplätze mit Fahrgasse; allenfalls Längsparker im Südstreifen (Ausfahrt über Gehweg ungeklärt).

# Konsequenzen und was für eine belastbare Aussage fehlt

GRUNDSTÜCK · TEILWEISE ABGELEITET

Offene Punkte

Fehlt: (1) die Fotos der Seiten 13, 15, 16 (oder der Hinweis, welches Baufeld im Nutzungskonzept „Baufeld 3“ ist); (2) der rechtskräftige Ursprungsplan Nr. 123 (14.04.2023) mit Festsetzungen zu Vollgeschossen/Höhen/Baugrenzen des Baufelds; (3) Katasterauszug/Vermessung für die Grenzen; (4) Fahrbahnhöhe der Erschließungsstraße vor dem Baukörper (Bauamt); (5) städtebaulicher Vertrag/Kaufvertrag mit Stellplatzregelung; (6) Zusage zur Mitnutzung des öffentlichen Parkplatzes/Baulast.

Folgerungen für die Variantenstudie: Die Varianten E/F auf dem hypothetischen Rechteck 32 × 30 m zeigen Obergrenzen. Auf den aus den amtlichen Plänen abgeleiteten Baufeldern (ca. 830–900 m², Baufenster ca. 27 × 19 m) bleiben nur kleinere Gebäude möglich (Nutzungskonzept: ca. 26 × 11,5 m); die Wohnflächen der Varianten sind dann nicht realisierbar. Erst nach Klärung der Punkte (1)–(6) lässt sich eine Variante dimensionieren.

Keine Variante wurde festgelegt; bestehende Modelle und B3 sind unverändert.