# Vergleich der Varianten B, C, E1–E4 und F1–F4

VERGLEICH · NICHT FESTGELEGT

Entwurfsstudie Baufeld 3 · alle Werte vorläufig · keine Variante festgelegt

Ziel: Gebäudehöhe bis 12,00 m planerisch ausnutzen (drei Geschosse, keine zusätzlichen), umlaufender säulengestützter Vorbau, Zufahrt und Stellplätze unter und neben dem Vorbau. Keine Variante ist festgelegt; B3 (Variante A) und alle bestehenden Modelle bleiben unverändert. Alle Flächen sind vorläufig, bis Grundstücksgrenzen und Baugrenzen verlässlich geklärt sind.

| | Bestätigt (Quelle) | Annahme / unbestätigt |
|---|---|---|
| **Grundstück** | ca. 960 m² (Projektangabe); amtliche Unterlagen: B-Plan 123, 1. Änderung (Entwurf) mit Baugrenze 3,0 m zu Planstraße/Parkplatz | Zuschnitt 32 × 30 m = Hypothese H1; aus Nutzungskonzept abgeleitete Kandidaten ca. 33 × 25 m / 35 × 27 m (±2 m); Foto-Seiten 13/15/16 fehlen |
| **Höhe / Geschosse** | Entwurf B-Plan 123, 1. Änd.: H = 12,00 m über OK Fahrbahn, SH ≤ 0,30 m, TH 6,50 m, zwingend II Vollgeschosse, Dach ≥ 38°; 2–3 Geschosse laut Auftraggeber | Plan nur ENTWURF, Ursprungsplan unbekannt; 12 m gelten erst nach Klärung (Fahrbahnhöhe, Dachform, Vollgeschosse) als eingehalten |
| **Stellplätze Wohnen** | KEINE gesetzliche Pflicht seit 01.07.2024 (§ 47 Abs. 1 Satz 3 NBauO; FAQ Land Niedersachsen Stand 11.07.2025) | ob B-Plan/städtebaulicher Vertrag/Kaufvertrag Stellplätze für Wohnungen verlangt: unbekannt |
| **Stellplätze Gastro/Büro** | Pflicht besteht; Bemessung bedarfsorientiert (Richtzahlen Erlass: Gaststätte 1 je 8–12 Sitzplätze, Büro 1 je 30–40 m²) | Gaststättenart („örtliche Bedeutung“) und Sitzplatzzahl angenommen |
| **Maße** | – | Stellplatz 2,50 × 5,00 m, Fahrgasse 6,00 m, Säule Ø 0,40 m (Vorgaben/Annahmen), Zufahrtslage |
| **Wohnfläche** | B3: 846 m², 16 WE (Plan) | übrige Varianten aus Geschosskonturen geschätzt (0,88 × Wohnstreifen) |

# Grundstück, Baugrenzen und Quellenstatus

VERGLEICH · NICHT FESTGELEGT

Was gesichert ist, was nur aus Beschreibungen stammt und was Hypothese ist


| Punkt | Stand | Herkunft / Bemerkung |
|---|---|---|
| **Grundstücksfläche ca. 960 m²** | GESICHERT (Projektangabe) | Projektunterlagen/Auftraggeber; nicht am Liegenschaftsnachweis geprüft |
| **Zuschnitt 32 × 30 m** | HYPOTHESE H1 | Nur aus 960 m² und B3-Annahme; weder vermessen noch aus einem Plan gemessen |
| **B-Plan Nr. 123 „Ehemalige Grundschule“, 1. Änderung (Entwurf 25.09.2026): MI, GRZ 0,6, II zwingend, TH 6,50 m, H 12,00 m, SH 0,30 m, Baugrenze 3 m** | GESICHERT (Entwurf) | amtliche Unterlagen der Stadt Werlte (sgwerlte.de), in quellen_stadt/ abgelegt; nicht rechtskräftig |
| **Foto-Seiten 13/15/16 des Auftraggebers („zwei- bis dreigeschossig“)** | FEHLEN | ZIP nicht angekommen; Seite 15/16 entsprechen vermutlich Abb. 2/3 der 1. Änderung (unbestätigt) |
| **Zuordnung „Baufeld 3“ im Nutzungskonzept** | UNBEKANNT | ohne Seite 13 nicht bestimmbar; Kandidaten K1/K2 abgeleitet |
| **Baugrenzen / Baulinien, GRZ, Abstandsflächen** | UNBEKANNT | keine Maße am Plan abgelesen; alle Konturen in den Plänen sind Hypothese |
| **Erschließungsstraße, Zufahrt, Platzseite** | ANNAHME | Platz an der Seite y = 0; Zufahrt von Osten (E) bzw. Süden (F) angenommen |
| **Stellplatz 2,50 × 5,00 m, Fahrgasse 6,00 m** | ANNAHME (Auftraggeber, vorläufig) | Abgleich mit Stellplatzsatzung/Garagenverordnung ausstehend |

Die ZIP-Datei mit den Fotos der Seiten 13, 15 und 16 ist in dieser Sitzung nicht angekommen; der Ordner quellen_stadt/fotos_stadt_unterlagen/ ist leer. Grundlage sind die amtlichen Planunterlagen der Stadt (Entwurf B-Plan 123, 1. Änderung). Konturen aus den Plänen sind als ABGELEITET (±2 m) gekennzeichnet, gesicherte Maße getrennt.

# Planungsrecht: Höhe 12,00 m und ihr Bezugspunkt

GRUNDSTÜCK · TEILWEISE ABGELEITET

B-Plan Nr. 123, 1. Änderung, Entwurf (Textliche Festsetzung 1.2) · Antwort auf: verbindlich festgesetzt? von wo gemessen?

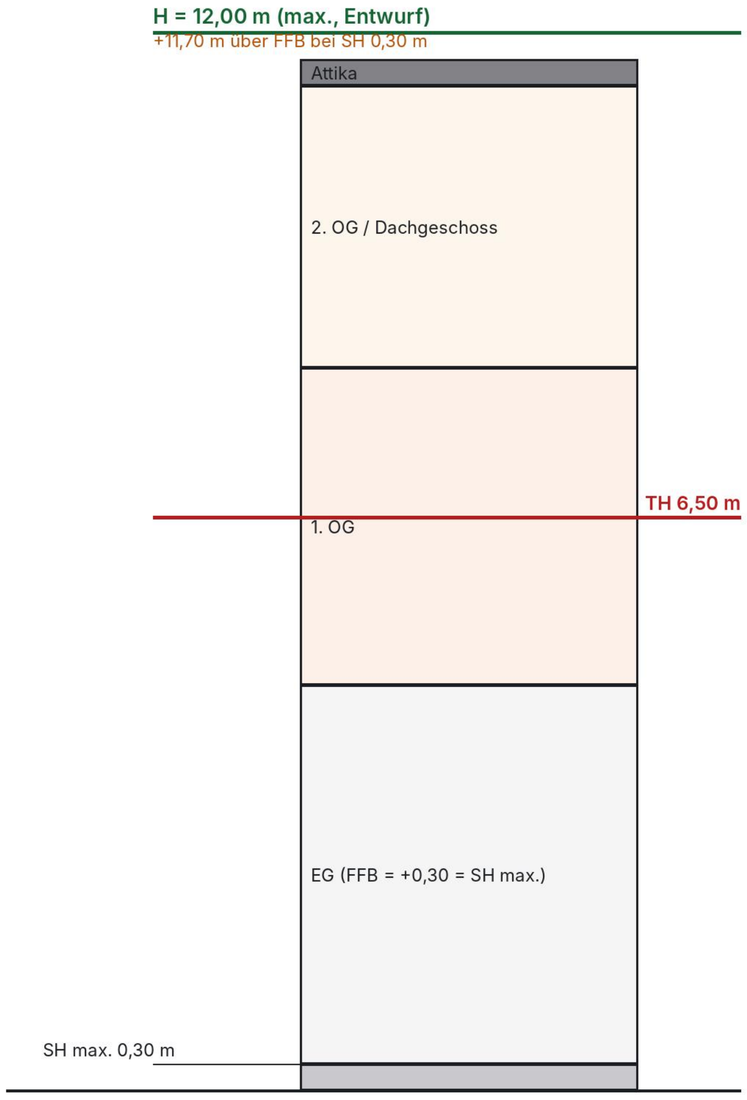



| Frage | Antwort |
|---|---|
| **Ist 12 m verbindlich festgesetzt?** | Im ENTWURF der 1. Änderung (H = 12,00 m). Satzungsbeschluss steht aus; der rechtskräftige Ursprungsplan 123 (14.04.2023) liegt nicht vor. → Nicht als verbindlich nachgewiesen. |
| **Von wo gemessen?** | Unterer Bezugspunkt: Oberkante Fahrbahn der nächstgelegenen ausgebauten Erschließungsstraße in der Mitte vor dem Baukörper (Höhe beim Bauamt erfragbar). Oberer Punkt: Oberkante Baukörper (First, Hauptgesims); untergeordnete Teile (Antennen, Schornsteine) zählen nicht. |
| **Verhältnis zu FFB EG** | FFB EG max. 0,30 m über dem Bezugspunkt (SH). Bei SH 0,30 m: Baukörper max. +11,70 m über FFB; E/F zeichnen +12,00 m über FFB → bei SH > 0 überschritten, nur bei FFB = Fahrbahnhöhe möglich. |
| **Traufhöhe** | max. 6,50 m (Schnittkante Mauerwerk/Dachhaut): Oberkante 1. OG der Entwürfe (+7,90 / +8,20 m) liegt darüber. |
| **Vollgeschosse / Dach** | II zwingend; Hauptdach geneigt ≥ 38° (Flachdach nur Verbindungsbauten, ≥ 1,0 m unter First, bzw. untergeordnete Teile ≤ 70 m²). Dreigeschossige Flachdachbauten (B3, B, C, E, F) passen nicht zum Entwurf. |
| **Fazit** | Die 12,00 m bleiben Planungsziel, gelten aber erst als eingehalten, wenn (1) Ursprungsplan/Satzung für Baufeld 3 vorliegt, (2) Fahrbahnhöhe vor dem Baukörper bekannt ist, (3) Traufe/Dachform/Vollgeschosse geklärt sind. |

# Abgeleitete Grundstückskonturen (Näherung aus dem Nutzungskonzept)

GRUNDSTÜCK · TEILWEISE ABGELEITET

Blau: Kandidat K1, grün: Kandidat K2, orange: Baufenster K1 (3 m Abstand) · Maßstabsabgriff aus Abb. 3, ±2 m · KEINE vermessenen Grenzen

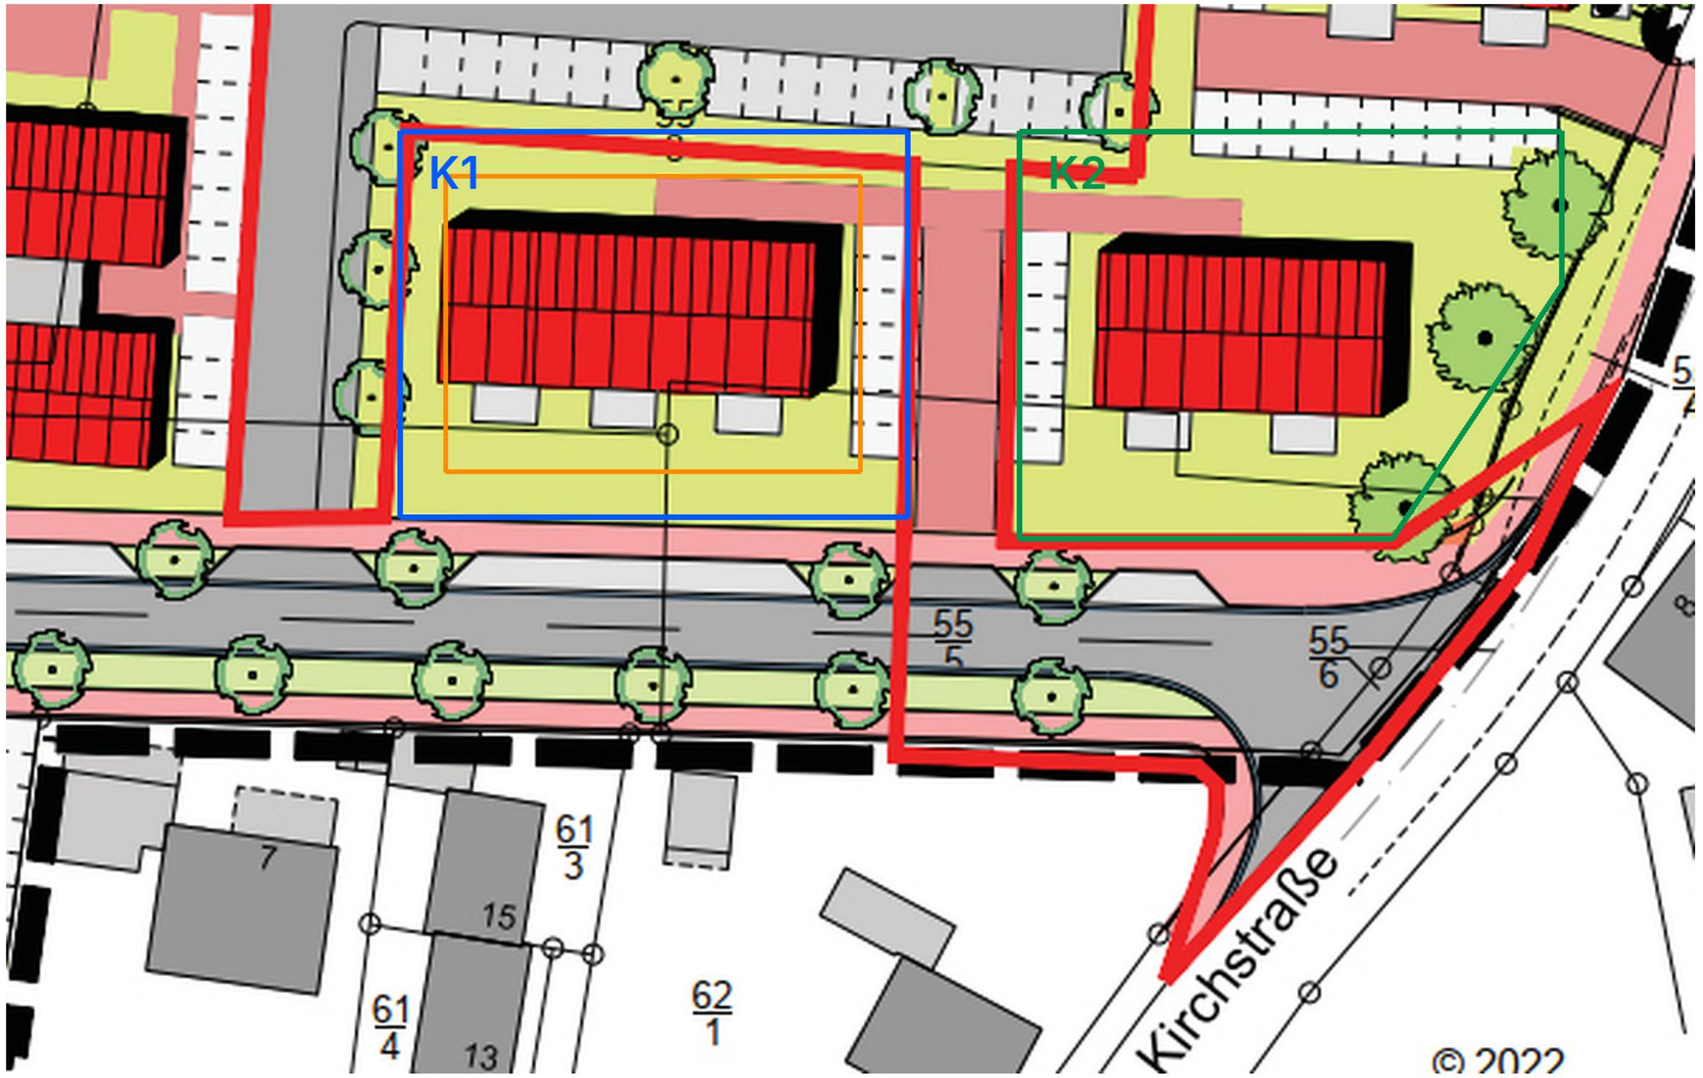


Ableitung: Maßstab 1:1000 der Abbildung; Straßenbreite Planstraße 16 m und Stichstraße/Parkplatz-Arm 11 m dienten als Kontrolle. Die grünen Flächen zwischen Planstraße (Süden), Parkplatz (Norden), Stichstraße (Westen) und Fuß-/Radweg (Osten) sind als Baufelder abgegrenzt; Parzellengrenzen sind in der Abbildung nicht eingezeichnet.


K1: ca. 33 × 25 m ≈ 830 m². K2: ca. 35 × 27 m ≈ 900 m² (Trapez). Die Projektangabe 960 m² passt zu keinem der beiden genau; Baufeld 3 kann also ein anderes Baufeld sein oder Teile der angrenzenden Wege einschließen. Die Zuordnung erfordert Seite 13/15/16 des Auftraggebers.

Baugrenzen (Entwurf): 3,0 m Abstand zu Planstraße und Parkplatz (gesichert); Ost/West angenommen. Baufenster K1 ≈ 27 × 19 m = 513 m².

# Lageplan Kandidat K1: Baufenster und Gebäudefußabdrücke

GRUNDSTÜCK · TEILWEISE ABGELEITET

Maße in m, Näherung ±2 m · Baugrenze N/S 3,0 m gesichert, W/O 3,0 m angenommen · Parken auf eigener Fläche nach Fußabdruck

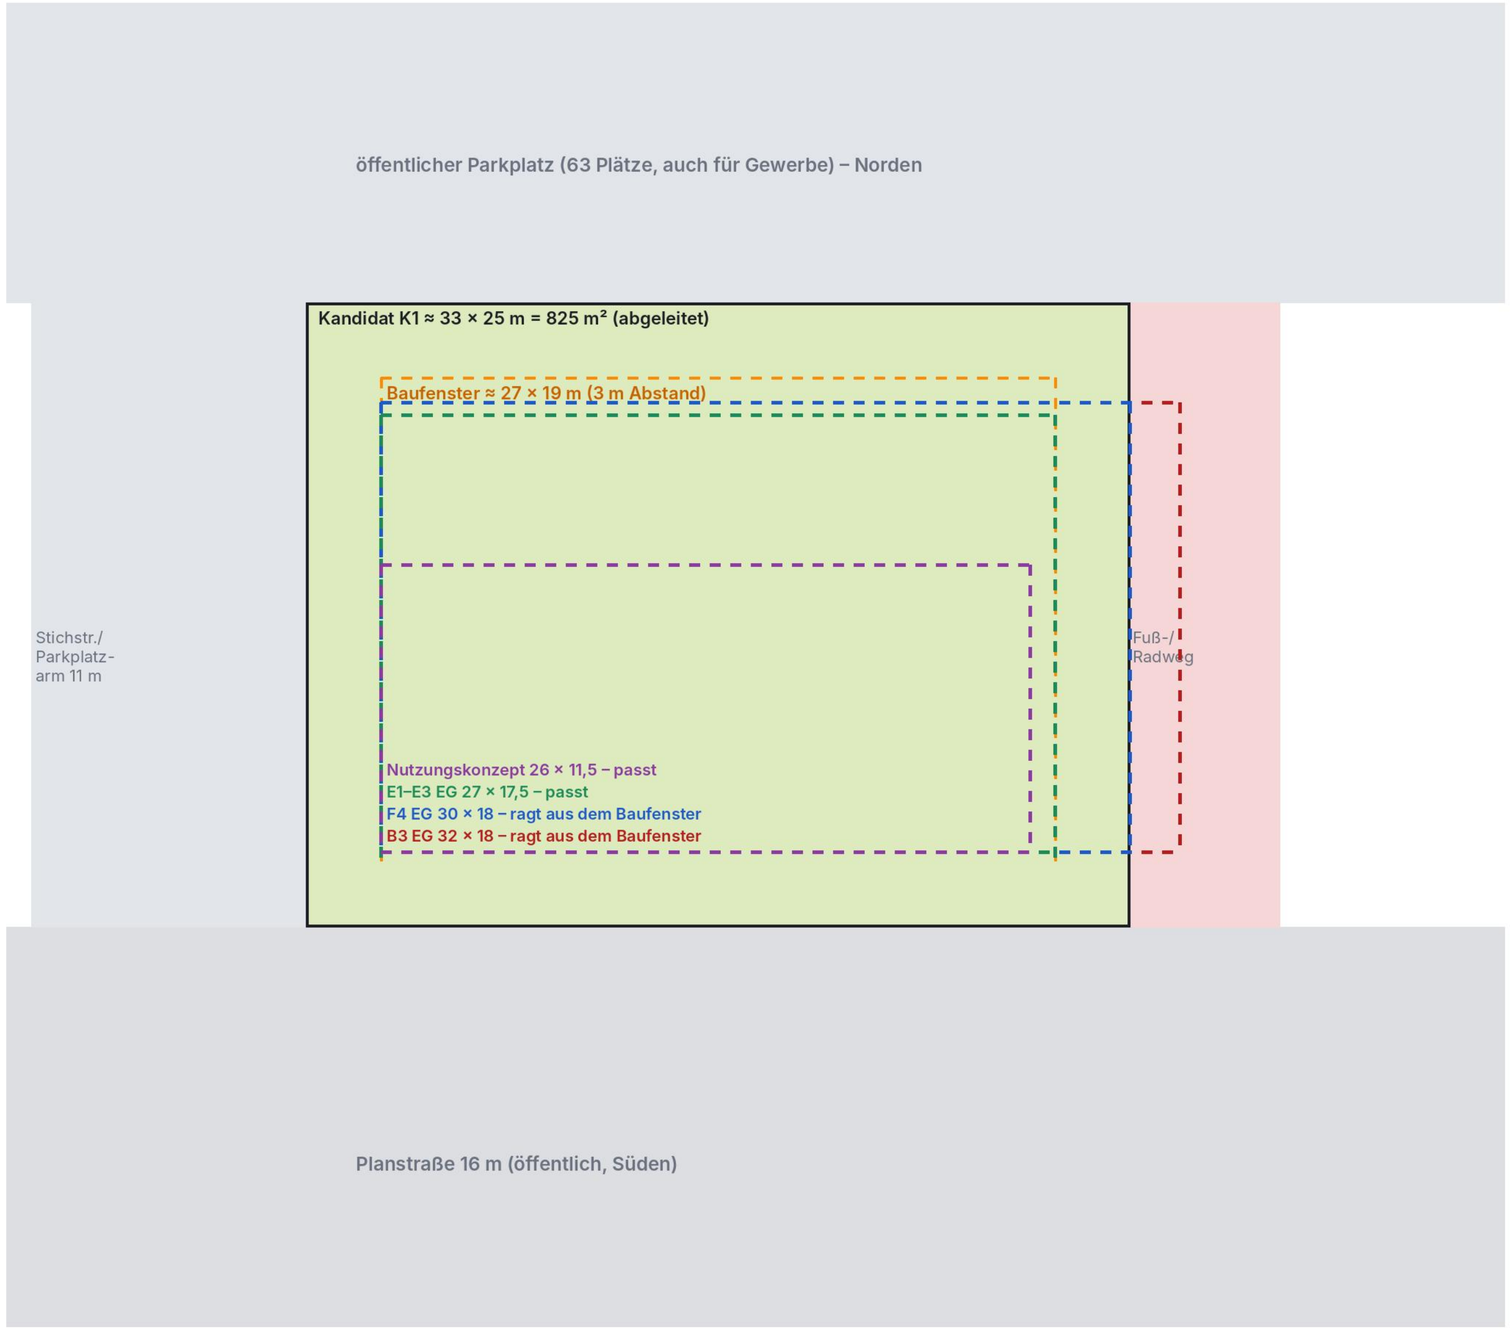


| Fußabdruck | Baufenster K1 27 × 19 | Baufenster K2 ≈ 29 × 21 |
|---|---|---|
| B3 / A, B, C, D: EG 32 × 18 m | passt NICHT | passt NICHT |
| E1–E3: EG 27 × 17,5 m | passt | passt |
| E4: EG 27 × 12,5 m | passt | passt |
| F1–F3: EG 18 × 30 m (30 m tief) | passt NICHT | passt NICHT |
| F4: EG 30 × 18 m | passt NICHT | passt NICHT |
| Nutzungskonzept (Abb. 3): ca. 26 × 11,5 m | passt | passt |

Befund (unter dem Vorbehalt der Kandidatenwahl): Der Entwurf B3 (EG 32 × 18 m, 576 m²) passt in keines der beiden Baufenster. F mit 540 m² passt nur in der gedrehten Lesart (30 × 18 m) und nur bei breiterem Baufenster; die wörtliche Lesart 18 × 30 m (30 m tief) passt nicht. Umlaufender Vorbau über die Baugrenze und Parken unter dem Vorbau auf eigener Fläche sind auf den abgeleiteten Grundstücken nicht möglich. Stellplätze für Gastro/Büro müssten über den öffentlichen Parkplatz (63 Plätze, Baulast/Mitnutzung ungeklärt) oder die vom Nutzungskonzept vorgesehenen privaten Stellplätze neben den Gebäuden nachgewiesen werden.


Parken auf K1: nach Abzug von Baufenster und Baugrenzstreifen (3 m) bleiben ≤ 3–4,5 m Tiefe → keine 5-m-Stellplätze mit Fahrgasse; allenfalls Längsparker im Südstreifen (Ausfahrt über Gehweg ungeklärt).

# Erhöhte Schrägansichten im Vergleich


gleiche Kamera, gleiche Darstellung

VERGLEICH · NICHT FESTGELEGT


**B – Umlaufender Vorbau mit Säulen**

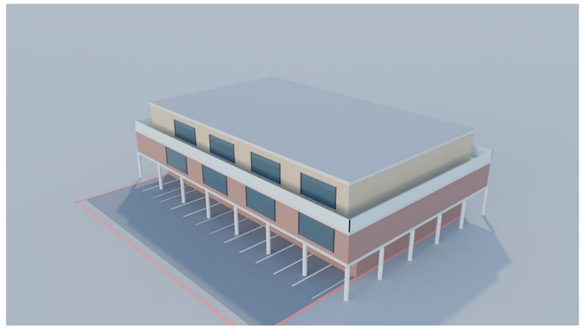


**C – Maximierung der Wohnfläche**

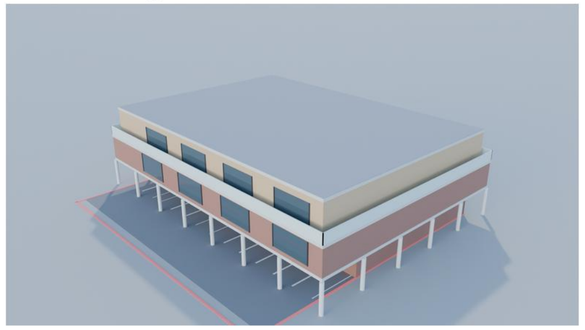


**E1 – Vorbau bis Attika**

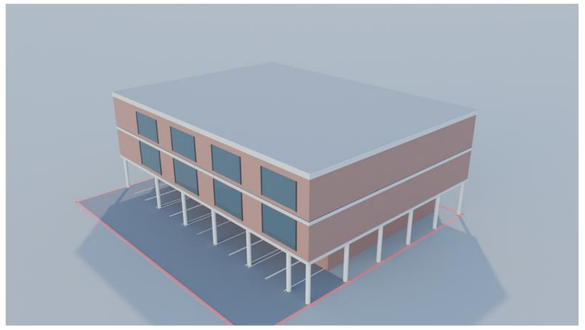


**E2 – Staffel 1,50 m zurück**

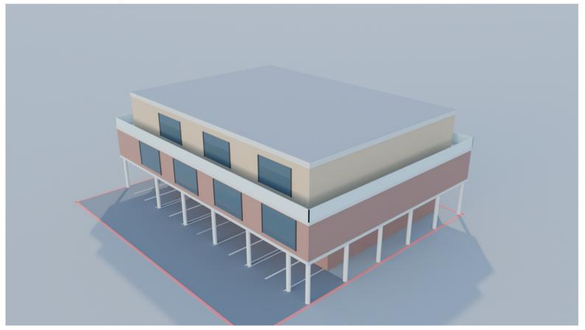


**F1 – EG 18×30 m, Vorbau bis Attika**

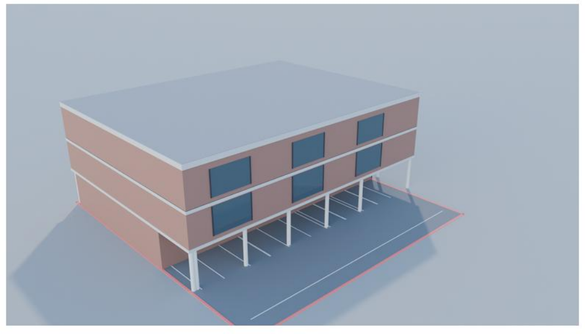


**F2 – EG 18×30 m, Staffel 1,50 m**

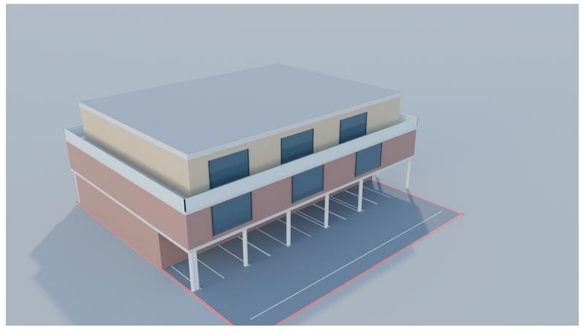

**F3 – EG 18×30 m, Staffel 3,00 m**

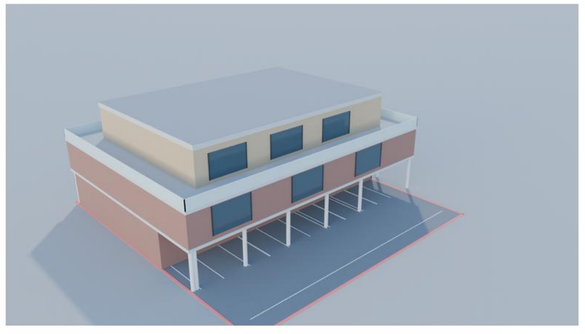

**F4 – EG 30×18 m**

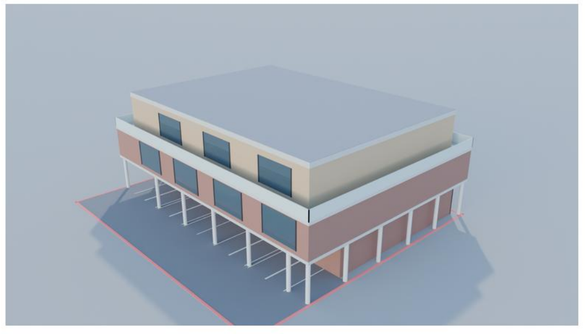


# Lagepläne im Vergleich (Stellplätze, Säulen, Zufahrt)


grün = funktioniert, orange = eingeschränkt, rot = Konflikt, rosa = nur rechnerisch verbleibend

VERGLEICH · NICHT FESTGELEGT


## E1 – Vorbau bis Attika (Staffel d

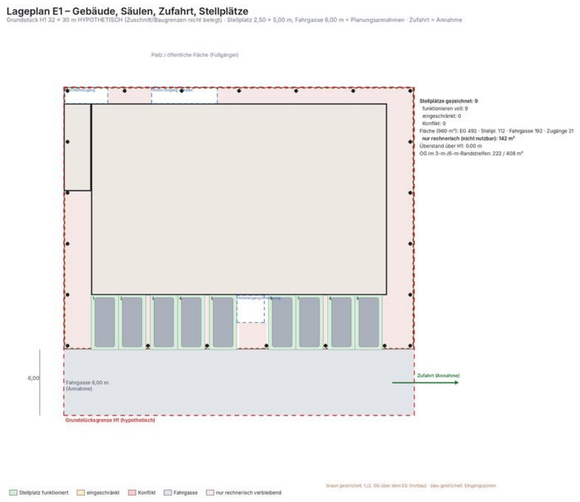



## E4 – zweireihiges Parken, kleiner

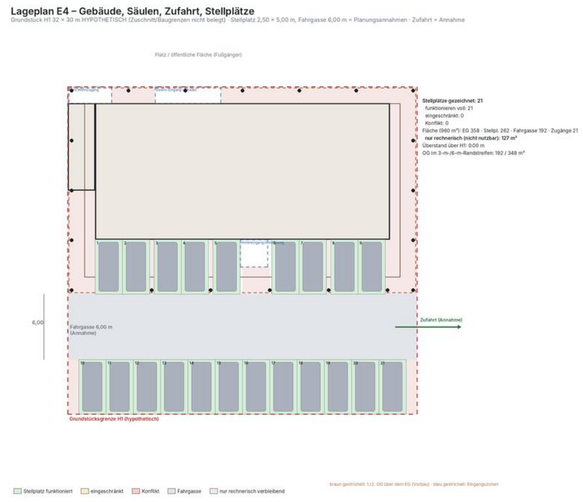


## F2 – EG 18×30 m, Staffel 1,50 m

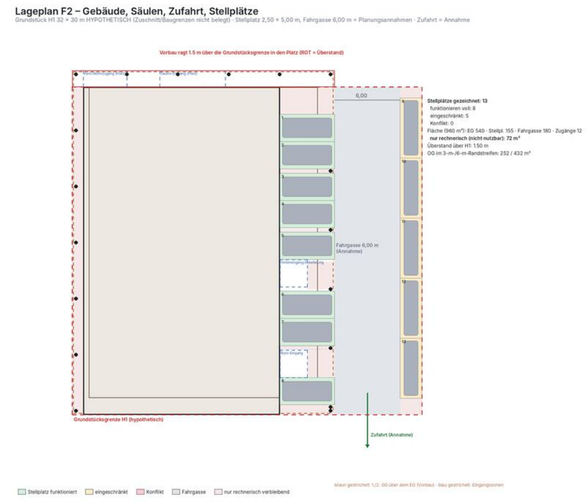


## F4 – EG 30×18 m (gedreht), Staffe

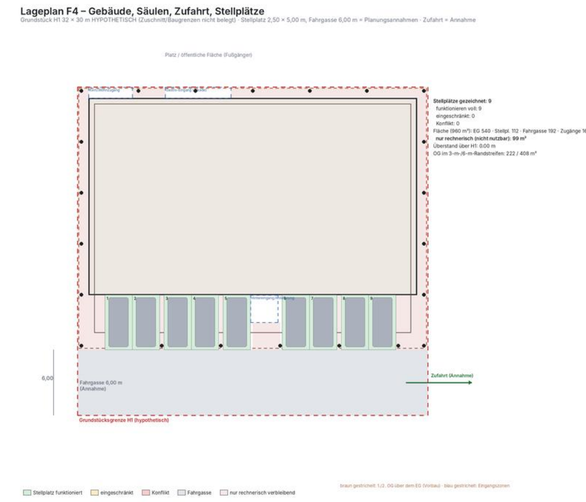

# Vergleichstabelle 1: Flächen, Gewerbe, Wohnungen

VERGLEICH · NICHT FESTGELEGT

alle Werte vorläufig; Wohnfläche = 0,88 × Wohnstreifen, schematisch

| Kennzahl | A | B | C | E1 | E2 | E3 | E4 | F1 | F2 | F3 | F4 |
|---|---|---|---|---|---|---|---|---|---|---|---|
| Höhe Attika (Bezug offen) | 9,90 | 9,90 | 9,90 | 12,00 | 12,00 | 12,00 | 12,00 | 12,00 | 12,00 | 12,00 | 12,00 |
| Außenmaß EG (m) | 32×18 | 32×18 | 32×18 | 30×18 | 30×18 | 30×18 | 30×12 | 18×30 | 18×30 | 18×30 | 30×18 |
| Grundfläche EG (m²) | 576 | 576 | 576 | 492 | 492 | 492 | 358 | 540 | 540 | 540 | 540 |
| Grundfläche 1. OG (m²) | 660 | 788 | 892 | 768 | 768 | 768 | 608 | 756 | 756 | 756 | 768 |
| Grundfläche 2. OG / Staffel (m²) | 539 | 624 | 798 | 768 | 609 | 468 | 464 | 756 | 598 | 459 | 609 |
| Gastraum (m²) / Plätze innen | 280/120 | 280/120 | 280/120 | 281/120 | 281/120 | 281/120 | 198/85 | 232/99 | 232/99 | 232/99 | 307/132 |
| Wohnfläche netto (m²) | 846 | 963 | 1.159 | 1.084 | 960 | 852 | 727 | 1.065 | 942 | 835 | 960 |
| Δ Wohnfläche gg. A (m²) | +0 | +117 | +313 | +238 | +114 | +6 | -119 | +219 | +96 | -11 | +114 |
| Wohnungen Standardmix | 16 | 18 | 18 | 18 | 16 | 15 | 16 | 14 | 14 | 13 | 16 |
| Größen min–max (m²) | 47–63 | 43–66 | 55–76 | 54–68 | 52–70 | 52–68 | 38–52 | 66–89 | 51–89 | 50–89 | 52–70 |
| Ø Wohnungsgröße (m²) | 53 | 54 | 64 | 60 | 60 | 57 | 45 | 76 | 67 | 64 | 60 |
| WE kleiner / größerer Mix | 19/13 | 21/14 | 21/14 | 20/14 | 19/12 | 17/12 | 19/12 | 18/12 | 17/11 | 16/11 | 19/12 |
| Säulen | 0 | 24 | 24 | 22 | 22 | 22 | 20 | 18 | 18 | 18 | 22 |
| Überstand über H1 (m) | 0,0 | 1,5 | 1,5 | 0,0 | 0,0 | 0,0 | 0,0 | 1,5 | 1,5 | 1,5 | 0,0 |

# Vergleichstabelle 2: Stellplätze (Pflicht und Ziel getrennt)

VERGLEICH · NICHT FESTGELEGT

„nutzbar“ nach geometrischer Prüfung (Säulen, Eingänge, Fahrgasse); B/C mit den 11 B3-Stellplätzen geprüft

| Kennzahl | A | B | C | E1 | E2 | E3 | E4 | F1 | F2 | F3 | F4 |
|---|---|---|---|---|---|---|---|---|---|---|---|
| **Stellplätze gezeichnet** | 11 | 11 | 11 | 9 | 9 | 9 | 21 | 13 | 13 | 13 | 9 |
| **davon voll nutzbar** | 11 | 5 | 5 | 9 | 9 | 9 | 21 | 8 | 8 | 8 | 9 |
| **eingeschränkt** | 0 | 0 | 0 | 0 | 0 | 0 | 0 | 5 | 5 | 5 | 0 |
| **Konflikt (Säule/Eingang/Gasse)** | 0 | 6 | 6 | 0 | 0 | 0 | 0 | 0 | 0 | 0 | 0 |
| **erforderlich § 47 (Gastro+Büro, Spanne)** | 11,4–16,9 | 11,4–16,9 | 11,4–16,9 | 11,4–16,9 | 11,4–16,9 | 11,4–16,9 | 8,5–12,5 | 9,7–14,3 | 9,7–14,3 | 9,7–14,3 | 12,4–18,3 |
| **erforderlich Mittel** | 13,6 | 13,6 | 13,6 | 13,6 | 13,6 | 13,6 | 10,1 | 11,6 | 11,6 | 11,6 | 14,8 |
| **erforderlich Wohnen** | 0 | 0 | 0 | 0 | 0 | 0 | 0 | 0 | 0 | 0 | 0 |
| **optional Wohnen 0,5–1,5/WE** | 8–24 | 9–27 | 9–27 | 9–27 | 8–24 | 8–22 | 8–24 | 7–21 | 7–21 | 6–20 | 8–24 |
| **nutzbar ≥ Untergrenze / Mittel / Obergrenze** | nein/nein/nein | nein/nein/nein | nein/nein/nein | nein/nein/nein | nein/nein/nein | nein/nein/nein | ja/ja/ja | ja/ja/nein | ja/ja/nein | ja/ja/nein | nein/nein/nein |
| **Bemerkung** | B3 | 6/11 gestört | 6/11 gestört | 1 Reihe | 1 Reihe | 1 Reihe | 2 Reihen | Sackgasse | Sackgasse | Sackgasse | 1 Reihe |

Wichtig: Die Bewertung der Stellplätze erfolgt gegen die gesetzliche Pflicht (Gastro + Büro), nicht gegen eine pauschale Wohnungsquote. E4 wird daher nicht wegen fehlender Wohnungsstellplätze abgewertet; es hat den größten Überhang gegenüber der Pflicht, bezahlt dies aber mit 135 m² weniger Gewerbe-EG gegenüber E1–E3. F1–F3 erreichen die Pflicht (Mittel) mit 13 nutzbaren Plätzen knapp; E1–E3 und F4 (9 Plätze) liegen darunter.

# Baurechtliche Ampel (vorläufig)

Keine Rechtsprüfung · bis zur Klärung von Grundstück, Baugrenzen und Satzungen offen

VERGLEICH · NICHT FESTGELEGT

| Kriterium | E1 | E2 | E3 | E4 | F1 | F2 | F3 | F4 |
|---|---|---|---|---|---|---|---|---|
| **Gebäudehöhe 12,00 m** | kritisch / offen: Attika +12,00 m über FFB. Entwurf B-Plan 123: H = 12,00 m über OK Fahrbahn, FFB max. +0,30 m → Baukörper max. +11,70 m über FFB; Fahrbahnhöhe unbekannt, Plan nur Entwurf – NICHT als eingehalten zu werten. | kritisch / offen: Attika +12,00 m über FFB. Entwurf B-Plan 123: H = 12,00 m über OK Fahrbahn, FFB max. +0,30 m → Baukörper max. +11,70 m über FFB; Fahrbahnhöhe unbekannt, Plan nur Entwurf – NICHT als eingehalten zu werten. | kritisch / offen: Attika +12,00 m über FFB. Entwurf B-Plan 123: H = 12,00 m über OK Fahrbahn, FFB max. +0,30 m → Baukörper max. +11,70 m über FFB; Fahrbahnhöhe unbekannt, Plan nur Entwurf – NICHT als eingehalten zu werten. | kritisch / offen: Attika +12,00 m über FFB. Entwurf B-Plan 123: H = 12,00 m über OK Fahrbahn, FFB max. +0,30 m → Baukörper max. +11,70 m über FFB; Fahrbahnhöhe unbekannt, Plan nur Entwurf – NICHT als eingehalten zu werten. | kritisch / offen: Attika +12,00 m über FFB. Entwurf B-Plan 123: H = 12,00 m über OK Fahrbahn, FFB max. +0,30 m → Baukörper max. +11,70 m über FFB; Fahrbahnhöhe unbekannt, Plan nur Entwurf – NICHT als eingehalten zu werten. | kritisch / offen: Attika +12,00 m über FFB. Entwurf B-Plan 123: H = 12,00 m über OK Fahrbahn, FFB max. +0,30 m → Baukörper max. +11,70 m über FFB; Fahrbahnhöhe unbekannt, Plan nur Entwurf – NICHT als eingehalten zu werten. | kritisch / offen: Attika +12,00 m über FFB. Entwurf B-Plan 123: H = 12,00 m über OK Fahrbahn, FFB max. +0,30 m → Baukörper max. +11,70 m über FFB; Fahrbahnhöhe unbekannt, Plan nur Entwurf – NICHT als eingehalten zu werten. | kritisch / offen: Attika +12,00 m über FFB. Entwurf B-Plan 123: H = 12,00 m über OK Fahrbahn, FFB max. +0,30 m → Baukörper max. +11,70 m über FFB; Fahrbahnhöhe unbekannt, Plan nur Entwurf – NICHT als eingehalten zu werten. |
| **Geschosse / Traufe / Dach** | kritisch / offen: Entwurf 1. Änderung: zwingend II Vollgeschosse, TH max. 6,50 m, Hauptdach geneigt ≥ 38° (Flachdach nur untergeordnet). Drei Geschosse mit Flachdach, Oberkante 1. OG +7,90 m und 2. OG = 100 % des 1. OG widersprechen dem Entwurf; Ursprungsplan unbekannt. | kritisch / offen: Entwurf 1. Änderung: zwingend II Vollgeschosse, TH max. 6,50 m, Hauptdach geneigt ≥ 38° (Flachdach nur untergeordnet). Drei Geschosse mit Flachdach, Oberkante 1. OG +7,90 m und 2. OG = 79 % des 1. OG widersprechen dem Entwurf; Ursprungsplan unbekannt. | kritisch / offen: Entwurf 1. Änderung: zwingend II Vollgeschosse, TH max. 6,50 m, Hauptdach geneigt ≥ 38° (Flachdach nur untergeordnet). Drei Geschosse mit Flachdach, Oberkante 1. OG +7,90 m und 2. OG = 61 % des 1. OG widersprechen dem Entwurf; Ursprungsplan unbekannt. | kritisch / offen: Entwurf 1. Änderung: zwingend II Vollgeschosse, TH max. 6,50 m, Hauptdach geneigt ≥ 38° (Flachdach nur untergeordnet). Drei Geschosse mit Flachdach, Oberkante 1. OG +7,90 m und 2. OG = 76 % des 1. OG widersprechen dem Entwurf; Ursprungsplan unbekannt. | kritisch / offen: Entwurf 1. Änderung: zwingend II Vollgeschosse, TH max. 6,50 m, Hauptdach geneigt ≥ 38° (Flachdach nur untergeordnet). Drei Geschosse mit Flachdach, Oberkante 1. OG +7,90 m und 2. OG = 100 % des 1. OG widersprechen dem Entwurf; Ursprungsplan unbekannt. | kritisch / offen: Entwurf 1. Änderung: zwingend II Vollgeschosse, TH max. 6,50 m, Hauptdach geneigt ≥ 38° (Flachdach nur untergeordnet). Drei Geschosse mit Flachdach, Oberkante 1. OG +7,90 m und 2. OG = 79 % des 1. OG widersprechen dem Entwurf; Ursprungsplan unbekannt. | kritisch / offen: Entwurf 1. Änderung: zwingend II Vollgeschosse, TH max. 6,50 m, Hauptdach geneigt ≥ 38° (Flachdach nur untergeordnet). Drei Geschosse mit Flachdach, Oberkante 1. OG +7,90 m und 2. OG = 61 % des 1. OG widersprechen dem Entwurf; Ursprungsplan unbekannt. | kritisch / offen: Entwurf 1. Änderung: zwingend II Vollgeschosse, TH max. 6,50 m, Hauptdach geneigt ≥ 38° (Flachdach nur untergeordnet). Drei Geschosse mit Flachdach, Oberkante 1. OG +7,90 m und 2. OG = 79 % des 1. OG widersprechen dem Entwurf; Ursprungsplan unbekannt. |
| **GRZ / Überdeckung** | zu prüfen: größte Geschossprojektion 768 m² = 80 % von 960 m² (GRZ 0,6 = 576 m² nur Annahme). | zu prüfen: größte Geschossprojektion 768 m² = 80 % von 960 m² (GRZ 0,6 = 576 m² nur Annahme). | zu prüfen: größte Geschossprojektion 768 m² = 80 % von 960 m² (GRZ 0,6 = 576 m² nur Annahme). | zu prüfen: größte Geschossprojektion 608 m² = 63 % von 960 m² (GRZ 0,6 = 576 m² nur Annahme). | zu prüfen: größte Geschossprojektion 756 m² = 79 % von 960 m² (GRZ 0,6 = 576 m² nur Annahme). | zu prüfen: größte Geschossprojektion 756 m² = 79 % von 960 m² (GRZ 0,6 = 576 m² nur Annahme). | zu prüfen: größte Geschossprojektion 756 m² = 79 % von 960 m² (GRZ 0,6 = 576 m² nur Annahme). | zu prüfen: größte Geschossprojektion 768 m² = 80 % von 960 m² (GRZ 0,6 = 576 m² nur Annahme). |
| **Grenzen / Baugrenzen** | kritisch / offen: Außenkante OG auf angenommener Grenze (0,00 m). Entwurf: Baugrenze 3,0 m zu Planstraße/Parkplatz – der Vorbau über die Baugrenze ist unzulässig; auf den aus den amtlichen Plänen abgeleiteten Baufeldern (≈ 27 × 19 m Baufenster) passt der Fußabdruck nicht (siehe Grundstücksanalyse). | kritisch / offen: Außenkante OG auf angenommener Grenze (0,00 m). Entwurf: Baugrenze 3,0 m zu Planstraße/Parkplatz – der Vorbau über die Baugrenze ist unzulässig; auf den aus den amtlichen Plänen abgeleiteten Baufeldern (≈ 27 × 19 m Baufenster) passt der Fußabdruck nicht (siehe Grundstücksanalyse). | kritisch / offen: Außenkante OG auf angenommener Grenze (0,00 m). Entwurf: Baugrenze 3,0 m zu Planstraße/Parkplatz – der Vorbau über die Baugrenze ist unzulässig; auf den aus den amtlichen Plänen abgeleiteten Baufeldern (≈ 27 × 19 m Baufenster) passt der Fußabdruck nicht (siehe Grundstücksanalyse). | kritisch / offen: Außenkante OG auf angenommener Grenze (0,00 m). Entwurf: Baugrenze 3,0 m zu Planstraße/Parkplatz – der Vorbau über die Baugrenze ist unzulässig; auf den aus den amtlichen Plänen abgeleiteten Baufeldern (≈ 27 × 19 m Baufenster) passt der Fußabdruck nicht (siehe Grundstücksanalyse). | kritisch / offen: Überstand 1,50 m über H1 (Platzseite); Außenkante sonst auf der Grenze. | kritisch / offen: Überstand 1,50 m über H1 (Platzseite); Außenkante sonst auf der Grenze. | kritisch / offen: Überstand 1,50 m über H1 (Platzseite); Außenkante sonst auf der Grenze. | kritisch / offen: Außenkante OG auf angenommener Grenze (0,00 m). Entwurf: Baugrenze 3,0 m zu Planstraße/Parkplatz – der Vorbau über die Baugrenze ist unzulässig; auf den aus den amtlichen Plänen abgeleiteten Baufeldern (≈ 27 × 19 m Baufenster) passt der Fußabdruck nicht (siehe Grundstücksanalyse). |
| **Stellplätze (gesetzlich)** | kritisch / offen: 9 nutzbar < erforderlich Mittel 13,6 (11,4–16,9): Ablöse/Mitbenutzung nötig | kritisch / offen: 9 nutzbar < erforderlich Mittel 13,6 (11,4–16,9): Ablöse/Mitbenutzung nötig | kritisch / offen: 9 nutzbar < erforderlich Mittel 13,6 (11,4–16,9): Ablöse/Mitbenutzung nötig | voraussichtlich ok: 21 nutzbar ≥ erforderlich bis 12,5 | zu prüfen: 13 nutzbar, erforderlich 9,7–14,3 (Mittel 11,6): Spanne der Bauaufsicht entscheidet | zu prüfen: 13 nutzbar, erforderlich 9,7–14,3 (Mittel 11,6): Spanne der Bauaufsicht entscheidet | zu prüfen: 13 nutzbar, erforderlich 9,7–14,3 (Mittel 11,6): Spanne der Bauaufsicht entscheidet | kritisch / offen: 9 nutzbar < erforderlich Mittel 14,8 (12,4–18,3): Ablöse/Mitbenutzung nötig |
| **Gewerbe im EG** | zu prüfen: EG 492 m² (B3: 576 m²); Gastraum ca. 281 m². | zu prüfen: EG 492 m² (B3: 576 m²); Gastraum ca. 281 m². | zu prüfen: EG 492 m² (B3: 576 m²); Gastraum ca. 281 m². | zu prüfen: EG 358 m² (B3: 576 m²); Gastraum ca. 198 m². | zu prüfen: EG 540 m² (B3: 576 m²); Gastraum ca. 232 m². | zu prüfen: EG 540 m² (B3: 576 m²); Gastraum ca. 232 m². | zu prüfen: EG 540 m² (B3: 576 m²); Gastraum ca. 232 m². | zu prüfen: EG 540 m² (B3: 576 m²); Gastraum ca. 307 m². |
| **Brandschutz / Feuerwehr** | zu prüfen: Vorbau über Stellplätzen/Fahrgasse, Aufstellflächen und Feuerwehrzufahrt, Rettungswege – Konzept erforderlich. | zu prüfen: Vorbau über Stellplätzen/Fahrgasse, Aufstellflächen und Feuerwehrzufahrt, Rettungswege – Konzept erforderlich. | zu prüfen: Vorbau über Stellplätzen/Fahrgasse, Aufstellflächen und Feuerwehrzufahrt, Rettungswege – Konzept erforderlich. | zu prüfen: Vorbau über Stellplätzen/Fahrgasse, Aufstellflächen und Feuerwehrzufahrt, Rettungswege – Konzept erforderlich. | zu prüfen: Vorbau über Stellplätzen/Fahrgasse, Aufstellflächen und Feuerwehrzufahrt, Rettungswege – Konzept erforderlich. | zu prüfen: Vorbau über Stellplätzen/Fahrgasse, Aufstellflächen und Feuerwehrzufahrt, Rettungswege – Konzept erforderlich. | zu prüfen: Vorbau über Stellplätzen/Fahrgasse, Aufstellflächen und Feuerwehrzufahrt, Rettungswege – Konzept erforderlich. | zu prüfen: Vorbau über Stellplätzen/Fahrgasse, Aufstellflächen und Feuerwehrzufahrt, Rettungswege – Konzept erforderlich. |

# Offene Fragen und Prüfbedarf

VERGLEICH · NICHT FESTGELEGT

Vor jeder Weiterentwicklung zu klären

• Fotos der städtischen Unterlagen (S. 13, 15, 16) in den Projektordner; daraus Grundstückszuschnitt, Baugrenzen, GRZ, Höhenbezugspunkt, Traufhöhe, Dachform, Abstände, Festsetzungen zu Stellplätzen/Zufahrten.
• Bebauungsplan-Stand: Entwurf (S. 15) – rechtskräftige Fassung; örtliche Bauvorschrift/Stellplatzsatzung für Nicht-Wohnungen; städtebaulicher Vertrag/Kaufvertrag (Stellplätze auch für Wohnungen möglich).
• Einstufung der Gaststätte („örtliche“ oder „überörtliche Bedeutung“), Sitzplatzzahl innen/außen, Büro mit/ohne Besucherverkehr.
• Höhenbezug der 12,00 m; Vollgeschoss-Definition für das 2. OG; Traufhöhe 6,50 m.
• Überbauung des Platzes (F1–F3: 1,5 m), Grenz- und Abstandsflächen, GRZ-Anrechnung überdeckter Stellplätze.
• Zufahrt: Straße, Gefälle, Sichtdreiecke; Feuerwehrzufahrt/Aufstellflächen unter dem Vorbau; Wendemöglichkeit in der Sackgasse (F1–F3).
• Stellplatzmaße/Garagenverordnung für Stellplätze neben Säulen und Parallelparker; Schleppkurven.
• Statik: Kragarme 1,0–5,0 m, Säulenraster 5,4 m, Fundamente; Brandschutz Vorbau.

Keine Variante ist ausgewählt.