Neue Mitte Werlte – Baufeld 3 – Variante B2 – 540 m² EG, Vorbau, Staffel 1,50 m

VORLÄUFIGER ENTWURF – NICHT GENEHMIGT – technische Zeichnungen für PDF-Import, keine Präsentation, keine Genehmigungsunterlage

Beschreibung

Neue Idee: EG 18,00 m (Platzseite) × 30,00 m = 540 m² (Hypothese, Grundstück 32 × 30 m = 960 m² unbestätigt, Rest 420 m²); OG1 kragt 1,00 m West, 1,50 m Platzseite, 5,00 m Ost (über Stellplätze) aus, rückseitig bündig (Grundstücksgrenze der Hypothese); oberstes Geschoss 1,50 m hinter der Außenkante des 1. OG zurückgesetzt (rundum).
Datenquelle: studie/varianten_f.py F2 (Planungsziel 24.10.2026)

Maße und Kennwerte

EG-Außenmaß 18,00 × 30,00 m = 540,0 m²
1. Obergeschoss (OG1): Umriss 24,00 × 31,50 m, Fläche 756,0 m²
2. Obergeschoss (oberstes Geschoss) – Staffel 1,50 m: Umriss 21,00 × 28,50 m, Fläche 598,5 m²
Höhen über ±0,00: OK FFB 1. OG +4,30; OK FFB oberstes Geschoss +7,90; OK Dach +11,50; OK Attika +12,00 m
Höhenstatus: HYPOTHETISCH (Höhenschema EG 4,30 / 1. OG 3,60 / oberstes Geschoss 3,60 / Attika 0,50 = 12,00 m aus varianten_e.py) – NICHT gesichert, nicht verbindlich
Decken: ANNAHME 0,45 m (Wert aus varianten_e.py DECKE)
Außenwand: Darstellung als Doppellinie 0,30 m = ANNAHME (Wandstärke NOCH OFFEN)
Säulen: 18 Stück, Ø 0,40 m (Annahme des Entwurfs)

Maßstab / Bezug

Alle Blätter 1:100 auf A2 quer. Maßstabsbalken unten: 10,00 m = 100 mm auf dem Blatt. Maße in Metern.
Grundrisse: x = West→Ost, y = von der Platzseite (unten) zur Rückseite (oben). Nordrichtung NOCH OFFEN.
Bezugshöhe ±0,00 = OK Fertigfußboden Erdgeschoss; Bezug zur OK Fahrbahn der Stadt NOCH OFFEN.

Blattverzeichnis

Blatt 1: Übersichtsblatt
Blatt 2: Grundriss Erdgeschoss (EG) – OK Fertigfußboden ±0,00 m (Höhenbezug ANNAHME)
Blatt 3: Grundriss 1. Obergeschoss (OG1) – OK Fertigfußboden +4,30 m (Höhenbezug ANNAHME)
Blatt 4: Grundriss 2. Obergeschoss (oberstes Geschoss) – Staffel 1,50 m – OK Fertigfußboden +7,90 m (Höhenbezug ANNAHME)
Blatt 5: Vorderansicht
Blatt 6: Rückansicht
Blatt 7: Westansicht
Blatt 8: Ostansicht
Blatt 9: Schnitt A–A mit Höhenkoten
Blatt 10: Stellplätze / Erschließung (getrennt)
Blatt 11: Rechtsebenen und offene Punkte
Blatt 12: Konsistenzprotokoll
Blätter 1–10 sind Zeichnungen (Vektor); Blätter 11–12 sind reine Textblätter (für den Import-Test entbehrlich).

Konsistenz (Kurzfassung)

[KONFLIKT] OG1: Geschoss ragt über die Hypothese-Grundstücksgrenze 32 × 30 m hinaus (x 0,00…24,00, y -1,50…30,00) – Grenze zum Platz/Baulinie NOCH OFFEN
[KONFLIKT] Vorbau (OG1-Kante minus EG-Wand) West/Platz/Ost/Rück = 1,00 / 1,50 / 5,00 / 0,00 m – Vorgabe 'umlaufend auf allen vier Seiten' ist rückseitig NICHT erfüllt (Grundstücksgrenze der Hypothese bei y = 30)
[KONFLIKT] Säulen (23.65, 29.3) und (23.65, 29.65) liegen nur 0,35 m auseinander (Ø 0,40 m, Säulen berühren/überschneiden sich)
[KONFLIKT] 6 Säulen stehen außerhalb der Hypothese-Grundstücksgrenze (y < 0 bzw. x < 0), z. B. (0.35, -1.15)
[KONFLIKT] Kern: EG-Kern x 1–5 / y 0–9,5 m; Entwurf nennt für die Obergeschosse einen Kern-Streifen y –1,5…2,5 m über die volle Breite – Treppe/Aufzug im OG liegen nicht über dem EG-Kern; Lage NOCH OFFEN, im OG-Plan nicht gezeichnet
Vollständiges Protokoll: letztes Blatt.

Legende (Linienarten)

- Außenwand (Doppellinie, grau gefüllt)
- Raumgrenze (dünn, grau)
- Säule Ø 0,40 m (voll)
- Fenster/Verglasung (3 Linien in der Wand)
- Tür (Linie in der Wandöffnung, ohne Anschlag)
- Maßlinie mit Schrägstrich (blau)
- Umriss darunterliegendes Geschoss / überdeckend
- Schnittlinie A–A
- Grundstücksgrenze HYPOTHESE (rot gestrichelt)
- Geschnittenes Bauteil (Schnitt, schwarz)

0 m — 5 m — 10 m
Maßstabsbalken 1:100 (10 m = 100 mm Blattmaß)

PROJEKT
Neue Mitte Werlte – Baufeld 3

VARIANTE
Variante B2 – 540 m² EG, Vorbau, Staffel 1,50 m

ZEICHNUNG
Übersichtsblatt

MASSSTAB
1:100 (Blattgröße A2 quer)

DATUM
27.10.2026

BLATT
1 / 12 – Übersichtsblatt

HÖHEN
HYPOTHETISCH (Höhenschema EG 4,30 / 1. OG 3,60 / oberstes Geschoss 3,60 / Attika 0,50 = 12,00 m aus varianten_e.py) – NICHT gesichert, nicht verbindlich

STATUS
VORLÄUFIGER ENTWURF – NICHT GENEHMIGT

ANMERKUNGEN
Maße in m.
Höhen: HYPOTHETISCH (Höhenschema EG 4,30 / 1. OG 3,60 / oberstes Geschoss 3,60 / Attika 0,50 = 12,00 m aus varianten_e.py) – NICHT gesichert, nicht verbindlich

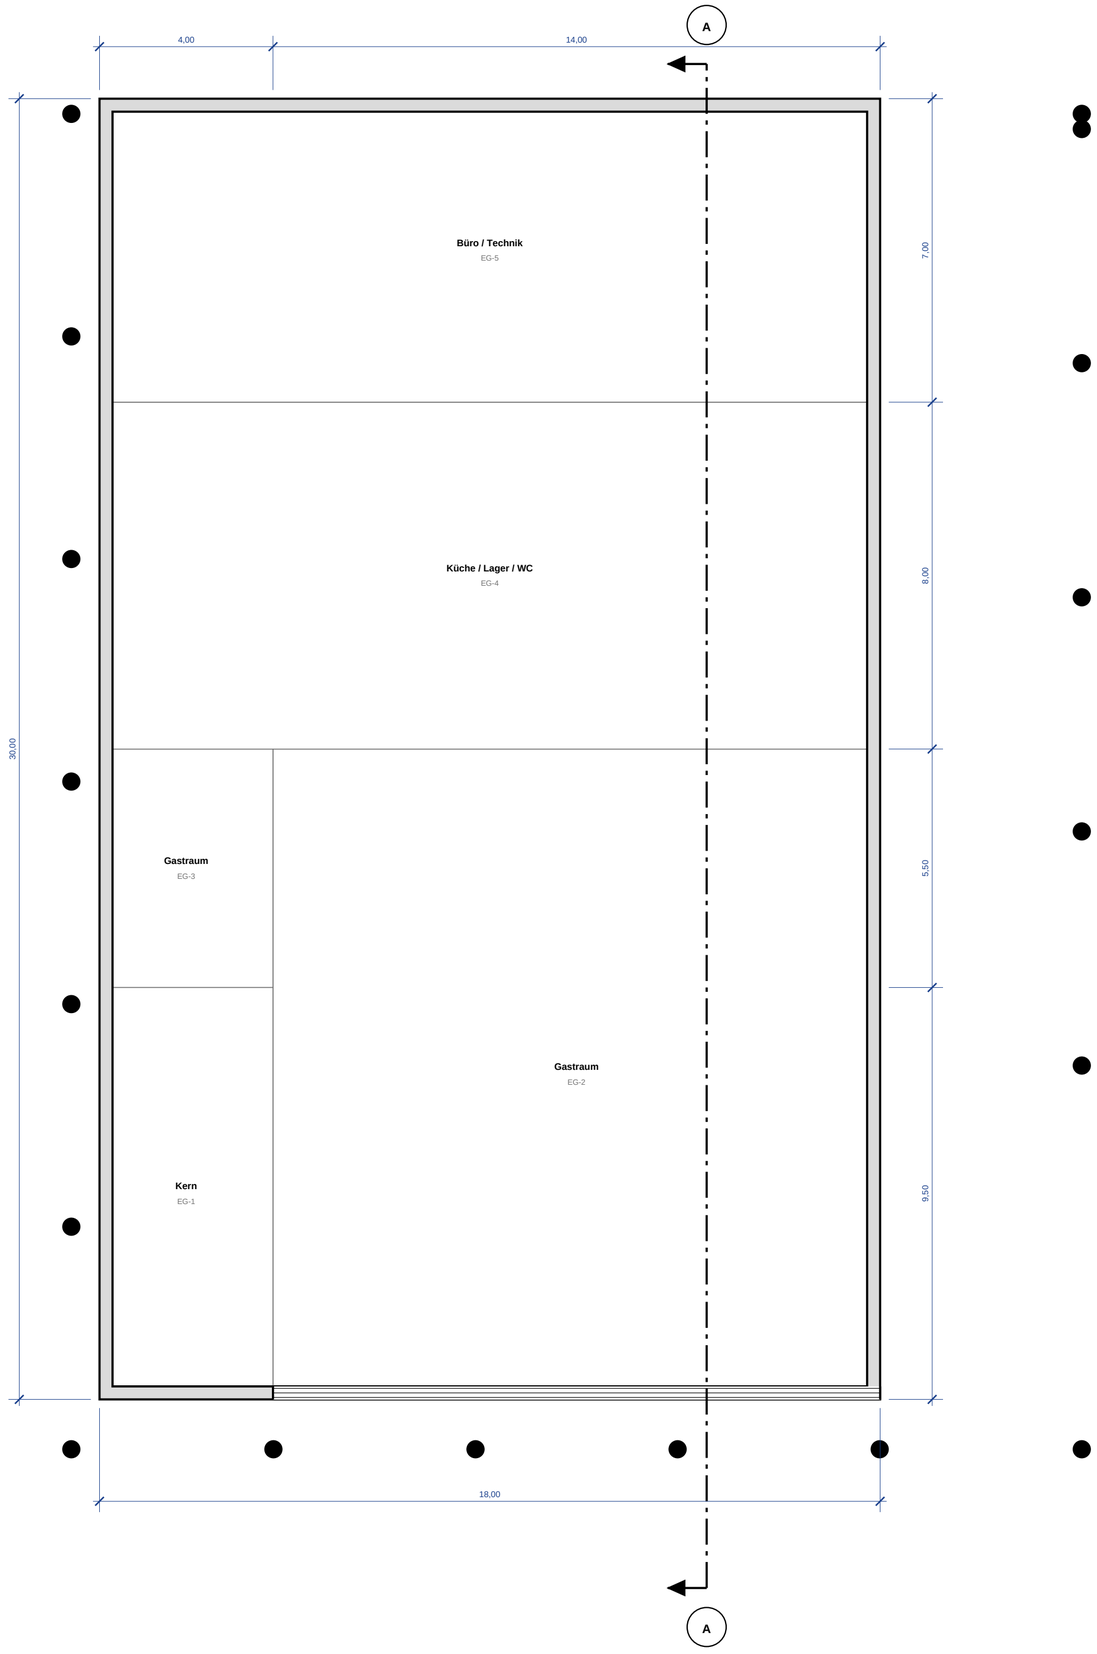

PROJEKT

Neue Mitte Werlte – Baufeld 3

VARIANTE

Variante B2 – 540 m² EG, Vorbau, Staffel 1,50 m

ZEICHNUNG

Grundriss Erdgeschoss (EG) – OK Fertigfußboden ±0,00 m (Höhenbezug ANNAHME)

MASSSTAB

1:100 (Blattgröße A2 quer)

DATUM

27.10.2026

BLATT

2 / 12 – Grundriss Erdgeschoss (EG) – OK Fertigfußboden ±0,00 m (Höhenbezug ANNAHME)

HÖHEN

HYPOTHETISCH (Höhenschema EG 4,30 / 1. OG 3,60 / oberstes Geschoss 3,60 / Attika 0,50 = 12,00 m aus varianten_e.py) – NICHT gesichert, nicht verbindlich

STATUS

VORLÄUFIGER ENTWURF – NICHT GENEHMIGT

ANMERKUNGEN

Wandstärke 0,30 m = ANNAHME (Darstellung).

Innentüren und Türanschläge NOCH OFFEN – nicht gezeichnet.

Maße in m. Maßketten blau, Bauteilkanten schwarz.

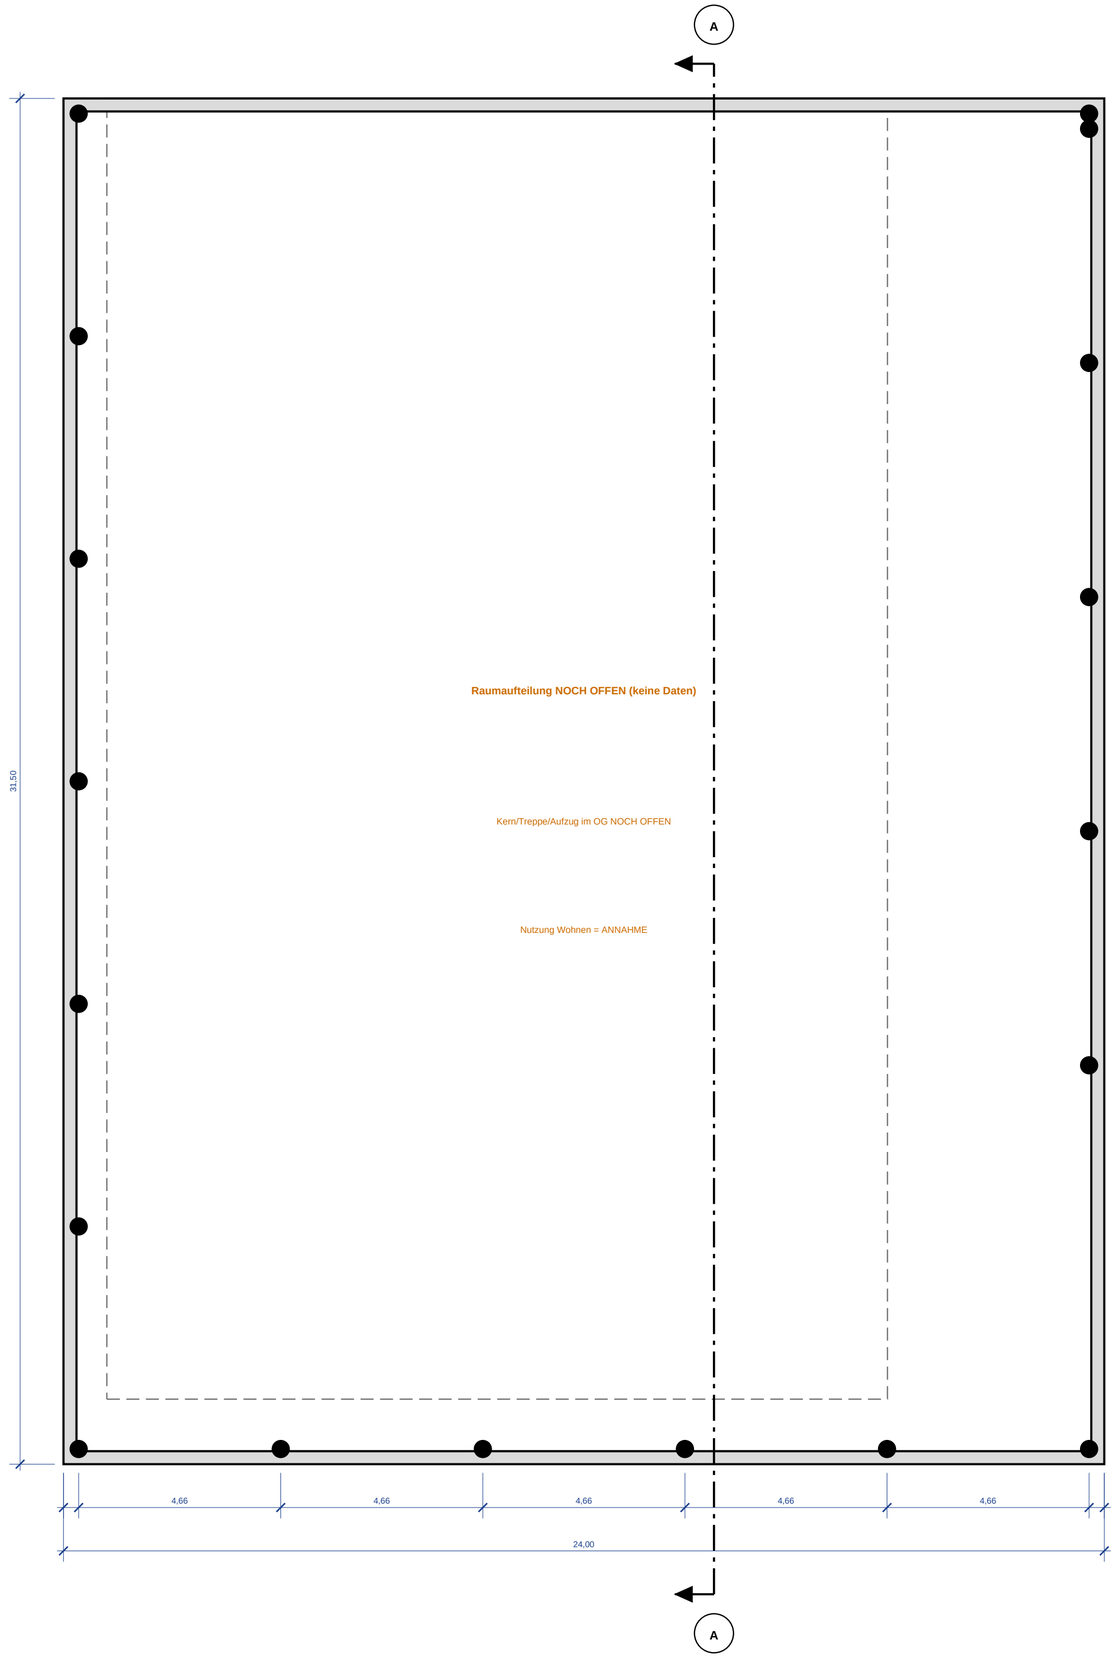

PROJEKT

Neue Mitte Werlte – Baufeld 3

VARIANTE

Variante B2 – 540 m² EG, Vorbau, Staffel 1,50 m

ZEICHNUNG

Grundriss 1. Obergeschoss (OG1) – OK Fertigfußboden +4,30 m (Höhenbezug ANNAHME)

MASSSTAB

1:100 (Blattgröße A2 quer)

DATUM

27.10.2026

BLATT

3 / 12 – Grundriss 1. Obergeschoss (OG1) – OK Fertigfußboden +4,30 m (Höhenbezug ANNAHME)

HÖHEN

HYPOTHETISCH (Höhenschema EG 4,30 / 1. OG 3,60 / oberstes Geschoss 3,60 / Attika 0,50 = 12,00 m aus varianten_e.py) – NICHT gesichert, nicht verbindlich

STATUS

VORLÄUFIGER ENTWURF – NICHT GENEHMIGT

ANMERKUNGEN

Wandstärke 0,30 m = ANNAHME (Darstellung).

Innentüren und Türanschläge NOCH OFFEN – nicht gezeichnet.

Maße in m. Maßketten blau, Bauteilkanten schwarz.

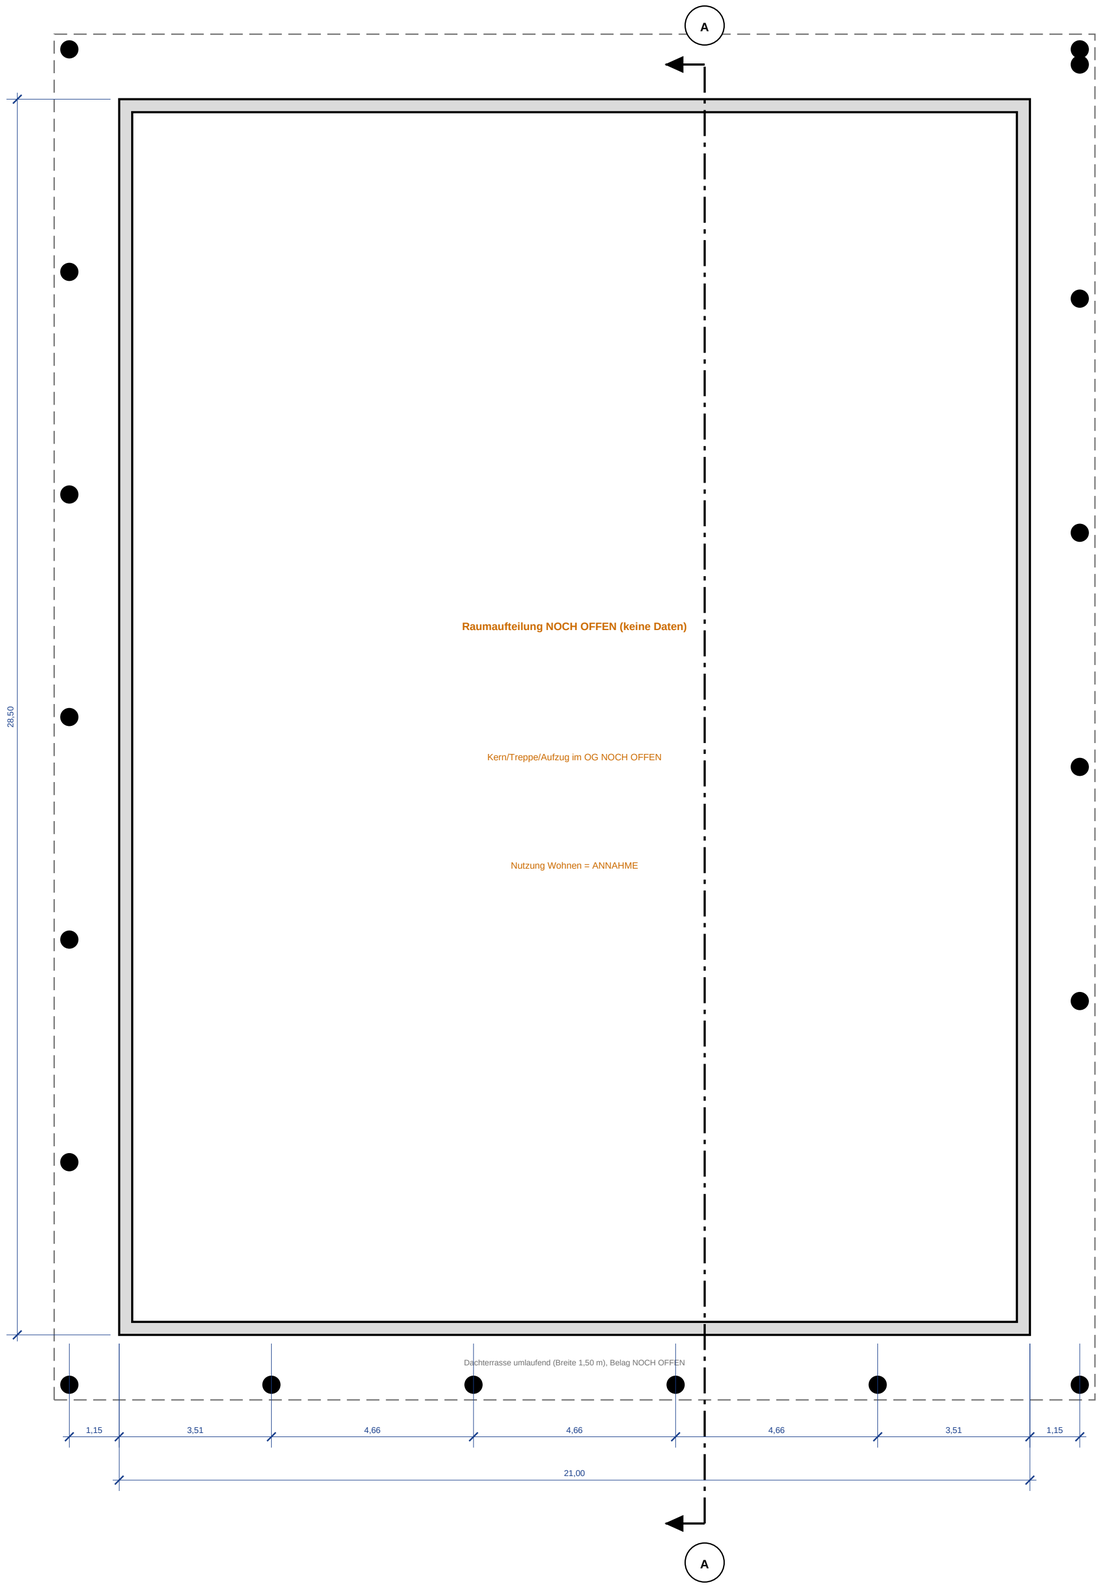

PROJEKT

Neue Mitte Werlte – Baufeld 3

VARIANTE

Variante B2 – 540 m² EG, Vorbau, Staffel 1,50 m

ZEICHNUNG

Grundriss 2. Obergeschoss (oberstes Geschoss) – Staffel 1,50 m – OK Fertigfußboden +7,90 m (Höhenbezug ANNAHME)

MASSSTAB

1:100 (Blattgröße A2 quer)

DATUM

27.10.2026

BLATT

4 / 12 – Grundriss 2. Obergeschoss (oberstes Geschoss) – Staffel 1,50 m – OK Fertigfußboden +7,90 m (Höhenbezug ANNAHME)

HÖHEN

HYPOTHETISCH (Höhenschema EG 4,30 / 1. OG 3,60 / oberstes Geschoss 3,60 / Attika 0,50 = 12,00 m aus varianten_e.py) – NICHT gesichert, nicht verbindlich

STATUS

VORLÄUFIGER ENTWURF – NICHT GENEHMIGT

ANMERKUNGEN

Wandstärke 0,30 m = ANNAHME (Darstellung).

Innentüren und Türanschläge NOCH OFFEN – nicht gezeichnet.

Maße in m. Maßketten blau, Bauteilkanten schwarz.

Vorderansicht (Platzseite, Blick von Platz)

Geschosshöhen: HYPOTHETISCH (Höhenschema EG 4,30 / 1. OG 3,60 / oberstes Geschoss 3,60 / Attika 0,50 = 12,00 m aus varianten_e.py) – NICHT gesichert, nicht verbindlich

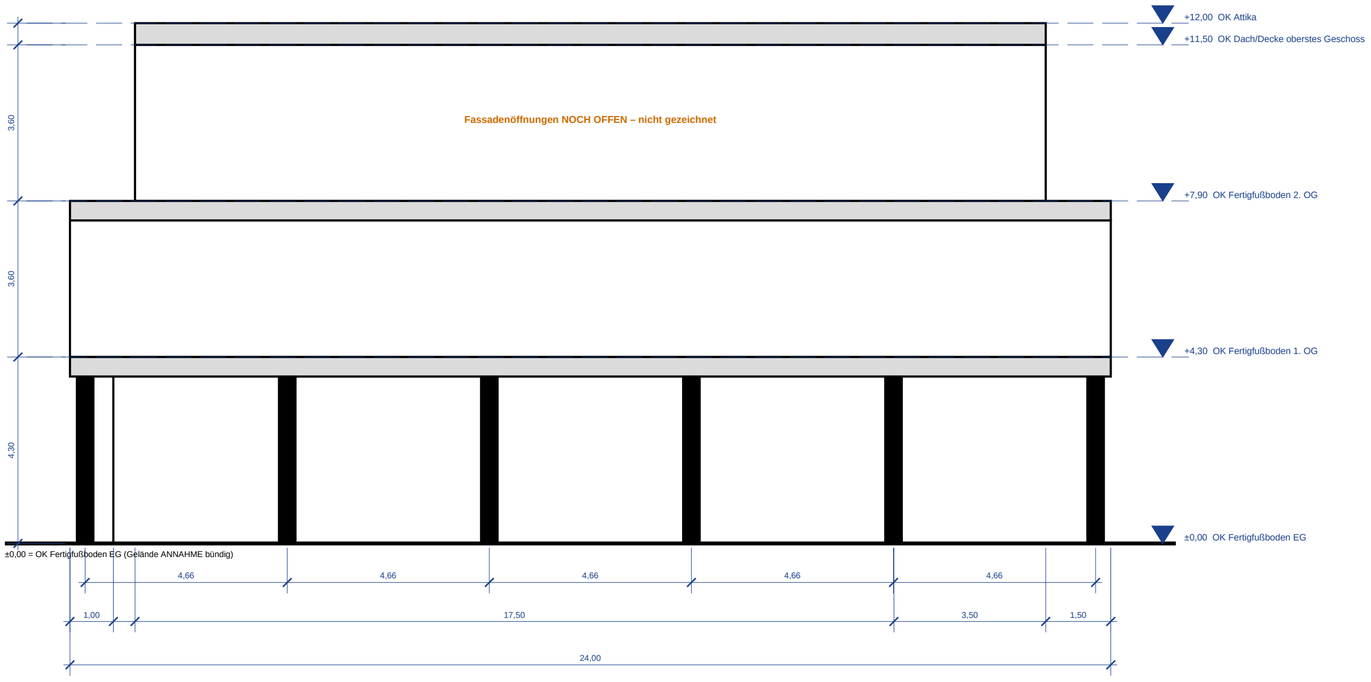

PROJEKT
Neue Mitte Werlte – Baufeld 3

VARIANTE
Variante B2 – 540 m² EG, Vorbau, Staffel 1,50 m

ZEICHNUNG
Vorderansicht

MASSSTAB
1:100 (Blattgröße A2 quer)

DATUM
27.10.2026

BLATT
5 / 12 – Vorderansicht

HÖHEN
HYPOTHETISCH (Höhenschema EG 4,30 / 1. OG 3,60 / oberstes Geschoss 3,60 / Attika 0,50 = 12,00 m aus varianten_e.py) – NICHT gesichert, nicht verbindlich

STATUS
VORLÄUFIGER ENTWURF – NICHT GENEHMIGT

ANMERKUNGEN
Maße in m.

Höhen: HYPOTHETISCH (Höhenschema EG 4,30 / 1. OG 3,60 / oberstes Geschoss 3,60 / Attika 0,50 = 12,00 m aus varianten_e.py) – NICHT gesichert, nicht verbindlich

Fassadenöffnungen von B1–B3: keine Daten – nicht gezeichnet.

Rückansicht (Blick von der Rückseite)

Geschosshöhen: HYPOTHETISCH (Höhenschema EG 4,30 / 1. OG 3,60 / oberstes Geschoss 3,60 / Attika 0,50 = 12,00 m aus varianten_e.py) – NICHT gesichert, nicht verbindlich

PROJEKT
Neue Mitte Werlte – Baufeld 3

VARIANTE
Variante B2 – 540 m² EG, Vorbau, Staffel 1,50 m

ZEICHNUNG
Rückansicht

MASSSTAB
1:100 (Blattgröße A2 quer)

DATUM
27.10.2026

BLATT
6 / 12 – Rückansicht

HÖHEN
HYPOTHETISCH (Höhenschema EG 4,30 / 1. OG 3,60 / oberstes Geschoss 3,60 / Attika 0,50 = 12,00 m aus varianten_e.py) – NICHT gesichert, nicht verbindlich

STATUS
VORLÄUFIGER ENTWURF – NICHT GENEHMIGT

ANMERKUNGEN
Maße in m.

Höhen: HYPOTHETISCH (Höhenschema EG 4,30 / 1. OG 3,60 / oberstes Geschoss 3,60 / Attika 0,50 = 12,00 m aus varianten_e.py) – NICHT gesichert, nicht verbindlich

Fassadenöffnungen von B1–B3: keine Daten – nicht gezeichnet.

Westansicht (Seite x = 0; Nordrichtung NOCH OFFEN)

Geschosshöhen: HYPOTHETISCH (Höhenschema EG 4,30 / 1. OG 3,60 / oberstes Geschoss 3,60 / Attika 0,50 = 12,00 m aus varianten_e.py) – NICHT gesichert, nicht verbindlich

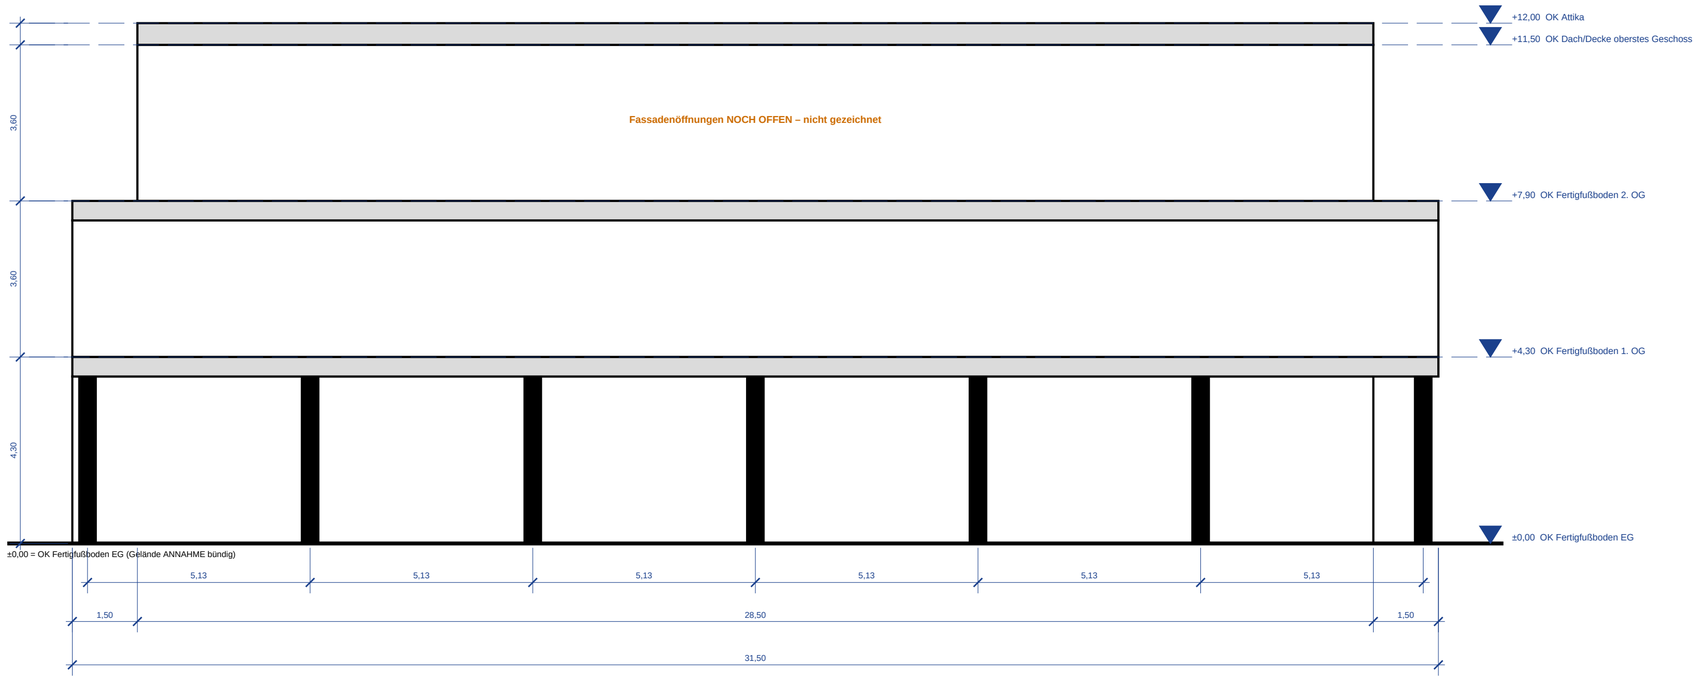

PROJEKT
Neue Mitte Werlte – Baufeld 3

VARIANTE
Variante B2 – 540 m² EG, Vorbau, Staffel 1,50 m

ZEICHNUNG
Westansicht

MASSSTAB
1:100 (Blattgröße A2 quer)

DATUM
27.10.2026

BLATT
7 / 12 – Westansicht

HÖHEN
HYPOTHETISCH (Höhenschema EG 4,30 / 1. OG 3,60 / oberstes Geschoss 3,60 / Attika 0,50 = 12,00 m aus varianten_e.py) – NICHT gesichert, nicht verbindlich

STATUS
VORLÄUFIGER ENTWURF – NICHT GENEHMIGT

ANMERKUNGEN
Maße in m.

Höhen: HYPOTHETISCH (Höhenschema EG 4,30 / 1. OG 3,60 / oberstes Geschoss 3,60 / Attika 0,50 = 12,00 m aus varianten_e.py) – NICHT gesichert, nicht verbindlich

Fassadenöffnungen von B1–B3: keine Daten – nicht gezeichnet.

Ostansicht (Seite Ost; Nordrichtung NOCH OFFEN)

Geschosshöhen: HYPOTHETISCH (Höhenschema EG 4,30 / 1. OG 3,60 / oberstes Geschoss 3,60 / Attika 0,50 = 12,00 m aus varianten_e.py) – NICHT gesichert, nicht verbindlich

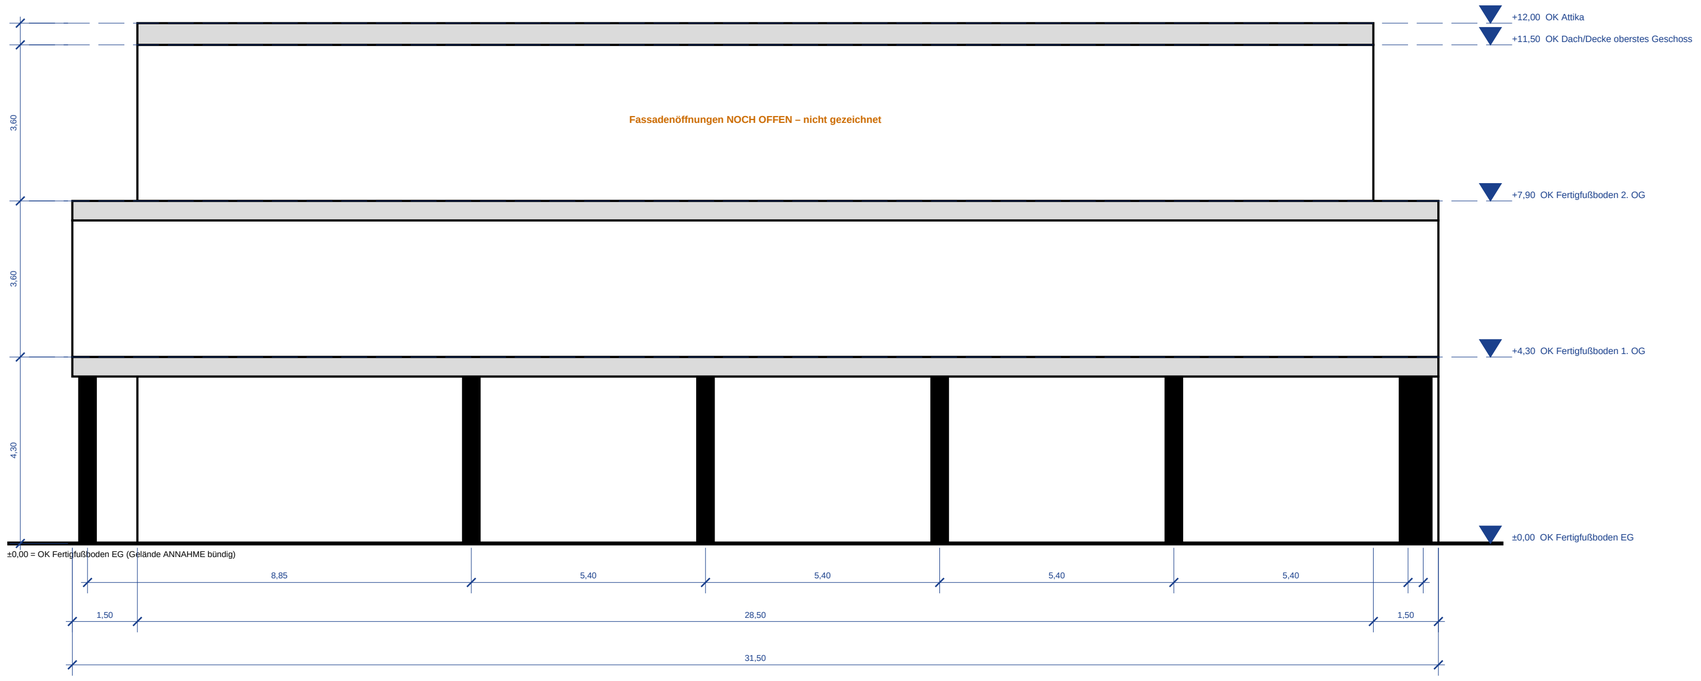

PROJEKT
Neue Mitte Werlte – Baufeld 3

VARIANTE
Variante B2 – 540 m² EG, Vorbau, Staffel 1,50 m

ZEICHNUNG
Ostansicht

MASSSTAB
1:100 (Blattgröße A2 quer)

DATUM
27.10.2026

BLATT
8 / 12 – Ostansicht

HÖHEN
HYPOTHETISCH (Höhenschema EG 4,30 / 1. OG 3,60 / oberstes Geschoss 3,60 / Attika 0,50 = 12,00 m aus varianten_e.py) – NICHT gesichert, nicht verbindlich

STATUS
VORLÄUFIGER ENTWURF – NICHT GENEHMIGT

ANMERKUNGEN
Maße in m.

Höhen: HYPOTHETISCH (Höhenschema EG 4,30 / 1. OG 3,60 / oberstes Geschoss 3,60 / Attika 0,50 = 12,00 m aus varianten_e.py) – NICHT gesichert, nicht verbindlich

Fassadenöffnungen von B1–B3: keine Daten – nicht gezeichnet.

Schnitt A–A (Schnittlinie x = 15,00 m, Blick nach Westen; Platzseite links)

Geschossdecken ANNAHME 0,45 m (Wert aus varianten_e.py DECKE); Höhen: HYPOTHETISCH (Höhenschema EG 4,30 / 1. OG 3,60 / oberstes Geschoss 3,60 / Attika 0,50 = 12,00 m aus varianten_e.py) – NICHT gesichert, nicht verbindlich

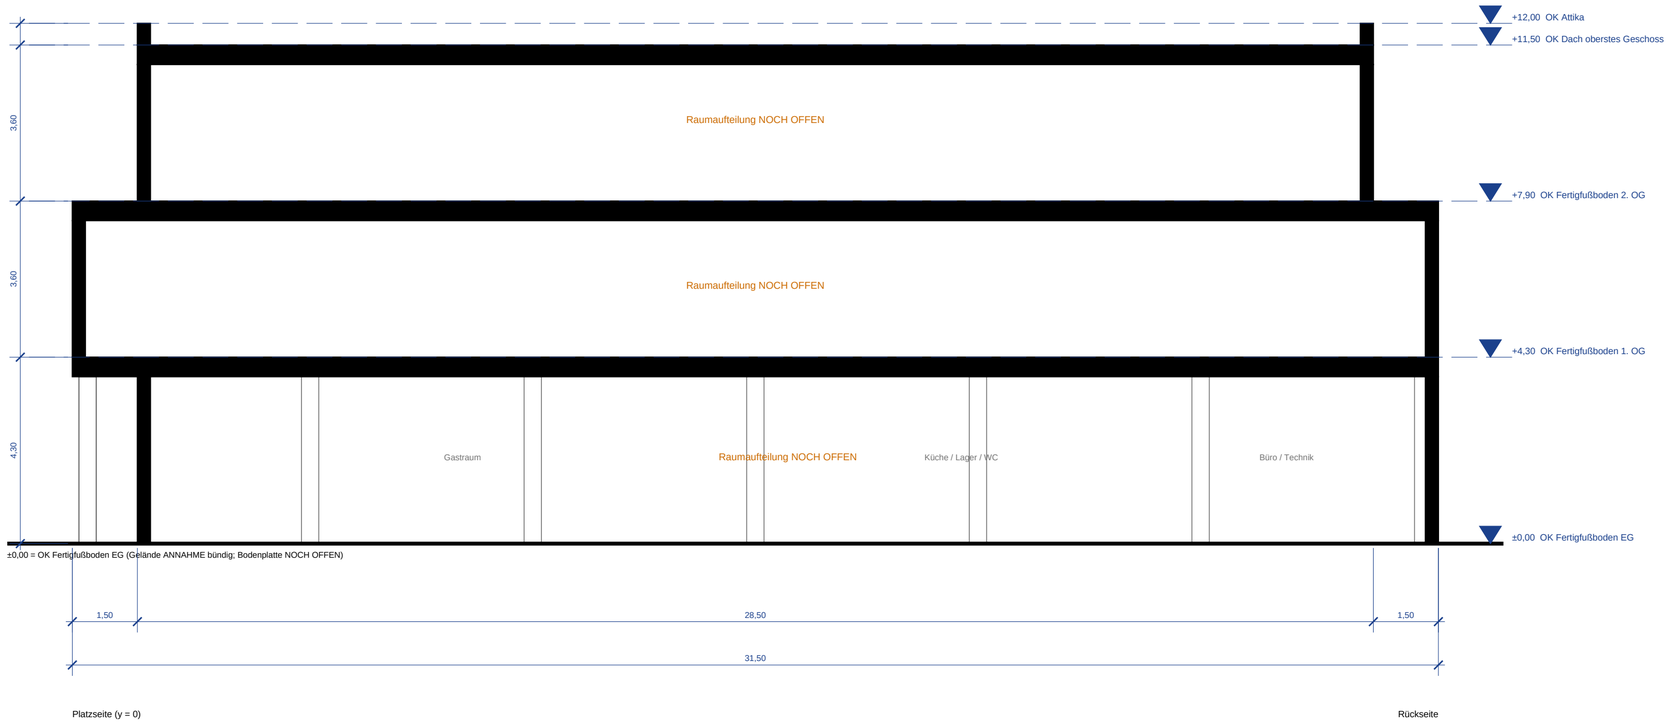

PROJEKT
Neue Mitte Werlte – Baufeld 3

VARIANTE
Variante B2 – 540 m² EG, Vorbau, Staffel 1,50 m

ZEICHNUNG
Schnitt A–A mit Höhenkoten

MASSSTAB
1:100 (Blattgröße A2 quer)

DATUM
27.10.2026

BLATT
9 / 12 – Schnitt A–A mit Höhenkoten

HÖHEN
HYPOTHETISCH (Höhenschema EG 4,30 / 1. OG 3,60 / oberstes Geschoss 3,60 / Attika 0,50 = 12,00 m aus varianten_e.py) – NICHT gesichert, nicht verbindlich

STATUS
VORLÄUFIGER ENTWURF – NICHT GENEHMIGT

ANMERKUNGEN
Maße in m.

Höhen: HYPOTHETISCH (Höhenschema EG 4,30 / 1. OG 3,60 / oberstes Geschoss 3,60 / Attika 0,50 = 12,00 m aus varianten_e.py) – NICHT gesichert, nicht verbindlich

Fassadenöffnungen von B1–B3: keine Daten – nicht gezeichnet.

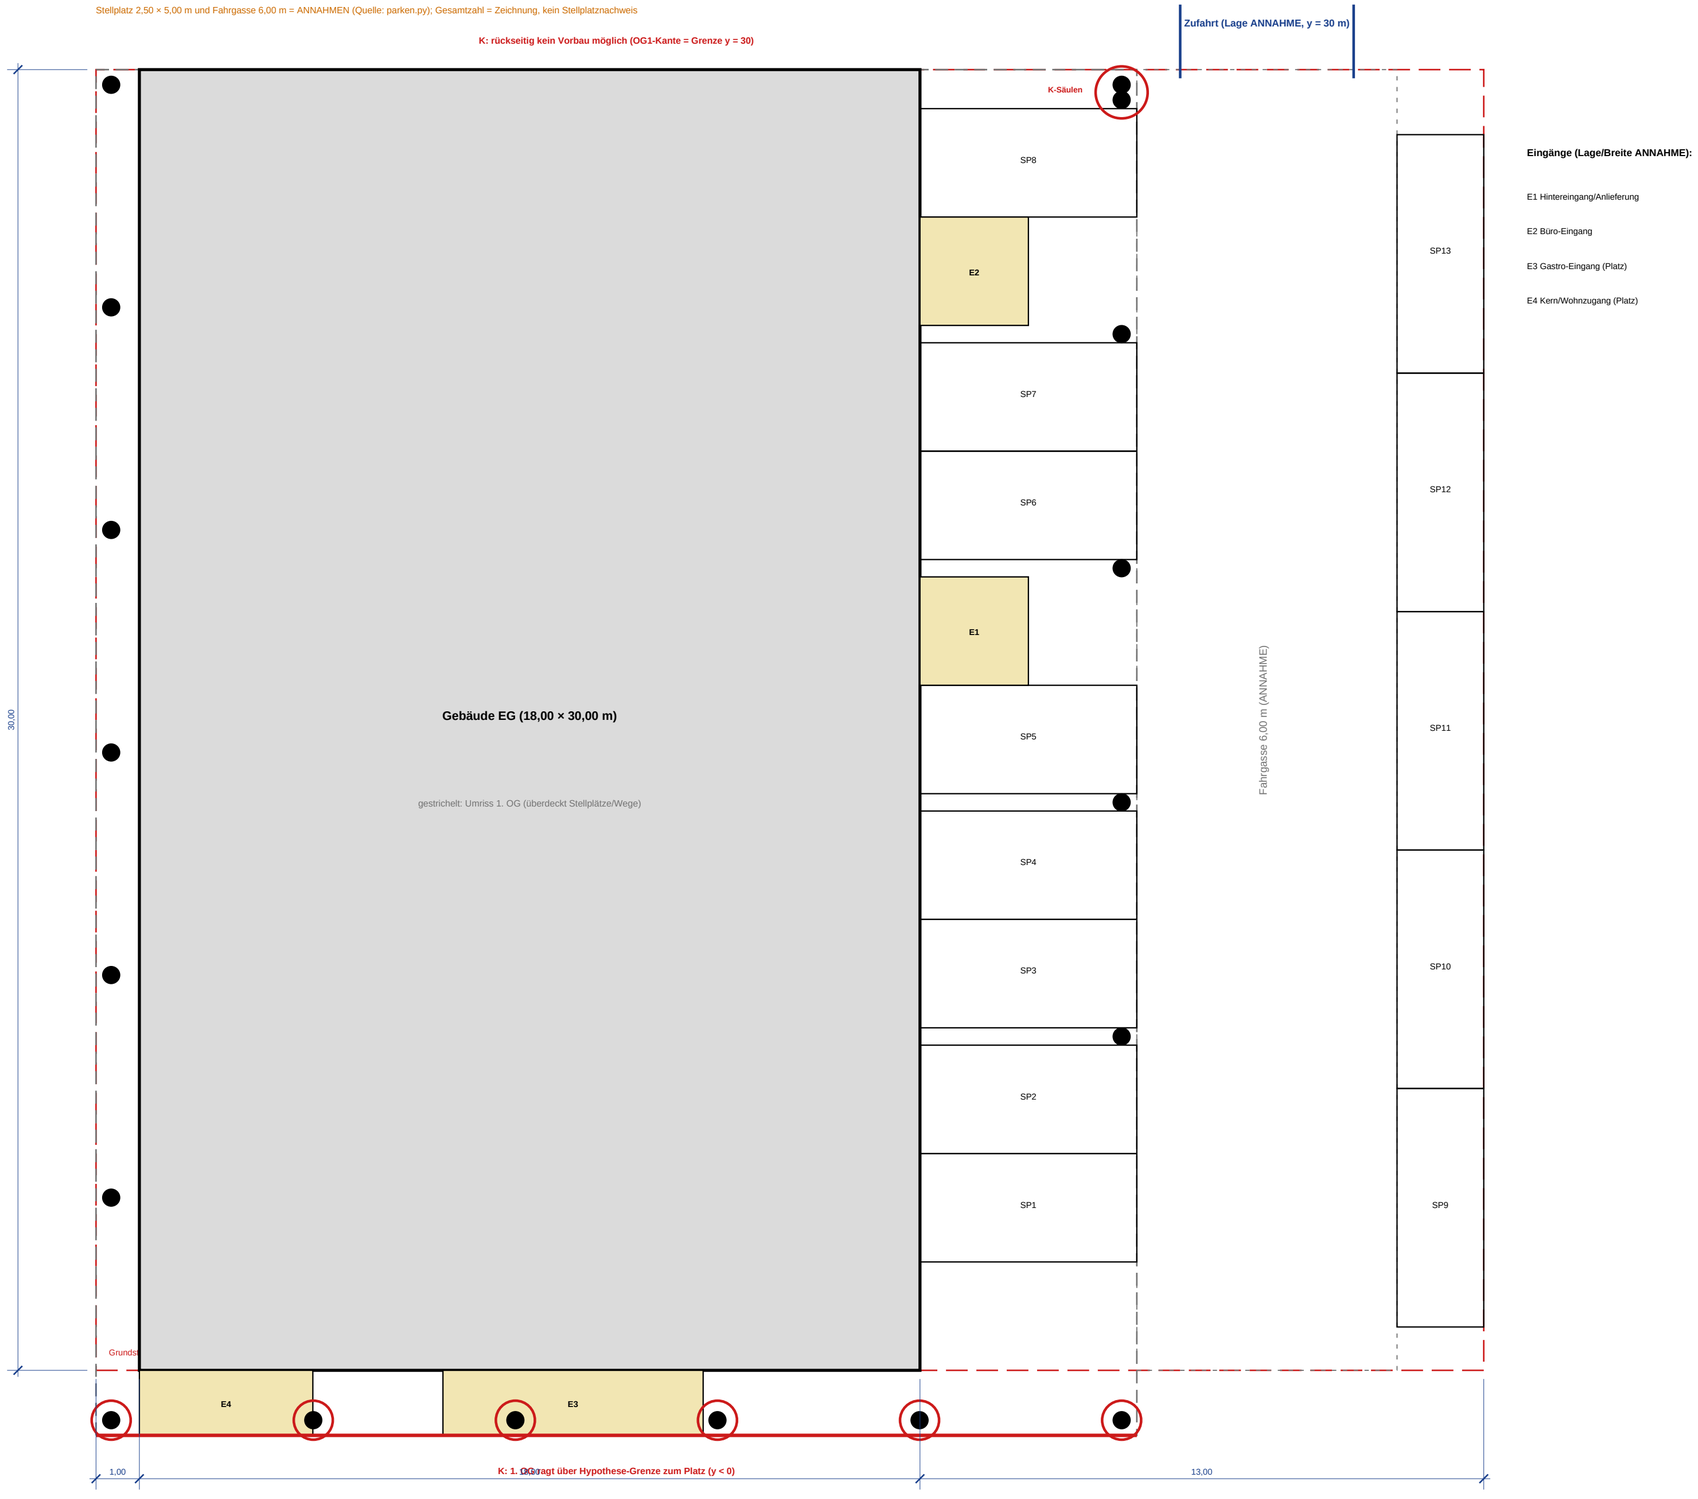

Eingänge (Lage/Breite ANNAHME):

E1 Hintereingang/Anlieferung

E2 Büro-Eingang

E3 Gastro-Eingang (Platz)

E4 Kern/Wohnzugang (Platz)

PROJEKT
Neue Mitte Werlte – Baufeld 3

VARIANTE
Variante B2 – 540 m² EG, Vorbau, Staffel 1,50 m

ZEICHNUNG
Stellplätze / Erschließung (getrennt)

MASSSTAB
1:100 (Blattgröße A2 quer)

DATUM
27.10.2026

BLATT
10 / 12 – Stellplätze / Erschließung (getrennt)

HÖHEN
HYPOTHETISCH (Höhenschema EG 4,30 / 1. OG 3,60 / oberstes Geschoss 3,60 / Attika 0,50 = 12,00 m aus varianten_e.py) – NICHT gesichert, nicht verbindlich

STATUS
VORLÄUFIGER ENTWURF – NICHT GENEHMIGT

ANMERKUNGEN
Maße in m.

Höhen: HYPOTHETISCH (Höhenschema EG 4,30 / 1. OG 3,60 / oberstes Geschoss 3,60 / Attika 0,50 = 12,00 m aus varianten_e.py) – NICHT gesichert, nicht verbindlich

Rechtsebenen und Datenstände – getrennt zu lesen (keine Aussage zur Zulässigkeit)

EBENE 1 – Alter B3-Geometriestand (Modell v4, Planstand Blatt 14): in diesem PDF NICHT verwendet; nur als Vergleich im Paket A.
EBENE 2 – Neue Entwurfsannahmen (Planungsziel 24.10.2026: EG 18 × 30 m = 540 m², Vorbau, Säulen, Zielhöhe 12,00 m nicht bindend): in DIESEM PDF verwendet (varianten_f.py); alle Werte sind Entwurfsannahmen.
EBENE 3 – B-Plan Nr. 123 (14.04.2023, rechtskräftig, wahrscheinlich MI 3 / Flurstück 59/1): MI 3 – II bis III Vollgeschosse, GRZ 0,6, Traufhöhe 9,80 m, Gebäudehöhe 15,00 m, Sockel 0,30 m; Hauptdach ≥ 38° (Flachdach nur untergeordnet); Höhenbezug OK Fahrbahn. Zuordnung Baufeld 3 = MI 3 ist NICHT bestätigt.
EBENE 4 – Änderungsentwurf 2026 (kein Beschluss, nicht rechtskräftig): II Vollgeschosse zwingend, Traufhöhe 6,50 m, Gebäudehöhe 12,00 m; erfasst MI 3 nach vorliegendem Stand nicht.
EBENE 5 – Offener Höhenbezug: ±0,00 = OK Fertigfußboden EG ist eine Zeichnungsannahme; Anbindung an OK Fahrbahn und Gelände NOCH OFFEN. Geschosshöhen dieses PDFs: HYPOTHETISCH (Höhenschema EG 4,30 / 1. OG 3,60 / oberstes Geschoss 3,60 / Attika 0,50 = 12,00 m aus varianten_e.py) – NICHT gesichert, nicht verbindlich.
Die Zeichnungen enthalten KEINE Aussage, ob eine Variante baurechtlich zulässig ist; kein Geschossvergleich mit den Ebenen 3 und 4 wurde als Ergebnis eingetragen.

Nicht gesichert / NOCH OFFEN in diesem PDF

- Wandstärken (0,30 m Darstellung ANNAHME)
- Deckenstärken (0,45 m ANNAHME)
- Fenster, Türen, Brüstungen: keine Daten – nicht gezeichnet (nur Glasfront-Lage Gastro aus dem Entwurf als ANNAHME)
- Innenaufteilung 1. OG und oberstes Geschoss (Wohnen/Kern) – keine Raumdaten
- Treppen-/Aufzugslage im OG (Kern-Streifen laut Entwurf widerspricht der EG-Kernlage, siehe Konsistenzprotokoll)
- Geschosshöhen (hypothetisch) und Höhenbezug
- Grundstückszuschnitt (Hypothese 32 × 30 m), Lage von Zufahrt/Straße
- Rückseitiger Vorbau: auf der Hypothese-Grenze nicht möglich (0,00 m)
- Stellplatzmaß 2,50 × 5,00 m und Fahrgasse 6,00 m sind Annahmen

PROJEKT
Neue Mitte Werlte – Baufeld 3

VARIANTE
Variante B2 – 540 m² EG, Vorbau, Staffel 1,50 m

ZEICHNUNG
Rechtsebenen und offene Punkte

MASSSTAB
1:100 (Blattgröße A2 quer)

DATUM
27.10.2026

BLATT
11 / 12 – Rechtsebenen und offene Punkte

HÖHEN
HYPOTHETISCH (Höhenschema EG 4,30 / 1. OG 3,60 / oberstes Geschoss 3,60 / Attika 0,50 = 12,00 m aus varianten_e.py) – NICHT gesichert, nicht verbindlich

STATUS
VORLÄUFIGER ENTWURF – NICHT GENEHMIGT

ANMERKUNGEN
Maße in m.
Höhen: HYPOTHETISCH (Höhenschema EG 4,30 / 1. OG 3,60 / oberstes Geschoss 3,60 / Attika 0,50 = 12,00 m aus varianten_e.py) – NICHT gesichert, nicht verbindlich

Konsistenzprotokoll (automatisch aus dem gemeinsamen Modell; Widersprüche sind dokumentiert, NICHT stillschweigend korrigiert)

[OK] EG-Außenmaß 18,00 × 30,00 m = 540 m² (Vorgabe 18 × 30 = 540 m²)
[HINWEIS] Restfläche Grundstück (Hypothese 960 m²): 420 m² – 960 m² Grundstück ist NICHT bestätigt
[KONFLIKT] OG1: Geschoss ragt über die Hypothese-Grundstücksgrenze 32 × 30 m hinaus (x 0,00…24,00, y -1,50…30,00) – Grenze zum Platz/Baulinie NOCH OFFEN
[OK] Höhenfolge +0,00 < +4,30 < +7,90 < +11,50 < +12,00 m
[HINWEIS] Gesamthöhe Attika-OK 12,00 m über ±0,00 (OK FFB EG); Bezug zur Stadt (OK Fahrbahn) NOCH OFFEN – keine Aussage zur Zulässigkeit
[OK] Rücksprung oberstes Geschoss zur Außenkante des 1. OG West/Platz/Ost/Rück = 1,50 / 1,50 / 1,50 / 1,50 m (Soll 1,50 rundum)
[KONFLIKT] Vorbau (OG1-Kante minus EG-Wand) West/Platz/Ost/Rück = 1,00 / 1,50 / 5,00 / 0,00 m – Vorgabe 'umlaufend auf allen vier Seiten' ist rückseitig NICHT erfüllt (Grundstücksgrenze der Hypothese bei y = 30)
[OK] 18 Säulen Ø 0,40 m, Lage am Rand der Auskragung des 1. OG
[OK] alle Säulenachsen liegen innerhalb des OG1-Umrisses
[KONFLIKT] Säulen (23.65, 29.3) und (23.65, 29.65) liegen nur 0,35 m auseinander (Ø 0,40 m, Säulen berühren/überschneiden sich)
[KONFLIKT] 6 Säulen stehen außerhalb der Hypothese-Grundstücksgrenze (y < 0 bzw. x < 0), z. B. (0.35, -1.15)
[OK] keine Säule überschneidet einen Stellplatz
[OK] keine Säule steht im EG-Gebäude
[HINWEIS] Achsabstände Ostreihe: 8,85, 5,40, 5,40, 5,40, 5,40, 0,35 m (Raster 5,40 m aus Stellplatzpaaren, unregelmäßig am Ende)
[HINWEIS] Rückseite (y = 29,65 m): 2 Säulen – Rückfassade des 1. OG ist zwischen den Ecken ohne Säulen
[OK] EG: 5 Räume, keine Überschneidungen
[OK] EG: Raumflächensumme 540,0 m² (brutto) gegen Geschossumriss 540,0 m²
[KONFLIKT] Kern: EG-Kern x 1–5 / y 0–9,5 m; Entwurf nennt für die Obergeschosse einen Kern-Streifen y –1,5…2,5 m über die volle Breite – Treppe/Aufzug im OG liegen nicht über dem EG-Kern; Lage NOCH OFFEN, im OG-Plan nicht gezeichnet
[HINWEIS] Fenster, Türen, Brüstungen und Geschossraumaufteilung für B1–B3 liegen nicht vor – Ansichten ohne Öffnungen, OG ohne Räume (bewusst nicht erfunden)
[HINWEIS] 13 Stellplätze; Rechteckmaße in x × y [(2.0, 5.5), (5.0, 2.5)] – 2,50 × 5,00 m und 6,00 m Fahrgasse sind ANNAHMEN
[OK] Stellplätze überschneiden sich nicht
[OK] kein Stellplatz liegt im EG-Gebäude
[OK] alle Stellplätze innerhalb der Hypothese-Grundstücksgrenze
[HINWEIS] 8 von 13 Stellplätzen vollständig vom 1. OG überdeckt (Ostauskragung 5,00 m über der Stellplatzreihe); Parallelparker außerhalb
[HINWEIS] Fahrgasse 6,00 × 30,00 m (Annahme)

Ableitung

Alle Grundrisse, Ansichten, der Schnitt und der Lageplan dieses PDFs werden aus demselben Modell-Dict gezeichnet (Umrisse, Höhen, Säulen, Öffnungen, Stellplätze). Abweichungen zwischen Blättern sind dadurch ausgeschlossen; die Widersprüche liegen in den Eingangsdaten.

PROJEKT
Neue Mitte Werlte – Baufeld 3

VARIANTE
Variante B2 – 540 m² EG, Vorbau, Staffel 1,50 m

ZEICHNUNG
Konsistenzprotokoll

MASSSTAB
1:100 (Blattgröße A2 quer)

DATUM
27.10.2026

BLATT
12 / 12 – Konsistenzprotokoll

HÖHEN
HYPOTHETISCH (Höhenschema EG 4,30 / 1. OG 3,60 / oberstes Geschoss 3,60 / Attika 0,50 = 12,00 m aus varianten_e.py) – NICHT gesichert, nicht verbindlich

STATUS
VORLÄUFIGER ENTWURF – NICHT GENEHMIGT

ANMERKUNGEN
Maße in m.

Höhen: HYPOTHETISCH (Höhenschema EG 4,30 / 1. OG 3,60 / oberstes Geschoss 3,60 / Attika 0,50 = 12,00 m aus varianten_e.py) – NICHT gesichert, nicht verbindlich