Variante E – 12 m und umlaufender Vorbau mit Parken

VARIANTE E · NICHT FESTGELEGT

Entwurfsstudie Neue Mitte Werlte – Baufeld 3 · Ergänzung der Variantenstudie · keine Variante festgelegt


Ziel: Gebäudehöhe bis 12,00 m planerisch ausnutzen (drei Geschosse, keine zusätzlichen), oberen Geschosse auf allen vier Seiten über das Erdgeschoss auskragen und von Säulen tragen lassen, die Flächen unter und neben dem Vorbau für Zufahrt, Fahrgasse und Stellplätze nutzen. Vier Teilvarianten zeigen unterschiedliche Staffelrücksprünge (E1 bis Attika, E2 1,50 m, E3 3,00 m) und ein zweireihiges Parkkonzept (E4).

	Bestätigt (Quelle)	Annahme / unbestätigt
Grundstück	ca. 960 m², B-Plan Nr. 123, Baufeld 3, Mischgebiet	ZUSCHNITT 32 × 30 m = Hypothese H1. Der tatsächliche Zuschnitt aus den städtischen Unterlagen liegt in den Projektdateien NICHT vor (nur Fotos im ChatGPT-Chat). Baugrenzen, Abstände, Erschließungsstraße unbekannt.
Höhe / Geschosse	max. 12,00 m und 2–3 Geschosse (Auftraggeber, B-Plan-Entwurf)	Höhenbezug; Traufhöhe 6,50 m; Vollgeschoss-Definition
Stellplatz/Gasse	–	2,50 × 5,00 m und 6,00 m (Auftraggeber als vorläufige Annahme), Säule Ø 0,40 m, Zufahrt von Osten
Wohnfläche	B3: 846 m², 16 WE (Plan)	E: aus Geschosskonturen geschätzt, 0,88 × Wohnstreifen
Realisierbarkeit	–	Zusätzliche Flächen gelten erst als realisierbar, wenn Grundstück, Baugrenzen und Baurecht geprüft sind.

Höhenrahmen: B3 (+9,90 m) gegen 12,00 m

Schnittschema, Höhenbezug und Raumhöhen · alle Höhen vorläufig

VARIANTE E · NICHT FESTGELEGT

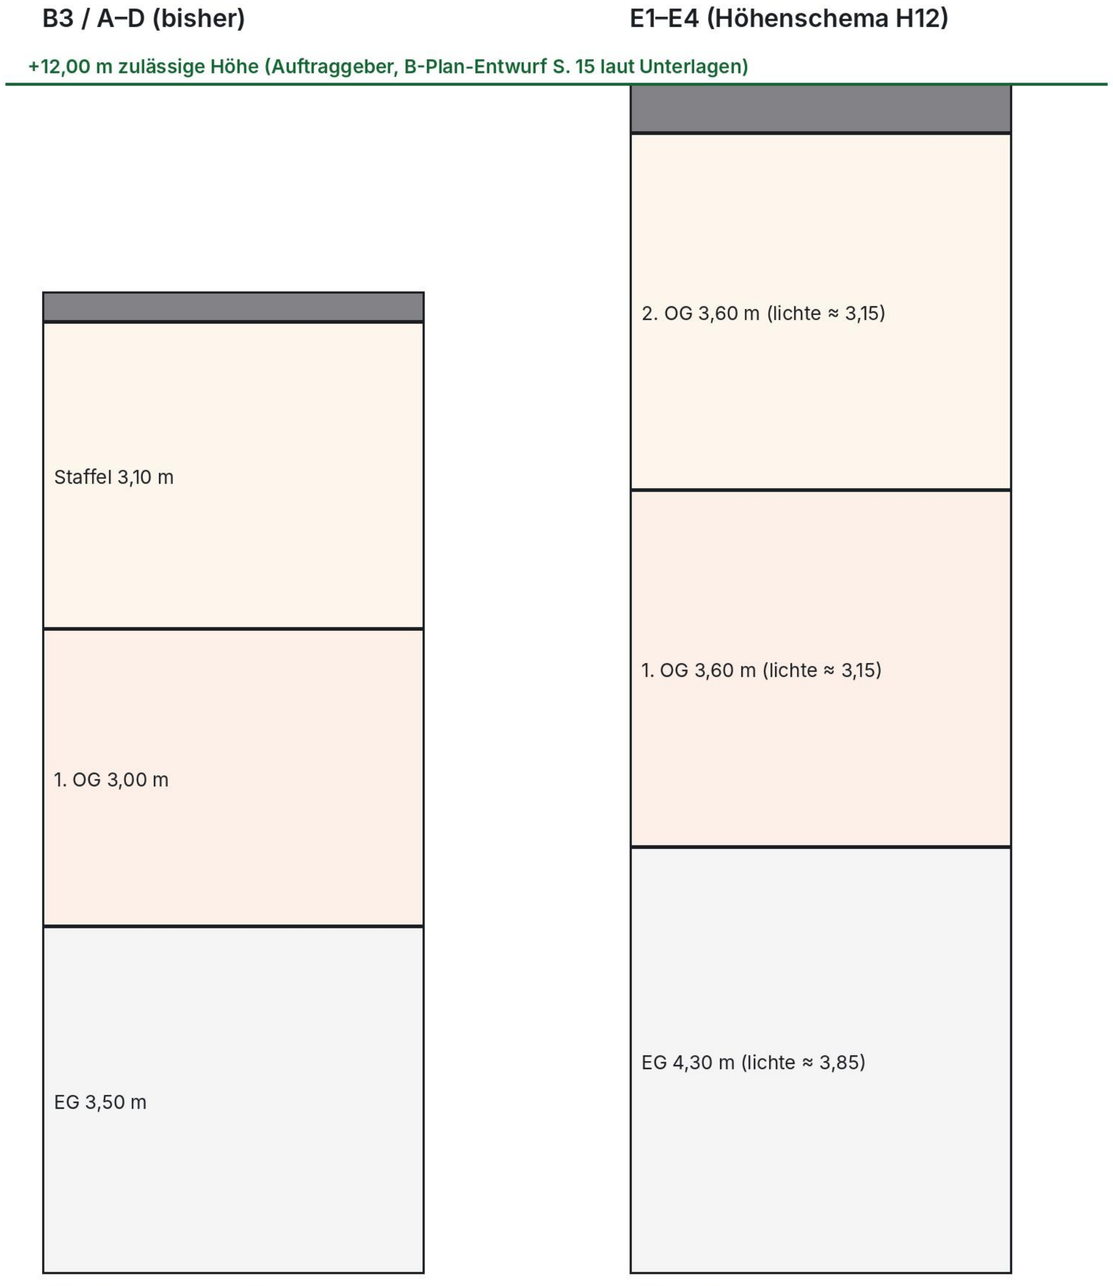

Aspekt	Aussage / Annahme
Höhenbezug	±0,00 = OK Fertigfußboden Erdgeschoss (Bezug Blatt 14). Der Bezugspunkt der Stadt für „12,00 m“ (Gelände, Straßenhöhe, OK Platz) ist NICHT belegt – Differenz zwischen FFB und Gelände unbekannt.
Nutzung der 2,10 m	Statt eines vierten Geschosses (nicht angenommen, nach B-Plan max. drei) fließen die 2,10 m in größere Geschosshöhen: EG +0,80 m (Gastro, Stützweite/Technik), je Wohngeschoss +0,60 m (lichte Höhe ≈ 3,15 statt ≈ 2,65 m: großzügigere Räume, Galerie-/Hochbett-Optionen, bessere Belichtung).
Folge für Wohnfläche	Keine direkte: Fläche entsteht aus der Grundfläche, nicht aus der Höhe. Höhere Geschosse erhöhen Baukosten und Fassadenfläche; Wohnfläche steigt nur über größere Obergeschosse (Vorbau).
Reserve	Mit Attika = 12,00 m keine Reserve für Aufzugsüberfahrt, Absturzsicherung, Technikaufbauten oder Messtoleranz. Alternative: Attika bei +11,50 m (Geschosse 4,10/3,45/3,45) lässt 0,50 m Reserve.
Offen	Traufhöhe 6,50 m laut project_brief (festgesetzt?) gegen +7,90 m Oberkante 1. OG; Definition Vollgeschoss/Staffelgeschoss; Dachform; ob Attika/Brüstung zur Gebäudehöhe zählt.

Benötigte Unterlagen für das reale Grundstück

VARIANTE E · NICHT FESTGELEGT

Ohne diese Angaben bleibt der Lageplan eine Annahme

1. Planzeichnung des Bebauungsplans Nr. 123 (Seite 15 der städtischen Unterlagen) als PDF oder hochaufgelöstes Bild, mit Maßstab bzw. Maßketten.
2. Zuschnitt von Baufeld 3: Eckkoordinaten oder Maße der Grenzen (Flurstück/Liegenschaftskarte), Fläche 960 m² verifizieren.
3. Baugrenzen/Baulinien, Bauweise, Grundflächenzahl, Geschossigkeit, Höhenbezugspunkt, Traufhöhe, Dachform, Festsetzungen zu Stellplätzen.
4. Lage der Erschließungsstraße(n), Zufahrtsverbote/-bereiche, Verlauf des Platzes (Platzseite), Gehwege, Nachbargrundstücke.
5. Stellplatzsatzung der Gemeinde (Anzahl je WE/Gewerbe, Ablöse) und ggf. Gestaltungssatzung.

Sobald diese Daten vorliegen, wird der Zuschnitt in varianten_e.py (PLOT_POLY) ersetzt; Lageplan, Stellplatzprüfung und Überstandsprüfung rechnen neu.

Abgleich im Projekt: Die B3-Pläne nehmen dieselbe Hypothese (32 × 30 m, 11 Stellplätze y 18–23) an; sie ist nirgends mit einem Originalmaß belegt.

Überblick E1–E4

VARIANTE E · NICHT FESTGELEGT

Standardmix · vorläufige Werte · Referenz B3 (A)


Kennzahl	A Referenz B3	E1 – Vorbau bis Attika (Staffel deckungsgleich)	E2 – Staffel 1,50 m zurück	E3 – Staffel 3,00 m zurück	E4 – zweireihiges Parken, kleineres EG
Staffelrücksprung	0,8 m	0.0 m	1.5 m	3.0 m	1.5 m
Grundfläche EG / 1. OG / 2. OG (m²)	576 / 660 / 539	492 / 768 / 768	492 / 768 / 609	492 / 768 / 468	358 / 608 / 464
Wohnfläche netto (m²)	846	1.084	960	852	727
Δ Wohnfläche gg. A	±0	+238 m² (+28 %)	+114 m² (+13 %)	+6 m² (+1 %)	-119 m² (-14 %)
Wohnungen (Standardmix)	16	18	16	15	16
Stellplätze gezeichnet	11	10	10	10	22
Stellplatzbedarf (Ansatz)	53,9	52,5	49,5	48,0	42,6
Säulen	0	23	23	23	21
Höhe Attika	9,90 m	12,00 m	12,00 m	12,00 m	12,00 m

Befund: Der umlaufende Vorbau bringt gegenüber B3 bis zu +238 m² Wohnfläche (E1), kostet aber 84 m² Gewerbefläche im EG und erreicht mit dem 32-m-breiten Grundstück nur 10 Stellplätze (E1–E3) bzw. 22 (E4, zweireihig, mit nur 358 m² EG). Der Stellplatzbedarf von rund 50 bleibt in jedem Fall weit unterschritten. Zahlen sind Annahmen auf hypothetischem Grundstück.

E1 – Vorbau bis Attika (Staffel deckungsgleich)

Entwurfsstudie Baufeld 3 · Konzeptvariante, keine Genehmigungsplanung

E1 · NICHT FESTGELEGT

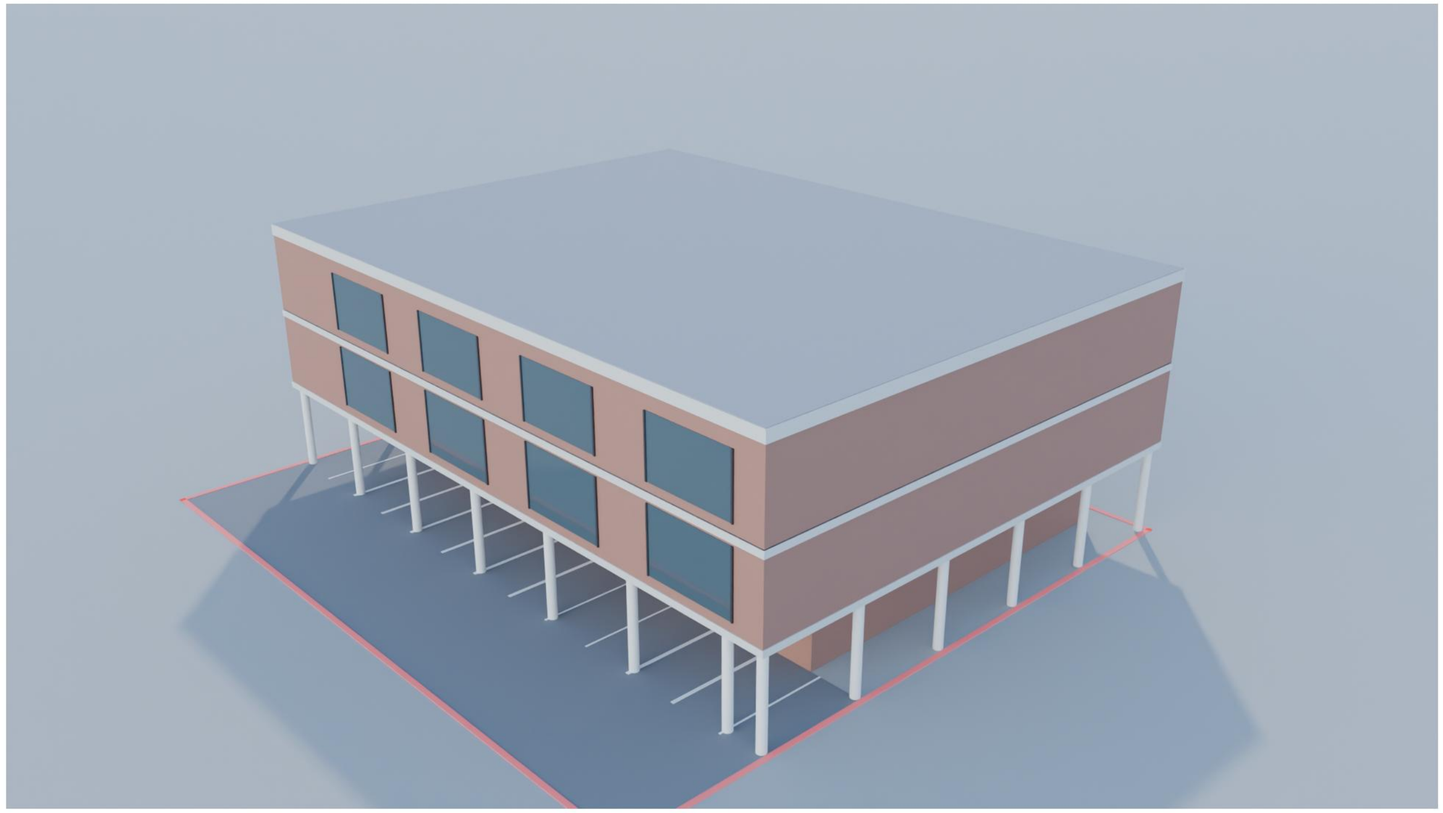

12,00 m Gesamthöhe, drei Geschosse; 1. und 2. OG kragen auf allen vier Seiten über das Erdgeschoss (vorn 1,50 m Arkade, seitlich 2,50 m, hinten 5,00 m über der Stellplatzreihe) und sind deckungsgleich bis zur Attika; Säulen am Rand.

Kennzahl	Wert (vorläufig)
Höhe	12,00 m Attika (EG 4,30 · 1. OG 3,60 · 2. OG 3,60 · Dach/Attika 0,50 m), 3 Geschosse
Grundfläche EG / 1. OG / 2. OG	492 / 768 / 768 m²
Außenmaße EG / 1. OG / 2. OG	29.5 × 17.5 / 32.0 × 24.0 / 32.0 × 24.0 m
Wohnfläche netto (geschätzt)	1.084 m² (1. OG 542 + 2. OG 542)
Wohnungen (Standardmix)	18 WE (9 + 9), 54–68 m², Ø 60 m²
Wohnungen anderer Mix	klein 20 WE (Ø 54 m²) · groß 14 WE (Ø 77 m²)
Säulen	23 Säulen Ø 0,40 m, Raster Rückseite 5,0 m (= 2 Stellplätze)
Stellplätze	10 (Reihe 1: 10, Reihe 2: 0); Bedarf ca. 52,5
Ein-/Ausfahren (geometrisch)	alle Plätze frei erreichbar
Überstand über Grundstück H1	0,00 m (Außenkante OG auf Grenze)

Alle Maße sind Planungsannahmen: Stellplatz 2,50 × 5,00 m, Fahrgasse 6,00 m, Säule Ø 0,40 m, Grundstück 32 × 30 m (Hypothese, tatsächlicher Zuschnitt unbestätigt), Zufahrt von Osten (Annahme). Wohnfläche = 0,88 × Wohnstreifen, schematisch. Nichts ist genehmigt, bemessen oder abgestimmt.


E1: Lageplan mit Gebäude, Säulen, Zufahrt und Stellplätzen

E1 – Vorbau bis Attika (Staffel deckungsgleich)

E1 · NICHT FESTGELEGT

Lageplan E1 – Gebäude, Säulen, Zufahrt und Stellplätze

Grundstück H1 32 × 30 m HYPOTHETISCH (tatsächlicher Zuschnitt Baufeld 3 liegt nicht vor) · Stellplatz 2,50 × 5,00 m, Fahrgasse 6,00 m = Planungsannahmen · Zufahrt von Osten = Annahme

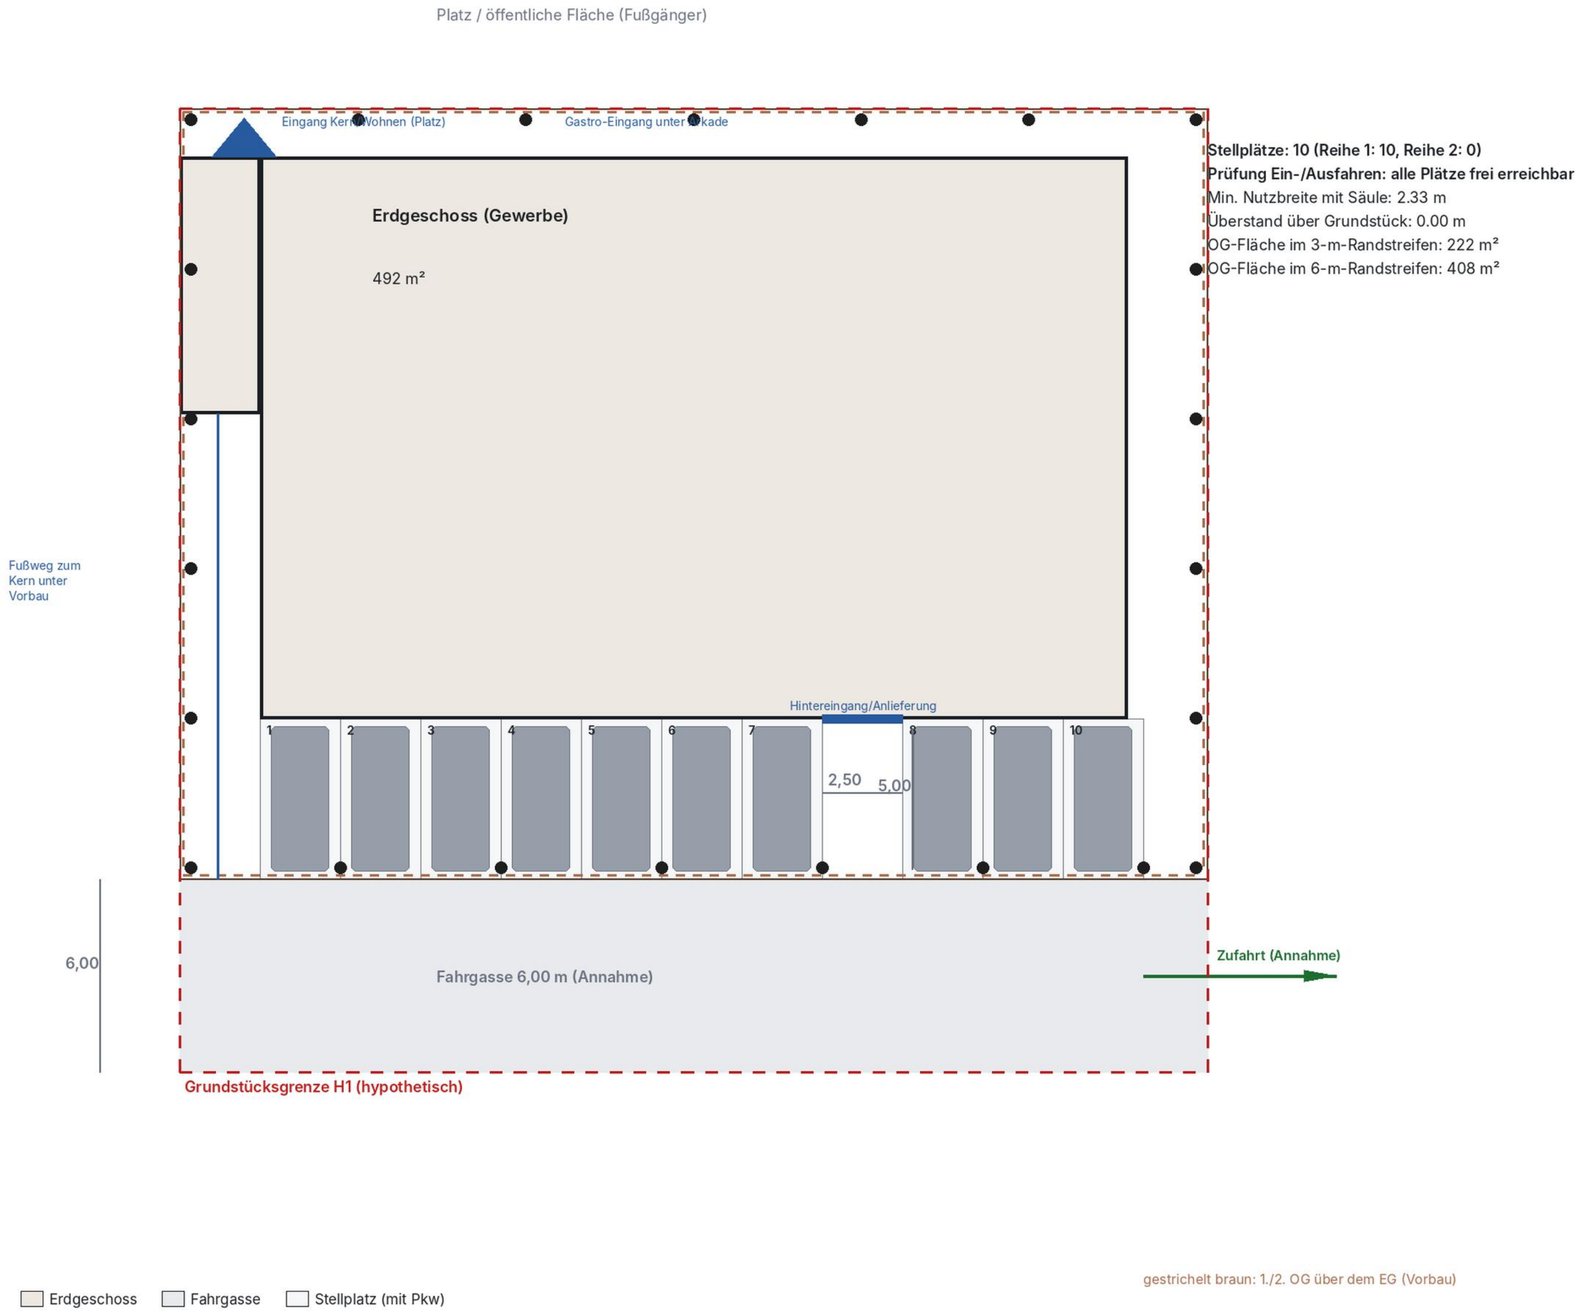

Parkprüfung	
Stellplätze	10
Ein-/Ausfahren	frei
Fahrgasse	6,00 m (Annahme)
Min. Nutzbreite mit Säule	2.33 m
Überstand H1	0,00 m

- vereinfachte Geometrieprüfung (Rechteckfreiraum 6,00 m vor 5,00 m tiefen 90°-Stellplätzen), keine Schleppkurven-Simulation
- Säulen (Ø 0,40 m) auf der Stellplatzgrenze: Nutzbreite 2,50 – 0,20 = 2,30 m je Platz (Mindestmaß/Stellplatzverordnung prüfen)
- Zufahrt von Osten ist Annahme (Lage der Erschließungsstraße unbekannt)
- Lücke zwischen Platz 7 und 8 (x 20,0–22,5): Stellplatz entfällt für Hintereingang/Anlieferung Gewerbe; Fußweg zum Kern an der Westseite (x 0–2,5) unter dem Vorbau

E1: Grundrisse EG, 1. OG, 2. OG


E1 – Vorbau bis Attika (Staffel deckungsgleich) · schematisch

E1 · NICHT FESTGELEGT

Erdgeschoss

E1: Erdgeschoss (schematisch)

Grundriss schematisch · Wohnungsaufteilung = Streifenmodell (Mittelgang 2,0 m), netto = 0,88 × brutto · Säulen Ø 0,40 m · Grundstück H1 hypothetisch

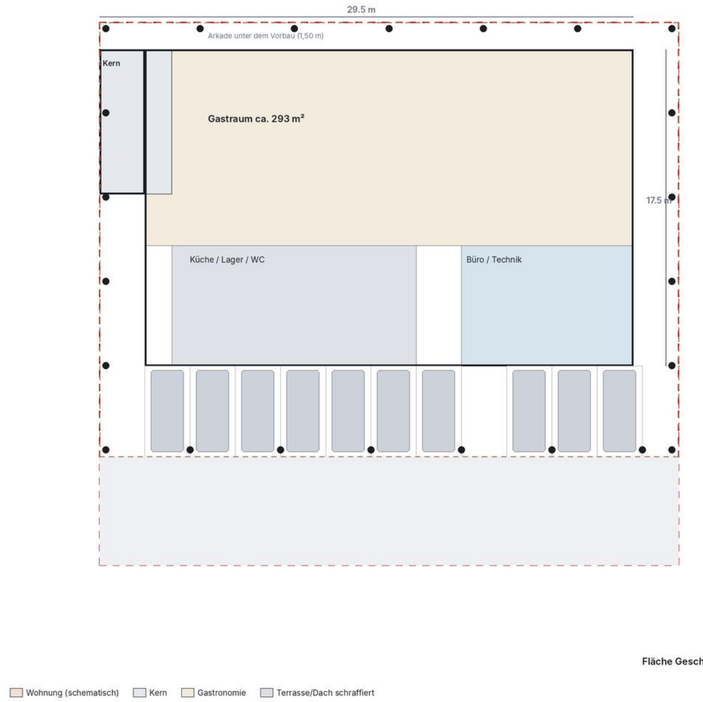


Fläche Geschoss 492 m²

1. Obergeschoss

E1: 1. Obergeschoss (schematisch)

Grundriss schematisch · Wohnungsaufteilung = Streifenmodell (Mittelgang 2,0 m), netto = 0,88 × brutto · Säulen Ø 0,40 m · Grundstück H1 hypothetisch

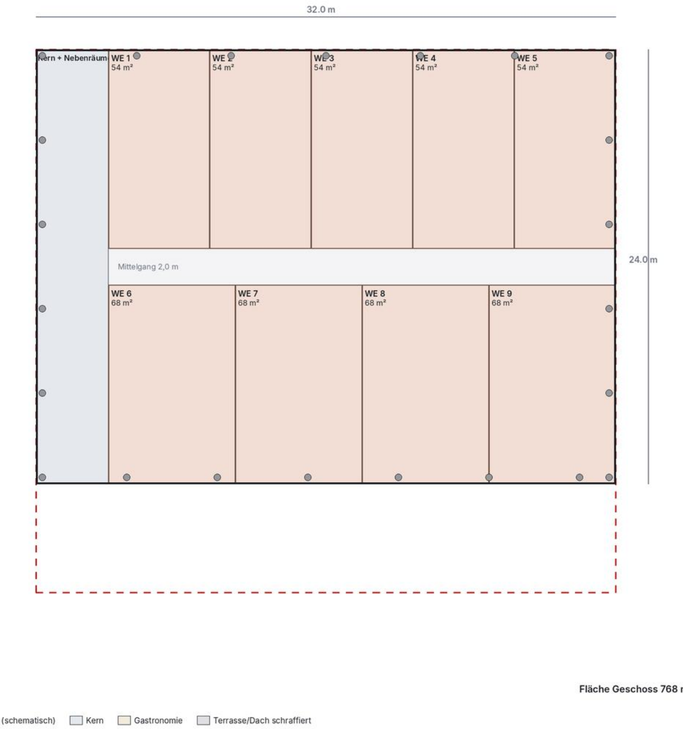


Fläche Geschoss 768 m²

2. Obergeschoss

E1: 2. Obergeschoss (schematisch)

Grundriss schematisch · Wohnungsaufteilung = Streifenmodell (Mittelgang 2,0 m), netto = 0,88 × brutto · Säulen Ø 0,40 m · Grundstück H1 hypothetisch

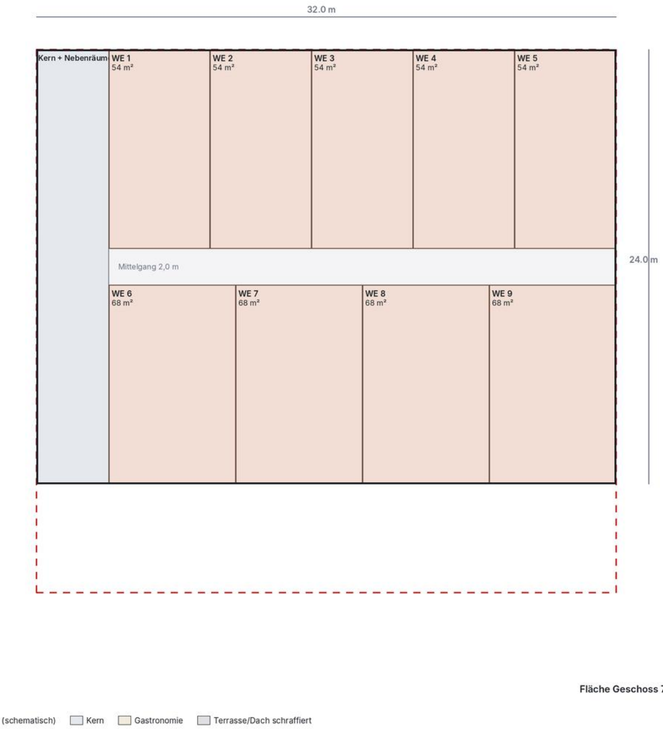

Fläche Geschoss 768 m²

Wohnung (schematisch) Kern Gastronomie Terrasse/Dach schraffiert

Wohnung (schematisch) Kern Gastronomie Terrasse/Dach schraffiert

Wohnung (schematisch) Kern Gastronomie Terrasse/Dach schraffiert

E1: vier Fassaden


E1 · NICHT FESTGELEGT

E1 – Vorbau bis Attika (Staffel deckungsgleich) · orthogonale Ansichten aus dem 3D-Modell

Vorderfassade (Platzseite)



Rückfassade (Stellplatzseite)

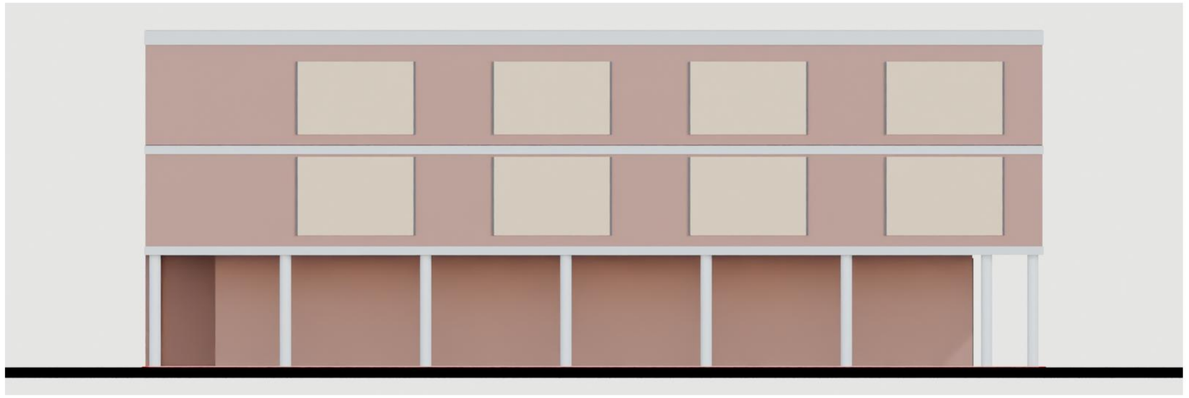

Seitenfassade West



Seitenfassade Ost



E1: Gebäudeschnitt mit Geschosshöhen und 3D-Ansicht

E1 – Vorbau bis Attika (Staffel deckungsgleich)

E1 · NICHT FESTGELEGT


E1: Schnitt bei x = 16.25 m mit Geschosshöhen (schematisch)


Platzseite links, Rückseite rechts · Höhenbezug ±0,00 = OK Fertigfußboden EG (Planbezug Blatt 14) – Bezugspunkt der Stadt für die 12,00 m ist NICHT belegt



Geschosshöhen: EG 4,30 m · 1. OG 3,60 m · 2. OG 3,60 m · Dach/Attika 0,50 m = 12,00 m. Reserve 0,00 m: Aufzugsüberfahrt, Dachaufbauten und Messtoleranz wären zusätzlich zu klären.

Säulen im Schnitt: 1 (Achse x ≈ 15 m) · Säulen insgesamt: 23 · Stellplatz-Decke Vorbau-Unterkante +3,85 m

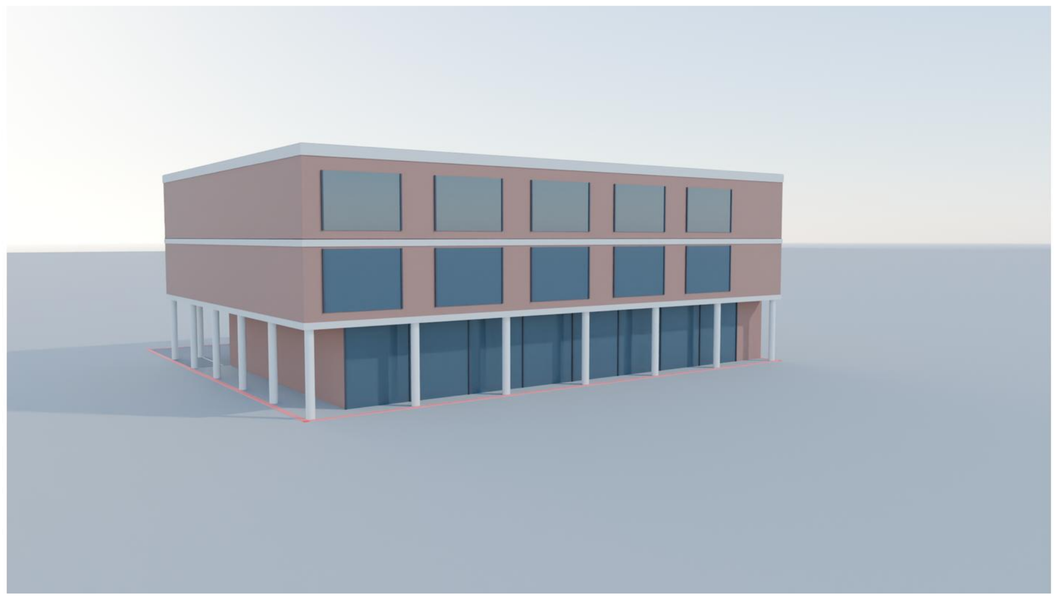


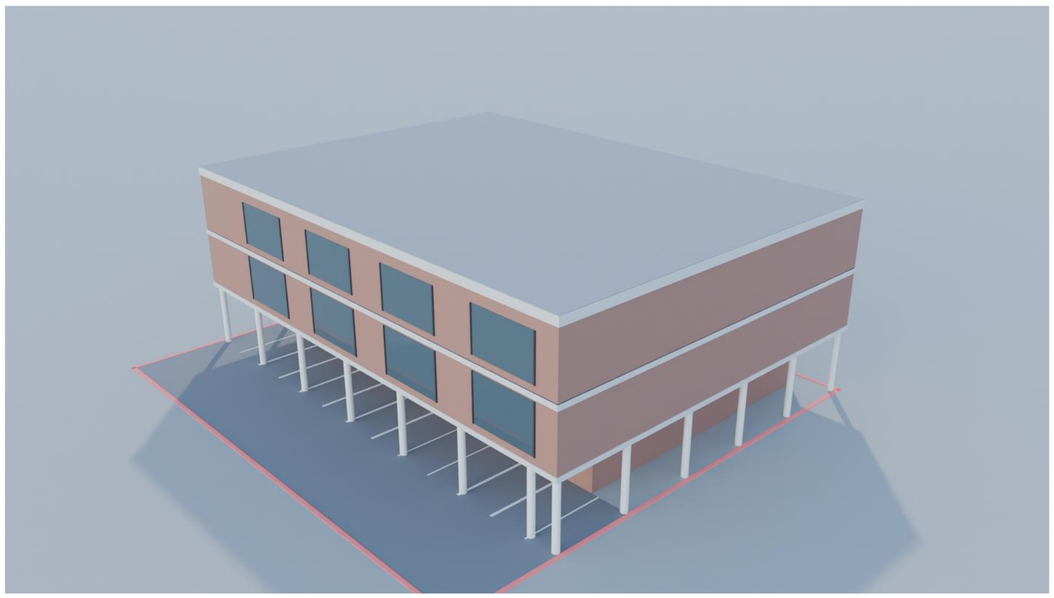

E2 – Staffel 1,50 m zurück

Entwurfsstudie Baufeld 3 · Konzeptvariante, keine Genehmigungsplanung

E2 · NICHT FESTGELEGT

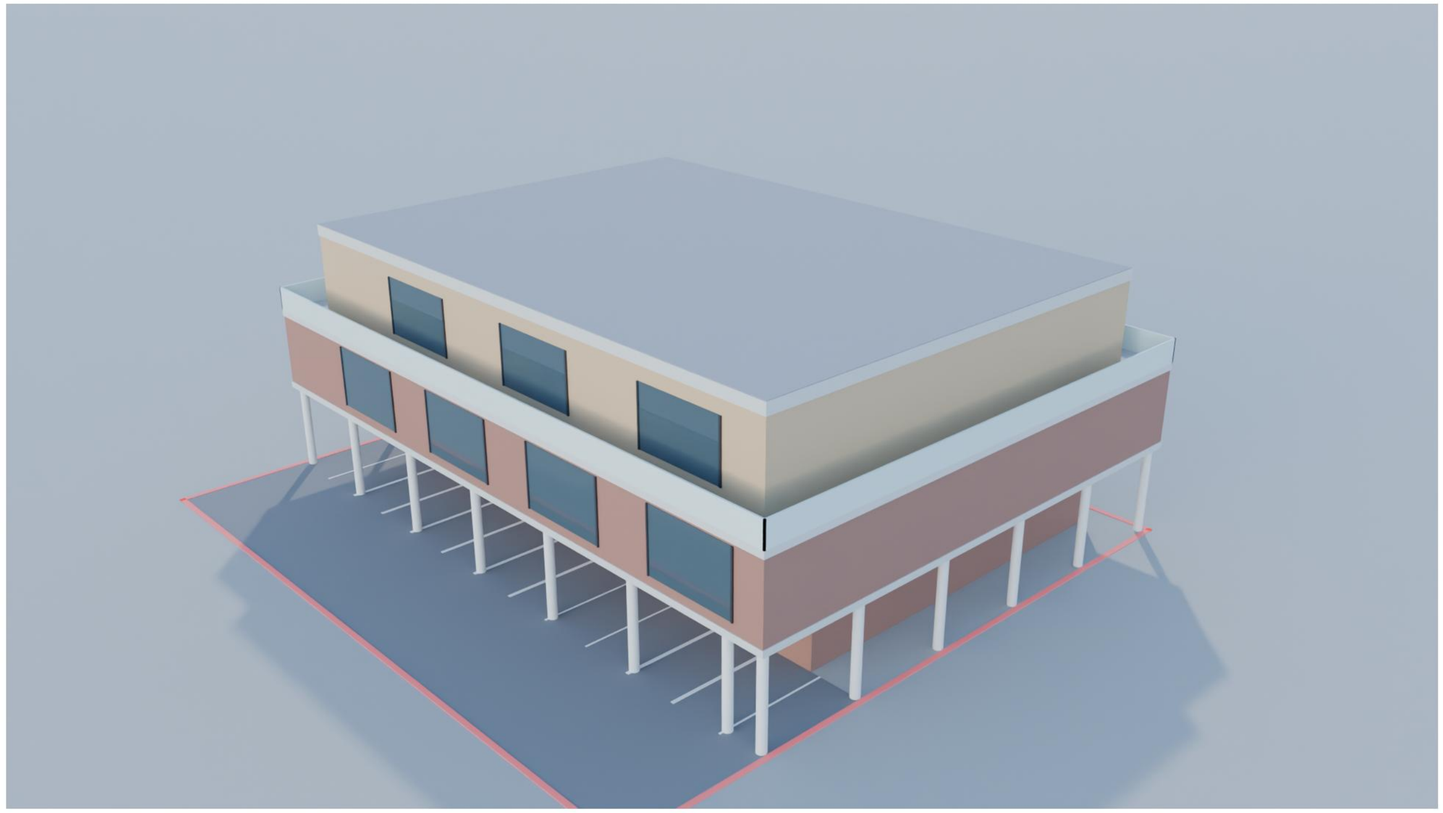

Wie E1, das 2. OG springt rundum 1,50 m hinter die Kante des 1. OG zurück (umlaufende Dachterrasse).

Kennzahl	Wert (vorläufig)
Höhe	12,00 m Attika (EG 4,30 · 1. OG 3,60 · 2. OG 3,60 · Dach/Attika 0,50 m), 3 Geschosse
Grundfläche EG / 1. OG / 2. OG	492 / 768 / 609 m²
Außenmaße EG / 1. OG / 2. OG	29.5 × 17.5 / 32.0 × 24.0 / 29.0 × 21.0 m
Wohnfläche netto (geschätzt)	960 m² (1. OG 542 + 2. OG 418)
Wohnungen (Standardmix)	16 WE (9 + 7), 52–70 m², Ø 60 m²
Wohnungen anderer Mix	klein 19 WE (Ø 50 m²) · groß 12 WE (Ø 80 m²)
Säulen	23 Säulen Ø 0,40 m, Raster Rückseite 5,0 m (= 2 Stellplätze)
Stellplätze	10 (Reihe 1: 10, Reihe 2: 0); Bedarf ca. 49,5
Ein-/Ausfahren (geometrisch)	alle Plätze frei erreichbar
Überstand über Grundstück H1	0,00 m (Außenkante OG auf Grenze)

Alle Maße sind Planungsannahmen: Stellplatz 2,50 × 5,00 m, Fahrgasse 6,00 m, Säule Ø 0,40 m, Grundstück 32 × 30 m (Hypothese, tatsächlicher Zuschnitt unbestätigt), Zufahrt von Osten (Annahme). Wohnfläche = 0,88 × Wohnstreifen, schematisch. Nichts ist genehmigt, bemessen oder abgestimmt.


E2: Lageplan mit Gebäude, Säulen, Zufahrt und Stellplätzen

E2 – Staffel 1,50 m zurück

E2 · NICHT FESTGELEGT

Lageplan E2 – Gebäude, Säulen, Zufahrt und Stellplätze

Grundstück H1 32 × 30 m HYPOTHETISCH (tatsächlicher Zuschnitt Baufeld 3 liegt nicht vor) · Stellplatz 2,50 × 5,00 m, Fahrgasse 6,00 m = Planungsannahmen · Zufahrt von Osten = Annahme

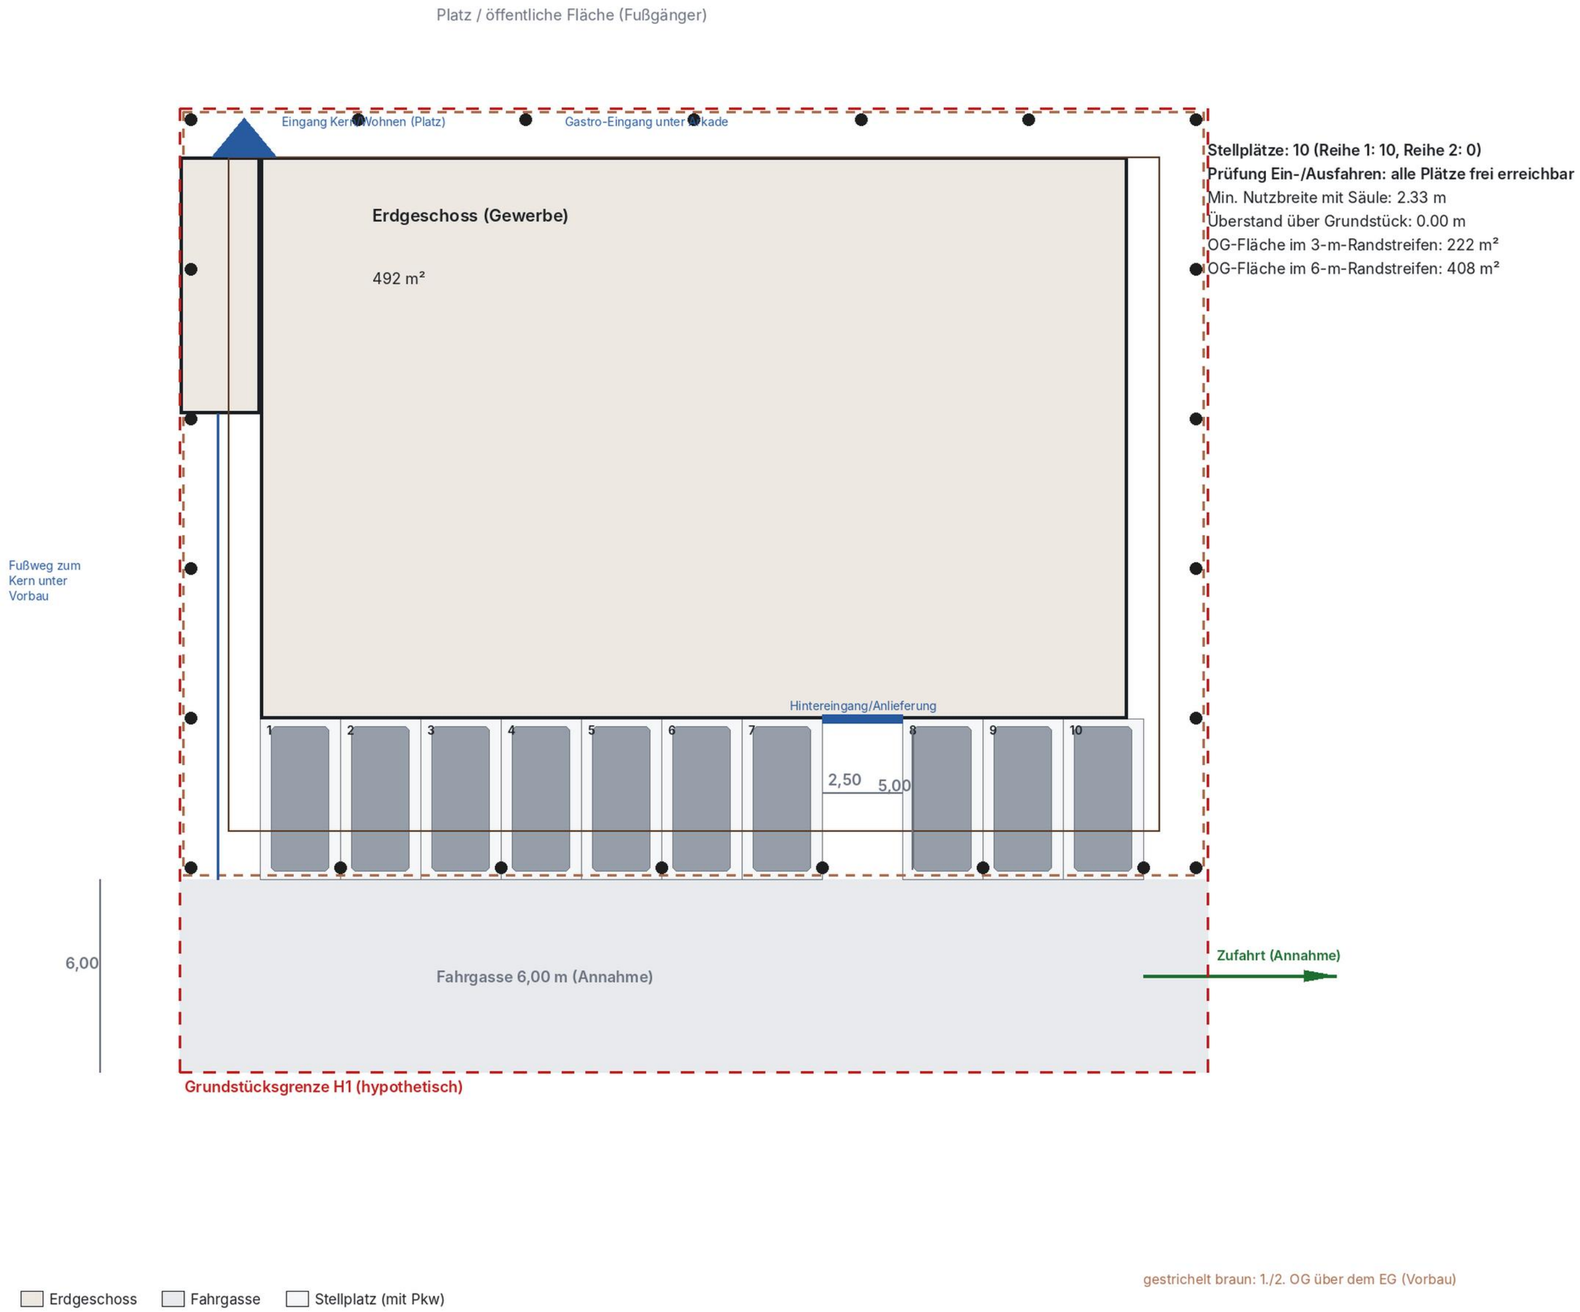

Parkprüfung	
Stellplätze	10
Ein-/Ausfahren	frei
Fahrgasse	6,00 m (Annahme)
Min. Nutzbreite mit Säule	2.33 m
Überstand H1	0,00 m

- vereinfachte Geometrieprüfung (Rechteckfreiraum 6,00 m vor 5,00 m tiefen 90°-Stellplätzen), keine Schleppkurven-Simulation
- Säulen (Ø 0,40 m) auf der Stellplatzgrenze: Nutzbreite 2,50 − 0,20 = 2,30 m je Platz (Mindestmaß/Stellplatzverordnung prüfen)
- Zufahrt von Osten ist Annahme (Lage der Erschließungsstraße unbekannt)
- Lücke zwischen Platz 7 und 8 (x 20,0–22,5): Stellplatz entfällt für Hintereingang/Anlieferung Gewerbe; Fußweg zum Kern an der Westseite (x 0–2,5) unter dem Vorbau

E2: Grundrisse EG, 1. OG, 2. OG


E2 – Staffel 1,50 m zurück · schematisch

E2 · NICHT FESTGELEGT

Erdgeschoss

E2: Erdgeschoss (schematisch)

Grundriss schematisch · Wohnungsaufteilung = Streifenmodell (Mittelgang 2,0 m), netto = 0,88 × brutto · Säulen Ø 0,40 m · Grundstück H1 hypothetisch

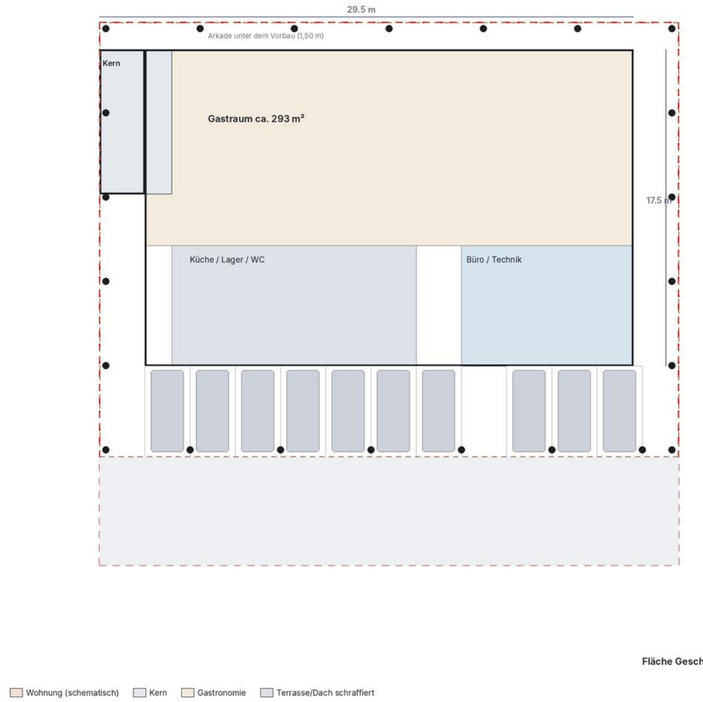


Fläche Geschoss 492 m²

Wohnung (schematisch) Kern Gastronomie Terrasse/Dach schraffiert

1. Obergeschoss

E2: 1. Obergeschoss (schematisch)

Grundriss schematisch · Wohnungsaufteilung = Streifenmodell (Mittelgang 2,0 m), netto = 0,88 × brutto · Säulen Ø 0,40 m · Grundstück H1 hypothetisch

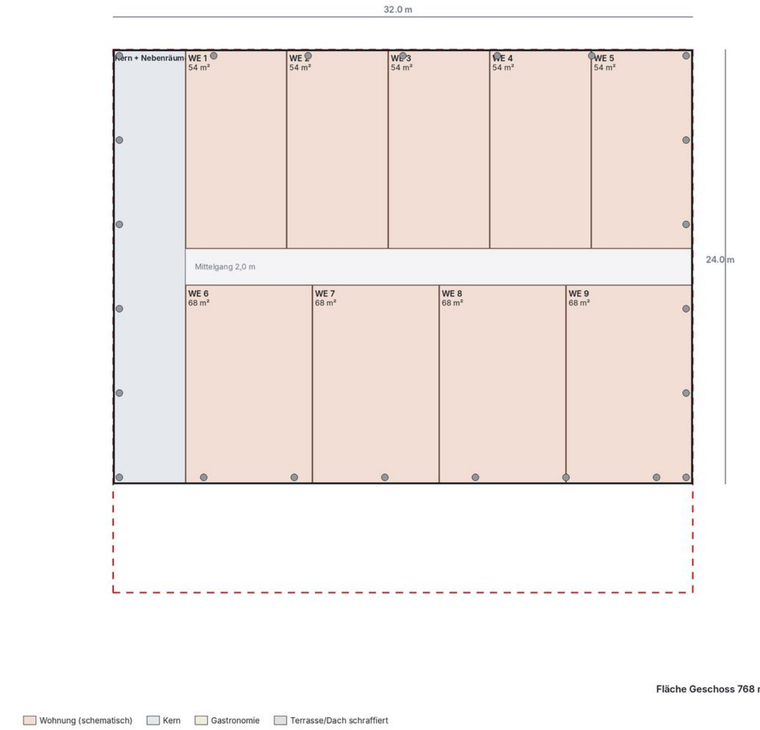


Fläche Geschoss 768 m²

Wohnung (schematisch) Kern Gastronomie Terrasse/Dach schraffiert

2. Obergeschoss

E2: 2. Obergeschoss (Staffel) (schematisch)

Grundriss schematisch · Wohnungsaufteilung = Streifenmodell (Mittelgang 2,0 m), netto = 0,88 × brutto · Säulen Ø 0,40 m · Grundstück H1 hypothetisch

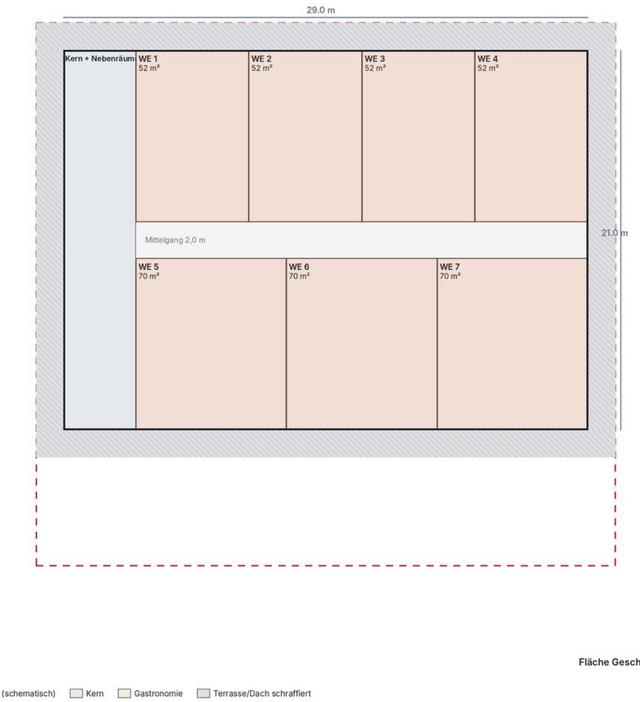

Fläche Geschoss 609 m²

Wohnung (schematisch) Kern Gastronomie Terrasse/Dach schraffiert

E2: vier Fassaden


E2 – Staffel 1,50 m zurück · orthogonale Ansichten aus dem 3D-Modell

E2 · NICHT FESTGELEGT

Vorderfassade (Platzseite)



Rückfassade (Stellplatzseite)

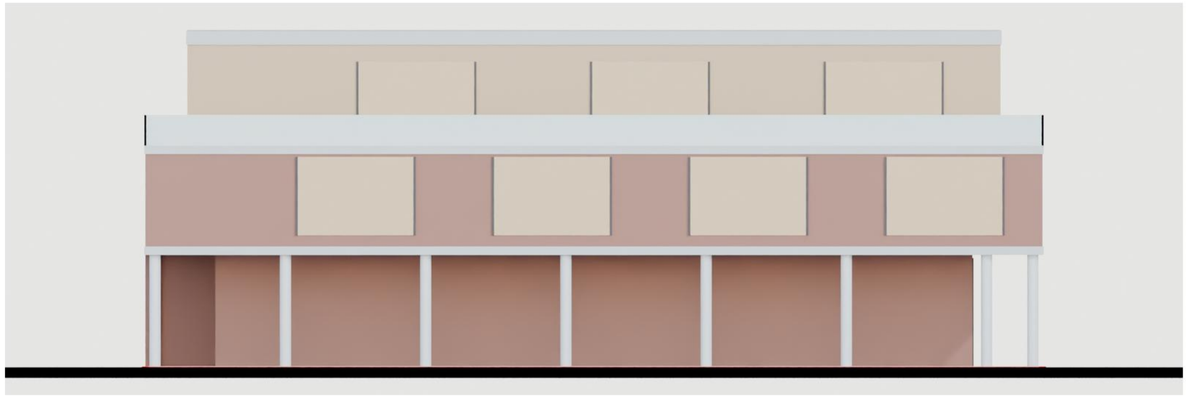

Seitenfassade West



Seitenfassade Ost



E2: Gebäudeschnitt mit Geschosshöhen und 3D-Ansicht

E2 – Staffel 1,50 m zurück


E2 · NICHT FESTGELEGT


E2: Schnitt bei x = 16.25 m mit Geschosshöhen (schematisch)

Platzseite links, Rückseite rechts · Höhenbezug ±0,00 = OK Fertigfußboden EG (Planbezug Blatt 14) – Bezugspunkt der Stadt für die 12,00 m ist NICHT belegt



Geschosshöhen: EG 4,30 m · 1. OG 3,60 m · 2. OG 3,60 m · Dach/Attika 0,50 m = 12,00 m. Reserve 0,00 m: Aufzugsüberfahrt, Dachaufbauten und Messtoleranz wären zusätzlich zu klären.
Säulen im Schnitt: 1 (Achse x ≈ 15 m) · Säulen insgesamt: 23 · Stellplatz-Decke Vorbau-Unterkante +3,85 m

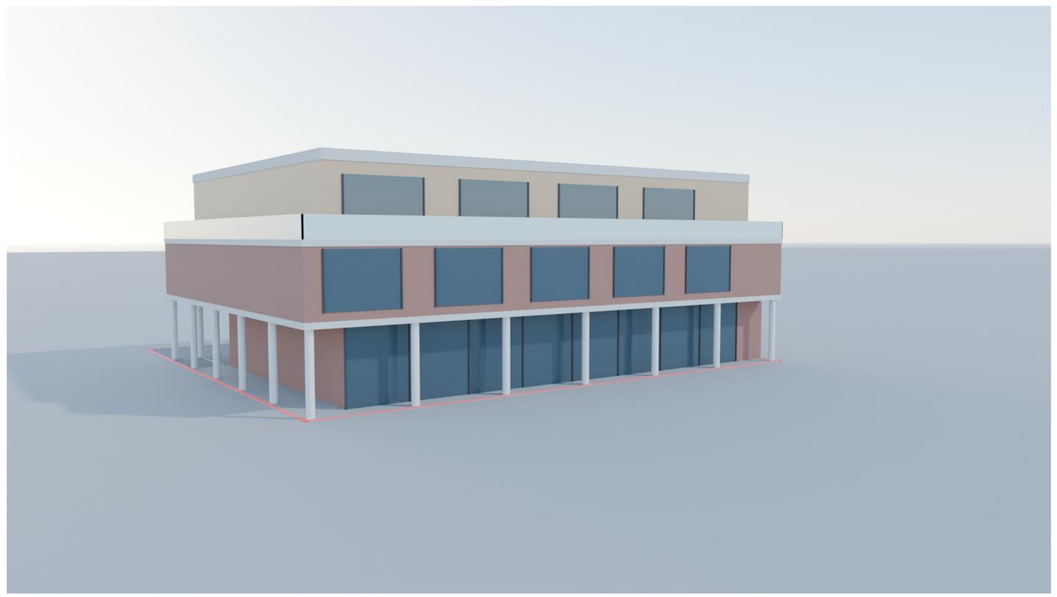


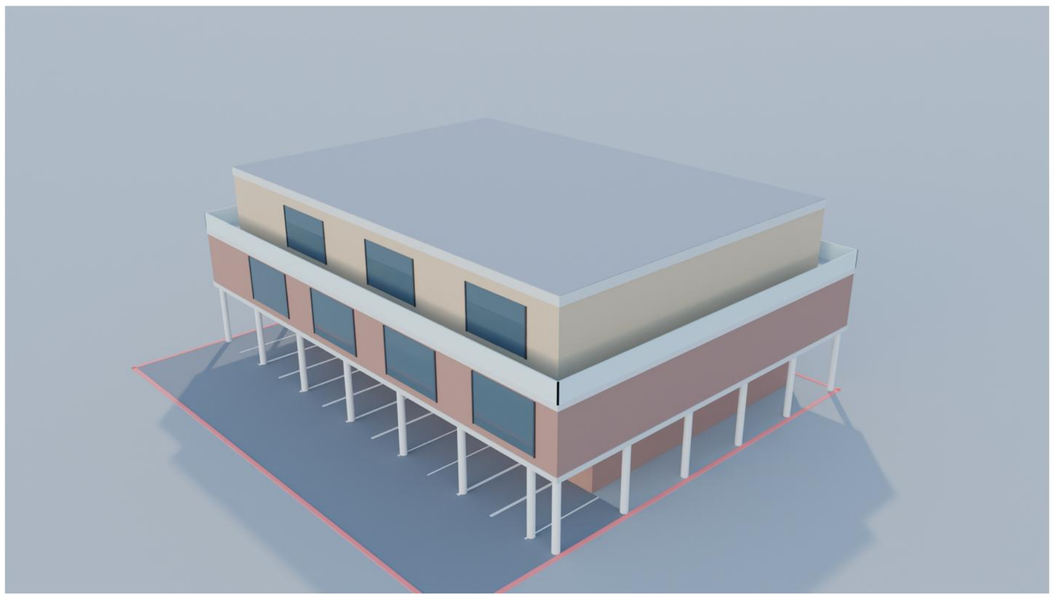

E3 – Staffel 3,00 m zurück

Entwurfsstudie Baufeld 3 · Konzeptvariante, keine Genehmigungsplanung

E3 · NICHT FESTGELEGT

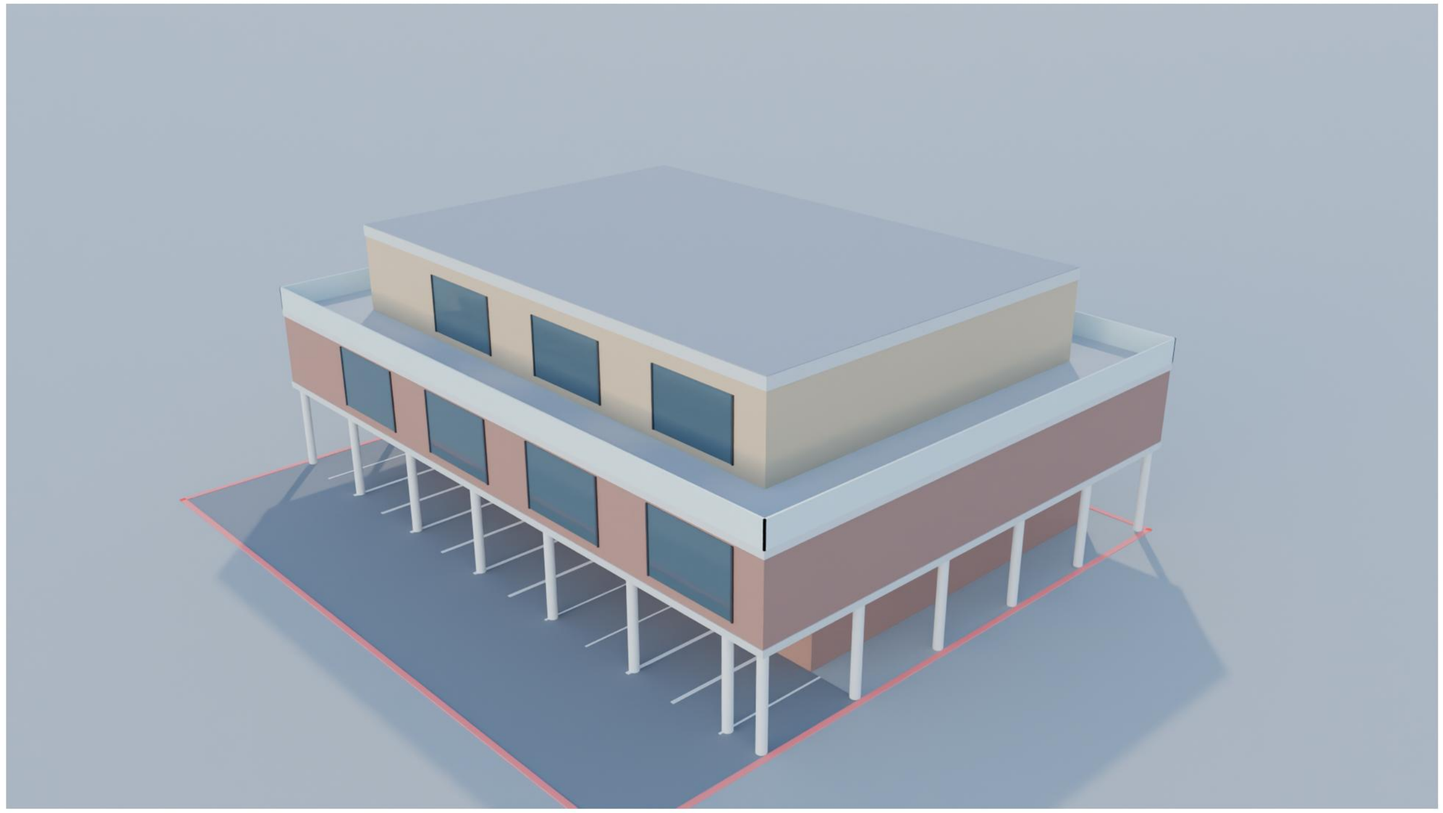

Wie E1, das 2. OG springt rundum 3,00 m zurück (breite umlaufende Dachterrasse, kleineres Staffelgeschoss).

Kennzahl	Wert (vorläufig)
Höhe	12,00 m Attika (EG 4,30 · 1. OG 3,60 · 2. OG 3,60 · Dach/Attika 0,50 m), 3 Geschosse
Grundfläche EG / 1. OG / 2. OG	492 / 768 / 468 m²
Außenmaße EG / 1. OG / 2. OG	29.5 × 17.5 / 32.0 × 24.0 / 26.0 × 18.0 m
Wohnfläche netto (geschätzt)	852 m² (1. OG 542 + 2. OG 310)
Wohnungen (Standardmix)	15 WE (9 + 6), 52–68 m², Ø 57 m²
Wohnungen anderer Mix	klein 17 WE (Ø 50 m²) · groß 12 WE (Ø 71 m²)
Säulen	23 Säulen Ø 0,40 m, Raster Rückseite 5,0 m (= 2 Stellplätze)
Stellplätze	10 (Reihe 1: 10, Reihe 2: 0); Bedarf ca. 48,0
Ein-/Ausfahren (geometrisch)	alle Plätze frei erreichbar
Überstand über Grundstück H1	0,00 m (Außenkante OG auf Grenze)

Alle Maße sind Planungsannahmen: Stellplatz 2,50 × 5,00 m, Fahrgasse 6,00 m, Säule Ø 0,40 m, Grundstück 32 × 30 m (Hypothese, tatsächlicher Zuschnitt unbestätigt), Zufahrt von Osten (Annahme). Wohnfläche = 0,88 × Wohnstreifen, schematisch. Nichts ist genehmigt, bemessen oder abgestimmt.


E3: Lageplan mit Gebäude, Säulen, Zufahrt und Stellplätzen

E3 – Staffel 3,00 m zurück

E3 · NICHT FESTGELEGT

Lageplan E3 – Gebäude, Säulen, Zufahrt und Stellplätze

Grundstück H1 32 × 30 m HYPOTHETISCH (tatsächlicher Zuschnitt Baufeld 3 liegt nicht vor) · Stellplatz 2,50 × 5,00 m, Fahrgasse 6,00 m = Planungsannahmen · Zufahrt von Osten = Annahme

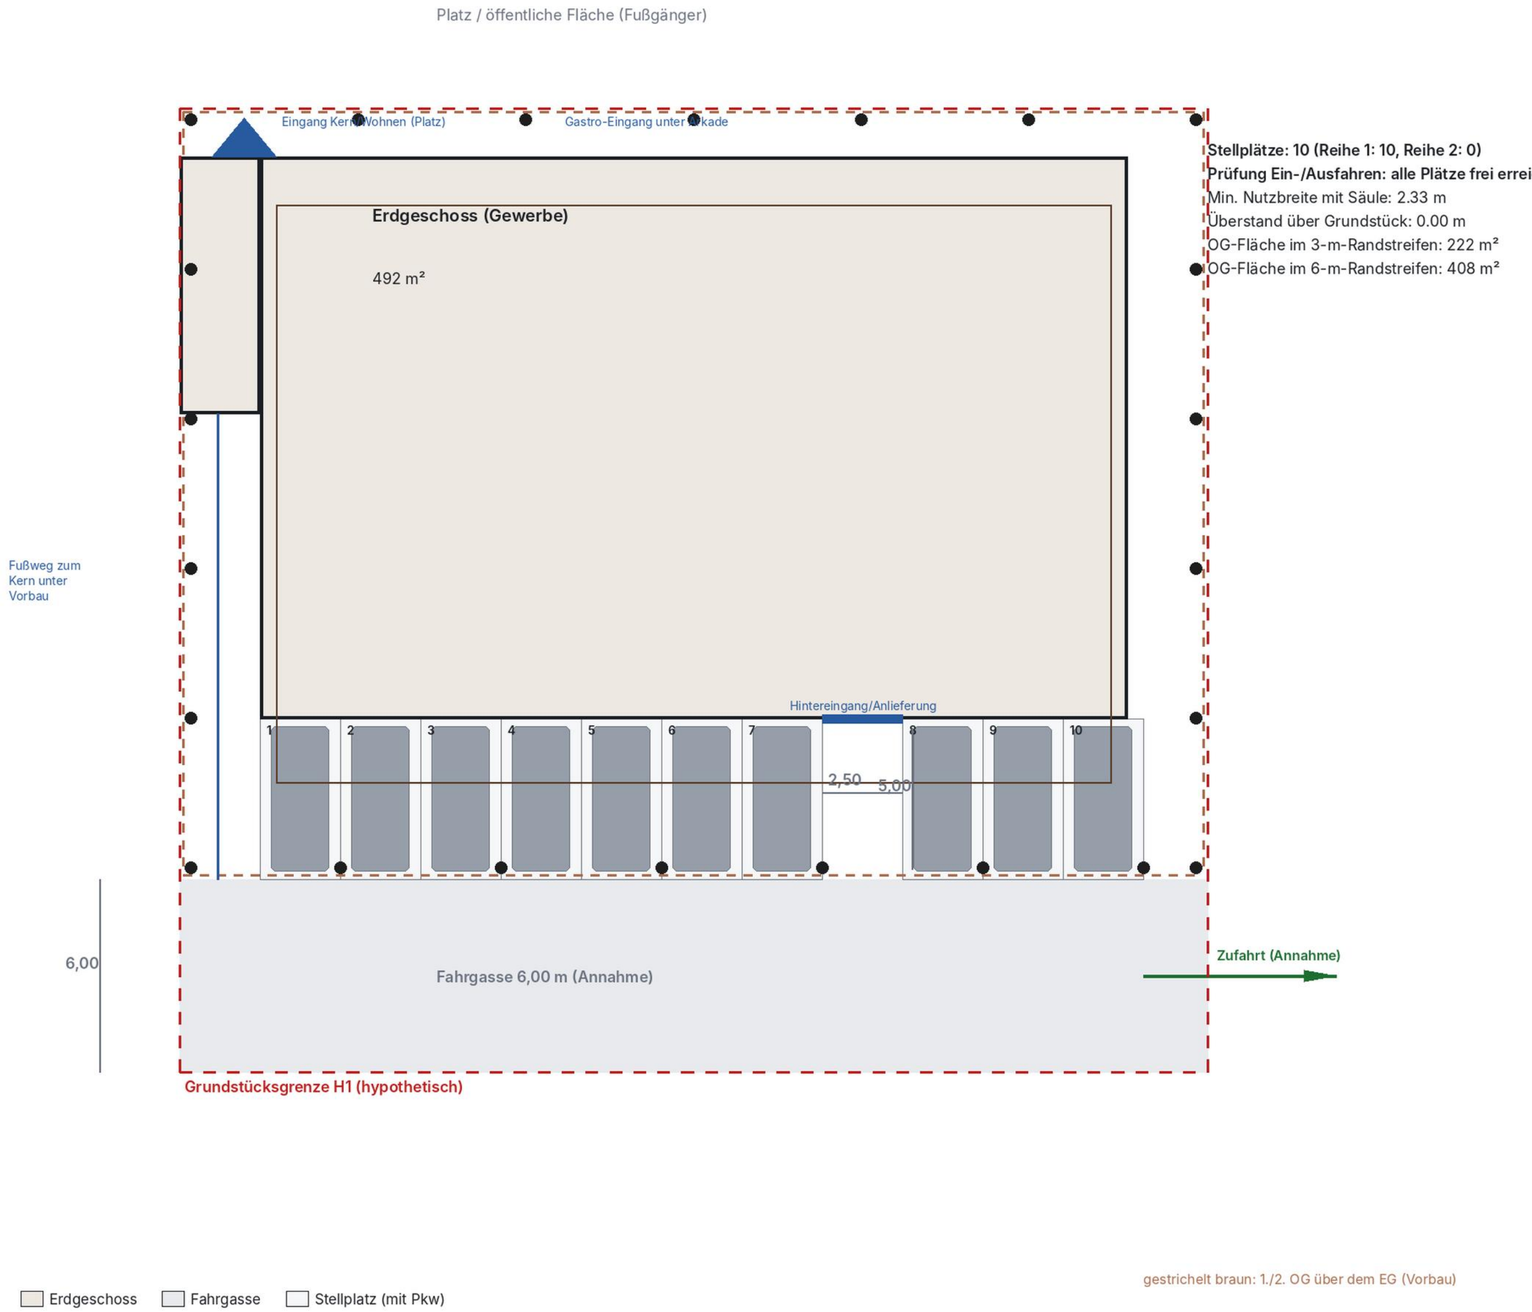

Parkprüfung	
Stellplätze	10
Ein-/Ausfahren	frei
Fahrgasse	6,00 m (Annahme)
Min. Nutzbreite mit Säule	2.33 m
Überstand H1	0,00 m

- vereinfachte Geometrieprüfung (Rechteckfreiraum 6,00 m vor 5,00 m tiefen 90°-Stellplätzen), keine Schleppkurven-Simulation
- Säulen (Ø 0,40 m) auf der Stellplatzgrenze: Nutzbreite 2,50 − 0,20 = 2,30 m je Platz (Mindestmaß/Stellplatzverordnung prüfen)
- Zufahrt von Osten ist Annahme (Lage der Erschließungsstraße unbekannt)
- Lücke zwischen Platz 7 und 8 (x 20,0–22,5): Stellplatz entfällt für Hintereingang/Anlieferung Gewerbe; Fußweg zum Kern an der Westseite (x 0–2,5) unter dem Vorbau

E3: Grundrisse EG, 1. OG, 2. OG


E3 – Staffel 3,00 m zurück · schematisch

E3 · NICHT FESTGELEGT

Erdgeschoss

E3: Erdgeschoss (schematisch)

Grundriss schematisch · Wohnungsaufteilung = Streifenmodell (Mittelgang 2,0 m), netto = 0,88 × brutto · Säulen Ø 0,40 m · Grundstück H1 hypothetisch

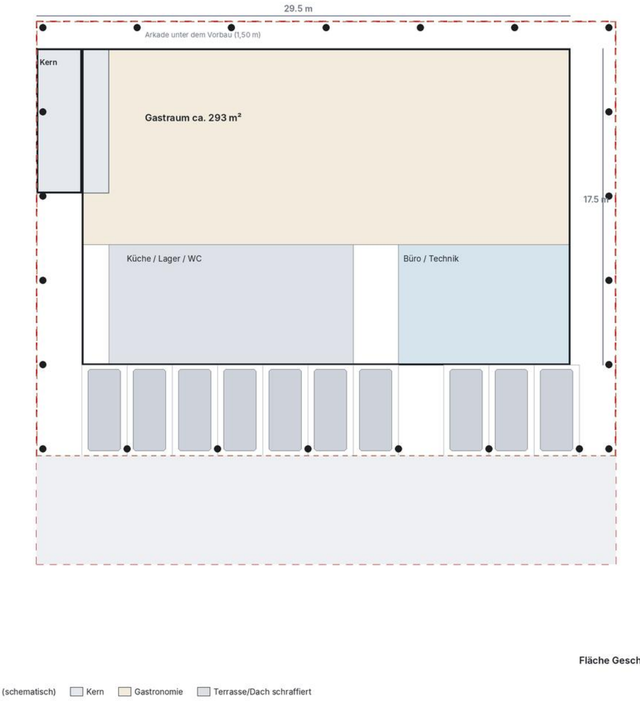


Fläche Geschoss 492 m²

Wohnung (schematisch) Kern Gastronomie Terrasse/Dach schraffiert

1. Obergeschoss

E3: 1. Obergeschoss (schematisch)

Grundriss schematisch · Wohnungsaufteilung = Streifenmodell (Mittelgang 2,0 m), netto = 0,88 × brutto · Säulen Ø 0,40 m · Grundstück H1 hypothetisch

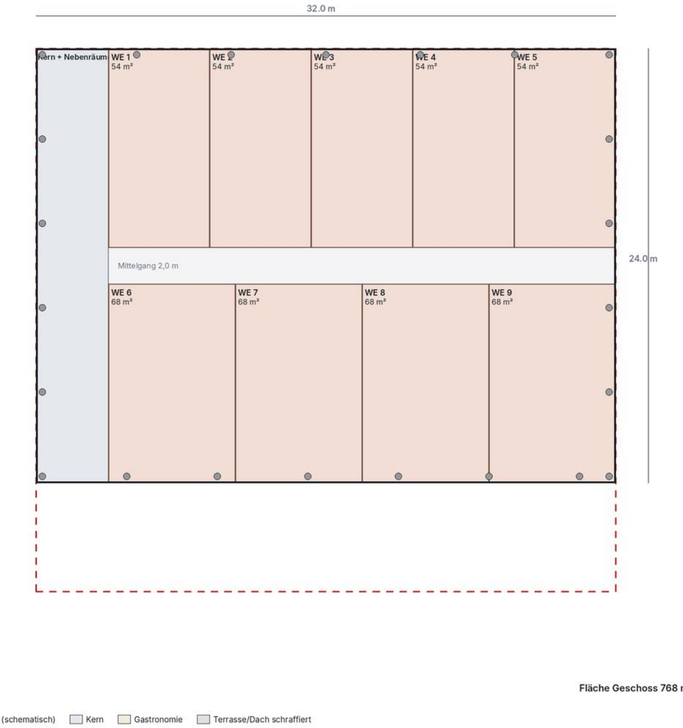


Fläche Geschoss 768 m²

Wohnung (schematisch) Kern Gastronomie Terrasse/Dach schraffiert

2. Obergeschoss

E3: 2. Obergeschoss (Staffel) (schematisch)

Grundriss schematisch · Wohnungsaufteilung = Streifenmodell (Mittelgang 2,0 m), netto = 0,88 × brutto · Säulen Ø 0,40 m · Grundstück H1 hypothetisch

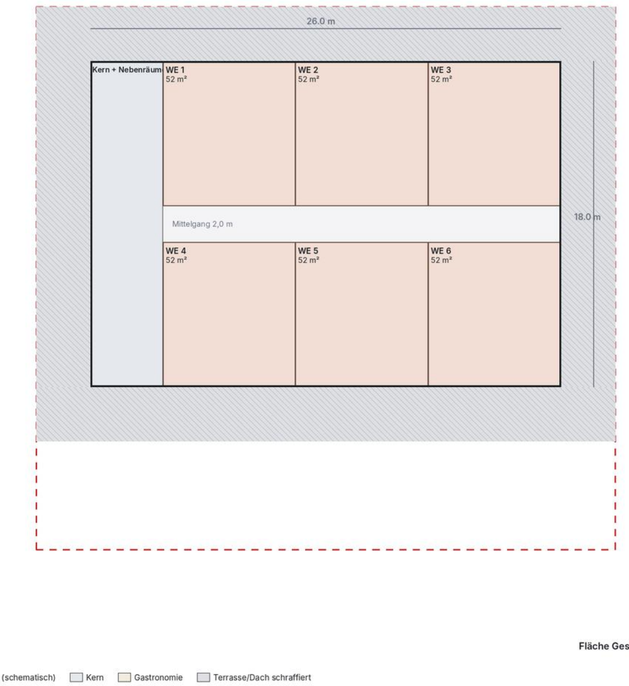

Fläche Geschoss 468 m²

Wohnung (schematisch) Kern Gastronomie Terrasse/Dach schraffiert

E3: vier Fassaden


E3 – Staffel 3,00 m zurück · orthogonale Ansichten aus dem 3D-Modell

E3 · NICHT FESTGELEGT

Vorderfassade (Platzseite)



Rückfassade (Stellplatzseite)

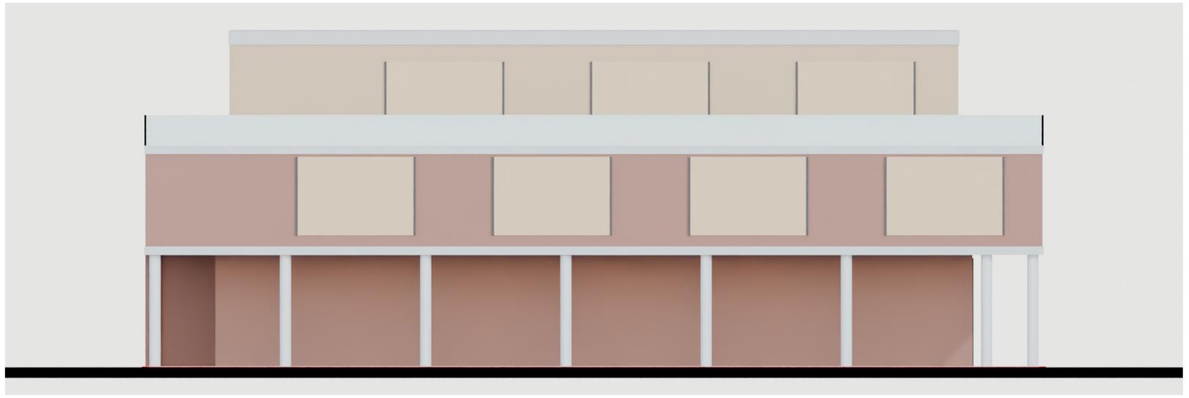

Seitenfassade West



Seitenfassade Ost



E3: Gebäudeschnitt mit Geschosshöhen und 3D-Ansicht

E3 – Staffel 3,00 m zurück

E3 · NICHT FESTGELEGT


E3: Schnitt bei x = 16.25 m mit Geschosshöhen (schematisch)


Platzseite links, Rückseite rechts · Höhenbezug ±0,00 = OK Fertigfußboden EG (Planbezug Blatt 14) – Bezugspunkt der Stadt für die 12,00 m ist NICHT belegt



Geschosshöhen: EG 4,30 m · 1. OG 3,60 m · 2. OG 3,60 m · Dach/Attika 0,50 m = 12,00 m. Reserve 0,00 m: Aufzugsüberfahrt, Dachaufbauten und Messtoleranz wären zusätzlich zu klären.

Säulen im Schnitt: 1 (Achse x ≈ 15 m) · Säulen insgesamt: 23 · Stellplatz-Decke Vorbau-Unterkante +3,85 m

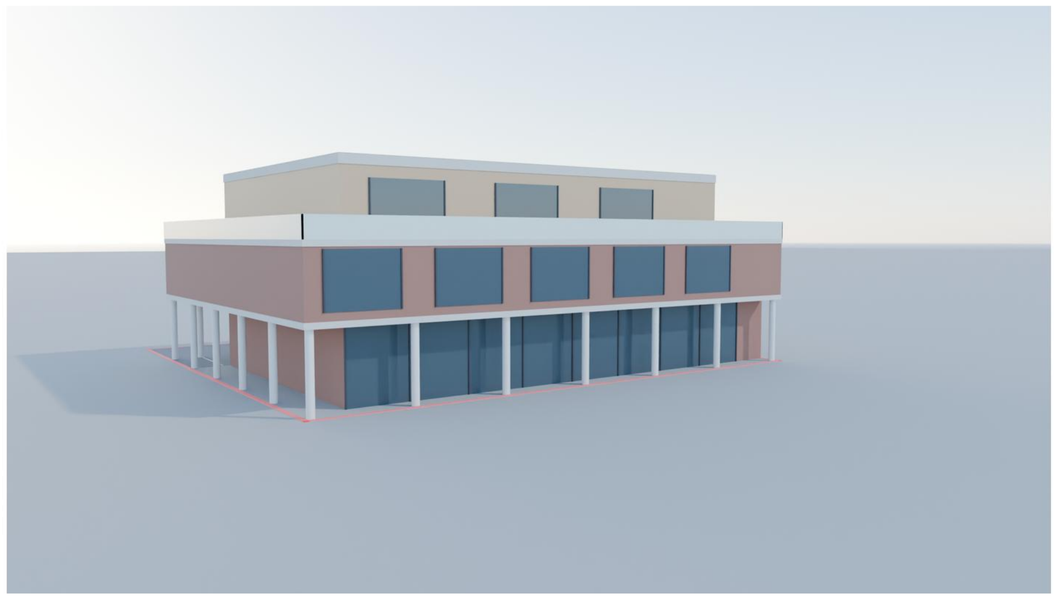


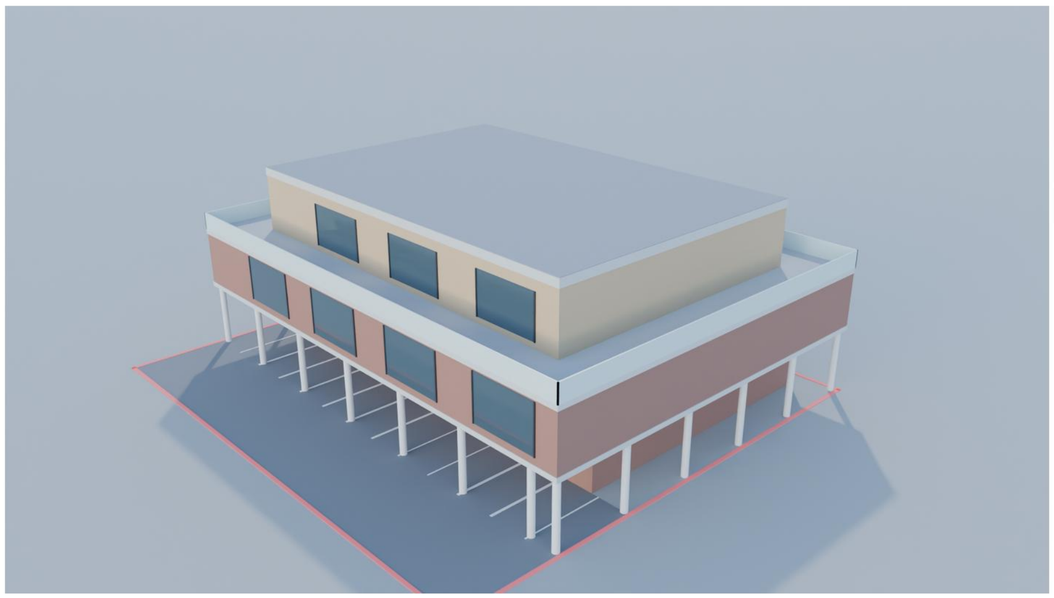

E4 – zweireihiges Parken, kleineres EG

Entwurfsstudie Baufeld 3 · Konzeptvariante, keine Genehmigungsplanung

E4 · NICHT FESTGELEGT

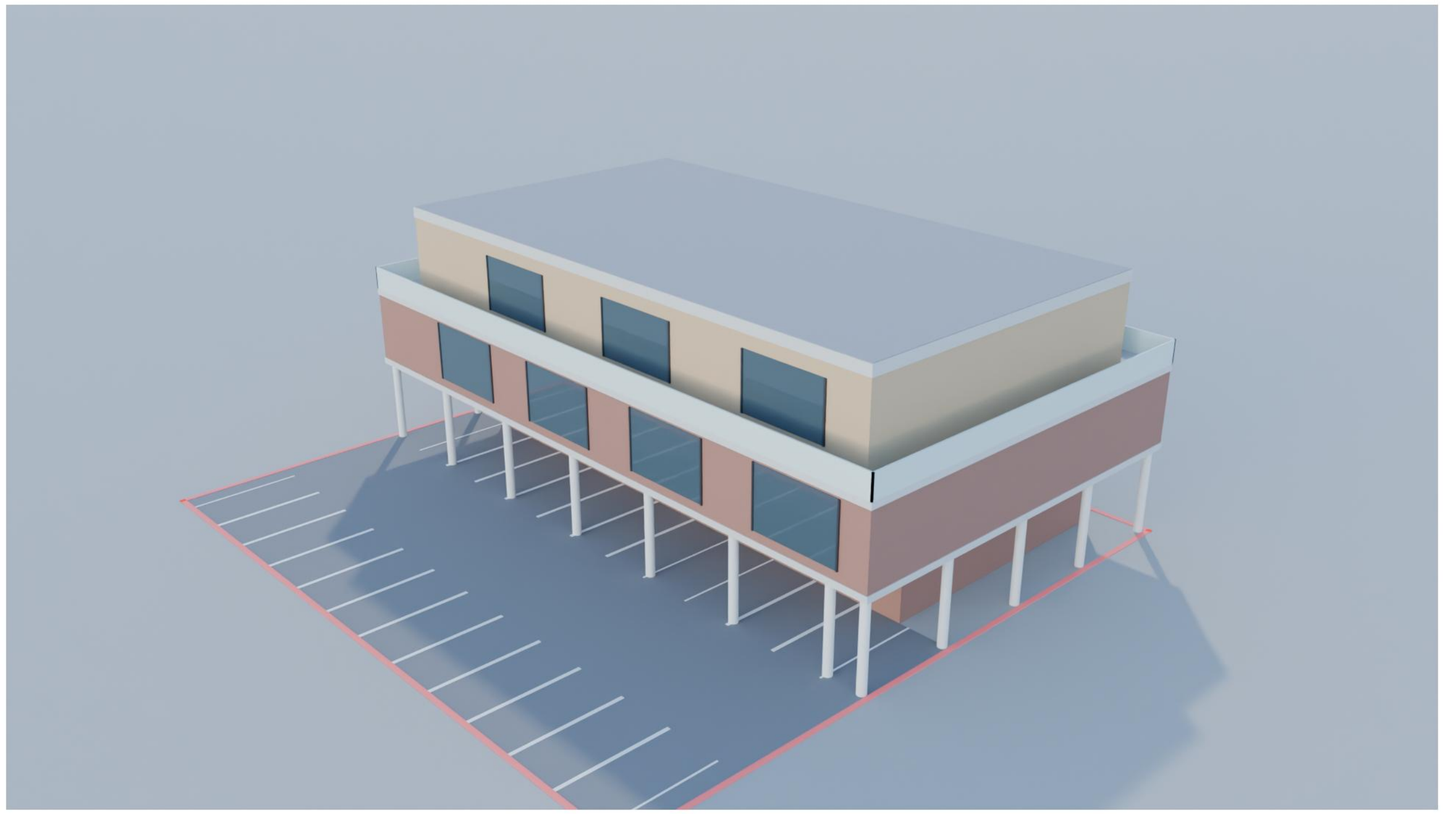

Wie E2, aber Erdgeschoss nur 14 m tief: zwei Stellplatzreihen (eine unter dem 5-m-Vorbau hinten, eine frei) mit 6-m-Fahrgasse dazwischen; dafür weniger Gewerbefläche.

Kennzahl	Wert (vorläufig)
Höhe	12,00 m Attika (EG 4,30 · 1. OG 3,60 · 2. OG 3,60 · Dach/Attika 0,50 m), 3 Geschosse
Grundfläche EG / 1. OG / 2. OG	358 / 608 / 464 m²
Außenmaße EG / 1. OG / 2. OG	29.5 × 12.5 / 32.0 × 19.0 / 29.0 × 16.0 m
Wohnfläche netto (geschätzt)	727 m² (1. OG 419 + 2. OG 308)
Wohnungen (Standardmix)	16 WE (9 + 7), 38–52 m², Ø 45 m²
Wohnungen anderer Mix	klein 19 WE (Ø 38 m²) · groß 12 WE (Ø 61 m²)
Säulen	21 Säulen Ø 0,40 m, Raster Rückseite 5,0 m (= 2 Stellplätze)
Stellplätze	22 (Reihe 1: 10, Reihe 2: 12); Bedarf ca. 42,6
Ein-/Ausfahren (geometrisch)	alle Plätze frei erreichbar
Überstand über Grundstück H1	0,00 m (Außenkante OG auf Grenze)

Alle Maße sind Planungsannahmen: Stellplatz 2,50 × 5,00 m, Fahrgasse 6,00 m, Säule Ø 0,40 m, Grundstück 32 × 30 m (Hypothese, tatsächlicher Zuschnitt unbestätigt), Zufahrt von Osten (Annahme). Wohnfläche = 0,88 × Wohnstreifen, schematisch. Nichts ist genehmigt, bemessen oder abgestimmt.


E4: Lageplan mit Gebäude, Säulen, Zufahrt und Stellplätzen

E4 – zweireihiges Parken, kleineres EG

E4 · NICHT FESTGELEGT

Lageplan E4 – Gebäude, Säulen, Zufahrt und Stellplätze

Grundstück H1 32 × 30 m HYPOTHETISCH (tatsächlicher Zuschnitt Baufeld 3 liegt nicht vor) · Stellplatz 2,50 × 5,00 m, Fahrgasse 6,00 m = Planungsannahmen · Zufahrt von Osten = Annahme

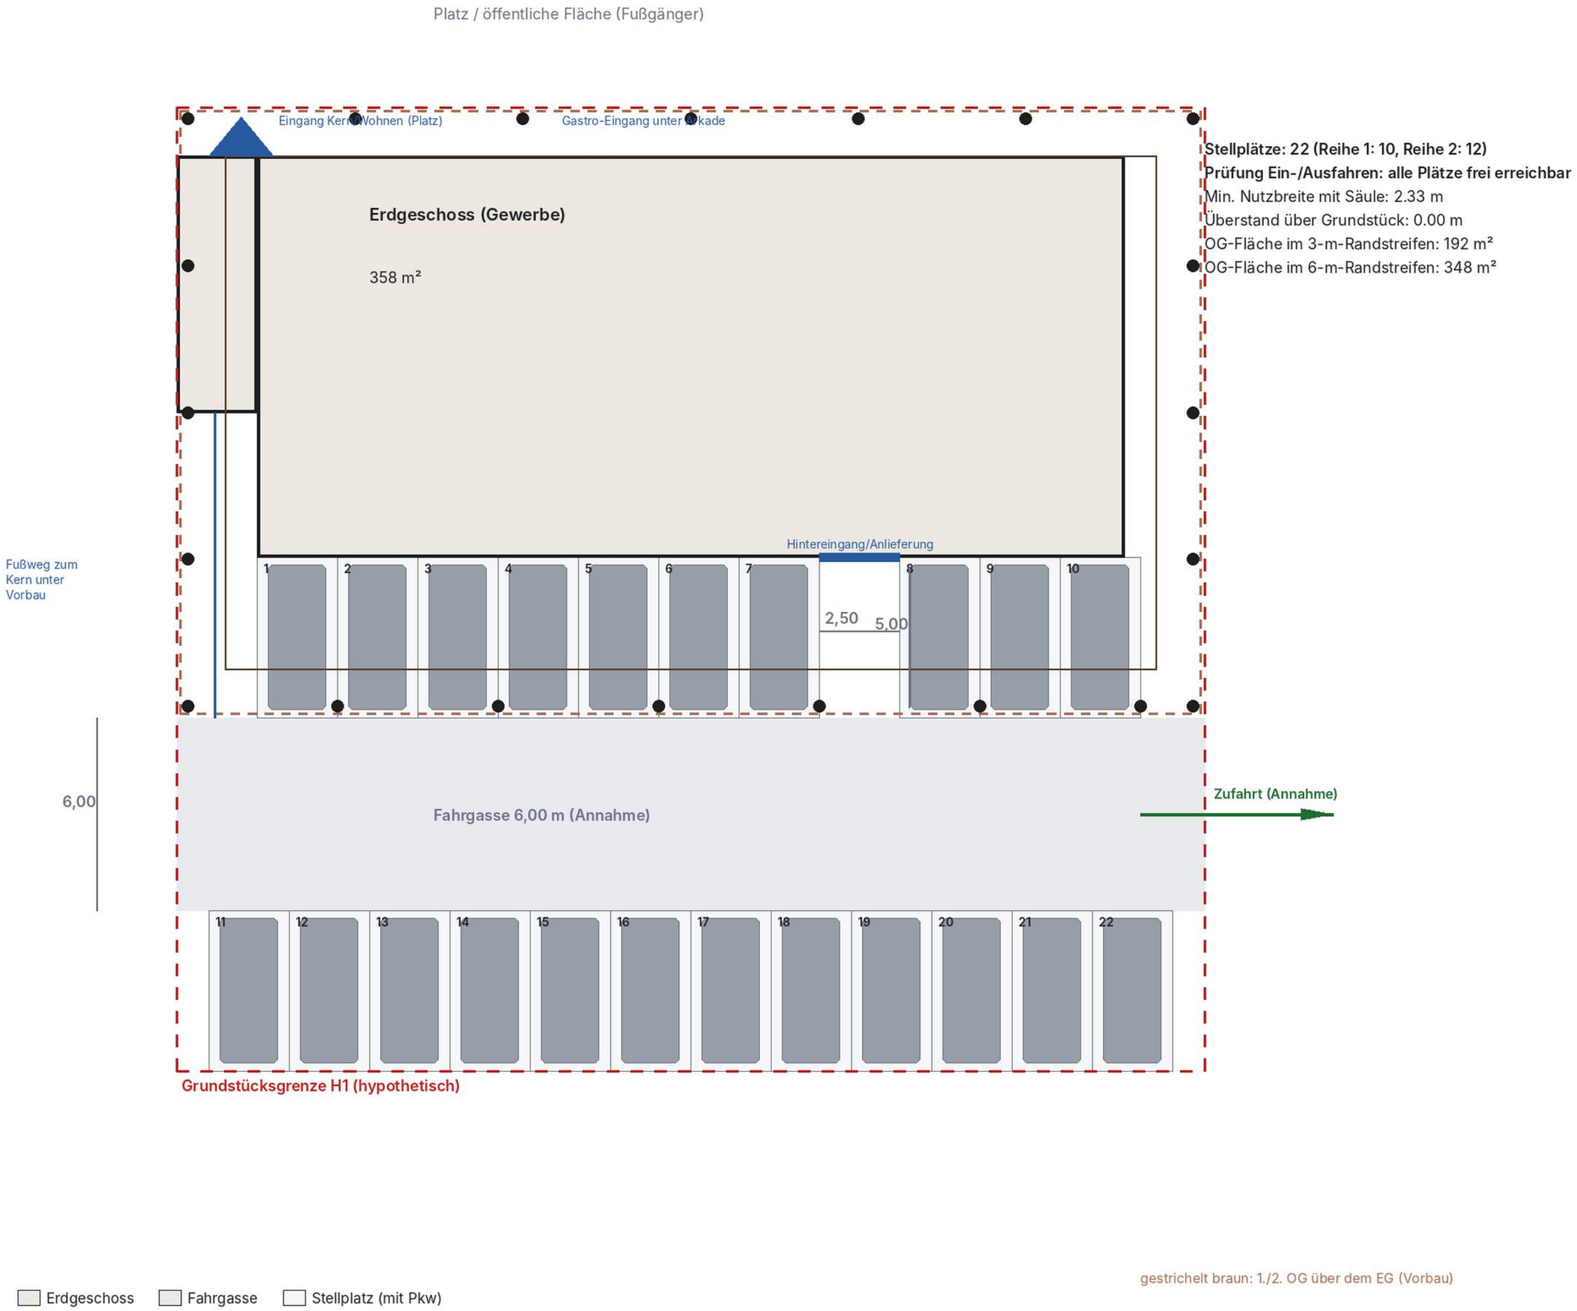

Parkprüfung	
Stellplätze	22
Ein-/Ausfahren	frei
Fahrgasse	6,00 m (Annahme)
Min. Nutzbreite mit Säule	2.33 m
Überstand H1	0,00 m

- vereinfachte Geometrieprüfung (Rechteckfreiraum 6,00 m vor 5,00 m tiefen 90°-Stellplätzen), keine Schleppkurven-Simulation
- Säulen (Ø 0,40 m) auf der Stellplatzgrenze: Nutzbreite 2,50 − 0,20 = 2,30 m je Platz (Mindestmaß/Stellplatzverordnung prüfen)
- Zufahrt von Osten ist Annahme (Lage der Erschließungsstraße unbekannt)
- Lücke zwischen Platz 7 und 8 (x 20,0–22,5): Stellplatz entfällt für Hintereingang/Anlieferung Gewerbe; Fußweg zum Kern an der Westseite (x 0–2,5) unter dem Vorbau


E4: Grundrisse EG, 1. OG, 2. OG

E4 – zweireihiges Parken, kleineres EG · schematisch

E4 · NICHT FESTGELEGT

Erdgeschoss

E4: Erdgeschoss (schematisch)
Grundriss schematisch · Wohnungsaufteilung = Streifenmodell (Mittelgang 2,0 m), netto = 0,88 × brutto · Säulen Ø 0,40 m · Grundstück H1 hypothetisch

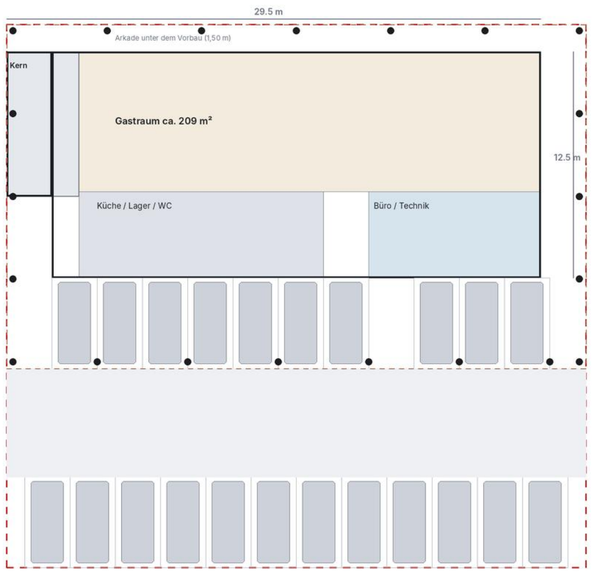


Fläche Geschoss 358 m²

Wohnung (schematisch) Kern Gastronomie Terrasse/Dach schraffiert

1. Obergeschoss

E4: 1. Obergeschoss (schematisch)
Grundriss schematisch · Wohnungsaufteilung = Streifenmodell (Mittelgang 2,0 m), netto = 0,88 × brutto · Säulen Ø 0,40 m · Grundstück H1 hypothetisch

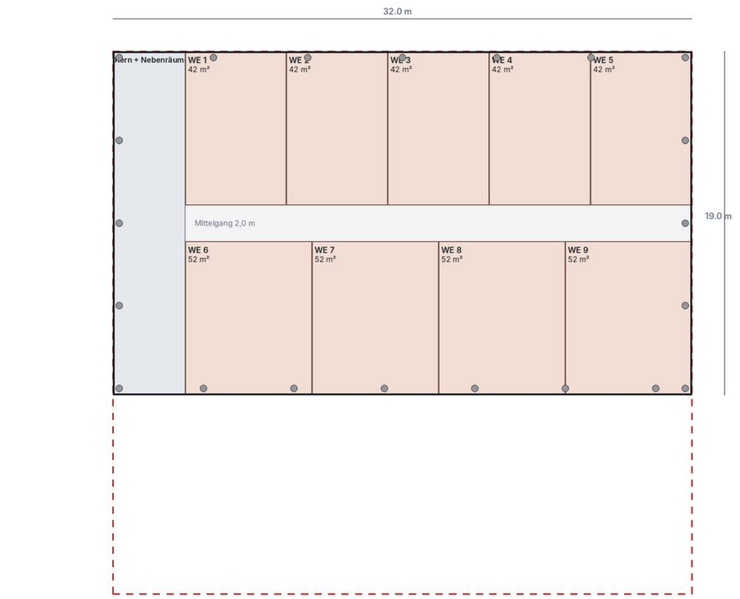


Fläche Geschoss 608 m²

Wohnung (schematisch) Kern Gastronomie Terrasse/Dach schraffiert

2. Obergeschoss

E4: 2. Obergeschoss (Staffel) (schematisch)
Grundriss schematisch · Wohnungsaufteilung = Streifenmodell (Mittelgang 2,0 m), netto = 0,88 × brutto · Säulen Ø 0,40 m · Grundstück H1 hypothetisch

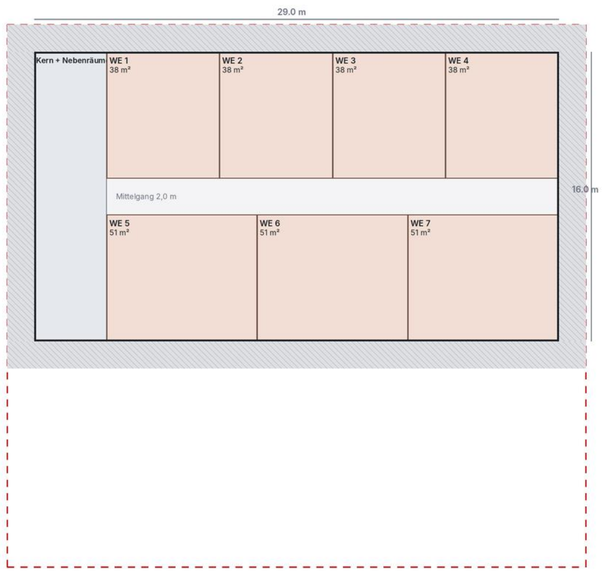

Fläche Geschoss 464 m²

Wohnung (schematisch) Kern Gastronomie Terrasse/Dach schraffiert

E4: vier Fassaden


E4 – zweireihiges Parken, kleineres EG · orthogonale Ansichten aus dem 3D-Modell

E4 · NICHT FESTGELEGT

Vorderfassade (Platzseite)



Rückfassade (Stellplatzseite)

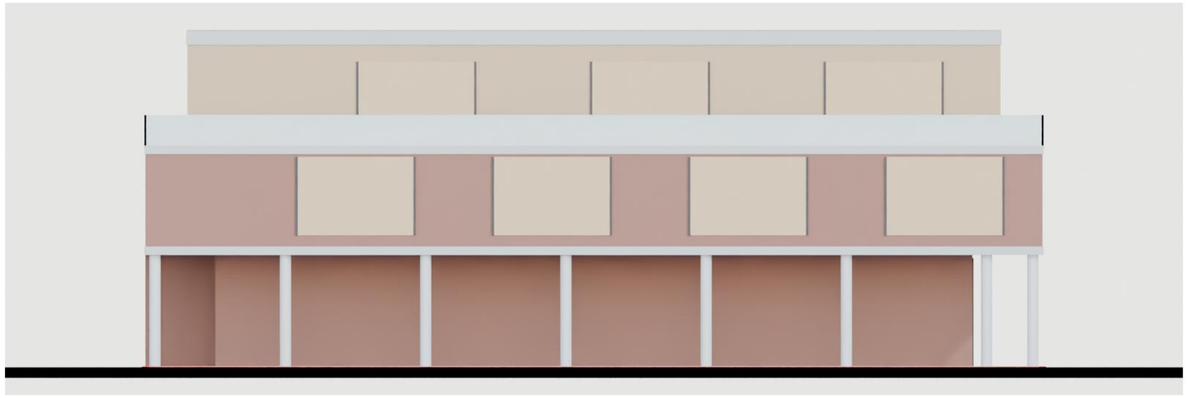

Seitenfassade West



Seitenfassade Ost




E4: Gebäudeschnitt mit Geschosshöhen und 3D-Ansicht

E4 – zweireihiges Parken, kleineres EG

E4 · NICHT FESTGELEGT


E4: Schnitt bei x = 16.25 m mit Geschosshöhen (schematisch)


Platzseite links, Rückseite rechts · Höhenbezug ±0,00 = OK Fertigfußboden EG (Planbezug Blatt 14) – Bezugspunkt der Stadt für die 12,00 m ist NICHT belegt

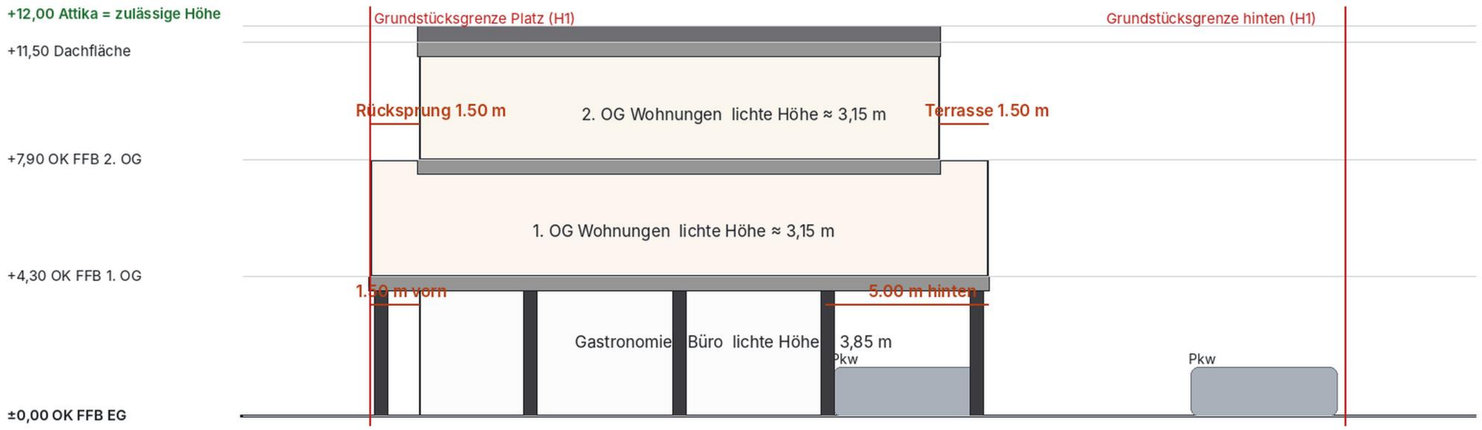

Geschosshöhen: EG 4,30 m · 1. OG 3,60 m · 2. OG 3,60 m · Dach/Attika 0,50 m = 12,00 m. Reserve 0,00 m: Aufzugsüberfahrt, Dachaufbauten und Messtoleranz wären zusätzlich zu klären.

Säulen im Schnitt: 1 (Achse x ≈ 15 m) · Säulen insgesamt: 21 · Stellplatz-Decke Vorbau-Unterkante +3,85 m

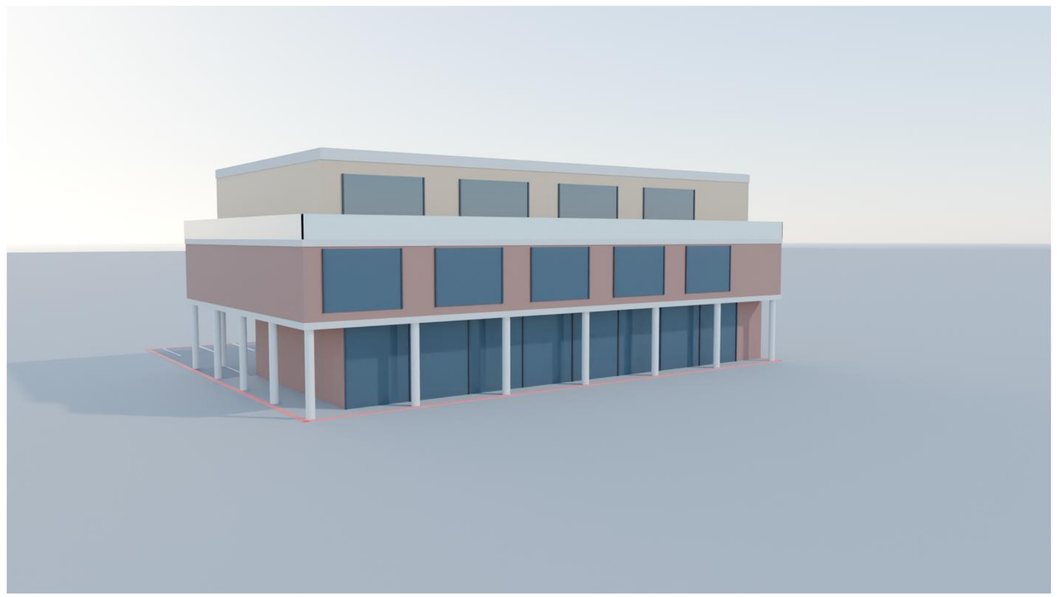

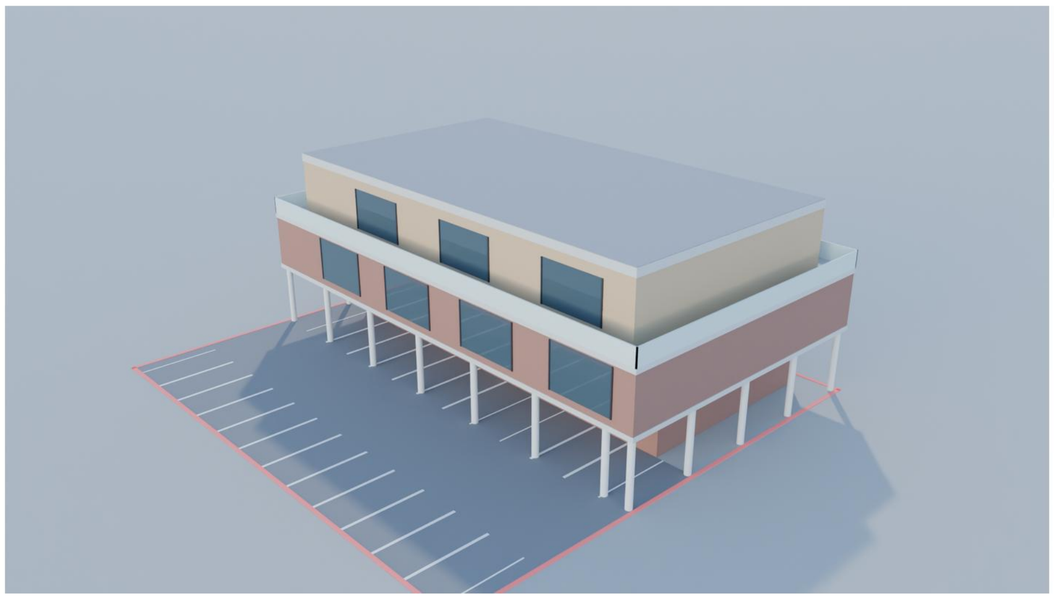

Baurechtliche Ampel E1–E4 (vorläufig)

VARIANTE E · NICHT FESTGELEGT

Keine Rechtsprüfung · alles bis zur Klärung von Grundstück, Baugrenzen und Satzungen offen

Kriterium	E1	E2	E3	E4
Gebäudehöhe max. 12,00 m	zu prüfen: Attika +12,00 m = Grenzwert, Reserve 0,00 m; Höhenbezug der Stadt unbelegt, Aufzugsüberfahrt/Dachaufbauten zusätzlich.	zu prüfen: Attika +12,00 m = Grenzwert, Reserve 0,00 m; Höhenbezug der Stadt unbelegt, Aufzugsüberfahrt/Dachaufbauten zusätzlich.	zu prüfen: Attika +12,00 m = Grenzwert, Reserve 0,00 m; Höhenbezug der Stadt unbelegt, Aufzugsüberfahrt/Dachaufbauten zusätzlich.	zu prüfen: Attika +12,00 m = Grenzwert, Reserve 0,00 m; Höhenbezug der Stadt unbelegt, Aufzugsüberfahrt/Dachaufbauten zusätzlich.
Geschosse (2–3)	zu prüfen: 3 Geschosse; 2. OG = 100 % des 1. OG – Vollgeschoss-Frage (NBauO/B-Plan) klären. Traufhöhe 6,50 m (project_brief) bei +7,90 m Vorbau-Oberkante prüfen.	zu prüfen: 3 Geschosse; 2. OG = 79 % des 1. OG – Vollgeschoss-Frage (NBauO/B-Plan) klären. Traufhöhe 6,50 m (project_brief) bei +7,90 m Vorbau-Oberkante prüfen.	zu prüfen: 3 Geschosse; 2. OG = 61 % des 1. OG – Vollgeschoss-Frage (NBauO/B-Plan) klären. Traufhöhe 6,50 m (project_brief) bei +7,90 m Vorbau-Oberkante prüfen.	zu prüfen: 3 Geschosse; 2. OG = 76 % des 1. OG – Vollgeschoss-Frage (NBauO/B-Plan) klären. Traufhöhe 6,50 m (project_brief) bei +7,90 m Vorbau-Oberkante prüfen.
GRZ / überdeckte Fläche	zu prüfen: Größte Geschossprojektion 768 m² = 80 % von 960 m² (theoretisch GRZ 0,6 = 576 m², Kappung 0,8 angenommen; Anrechnung überdeckter Stellplätze ungeklärt).	zu prüfen: Größte Geschossprojektion 768 m² = 80 % von 960 m² (theoretisch GRZ 0,6 = 576 m², Kappung 0,8 angenommen; Anrechnung überdeckter Stellplätze ungeklärt).	zu prüfen: Größte Geschossprojektion 768 m² = 80 % von 960 m² (theoretisch GRZ 0,6 = 576 m², Kappung 0,8 angenommen; Anrechnung überdeckter Stellplätze ungeklärt).	zu prüfen: Größte Geschossprojektion 608 m² = 63 % von 960 m² (theoretisch GRZ 0,6 = 576 m², Kappung 0,8 angenommen; Anrechnung überdeckter Stellplätze ungeklärt).
Baugrenzen / Grundstücksgrenzen	zu prüfen: Außenkante der Obergeschosse liegt auf der angenommenen Grenze (0,00 m Überstand), Säulen 0,35 m innen; 222 m² (3 m) bzw. 408 m² (6 m) des 1. OG lägen im Abstandsszenario – Baugrenze/Abstandsflächen/Grenzbebauung ungeklärt.	zu prüfen: Außenkante der Obergeschosse liegt auf der angenommenen Grenze (0,00 m Überstand), Säulen 0,35 m innen; 222 m² (3 m) bzw. 408 m² (6 m) des 1. OG lägen im Abstandsszenario – Baugrenze/Abstandsflächen/Grenzbebauung ungeklärt.	zu prüfen: Außenkante der Obergeschosse liegt auf der angenommenen Grenze (0,00 m Überstand), Säulen 0,35 m innen; 222 m² (3 m) bzw. 408 m² (6 m) des 1. OG lägen im Abstandsszenario – Baugrenze/Abstandsflächen/Grenzbebauung ungeklärt.	zu prüfen: Außenkante der Obergeschosse liegt auf der angenommenen Grenze (0,00 m Überstand), Säulen 0,35 m innen; 192 m² (3 m) bzw. 348 m² (6 m) des 1. OG lägen im Abstandsszenario – Baugrenze/Abstandsflächen/Grenzbebauung ungeklärt.
Stellplätze	kritisch / offen: 10 Plätze gezeichnet gegenüber Bedarf ca. 52,5 – Defizit 42,5; Ablöse/Tiefgarage/Nachbarfläche zu klären.	kritisch / offen: 10 Plätze gezeichnet gegenüber Bedarf ca. 49,5 – Defizit 39,5; Ablöse/Tiefgarage/Nachbarfläche zu klären.	kritisch / offen: 10 Plätze gezeichnet gegenüber Bedarf ca. 48,0 – Defizit 38,0; Ablöse/Tiefgarage/Nachbarfläche zu klären.	kritisch / offen: 22 Plätze gezeichnet gegenüber Bedarf ca. 42,6 – Defizit 20,6; Ablöse/Tiefgarage/Nachbarfläche zu klären.
Gewerbe im EG	zu prüfen: EG 492 m² statt 576 m² bei B3 (-84 m²); Gastro-/Büro-Programm anpassen.	zu prüfen: EG 492 m² statt 576 m² bei B3 (-84 m²); Gastro-/Büro-Programm anpassen.	zu prüfen: EG 492 m² statt 576 m² bei B3 (-84 m²); Gastro-/Büro-Programm anpassen.	zu prüfen: EG 358 m² statt 576 m² bei B3 (-218 m²); Gastro-/Büro-Programm anpassen.
Brandschutz / Rettungswege	zu prüfen: Vorbau über Stellplätzen/Fahrgasse, Feuerwehrzufahrt und Aufstellflächen, Gebäudeklasse 4/5 – Konzept erforderlich.	zu prüfen: Vorbau über Stellplätzen/Fahrgasse, Feuerwehrzufahrt und Aufstellflächen, Gebäudeklasse 4/5 – Konzept erforderlich.	zu prüfen: Vorbau über Stellplätzen/Fahrgasse, Feuerwehrzufahrt und Aufstellflächen, Gebäudeklasse 4/5 – Konzept erforderlich.	zu prüfen: Vorbau über Stellplätzen/Fahrgasse, Feuerwehrzufahrt und Aufstellflächen, Gebäudeklasse 4/5 – Konzept erforderlich.

Offene Fragen und Prüfbedarf

VARIANTE E · NICHT FESTGELEGT

Was vor jeder Weiterentwicklung geklärt werden muss

- Tatsächlicher Grundstückszuschnitt, Baugrenzen, Abstandsflächen (bei 12 m Höhe: Grundregel 0,5 H = 6 m, ggf. reduziert), Grenzbebauung/Baulast.
- Höhenbezugspunkt der 12,00 m; Traufhöhe 6,50 m; Dachform; Vollgeschoss-Definition für das 2. OG (E3: 61 % des 1. OG).
- GRZ und Anrechnung überdeckter Stellplätze/Fahrgasse (Kappungsgrenze 0,8 angenommen); E1–E3 liegen exakt bei 768 m² = 0,80.
- Stellplatzbedarf ≈ 50 (Ansatz 1,5/WE, Gastro 1/10 m², Büro 1/30 m²) gegenüber 10–22: Satzung, Ablöse, Tiefgarage, Mitbenutzung öffentlicher Parkplätze.
- Zufahrt: Lage der Straße, Gefälle, Sichtdreiecke, Feuerwehrzufahrt/Aufstellflächen unter dem Vorbau.
- Statik: Kragarme 1,50 m (Arkade vorn), 2,50 m (Seiten), 5,00 m (hinten), Säulenraster 5,0 m, Fundamente, Auskragung bei drei Geschossen (Lasten aus 2 Wohngeschossen).
- Brandschutz: Vorbau über Stellplätzen/Fahrgasse, Rettungswege, Geschosshöhen > 7 m OK Fußboden prüfen (Gebäudeklasse).
- Gewerbe-EG schrumpft (492 bzw. 358 m² statt 576 m²): Gastro-/Büro-Programm und Pachtertrag neu bewerten.
- Förderung: nicht neu bewertet; Wohnungsgrößen s. Förder-PDF der Variantenstudie.

Nächster Schritt: Unterlagen zum Grundstück (siehe Seite „Benötigte Unterlagen“) bereitstellen; danach Auswahl bzw. Kombination der Teilvarianten durch den Auftraggeber. Keine Variante ist ausgewählt.