
Ansicht Platzfassade – Arbeitsstand OG-2

Ansicht M 1:150 · Fensterlage schematisch, Fenstermaße sind noch nicht festgelegt

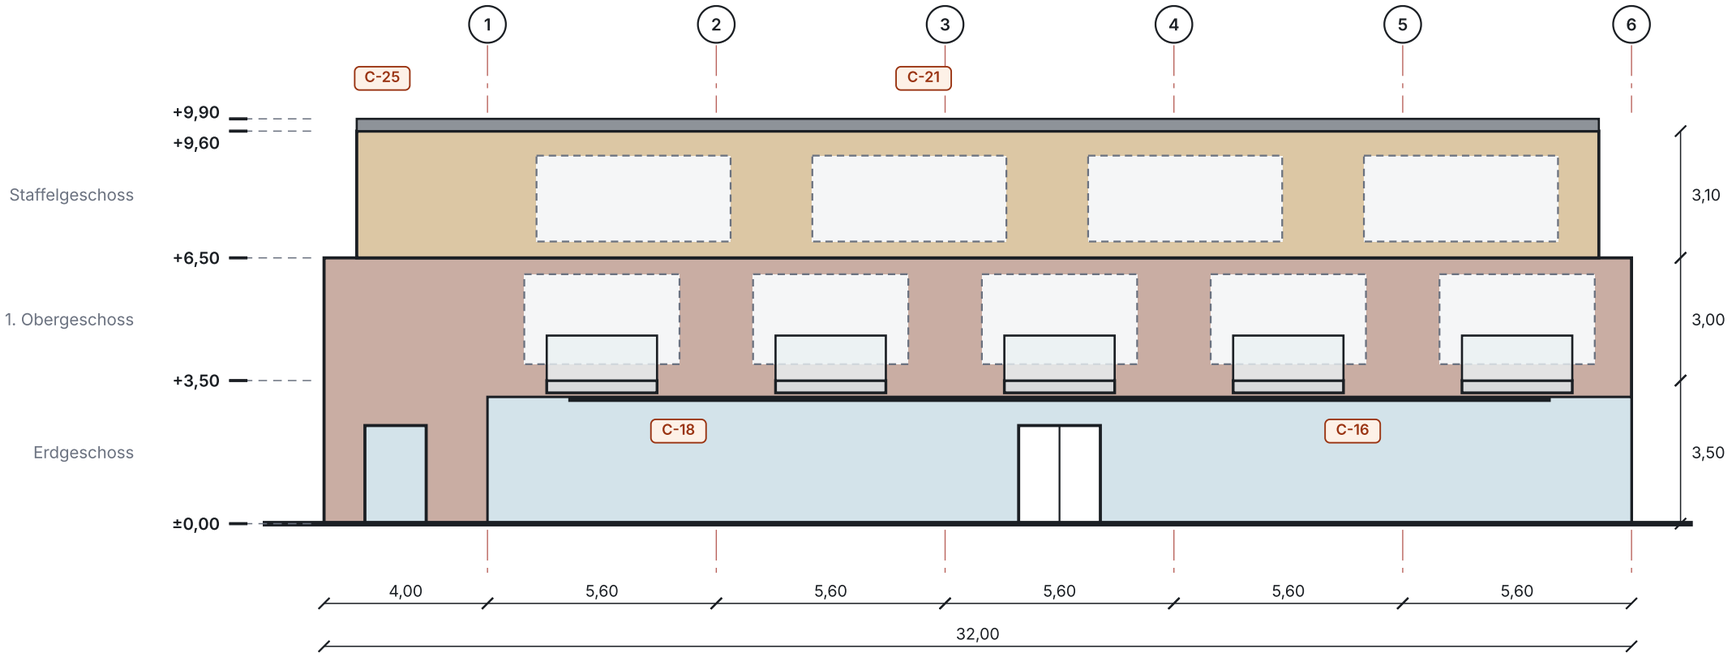

Maßstab 1:150

0 5 m

KENNZAHLEN

Gebäudebreite	**32,00 m**
Höhe Attika	**9,90 m**
Traufhöhe nach B-Plan	**6,50 m**

LEGENDE

- Klinker (dunkelrotbraun, hier aufgehellt dargestellt)
- Betonbalkonplatte
- Milchglas-Brüstung, 1,10 m
- Glasfront und Türen im Erdgeschoss
- Lärchenholz Staffelgeschoss
- Fensterlage schematisch (Maße offen)
- Stahlvordach (Annahme, Unterseite +3,00)

OFFENE PUNKTE (NICHT GELÖST)

- C-16 Stützen oder Träger in der 28 m langen Glasfront nicht nachgewiesen.
- C-18 Stahlvordach liegt unter den Balkonplatten.
- C-21 Staffel: Entwurf 4 Achsen, 1. OG 5, Renderings 7.
- C-25 Aufzug: Überfahrt über die Attika offen.
- C-03 Höhenmessregel der Stadt unbestätigt.

HINWEISE

Platzfassade mit fünf Balkonen im 1. OG. Staffelgeschoss 0,80 m zurückgesetzt, hier nicht sichtbar.

Flächen netto = Brutto × 0,88 (Annahme).

Himmelsrichtung unbekannt (C-13). Förderthemen sind nicht Gegenstand dieses Blatts.

Neue Mitte Werlte · Baufeld 3

Bauvorhaben: Restaurant und Bar, Büros, Wohnungen

Ansicht Platzfassade – Arbeitsstand OG-2

Maßstab 1:150 (A3)

Stand 22.10.2026 · Modell NEUE_MITTE_MASTER_DRAFT_A_003

VORLÄUFIGER ARBEITSSTAND – nicht freigegeben