Vergleich der Varianten B, C, E1–E4 und F1–F4

VERGLEICH · NICHT FESTGELEGT

Entwurfsstudie Baufeld 3 · alle Werte vorläufig · keine Variante festgelegt

Ziel: Gebäudehöhe bis 12,00 m planerisch ausnutzen (drei Geschosse, keine zusätzlichen), umlaufender säulengestützter Vorbau, Zufahrt und Stellplätze unter und neben dem Vorbau. Keine Variante ist festgelegt; B3 (Variante A) und alle bestehenden Modelle bleiben unverändert. Alle Flächen sind vorläufig, bis Grundstücksgrenzen und Baugrenzen verlässlich geklärt sind.

	Bestätigt (Quelle)	Annahme / unbestätigt
Grundstück	ca. 960 m²; B-Plan 123 rechtskräftig 2023: Baufeld 3 vermutlich MI 3 / Flurstück 59/1 mit Baugrenzen 10,0 m West, 3 m übrige Seiten	Zuschnitt 32 × 30 m = Hypothese H1; Planausschnitt: ≈ 42,3 × 22,7 m (geschätzt), Baufenster ≈ 27,7 × 15,9 m (abgeleitet); Foto-Seiten fehlen
Höhe / Geschosse	Plan A rechtskräftig 2023 (MI 3): II–III, TH 9,80 m, H 15,00 m; Plan B Entwurf 2026 (MI 2/Änderung): II zwingend, TH 6,50 m, H 12,00 m; beide: Dach ≥ 38°, Bezug OK Fahrbahn	Baufeld 3 nicht bestätigt; Fahrbahnhöhe unbekannt; Befreiungen (Dach, Baugrenze, TH) offen
Stellplätze Wohnen	KEINE gesetzliche Pflicht seit 01.07.2024 (§ 47 Abs. 1 Satz 3 NBauO; FAQ Land Niedersachsen Stand 11.07.2025)	ob B-Plan/städtebaulicher Vertrag/Kaufvertrag Stellplätze für Wohnungen verlangt: unbekannt
Stellplätze Gastro/Büro	Pflicht besteht; Bemessung bedarfsorientiert (Richtzahlen Erlass: Gaststätte 1 je 8–12 Sitzplätze, Büro 1 je 30–40 m²)	Gaststättenart („örtliche Bedeutung“) und Sitzplatzzahl angenommen
Maße	–	Stellplatz 2,50 × 5,00 m, Fahrgasse 6,00 m, Säule Ø 0,40 m (Vorgaben/Annahmen), Zufahrtslage
Wohnfläche	B3: 846 m², 16 WE (Plan)	übrige Varianten aus Geschosskonturen geschätzt (0,88 × Wohnstreifen)

Grundstück, Baugrenzen und Quellenstatus

VERGLEICH · NICHT FESTGELEGT

Was gesichert ist, was nur aus Beschreibungen stammt und was Hypothese ist

Punkt	Stand	Herkunft / Bemerkung
Grundstücksfläche ca. 960 m²	GESICHERT (Projektangabe)	Projektunterlagen/Auftraggeber; nicht am Liegenschaftsnachweis geprüft
Zuschnitt 32 × 30 m (Variantenstudie E/F)	HYPOTHESE H1	nur aus 960 m² und B3-Annahme; widerspricht dem Planausschnitt: Flurstück 59/1 ≈ 42,3 × 22,7 m (geschätzt), Baufenster ≈ 27,7 × 15,9 m (abgeleitet)
B-Plan Nr. 123 „Ehemalige Grundschule“, 1. Änderung (Entwurf 25.09.2026): MI, GRZ 0,6, II zwingend, TH 6,50 m, H 12,00 m, SH 0,30 m, Baugrenze 3 m	GESICHERT (Entwurf)	amtliche Unterlagen der Stadt Werlte (sgwerlte.de), in quellen_stadt/ abgelegt; nicht rechtskräftig
Foto-Seiten 13/15/16 des Auftraggebers („zwei- bis dreigeschossig“)	FEHLEN	ZIP nicht angekommen; Seite 15/16 entsprechen vermutlich Abb. 2/3 der 1. Änderung (unbestätigt)
Zuordnung „Baufeld 3“ im Nutzungskonzept	INDIZ: MI 3 / Flurstück 59/1	Fläche ≈ 960 m² und Z II–III passen; Seite 13 fehlt (unbestätigt)
Baugrenzen / Baulinien, GRZ, Abstandsflächen	UNBEKANNT	keine Maße am Plan abgelesen; alle Konturen in den Plänen sind Hypothese
Erschließungsstraße, Zufahrt, Platzseite	ANNAHME	Platz an der Seite y = 0; Zufahrt von Osten (E) bzw. Süden (F) angenommen
Stellplatz 2,50 × 5,00 m, Fahrgasse 6,00 m	ANNAHME (Auftraggeber, vorläufig)	Abgleich mit Stellplatzsatzung/Garagenverordnung ausstehend

Die ZIP-Datei mit den Fotos der Seiten 13, 15 und 16 ist in dieser Sitzung nicht angekommen; der Ordner quellen_stadt/fotos_stadt_unterlagen/ ist leer. Grundlage sind die amtlichen Planunterlagen der Stadt (Entwurf B-Plan 123, 1. Änderung). Konturen aus den Plänen sind als ABGELEITET/GESCHÄTZT gekennzeichnet, gesicherte Maße getrennt (siehe Entscheidungs-PDF).

Die zwei Planstände im Vergleich

ENTSCHEIDUNGSGRUNDLAGE · NICHTS FESTGELEGT


Fundstellen: Planzeichnung und textliche Festsetzungen (P23 / E26), Begründung 3.2–3.3


Merkmal	P23 MI 3 (und MI 1) – RECHTSKRÄFTIG 2023	P23 MI 2 – rechtskräftig 2023	E26 – 1. Änderung ENTWURF 2026
Rechtsstand	in Kraft seit 14.04.2023	in Kraft seit 14.04.2023	Entwurf, kein Satzungsbeschluss
Geltungsbereich	ganzes Plangebiet (1,27 ha), MI 3 = Flurstück 59/1	östlicher Block	ca. 3.874 m²; MI 3 liegt NICHT darin
Gebietsart / GRZ	Mischgebiet / 0,6	Mischgebiet / 0,6	Mischgebiet / 0,6
Vollgeschosse	II–III (Mindest-/Höchstmaß)	II zwingend	II zwingend
Traufhöhe TH	max. 9,80 m	max. 6,50 m	max. 6,50 m
Gebäudehöhe H	max. 15,00 m	max. 12,00 m	max. 12,00 m
Sockelhöhe SH	FFB EG ≤ 0,30 m über Bezugspunkt	wie MI 3	wie P23
Bezugspunkt	OK Fahrbahn der nächsten ausgebauten Erschließungsstraße, Mitte vor dem Baukörper; oben: OK Baukörper (First/Hauptgesims)	wie MI 3	wie P23
Dachform	Hauptdächer geneigt ≥ 38°; Flachdach nur Verbindungsbauten (≥ 1,0 m unter First), Wintergärten/untergeordnete Dachflächen ≤ 70 m²	wie MI 3	wie P23 (örtl. Bauvorschrift)
Bauweise	offen (bis 50 m)	offen	offen
Baugrenzen (MI 3)	10,0 m zur Marktstraße (W); 3 m Planstraße (N), 3 m Ost, 3 m Süd	an Baumstandorte orientiert	3,0 m zu Planstraße und Parkplatz
Stellplätze/Nebenanlagen	Garagen/Gebäude-Nebenanlagen entlang öffentl. Verkehrsflächen unzulässig; Baumreihe Marktstraße: Kronentraufbereich ohne Versiegelung	wie MI 3	öffentlicher Parkplatz 63 Plätze; Überdachung von Stellplätzen dort unzulässig
Fassade	Ziegelsichtmauerwerk nicht glasiert (Rot/Rotbraun), andere Materialien ≤ 1/2	wie MI 3	wie P23

Welches Grundstück ist Baufeld 3? (Indizien, UNBESTÄTIGT)

ENTSCHEIDUNGSGRUNDLAGE · NICHTS FESTGELEGT

Ausschnitt rechtskräftiger Plan 2023 (links) und Nutzungskonzept 2026 (rechts, Markierung = vermutete Lage)

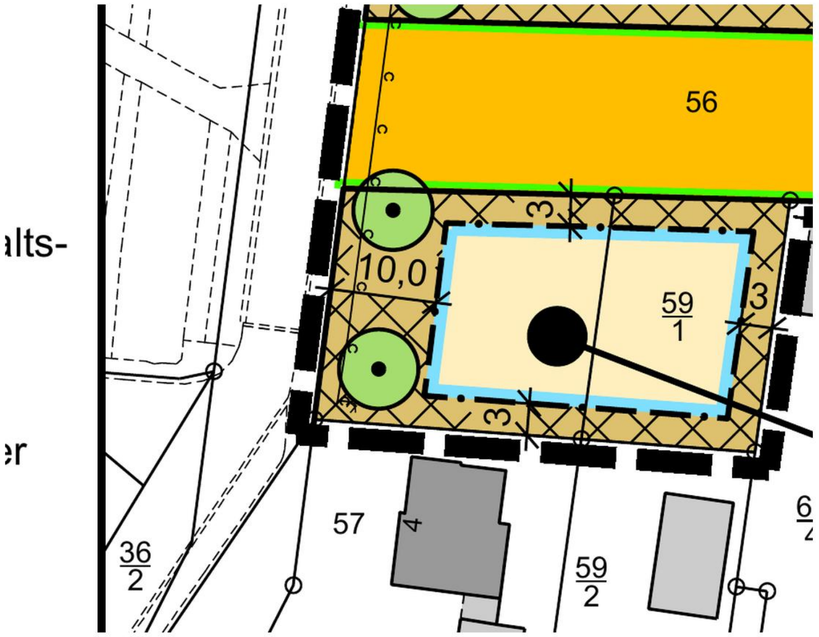

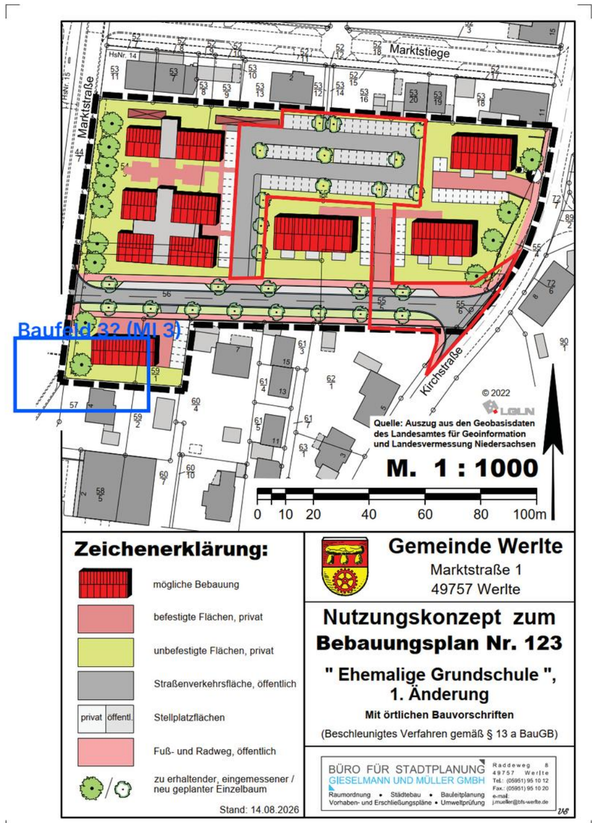

Indiz	Befund
Fläche	Flurstück 59/1 ≈ 960 m² (aus Planabbildung abgegriffen, ±3 %) = Projektangabe ca. 960 m²
Geschosse	MI 3: II–III = städtische Seite 13 „mindestens zwei, höchstens drei“ (MI 2: II zwingend – passt nicht)
Plan 2026	Änderungsbereich enthält MI 3 nicht → die „12,00 m“ der Seite 15 gelten für Baufeld 3 nicht
Gegenindiz	MI 1 hat ebenfalls II–III, H 15 m; die Baufeldnummern stehen in den geladenen Unterlagen nicht; Seite 13 fehlt
Folge	Bestätigung durch den Auftraggeber nötig (Foto Seite 13 / Baufeldplan)

Grundstücksmaße und Risiken: gesichert, abgeleitet, geschätzt

ENTSCHEIDUNGSGRUNDLAGE · NICHTS FESTGELEGT


Keine verbindlichen Grundstücksmaße aus einer abgebildeten/fotografierten Plankarte – amtlicher Lageplan erforderlich

Angabe	Wert	Status	Herkunft / Risiko
Baugrenzabstände MI 3	10,0 m W; 3 m N/O/S	GESICHERT (im Plan bemaßt)	Planzeichnung P23
Planstraße	16,0 m Querschnitt	GESICHERT	Begründung 3.3
Höhen, Z, GRZ, Dach, Bezugspunkt	siehe Planstände	GESICHERT (P23 rechtskräftig)	Textliche Festsetzungen 1.2, 2.2
Baufenster MI 3	≈ 27,7 × 15,9 m = 439 m²	ABGELEITET (Vektorplan 1:1000)	Polygon aus der PDF-Geometrie; Plan leicht gegen Nord gedreht; nicht vermessen
Flurstück 59/1	≈ 42,3 × 22,7 m ≈ 960 m²	GESCHÄTZT (±3 %)	aus der Planabbildung gemessen; Grenzen nur grafisch (Liegenschaftskarte Stand 08.06.2022)
Fahrbahnhöhe (Bezugspunkt)	unbekannt	FEHLT	Bauamt der Stadt Werlte (laut Festsetzung 1.2 erfragbar)
Amtlicher Lageplan / Vermessung	–	FEHLT	ÖbVI Dipl.-Ing. Jörg Jüngerink (Plan-Az. 22-7003); Gebäude in der Nutzung ist Stand 2022
Baumreihe Marktstraße	Kronen-/Wurzelschutz	GESICHERT (Festsetzung)	schränkt Stellplätze/Zufahrt im Westen ein; Kronendurchmesser unbekannt
Zufahrt/Ausfahrt zur Planstraße	–	ANNAHME	Lage, Sichtdreiecke, Gehwege (16 m Querschnitt) ungeklärt

Lageplan Flurstück 59/1: Baufenster und Fußabdrücke der Varianten

ENTSCHEIDUNGSGRUNDLAGE · NICHTS FESTGELEGT

Alle EG-Fußabdrücke aus F, E, B3 passen NICHT in das Baufenster · Umrisse an der Baufensterecke ausgerichtet · Maße abgeleitet/geschätzt

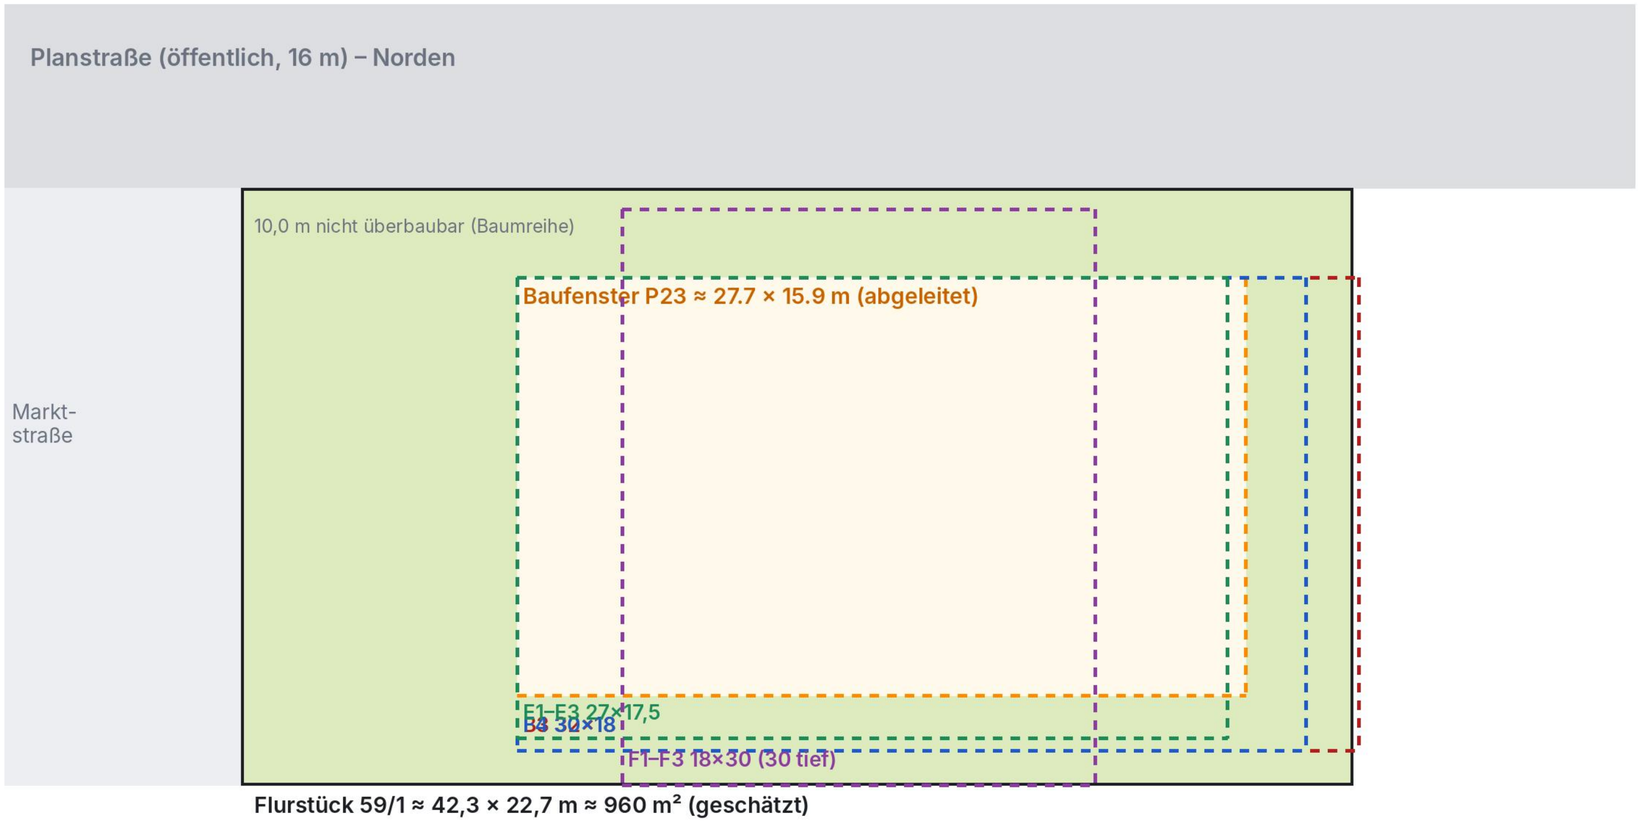

EG-Fußabdruck	Baufenster 27,7 × 15,9
B3 / A–D: 32 × 18 m	passt NICHT
E1–E3: 27 × 17,5 m	passt NICHT
E4: 27 × 12,5 m	passt
F1–F3: 18 × 30 m	passt NICHT
F4: 30 × 18 m	passt NICHT
G1: 27,7 × 15,9 m	passt


Zusätzlich: EG 540 m² übersteigt das Baufenster (439 m²) um 101 m² (+23 %). Die GRZ 0,6 erlaubt rechnerisch 576 m² Grundfläche – begrenzend wirkt die Baugrenze. Ein Vorbau über die Baugrenze hinaus ist unzulässig; ein umlaufender Vorbau müsste innerhalb des Baufensters bleiben.

Erhöhte Schrägansichten im Vergleich


gleiche Kamera, gleiche Darstellung

VERGLEICH · NICHT FESTGELEGT


B – Umlaufender Vorbau mit Säulen

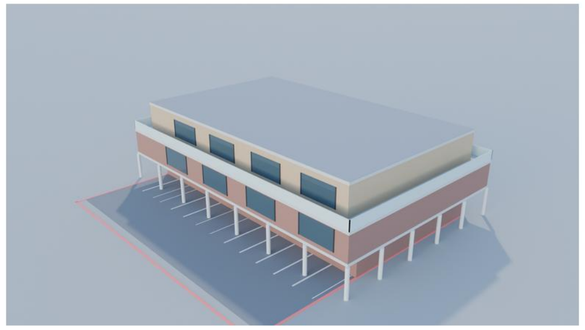


C – Maximierung der Wohnfläche

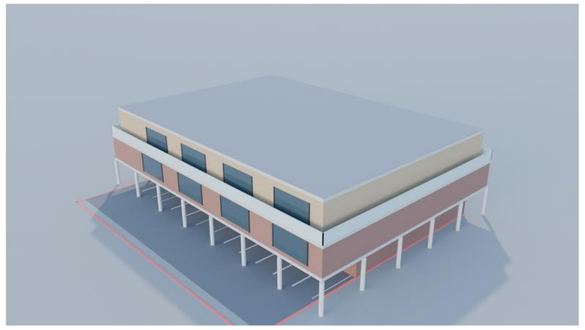


E1 – Vorbau bis Attika

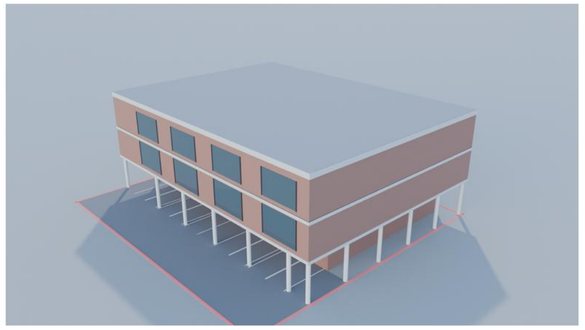


E2 – Staffel 1,50 m zurück

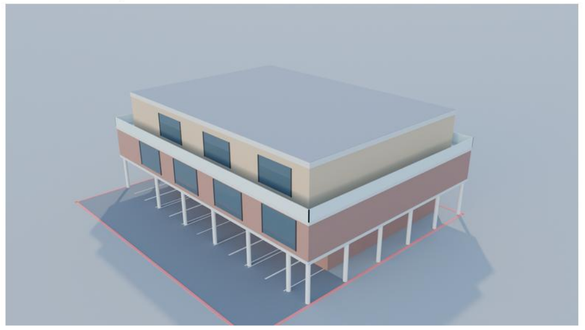


F1 – EG 18×30 m, Vorbau bis Attika

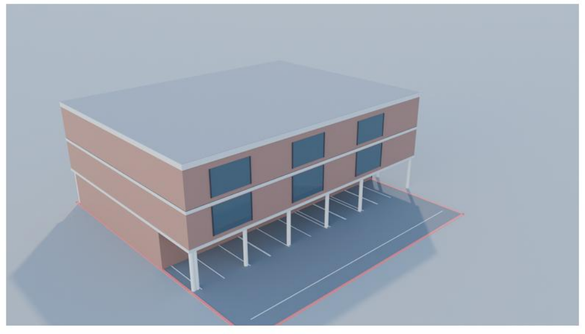


F2 – EG 18×30 m, Staffel 1,50 m

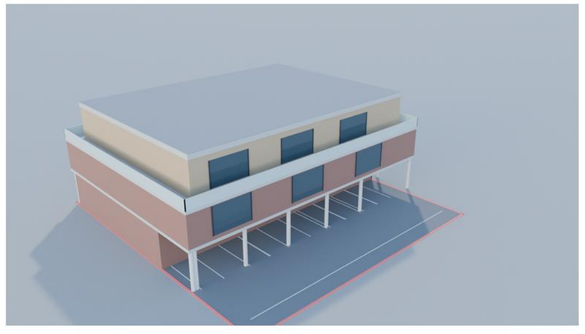

F3 – EG 18×30 m, Staffel 3,00 m

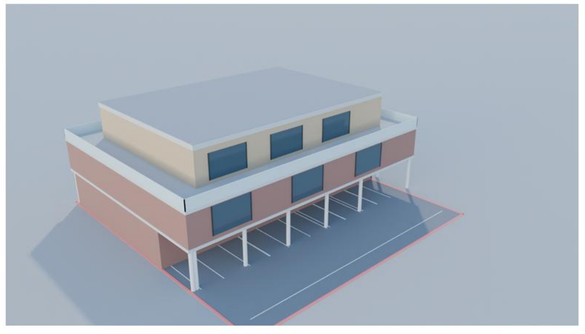

F4 – EG 30×18 m

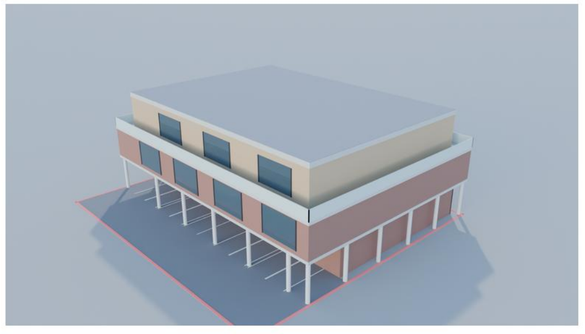


Lagepläne im Vergleich (Stellplätze, Säulen, Zufahrt)


grün = funktioniert, orange = eingeschränkt, rot = Konflikt, rosa = nur rechnerisch verbleibend

VERGLEICH · NICHT FESTGELEGT


E1 – Vorbau bis Attika (Staffel d

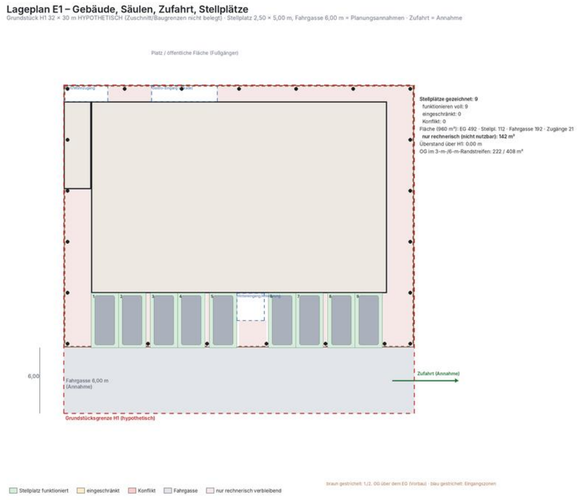


E4 – zweireihiges Parken, kleiner

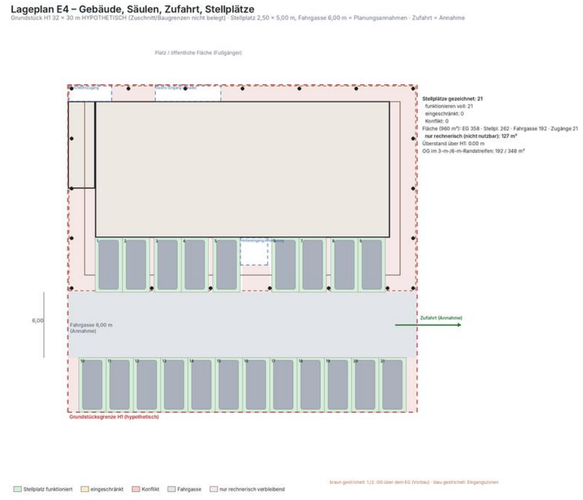

F2 – EG 18×30 m, Staffel 1,50 m

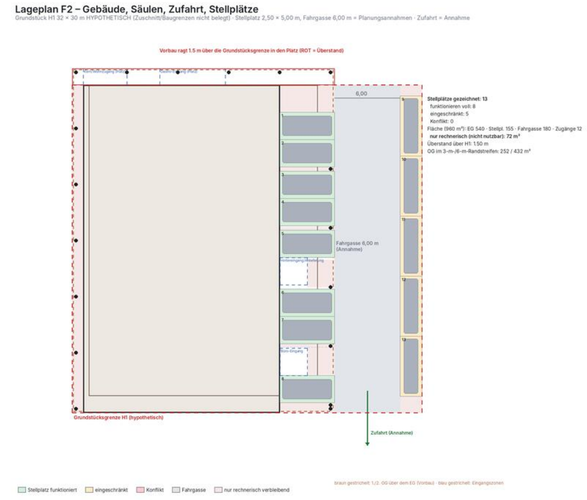

F4 – EG 30×18 m (gedreht), Staffe

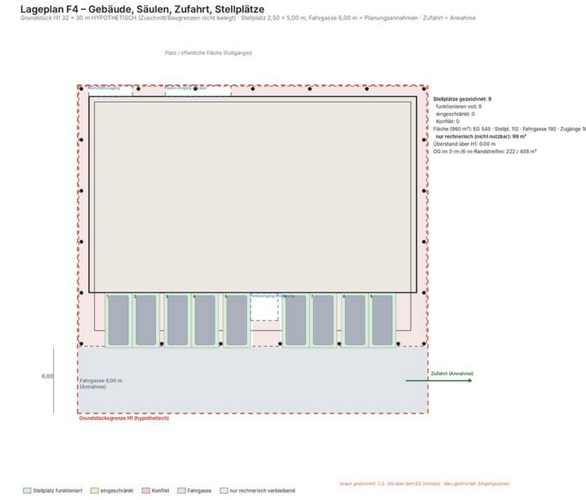

Vergleichstabelle 1: Flächen, Gewerbe, Wohnungen

VERGLEICH · NICHT FESTGELEGT

alle Werte vorläufig; Wohnfläche = 0,88 × Wohnstreifen, schematisch

Kennzahl	A	B	C	E1	E2	E3	E4	F1	F2	F3	F4
Höhe Attika (Bezug offen)	9,90	9,90	9,90	12,00	12,00	12,00	12,00	12,00	12,00	12,00	12,00
Außenmaß EG (m)	32×18	32×18	32×18	30×18	30×18	30×18	30×12	18×30	18×30	18×30	30×18
Grundfläche EG (m²)	576	576	576	492	492	492	358	540	540	540	540
Grundfläche 1. OG (m²)	660	788	892	768	768	768	608	756	756	756	768
Grundfläche 2. OG / Staffel (m²)	539	624	798	768	609	468	464	756	598	459	609
Gastraum (m²) / Plätze innen	280/120	280/120	280/120	281/120	281/120	281/120	198/85	232/99	232/99	232/99	307/132
Wohnfläche netto (m²)	846	963	1.159	1.084	960	852	727	1.065	942	835	960
Δ Wohnfläche gg. A (m²)	+0	+117	+313	+238	+114	+6	-119	+219	+96	-11	+114
Wohnungen Standardmix	16	18	18	18	16	15	16	14	14	13	16
Größen min–max (m²)	47–63	43–66	55–76	54–68	52–70	52–68	38–52	66–89	51–89	50–89	52–70
Ø Wohnungsgröße (m²)	53	54	64	60	60	57	45	76	67	64	60
WE kleiner / größerer Mix	19/13	21/14	21/14	20/14	19/12	17/12	19/12	18/12	17/11	16/11	19/12
Säulen	0	24	24	22	22	22	20	18	18	18	22
Überstand über H1 (m)	0,0	1,5	1,5	0,0	0,0	0,0	0,0	1,5	1,5	1,5	0,0

Vergleichstabelle 2: Stellplätze (Pflicht und Ziel getrennt)

VERGLEICH · NICHT FESTGELEGT

„nutzbar“ nach geometrischer Prüfung (Säulen, Eingänge, Fahrgasse); B/C mit den 11 B3-Stellplätzen geprüft

Kennzahl	A	B	C	E1	E2	E3	E4	F1	F2	F3	F4
Stellplätze gezeichnet	11	11	11	9	9	9	21	13	13	13	9
davon voll nutzbar	11	5	5	9	9	9	21	8	8	8	9
eingeschränkt	0	0	0	0	0	0	0	5	5	5	0
Konflikt (Säule/Eingang/Gasse)	0	6	6	0	0	0	0	0	0	0	0
erforderlich § 47 (Gastro+Büro, Spanne)	11,4–16,9	11,4–16,9	11,4–16,9	11,4–16,9	11,4–16,9	11,4–16,9	8,5–12,5	9,7–14,3	9,7–14,3	9,7–14,3	12,4–18,3
erforderlich Mittel	13,6	13,6	13,6	13,6	13,6	13,6	10,1	11,6	11,6	11,6	14,8
erforderlich Wohnen	0	0	0	0	0	0	0	0	0	0	0
optional Wohnen 0,5–1,5/WE	8–24	9–27	9–27	9–27	8–24	8–22	8–24	7–21	7–21	6–20	8–24
nutzbar ≥ Untergrenze / Mittel / Obergrenze	nein/nein/nein	nein/nein/nein	nein/nein/nein	nein/nein/nein	nein/nein/nein	nein/nein/nein	ja/ja/ja	ja/ja/nein	ja/ja/nein	ja/ja/nein	nein/nein/nein
Bemerkung	B3	6/11 gestört	6/11 gestört	1 Reihe	1 Reihe	1 Reihe	2 Reihen	Sackgasse	Sackgasse	Sackgasse	1 Reihe

Wichtig: Die Bewertung der Stellplätze erfolgt gegen die gesetzliche Pflicht (Gastro + Büro), nicht gegen eine pauschale Wohnungsquote. E4 wird daher nicht wegen fehlender Wohnungsstellplätze abgewertet; es hat den größten Überhang gegenüber der Pflicht, bezahlt dies aber mit 135 m² weniger Gewerbe-EG gegenüber E1–E3. F1–F3 erreichen die Pflicht (Mittel) mit 13 nutzbaren Plätzen knapp; E1–E3 und F4 (9 Plätze) liegen darunter.

Baurechtliche Ampel (vorläufig)

Keine Rechtsprüfung · bis zur Klärung von Grundstück, Baugrenzen und Satzungen offen

VERGLEICH · NICHT FESTGELEGT

Kriterium	E1	E2	E3	E4	F1	F2	F3	F4
Gebäudehöhe / Traufe	kritisch / offen: Attika +12,00 m über FFB, Wandhöhe ≈ +11,50 m. Plan A (rechtskräftig 2023, MI 3): H 15,00 m ok, aber TH 9,80 m überschritten. Plan B (Entwurf 2026, nicht einschlägig): H 12,00 m über OK Fahrbahn (FFB max. +0,30 m → Baukörper max. +11,70 m über FFB), TH 6,50 m überschritten. Fahrbahnhöhe unbekannt.	kritisch / offen: Attika +12,00 m über FFB, Wandhöhe ≈ +11,50 m. Plan A (rechtskräftig 2023, MI 3): H 15,00 m ok, aber TH 9,80 m überschritten. Plan B (Entwurf 2026, nicht einschlägig): H 12,00 m über OK Fahrbahn (FFB max. +0,30 m → Baukörper max. +11,70 m über FFB), TH 6,50 m überschritten. Fahrbahnhöhe unbekannt.	kritisch / offen: Attika +12,00 m über FFB, Wandhöhe ≈ +11,50 m. Plan A (rechtskräftig 2023, MI 3): H 15,00 m ok, aber TH 9,80 m überschritten. Plan B (Entwurf 2026, nicht einschlägig): H 12,00 m über OK Fahrbahn (FFB max. +0,30 m → Baukörper max. +11,70 m über FFB), TH 6,50 m überschritten. Fahrbahnhöhe unbekannt.	kritisch / offen: Attika +12,00 m über FFB, Wandhöhe ≈ +11,50 m. Plan A (rechtskräftig 2023, MI 3): H 15,00 m ok, aber TH 9,80 m überschritten. Plan B (Entwurf 2026, nicht einschlägig): H 12,00 m über OK Fahrbahn (FFB max. +0,30 m → Baukörper max. +11,70 m über FFB), TH 6,50 m überschritten. Fahrbahnhöhe unbekannt.	kritisch / offen: Attika +12,00 m über FFB, Wandhöhe ≈ +11,50 m. Plan A (rechtskräftig 2023, MI 3): H 15,00 m ok, aber TH 9,80 m überschritten. Plan B (Entwurf 2026, nicht einschlägig): H 12,00 m über OK Fahrbahn (FFB max. +0,30 m → Baukörper max. +11,70 m über FFB), TH 6,50 m überschritten. Fahrbahnhöhe unbekannt.	kritisch / offen: Attika +12,00 m über FFB, Wandhöhe ≈ +11,50 m. Plan A (rechtskräftig 2023, MI 3): H 15,00 m ok, aber TH 9,80 m überschritten. Plan B (Entwurf 2026, nicht einschlägig): H 12,00 m über OK Fahrbahn (FFB max. +0,30 m → Baukörper max. +11,70 m über FFB), TH 6,50 m überschritten. Fahrbahnhöhe unbekannt.	kritisch / offen: Attika +12,00 m über FFB, Wandhöhe ≈ +11,50 m. Plan A (rechtskräftig 2023, MI 3): H 15,00 m ok, aber TH 9,80 m überschritten. Plan B (Entwurf 2026, nicht einschlägig): H 12,00 m über OK Fahrbahn (FFB max. +0,30 m → Baukörper max. +11,70 m über FFB), TH 6,50 m überschritten. Fahrbahnhöhe unbekannt.	kritisch / offen: Attika +12,00 m über FFB, Wandhöhe ≈ +11,50 m. Plan A (rechtskräftig 2023, MI 3): H 15,00 m ok, aber TH 9,80 m überschritten. Plan B (Entwurf 2026, nicht einschlägig): H 12,00 m über OK Fahrbahn (FFB max. +0,30 m → Baukörper max. +11,70 m über FFB), TH 6,50 m überschritten. Fahrbahnhöhe unbekannt.
Geschosse / Dach	kritisch / offen: Plan A: II–III, drei Geschosse zulässig; Plan B: II zwingend (×). Beide Pläne: Hauptdach geneigt ≥ 38°, Flachdach nur untergeordnet → alle Flachdach-Entwürfe benötigen Befreiung; 2. OG = 100 % des 1. OG.	kritisch / offen: Plan A: II–III, drei Geschosse zulässig; Plan B: II zwingend (×). Beide Pläne: Hauptdach geneigt ≥ 38°, Flachdach nur untergeordnet → alle Flachdach-Entwürfe benötigen Befreiung; 2. OG = 79 % des 1. OG.	kritisch / offen: Plan A: II–III, drei Geschosse zulässig; Plan B: II zwingend (×). Beide Pläne: Hauptdach geneigt ≥ 38°, Flachdach nur untergeordnet → alle Flachdach-Entwürfe benötigen Befreiung; 2. OG = 61 % des 1. OG.	kritisch / offen: Plan A: II–III, drei Geschosse zulässig; Plan B: II zwingend (×). Beide Pläne: Hauptdach geneigt ≥ 38°, Flachdach nur untergeordnet → alle Flachdach-Entwürfe benötigen Befreiung; 2. OG = 76 % des 1. OG.	kritisch / offen: Plan A: II–III, drei Geschosse zulässig; Plan B: II zwingend (×). Beide Pläne: Hauptdach geneigt ≥ 38°, Flachdach nur untergeordnet → alle Flachdach-Entwürfe benötigen Befreiung; 2. OG = 100 % des 1. OG.	kritisch / offen: Plan A: II–III, drei Geschosse zulässig; Plan B: II zwingend (×). Beide Pläne: Hauptdach geneigt ≥ 38°, Flachdach nur untergeordnet → alle Flachdach-Entwürfe benötigen Befreiung; 2. OG = 79 % des 1. OG.	kritisch / offen: Plan A: II–III, drei Geschosse zulässig; Plan B: II zwingend (×). Beide Pläne: Hauptdach geneigt ≥ 38°, Flachdach nur untergeordnet → alle Flachdach-Entwürfe benötigen Befreiung; 2. OG = 61 % des 1. OG.	kritisch / offen: Plan A: II–III, drei Geschosse zulässig; Plan B: II zwingend (×). Beide Pläne: Hauptdach geneigt ≥ 38°, Flachdach nur untergeordnet → alle Flachdach-Entwürfe benötigen Befreiung; 2. OG = 79 % des 1. OG.
GRZ / Überdeckung	zu prüfen: größte Geschossprojektion 768 m² = 80 % von 960 m² (GRZ 0,6 = 576 m² nur Annahme).	zu prüfen: größte Geschossprojektion 768 m² = 80 % von 960 m² (GRZ 0,6 = 576 m² nur Annahme).	zu prüfen: größte Geschossprojektion 768 m² = 80 % von 960 m² (GRZ 0,6 = 576 m² nur Annahme).	zu prüfen: größte Geschossprojektion 608 m² = 63 % von 960 m² (GRZ 0,6 = 576 m² nur Annahme).	zu prüfen: größte Geschossprojektion 756 m² = 79 % von 960 m² (GRZ 0,6 = 576 m² nur Annahme).	zu prüfen: größte Geschossprojektion 756 m² = 79 % von 960 m² (GRZ 0,6 = 576 m² nur Annahme).	zu prüfen: größte Geschossprojektion 756 m² = 79 % von 960 m² (GRZ 0,6 = 576 m² nur Annahme).	zu prüfen: größte Geschossprojektion 768 m² = 80 % von 960 m² (GRZ 0,6 = 576 m² nur Annahme).
Grenzen / Baugrenzen	kritisch / offen: Baufenster MI 3 (P23) ≈ 27,7 × 15,9 m (abgeleitet), Baugrenzen 10,0 m West / 3 m übrige Seiten; EG-Fußabdruck und Vorbau über die Baugrenze passen nicht (siehe Entscheidungs-PDF).	kritisch / offen: Baufenster MI 3 (P23) ≈ 27,7 × 15,9 m (abgeleitet), Baugrenzen 10,0 m West / 3 m übrige Seiten; EG-Fußabdruck und Vorbau über die Baugrenze passen nicht (siehe Entscheidungs-PDF).	kritisch / offen: Baufenster MI 3 (P23) ≈ 27,7 × 15,9 m (abgeleitet), Baugrenzen 10,0 m West / 3 m übrige Seiten; EG-Fußabdruck und Vorbau über die Baugrenze passen nicht (siehe Entscheidungs-PDF).	kritisch / offen: Baufenster MI 3 (P23) ≈ 27,7 × 15,9 m (abgeleitet), Baugrenzen 10,0 m West / 3 m übrige Seiten; EG-Fußabdruck und Vorbau über die Baugrenze passen nicht (siehe Entscheidungs-PDF).	kritisch / offen: Überstand 1,50 m über H1 (Platzseite); Außenkante sonst auf der Grenze.	kritisch / offen: Überstand 1,50 m über H1 (Platzseite); Außenkante sonst auf der Grenze.	kritisch / offen: Überstand 1,50 m über H1 (Platzseite); Außenkante sonst auf der Grenze.	kritisch / offen: Baufenster MI 3 (P23) ≈ 27,7 × 15,9 m (abgeleitet), Baugrenzen 10,0 m West / 3 m übrige Seiten; EG-Fußabdruck und Vorbau über die Baugrenze passen nicht (siehe Entscheidungs-PDF).
Stellplätze (gesetzlich)	kritisch / offen: 9 nutzbar < erforderlich Mittel 13,6 (11,4–16,9): Ablöse/Mitbenutzung nötig	kritisch / offen: 9 nutzbar < erforderlich Mittel 13,6 (11,4–16,9): Ablöse/Mitbenutzung nötig	kritisch / offen: 9 nutzbar < erforderlich Mittel 13,6 (11,4–16,9): Ablöse/Mitbenutzung nötig	voraussichtlich ok: 21 nutzbar ≥ erforderlich bis 12,5	zu prüfen: 13 nutzbar, erforderlich 9,7–14,3 (Mittel 11,6): Spanne der Bauaufsicht entscheidet	zu prüfen: 13 nutzbar, erforderlich 9,7–14,3 (Mittel 11,6): Spanne der Bauaufsicht entscheidet	zu prüfen: 13 nutzbar, erforderlich 9,7–14,3 (Mittel 11,6): Spanne der Bauaufsicht entscheidet	kritisch / offen: 9 nutzbar < erforderlich Mittel 14,8 (12,4–18,3): Ablöse/Mitbenutzung nötig
Gewerbe im EG	zu prüfen: EG 492 m² (B3: 576 m²); Gastraum ca. 281 m².	zu prüfen: EG 492 m² (B3: 576 m²); Gastraum ca. 281 m².	zu prüfen: EG 492 m² (B3: 576 m²); Gastraum ca. 281 m².	zu prüfen: EG 358 m² (B3: 576 m²); Gastraum ca. 198 m².	zu prüfen: EG 540 m² (B3: 576 m²); Gastraum ca. 232 m².	zu prüfen: EG 540 m² (B3: 576 m²); Gastraum ca. 232 m².	zu prüfen: EG 540 m² (B3: 576 m²); Gastraum ca. 232 m².	zu prüfen: EG 540 m² (B3: 576 m²); Gastraum ca. 307 m².
Brandschutz / Feuerwehr	zu prüfen: Vorbau über Stellplätzen/Fahrgasse, Aufstellflächen und Feuerwehrzufahrt, Rettungswege – Konzept erforderlich.	zu prüfen: Vorbau über Stellplätzen/Fahrgasse, Aufstellflächen und Feuerwehrzufahrt, Rettungswege – Konzept erforderlich.	zu prüfen: Vorbau über Stellplätzen/Fahrgasse, Aufstellflächen und Feuerwehrzufahrt, Rettungswege – Konzept erforderlich.	zu prüfen: Vorbau über Stellplätzen/Fahrgasse, Aufstellflächen und Feuerwehrzufahrt, Rettungswege – Konzept erforderlich.	zu prüfen: Vorbau über Stellplätzen/Fahrgasse, Aufstellflächen und Feuerwehrzufahrt, Rettungswege – Konzept erforderlich.	zu prüfen: Vorbau über Stellplätzen/Fahrgasse, Aufstellflächen und Feuerwehrzufahrt, Rettungswege – Konzept erforderlich.	zu prüfen: Vorbau über Stellplätzen/Fahrgasse, Aufstellflächen und Feuerwehrzufahrt, Rettungswege – Konzept erforderlich.	zu prüfen: Vorbau über Stellplätzen/Fahrgasse, Aufstellflächen und Feuerwehrzufahrt, Rettungswege – Konzept erforderlich.

Offene Fragen und Prüfbedarf

VERGLEICH · NICHT FESTGELEGT

Vor jeder Weiterentwicklung zu klären

• Fotos der städtischen Unterlagen (S. 13, 15, 16) in den Projektordner; daraus Grundstückszuschnitt, Baugrenzen, GRZ, Höhenbezugspunkt, Traufhöhe, Dachform, Abstände, Festsetzungen zu Stellplätzen/Zufahrten.
• Bebauungsplan-Stand: Entwurf (S. 15) – rechtskräftige Fassung; örtliche Bauvorschrift/Stellplatzsatzung für Nicht-Wohnungen; städtebaulicher Vertrag/Kaufvertrag (Stellplätze auch für Wohnungen möglich).
• Einstufung der Gaststätte („örtliche“ oder „überörtliche Bedeutung“), Sitzplatzzahl innen/außen, Büro mit/ohne Besucherverkehr.
• Höhenbezug der 12,00 m; Vollgeschoss-Definition für das 2. OG; Traufhöhe 6,50 m.
• Überbauung des Platzes (F1–F3: 1,5 m), Grenz- und Abstandsflächen, GRZ-Anrechnung überdeckter Stellplätze.
• Zufahrt: Straße, Gefälle, Sichtdreiecke; Feuerwehrzufahrt/Aufstellflächen unter dem Vorbau; Wendemöglichkeit in der Sackgasse (F1–F3).
• Stellplatzmaße/Garagenverordnung für Stellplätze neben Säulen und Parallelparker; Schleppkurven.
• Statik: Kragarme 1,0–5,0 m, Säulenraster 5,4 m, Fundamente; Brandschutz Vorbau.

Keine Variante ist ausgewählt.