
Variante A – Obergeschosse moderat vergrößert (1,50 m)

Grundrisse und Schnitt M 1:250 · HYPOTHETISCH: Grundstücksform, Baufenster und Rechtsfragen sind nicht belegt


Erdgeschoss 32 × 18 m mit Stellplätzen

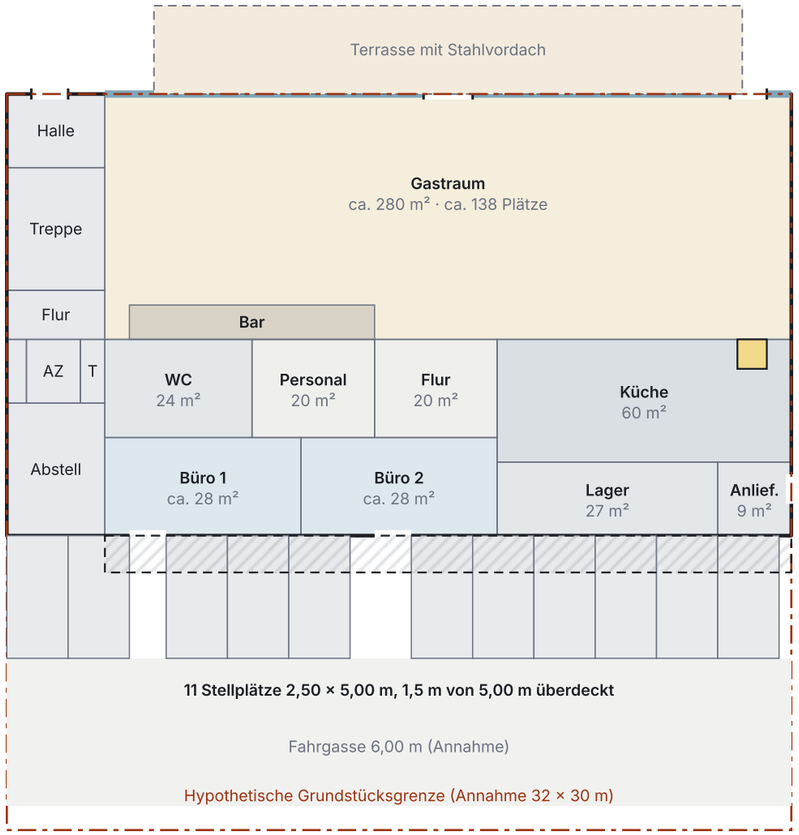


1. Obergeschoss (nur Wohnungen)



Schnitt bei x = 17,00 m

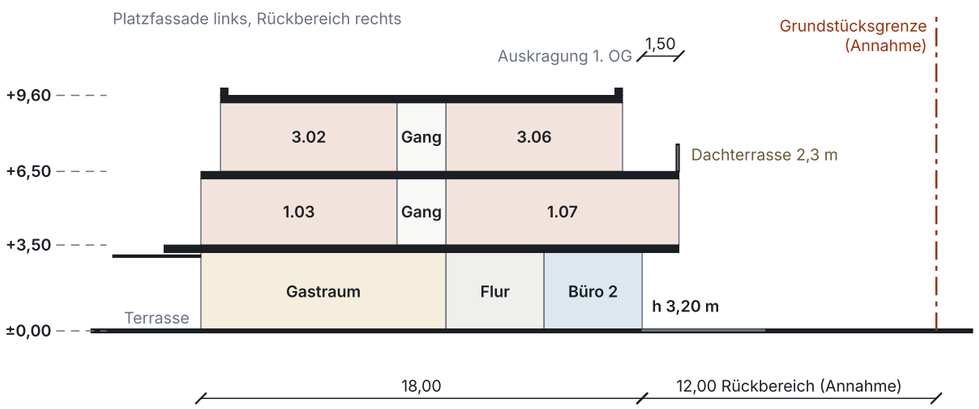

3. Geschoss, Staffel (nur Wohnungen)

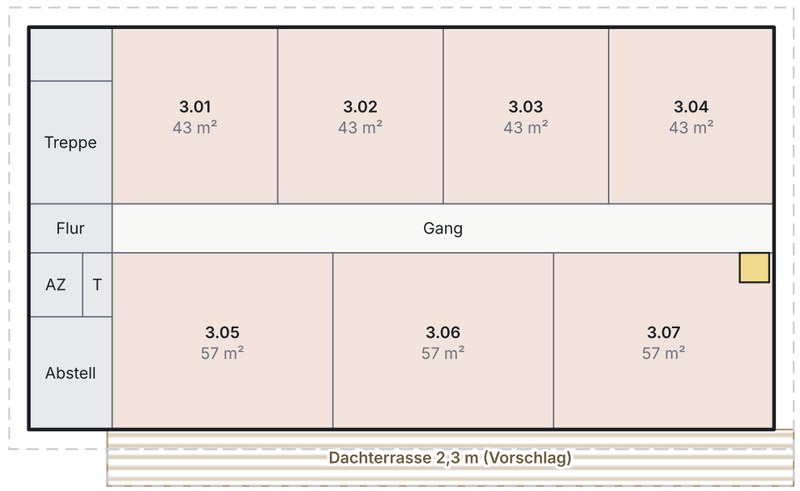

KENNZAHLEN

Außenmaß EG / 1. OG / 3. Geschoss	**32×18 / 32×19,5 / 30,4×16,4 m**
Auskragung 1. OG / Überstand Staffel	**1,50 / 0,00 m**
Gastronomie brutto, Innenplätze	**ca. 440 m², ca. 138**
Büros hinten, netto	**ca. 56 m²**
Wohnungen, Wohnfläche netto	**16, ca. 773 m²**
Stellplätze, überdeckt	**11, 1,5 von 5,0 m Tiefe**

LEGENDE

- Wohnung, Nummer nach Geschoss (1.xx, 3.xx), Wohnfläche netto
- Büro (EG, hinten)
- Gastraum und Bar
- Küche, Lager, WC, Personal, Anlieferung (Anlief.)
- Kern: Halle, Treppe, Flur, Abstell (AZ Aufzug, T Technik)
- Auskragung über Stellplätzen (hypothetisch)
- Dachterrasse auf dem 1. OG (Vorschlag)
- Küchenabluft-Schacht, alle Geschosse

OFFENE PUNKTE (NICHT GELÖST)

- **C-30** Baufenster, GRZ und Zählung von Auskragungen unbekannt; Projektion 618 m² gegen theoretisch 576 m²: nicht nachweisbar zulässig.
- **C-28** Stellplatzbedarf 61 laut Excel, hier 11 nachweisbar (Annahme).
- **C-29** Grundstückszuschnitt, Zufahrt und Anlieferung unbekannt (hier 32 × 30 m angenommen).
- **C-37** Büros 56 m² statt 165 m²: Mieteinnahmen und Gastro-Pacht nicht neu gerechnet.
- **C-35** Tragwerk der Auskragung.

HINWEISE

Erdgeschoss in allen Varianten gleich. Der Anbau ist abgestuft: 1. OG weiter ausgekragt als die Staffel, dazwischen eine Dachterrasse.

Flächen netto = Brutto × 0,88 (Annahme). Fenster, Türen und Wandstärken sind nicht festgelegt. Keine Variante ist festgelegt.

Neue Mitte Werlte · Baufeld 3

Bauvorhaben: Restaurant und Bar, Büros, Wohnungen

Variante A – Grundrisse und Schnitt

Maßstab 1:250 (A3)

Stand 22.10.2026 · Modell NEUE_MITTE_MASTER_DRAFT_A_003

VORLÄUFIGER ARBEITSSTAND – nicht freigegeben