
Gastronomie – maßstäbliche Möblierung, Layout normal

Grundriss M 1:100 · Tische 1,20 × 0,80 m (4 Plätze), Stühle 0,45 × 0,45 m, 12 Barhocker · Maße ASSUMED

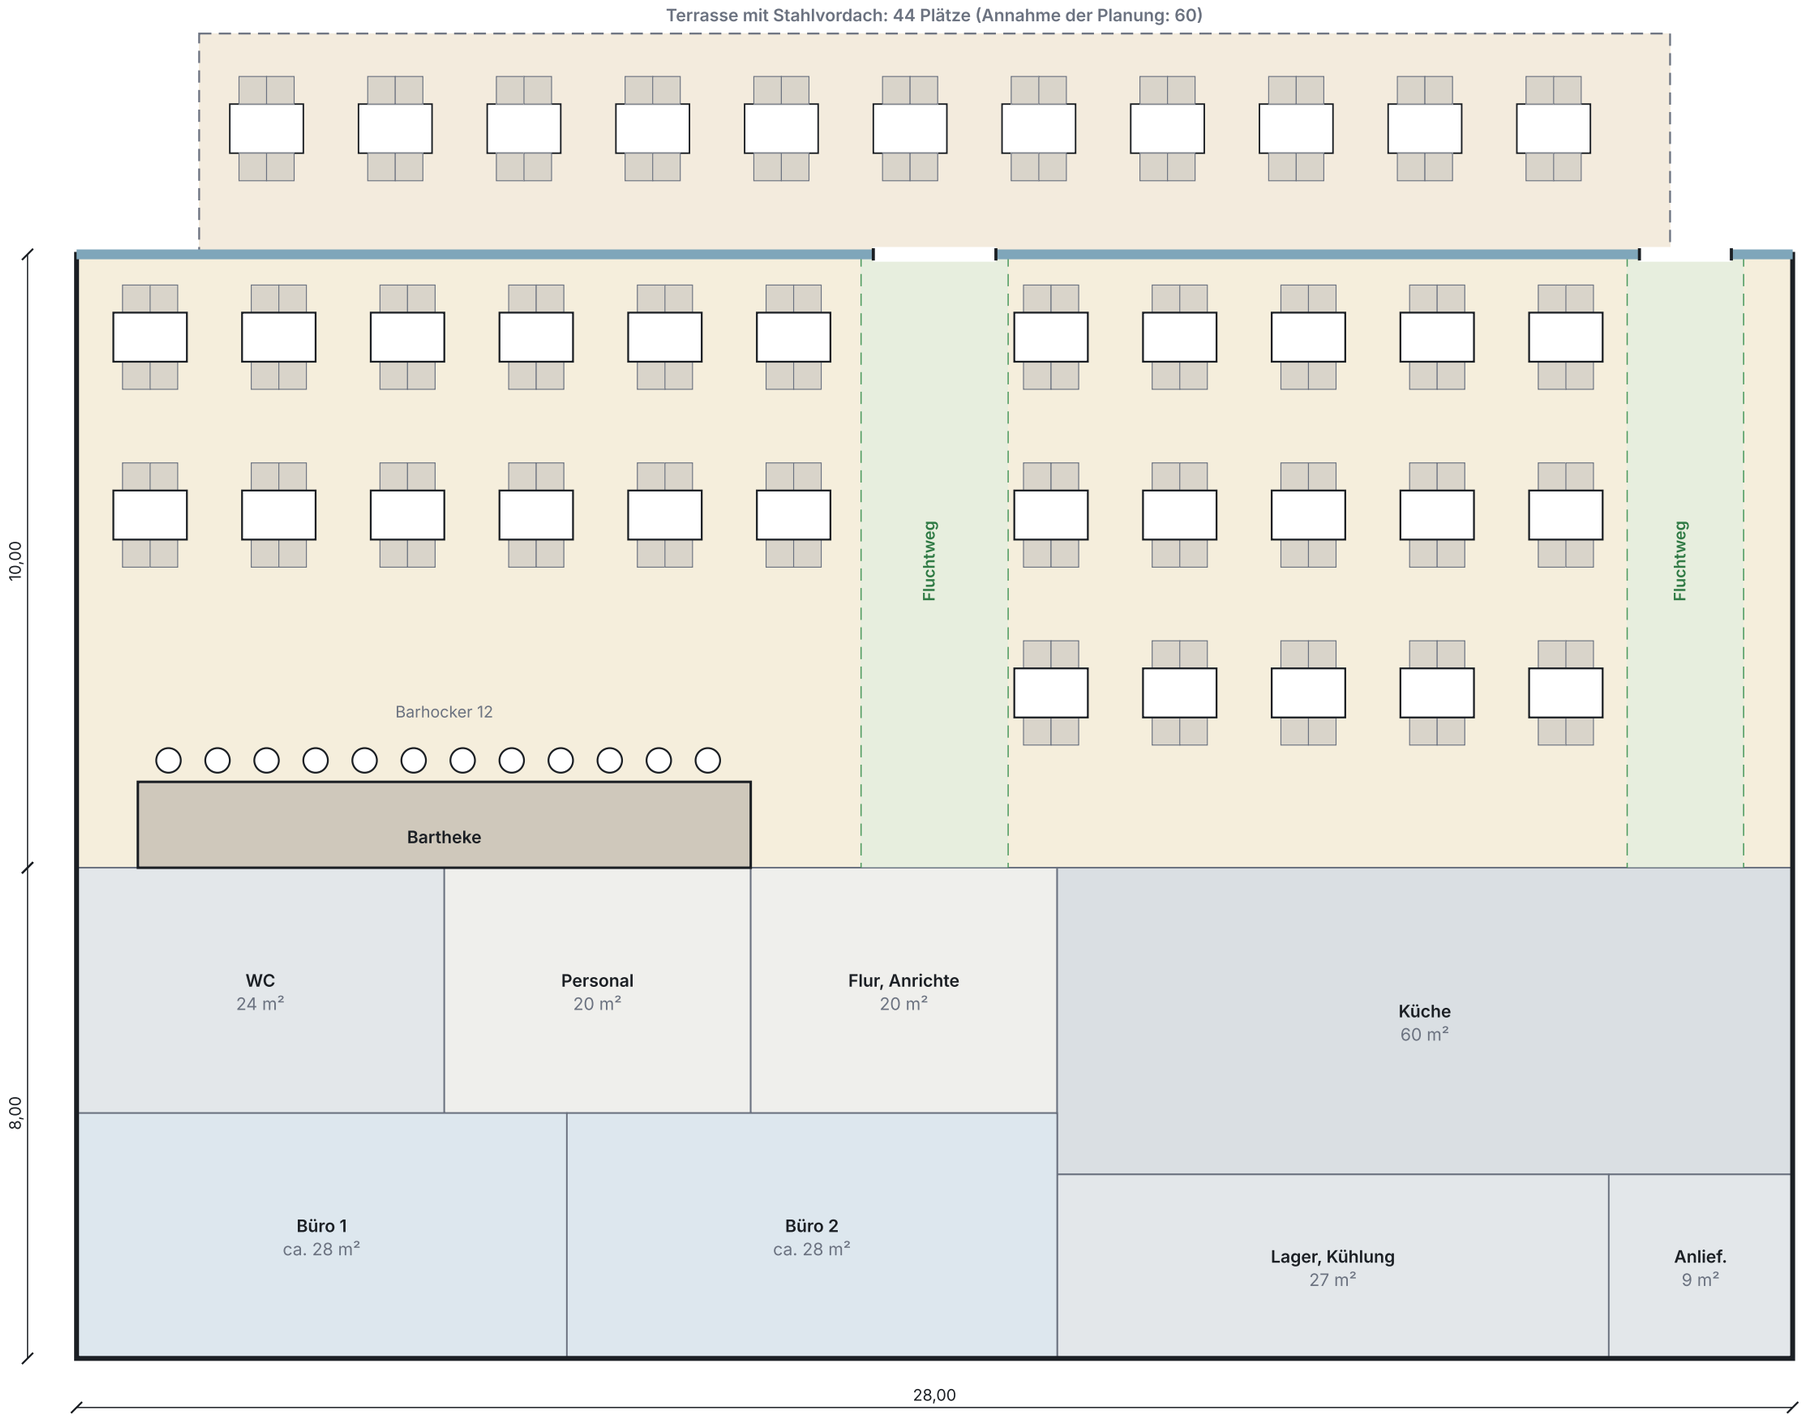

0 5 m Maßstab 1:100

KENNZAHLEN

Gastraum und Bar	**280 m²**
Innenplätze realistisch (normal)	**120**
davon Barhocker	**12**
komfortabel / dicht	**88 / 128**
Flächenregel der letzten Fassung	**138**
Terrasse (normal)	**44**
Fläche je Platz (normal)	**2,3 m²**

LEGENDE

- Tisch 1,20 × 0,80 m, 4 Plätze
- Stuhl 0,45 × 0,45 m
- Barhocker
- Fluchtweg vor den Ausgängen, 2,40 und 1,90 m breit
- Terrasse

OFFENE PUNKTE (NICHT GELÖST)

- **C-20** Gaststätte mit über 120 + 44 Plätzen: Einstufung als Sonderbau, Zahl der Ausgänge und Rettungsbreiten offen.
- **C-36** Fluchtwege nur als Annahme; Küche und Personal über Flur und Anlieferung Ost.
- **C-38** Barrierefreie Plätze und Fahrbahn für Rollstühle noch nicht nachgewiesen.

HINWEISE

Die 138 Plätze der letzten Fassung waren eine Flächenregel (2,1 m² je Platz). Die Möblierung zeigt: realistisch sind etwa 120, komfortabel 88, sehr dicht 128. Die Gastronomie wird nicht weiter verkleinert.

Reihen im Layout normal: Reihe 1: 11 Tische, Reihe 2: 11 Tische, Reihe 3: 5 Tische.

Neue Mitte Werlte · Baufeld 3

Bauvorhaben: Restaurant und Bar, Büros, Wohnungen

Gastronomie – Möblierung

Maßstab 1:100 (A3)


Stand 22.10.2026 · Arbeitsgrundlage B3 (Variante B, nicht festgelegt)

VORLÄUFIGER ARBEITSSTAND – nicht freigegeben


Büros hinten – Zugang, Büro-WC und Flur (drei Alternativen)

Grundrisse hinterer Erdgeschoss-Bereich M 1:150 · unabhängige Erreichbarkeit nur über die Rückseite, Fußweg vom Platz ungeklärt (C-29)


Alternative K: Büro-Foyer im Kern

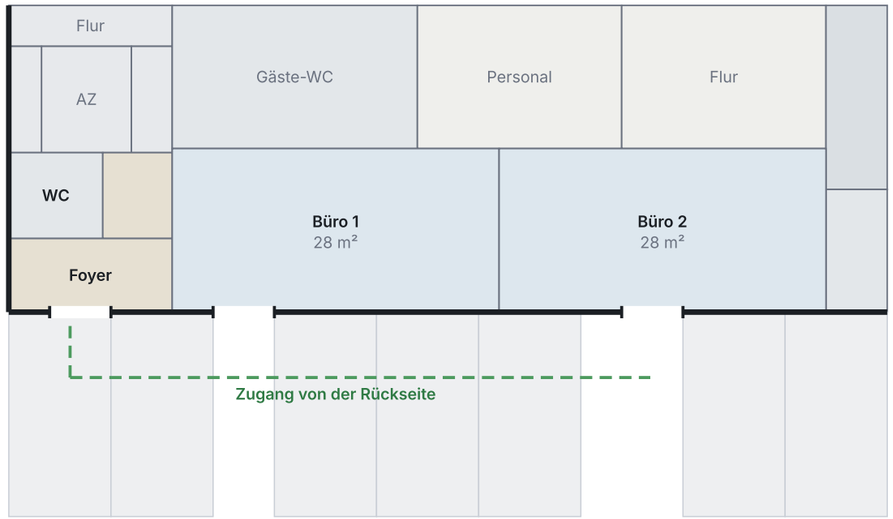

Alternative F: Flur und WC zwischen den Büros

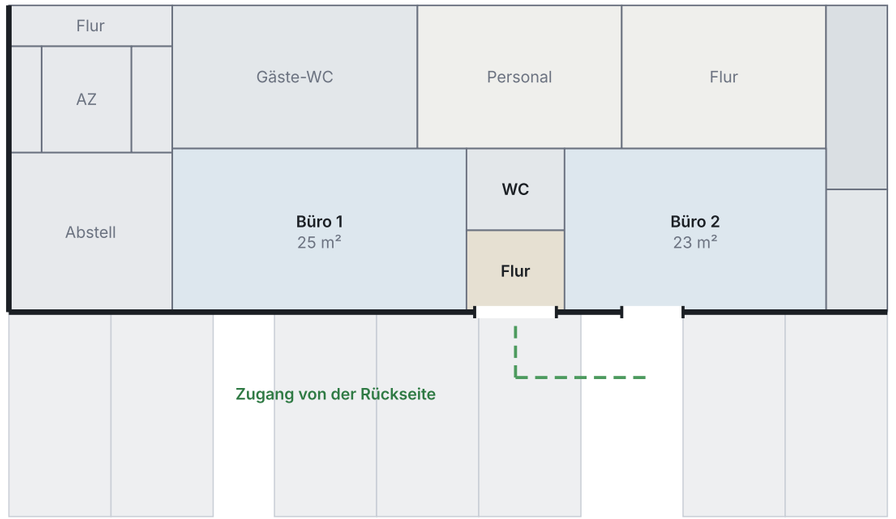

Alternative M: Mitbenutzung des Gäste-WC

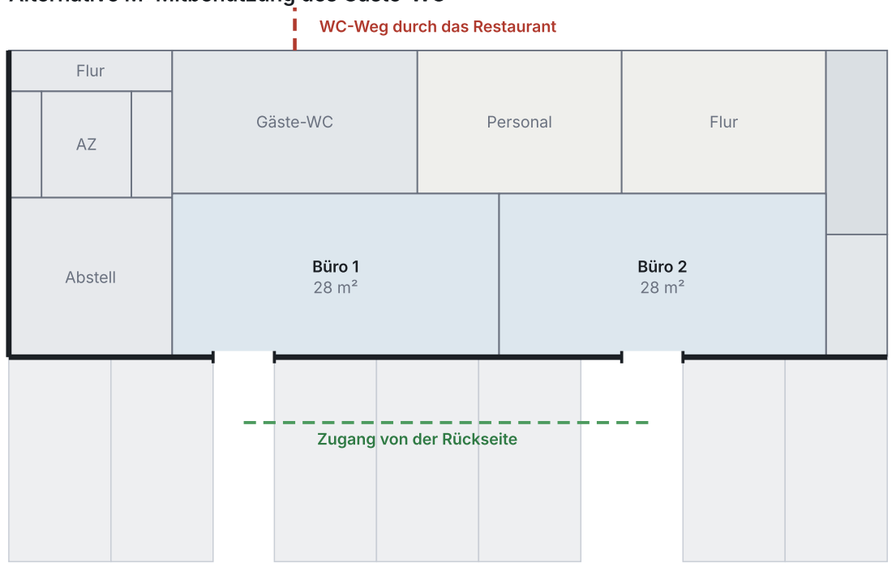

Vergleich der Alternativen

	K	F	M
Gastronomie	440 m²	440 m²	440 m²
Büros netto	56 m²	48 m²	56 m²
Büro-WC	im Foyer, 5 m²	zwischen Büros, 5 m²	Gäste-WC
WC von beiden Büros erreichbar	nur über außen	ja, innen	nur durch Restaurant
unabhängig vom Restaurant	ja (Rückseite)	ja (Rückseite)	nein (WC)
Barrierefreier Zugang	ja, eben	ja, eben	ja, eben
Verlust	Abstell Wohnen 16 m²	Bürofläche −8 m²	keiner

Arbeitsstand: Alternative K (Büros bleiben je 28 m², Gastronomie unverändert). Sie kostet den Abstellraum Wohnen im Erdgeschoss; ein neuer Ort für Fahrrad und Abstell ist offen (C-38). Alternative F löst die Wege innen, verkleinert die Büros auf 25 und 22 m².

KENNZAHLEN

Büro 1 und 2 (K)	**je ca. 28 m² netto**
Foyer mit Büro-WC (K)	**ca. 16 m² brutto**

LEGENDE

- Büro
- Büro-Foyer, Büro-Flur
- WC
- Weg von der Rückseite
- Weg durch das Restaurant

OFFENE PUNKTE (NICHT GELÖST)

- C-32 Büros nur rückseitig belichtet und erschlossen; Büro-WC jetzt in drei Alternativen geprüft.
- C-29 Fußweg vom Platz zur Rückseite und Grundstückszuschnitt unbekannt: unabhängige Erreichbarkeit nur unter dieser Voraussetzung.
- C-38 Abstell- und Fahrradraum Wohnen: neuer Ort offen.
- C-36 Fluchtwege der Büros: Rücktüren, nicht geprüft.

HINWEISE

Gastronomie bleibt bei 440 m²; keine Fläche wird ohne Alternativen abgegeben.

Flächen netto = Brutto × 0,88 (Annahme). Türen und Wandstärken nicht festgelegt.

Neue Mitte Werlte · Baufeld 3

Bauvorhaben: Restaurant und Bar, Büros, Wohnungen

Büros – Zugang, WC und Flur

Maßstab 1:150 (A3)


Stand 22.10.2026 · Arbeitsgrundlage B3 (Variante B, nicht festgelegt)

VORLÄUFIGER ARBEITSSTAND – nicht freigegeben


Arbeitsgrundlage B3 – Grundrisse und Schnitt (Variante B, nicht festgelegt)

M 1:250 · Mittelgang bei y 9,50 m für ausgeglichene Wohnungstiefen · HYPOTHETISCH: Grundstücksform, Baufenster und Rechtsfragen nicht belegt


Erdgeschoss 32 × 18 m (Alternative K, Büro-Foyer im Kern)

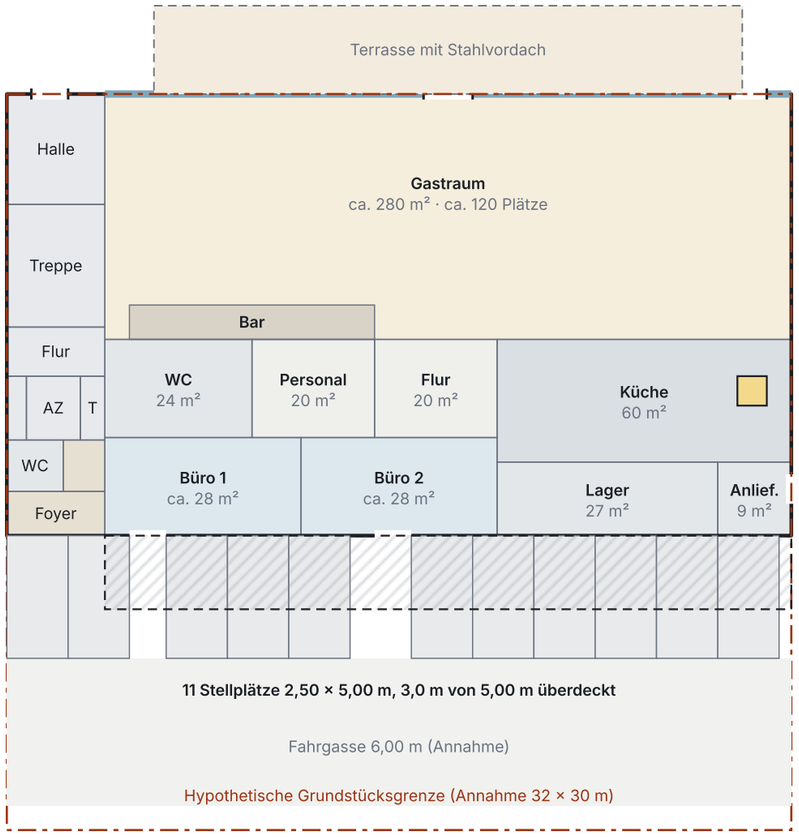


1. Obergeschoss (nur Wohnungen)

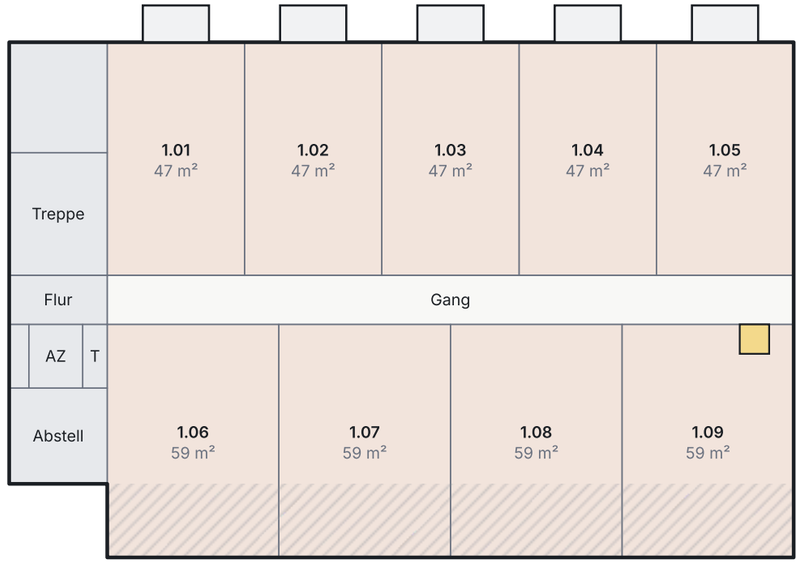

Schnitt bei x = 17,00 m

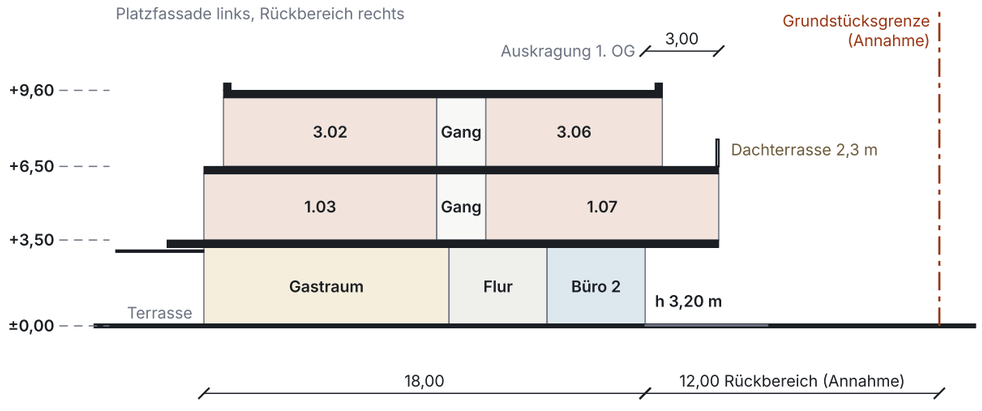

3. Geschoss, Staffel (nur Wohnungen)

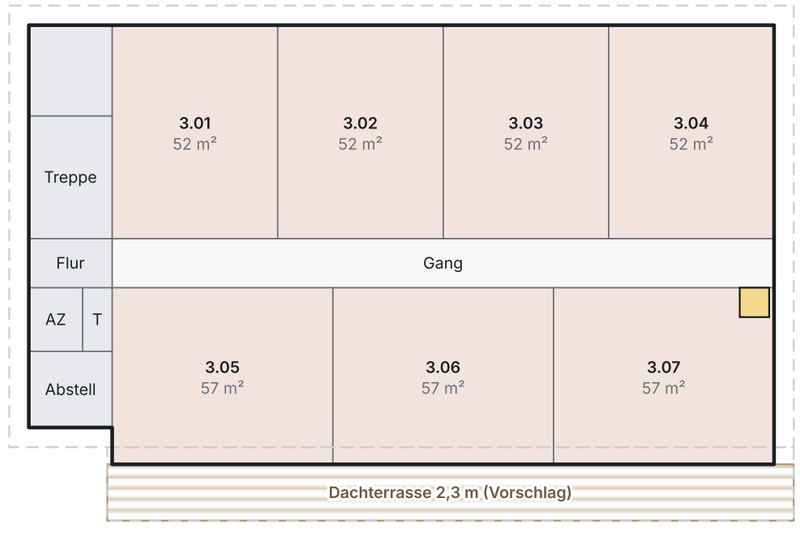

KENNZAHLEN

Außenmaß EG / 1. OG / 3. Geschoss	**32×18 / 32×21,0 / 30,4×17,9 m**
Anbau 1. OG / Überstand Staffel	**3,00 / 1,50 m**
Gastronomie, Innenplätze realistisch	**440 m², 120**
Büros, netto	**2 × 28 = 56 m²**
Wohnungen, Wohnfläche netto	**16, ca. 846 m²**
Dachterrasse hinten	**2,3 m tief**

LEGENDE

- Wohnung, Nummer nach Geschoss, Wohnfläche netto
- Büro
- Gastraum und Bar
- Küche, Lager, WC, Personal, Anlieferung
- Büro-Foyer
- Kern (AZ Aufzug, T Technik)
- Auskragung 1. OG über Stellplätzen
- Dachterrasse (Vorschlag)
- Küchenabluft-Schacht

OFFENE PUNKTE (NICHT GELÖST)

- **C-30** Baufenster, GRZ, Abstände, Zählung der Auskragung unbekannt; Projektion 660 m² gegen theoretisch 576 m².
- **C-28** Stellplatzbedarf und nachweisbare Stellplätze getrennt: siehe Blatt 26.
- **C-38** Abstell- und Fahrradraum Wohnen im EG entfällt (Alternative K).
- **C-22** Küchenabluft-Schacht läuft durch Wohnungen.

HINWEISE

Variante B ist nur Arbeitsgrundlage, nicht festgelegt. Gegenüber Version 2 liegt der Mittelgang bei y 9,50 m; die Wohnfläche ist unverändert.

Flächen netto = Brutto × 0,88 (Annahme). Fenster, Türen und Wandstärken nicht festgelegt.

Neue Mitte Werlte · Baufeld 3

Bauvorhaben: Restaurant und Bar, Büros, Wohnungen

Arbeitsgrundlage B3 – Grundrisse und Schnitt

Maßstab 1:250 (A3)

Stand 22.10.2026 · Arbeitsgrundlage B3 (Variante B, nicht festgelegt)

VORLÄUFIGER ARBEITSSTAND – nicht freigegeben

Wohnungsstudien – Grundrisse, Belichtung, Belüftung, Erschließung

Studien M 1:100 zur Prüfung der Nutzbarkeit (Variante B als Arbeitsgrundlage), keine Planung · Innenmaße mit Wandstärken ASSUMED

Wohnung 1.01–1.05 (1. OG vorn)



Eingang vom Mittelgang

- Wohnfläche netto ca, 46,8 m² (Modell)
- Wohnräume an der Fassade: 1, Raumtiefe 4,6 m
- Glasfläche (Annahme) ca, 7,0 m² = 29 % der Wohnraumfläche
- Innenliegend: Küche, Abstell, Bad, Flur (mechanische Lüftung)
- Einseitig belichtet, keine Querlüftung
- Außenraum: Balkon 2,70 × 1,50 m zum Platz
- Stufenlos über Aufzug und Mittelgang

Wohnung 1.06–1.09 (1. OG hinten)



Eingang vom Mittelgang

- Wohnfläche netto ca, 58,5 m² (Modell)
- Wohnräume an der Fassade: 2, Raumtiefe 4,6 m
- Glasfläche (Annahme) ca, 10,9 m² = 35 % der Wohnraumfläche
- Innenliegend: Küche, Bad, Flur, Abstell (mechanische Lüftung)
- Einseitig belichtet, keine Querlüftung
- Außenraum: kein Außenraum
- Stufenlos über Aufzug und Mittelgang


Wohnung 3.01–3.04 (Staffel vorn)



Eingang vom Mittelgang

- Wohnfläche netto ca, 51,7 m² (Modell)
- Wohnräume an der Fassade: 2, Raumtiefe 4,4 m
- Glasfläche (Annahme) ca, 10,3 m² = 36 % der Wohnraumfläche
- Innenliegend: Küche, Bad, Flur, Abstell (mechanische Lüftung)
- Einseitig belichtet, keine Querlüftung
- Außenraum: Umlauf 0,80 m, kein nutzbarer Außenraum
- Stufenlos über Aufzug und Mittelgang

Wohnung 3.05–3.07 (Staffel hinten)

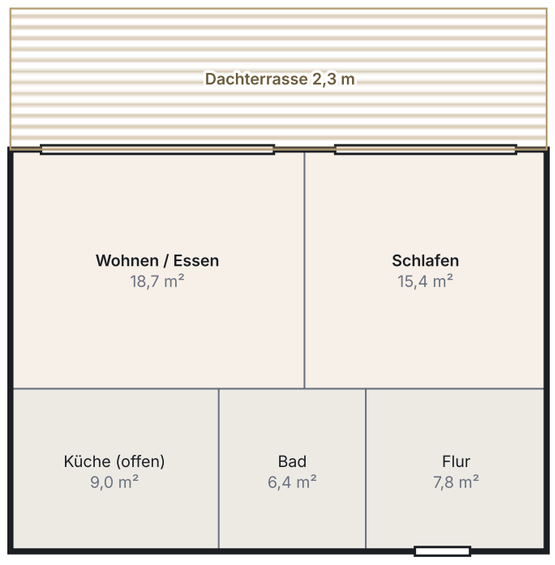

Eingang vom Mittelgang

- Wohnfläche netto ca, 57,0 m² (Modell)
- Wohnräume an der Fassade: 2, Raumtiefe 3,9 m
- Glasfläche (Annahme) ca, 13,8 m² = 40 % der Wohnraumfläche
- Innenliegend: Küche, Bad, Flur (mechanische Lüftung)
- Einseitig belichtet, keine Querlüftung
- Außenraum: Dachterrasse 9,0 × 2,3 m = 20,7 m²
- Stufenlos über Aufzug und Mittelgang

Maßstab 1:100

0 2 m

KENNZAHLEN

Typen	4
Wohnungen im Modell	16

LEGENDE

- Raum mit Fenster (Aufenthaltsraum)
- innenliegender Raum, mechanische Lüftung
- Fenster / Wohnungstür (Lage Annahme)
- Dachterrasse

OFFENE PUNKTE (NICHT GELÖST)

- C-26 Einseitig belichtete Wohnungen, Lage über der Gastro-Terrasse: Schall und Betriebszeiten nicht geprüft.
- C-33 Hintere Wohnungen im 1. OG ohne Außenraum (Loggien nur als Option, nicht geplant).
- C-39 Dachterrasse: Brüstung, Brand- und Schallschutz, Dachaufbau über Wohnungen und Zugang offen; keine Rettungsfunktion nachgewiesen.
- C-27 Rollstuhlgerechte Wohnung: Kandidaten sind T2 und T4, nicht nachgewiesen.

HINWEISE

Wohnungsgrößen sind Ergebnis der Gebäudetiefe (Mittelgang bei y 9,50 m: vorn 9,5 m, hinten 9,5 m), nicht der Flächenmaximierung. Küche und Bad liegen innen.

Glasfläche = 2,2 m Höhe × (Raumbreite − 0,9 m, höchstens 3,2 m); Regeln zu Tageslicht und Lüftung sind nicht geprüft.

Neue Mitte Werlte · Baufeld 3

Bauvorhaben: Restaurant und Bar, Büros, Wohnungen

Wohnungsstudien

Maßstab 1:100 (A3)


Stand 22.10.2026 · Arbeitsgrundlage B3 (Variante B, nicht festgelegt)

VORLÄUFIGER ARBEITSSTAND – nicht freigegeben


Fassadenkonzept rundum – schematische Ansichten, Arbeitsgrundlage B3

Ansichten M 1:250 · Material und Farbe der Platzfassade unverändert · Fensterformate Vorschlag (ASSUMED), nicht freigegeben

Ansicht Platzseite (unverändert)

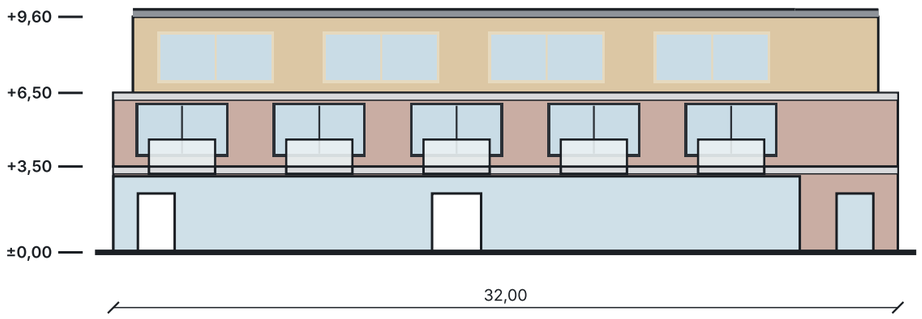


Ansicht Rückseite

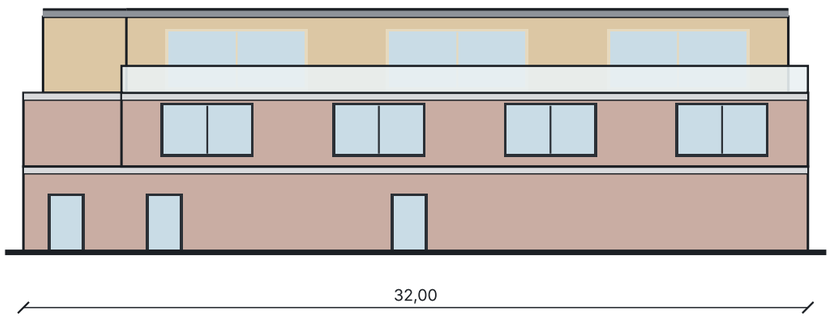


Höhen: ±0,00 Oberkante Erdgeschoss, +3,50 1. OG, +6,50 Traufe nach B-Plan und Staffel, +9,60 Staffeldecke, +9,90 Attika

Seitenansicht Kernseite (x = 0)

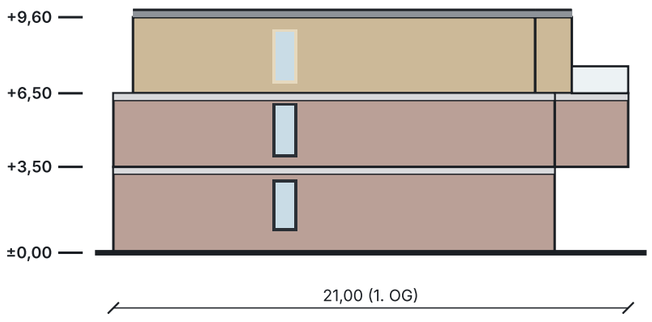

Seitenansicht Ostseite (x = 32)

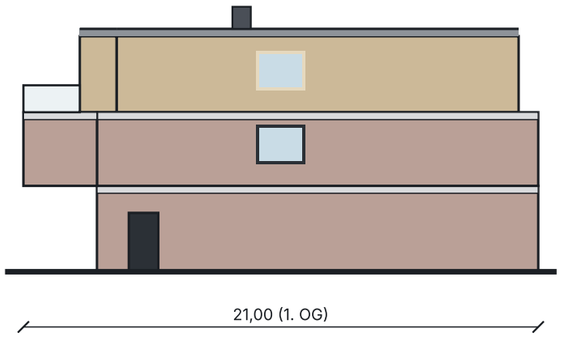

Kernseite: Platzfassade links, Rückseite rechts. Ostseite: Platzfassade rechts, Rückseite links. Himmelsrichtung unbekannt (C-13).

KENNZAHLEN

Tiefe EG / 1. OG / Staffel	**18,00 / 21,00 / 17,90 m**
Höhe Attika	**9,90 m**
Dachterrasse hinten	**2,3 m tief**

LEGENDE

- Klinker, dunkelrotbraun (hier aufgehellt)
- Betonbänder und Balkonplatten
- Lärchenholz Staffelgeschoss
- Milchglas-Brüstung, 1,10 m
- Glas, Türen
- schwarzer Stahlrahmen (Wohngeschoss, EG)
- helles Holzfenster (Staffel)

OFFENE PUNKTE (NICHT GELÖST)

- C-13 Himmelsrichtung und Platzseite unbekannt.
- C-19 Rückseite, Seiten und Dachterrasse sind nicht Teil des eingefrorenen Designs; hier ein Entwurfsvorschlag.
- C-30 Auskragung und Stufung: Baufenster, GRZ, Abstände und Höhen offen.
- C-35 Tragwerk der Auskragung (3,00 m, Sichtbeton-Untersicht).
- C-22 Abluftstutzen über dem Dach (Position offen).

HINWEISE

Gestaltungsregeln: Die Betonbänder der Platzfassade laufen um alle vier Seiten. Fensterachsen der Rückseite folgen den Wohnungsachsen, die Staffel hinten öffnet sich mit raumhohen Holzfenstern zur Dachterrasse.

Die Stufung ist ausgebildet: Auskragung mit Betonband, Dachterrasse mit Milchglas-Brüstung, Staffel in Lärchenholz. Kernseite mit Treppenhausschlitz, Ostseite mit Fenster am Gangende.

Neue Mitte Werlte · Baufeld 3

Bauvorhaben: Restaurant und Bar, Büros, Wohnungen

Fassadenkonzept rundum

Maßstab 1:250 (A3)

Stand 22.10.2026 · Arbeitsgrundlage B3 (Variante B, nicht festgelegt)

VORLÄUFIGER ARBEITSSTAND – nicht freigegeben

Stellplätze und baurechtliche Prüfpunkte – Bedarf, Nachweis und offene Fragen getrennt

Alle Werte hypothetisch oder Annahme; es wird keine Zulässigkeit behauptet. Die 32 × 30 m sind keine bestätigte Grundstücksgröße.

1. Stellplätze: Bedarf und Nachweis getrennt

	Bedarf (grobe Annahme der Excel, nicht Satzung)	Nachweislich möglich	Hypothese H1 (32 × 30 m, nicht bestätigt)
Wohnungen	16 × 1,5 = 24	0 (kein Lageplan, keine Grundstücksmaße)	–
Gastronomie	Gastraum und Bar 280 m² / 10 = 28	0	–
Büros	56 m² / 30 = 1,9	0	–
Summe	54 (Excel-Stand mit 12 Wohnungen und 165 m² Büro: 61)	0	11 Stellplätze 2,50 × 5,00 m
Fehlbetrag	–	gegenüber dem Bedarf: nicht bestimmbar	rechnerisch 43 Stellplätze
Überdeckung	–	–	3,0 von 5,0 m Tiefe durch die Auskragung; Durchfahrtshöhe 3,20 m (Annahme)

Die Stellplatzsatzung der Stadt ist nicht bekannt; der Bedarf folgt den groben Annahmen der Excel. Mögliche Lösungen (Stellplätze außerhalb des Grundstücks, Ablöse, Gemeinschaftsanlage, Fahrradstellplätze) sind mit der Stadt zu klären und nicht Teil dieser Geometrie. Die Überdachung erzeugt keine zusätzlichen Stellplätze.

2. Baurechtliche Prüfpunkte (alle offen)

Thema	Wert im Modell (hypothetisch)	Status	Nötige Unterlage
GRZ	Grundfläche EG 576 m² = 0,60 × 960 m²; Projektion 1. OG 660 m² = 0,69	OFFEN: Zählung von Auskragungen, Terrassen, Stellplätzen unbekannt; Variante nicht nachweisbar zulässig	B-Plan Nr. 123, Auslegung der GRZ
Baufenster	Gebäude 32 × 18 m; Sichtschätzung des Baufensters nur 400–460 m²	OFFEN (C-01): Nachweis fehlt	Baufenster-Koordinaten, Lageplan
Auskragung	3,00 m hinten über Stellplätzen, Staffel 1,50 m kürzer	OFFEN: Baugrenze und Überbauung der Stellplatzfläche	B-Plan, Stadt
Abstände	Rückbereich 12 m (aus 32 × 30 m angenommen)	OFFEN: Grenzabstand und Abstandsflächen unbekannt	Lageplan mit Grenzen, NBauO
Höhen	Traufe 6,50 m, Staffeldecke 9,60 m, Attika 9,90 m, Maximum 12,00 m	OFFEN (C-03): Messregel unbestätigt	B-Plan, Stadt
Geschosse	EG, 1. OG, Staffel (Staffel 87 % des Geschosses darunter)	OFFEN (C-02): Vollgeschoss und Zahl zulässig?	B-Plan, Stadt
Brandschutz und Rettungswege	Gaststätte 120 + 44 Plätze, Büros, 16 Wohnungen, ein Treppenraum, Dachterrasse	OFFEN (C-15, C-20, C-36, C-39)	Brandschutzkonzept
Terrasse und Vordach am Platz	24 × 3,6 m, Vordach, Balkone 1,50 m über der Fassade	OFFEN: Eigentum und Sondernutzung des Platzes	Lageplan, Stadt

KENNZAHLEN

Bedarf (Annahme)	**ca. 54**
nachweislich möglich	**0**
Hypothese H1	**11**

OFFENE PUNKTE (NICHT GELÖST)

- C-28 Stellplätze: Bedarf und Nachweis getrennt, Fehlbetrag offen.
- C-29 Grundstückszuschnitt, Zufahrt, Anlieferung unbekannt.
- C-30 Baurechtliche Zulässigkeit nicht nachgewiesen.

HINWEISE

Keine Variante gilt als zulässig, solange die Nachweise fehlen.

Neue Mitte Werlte · Baufeld 3

Bauvorhaben: Restaurant und Bar, Büros, Wohnungen

Stellplätze und Prüfpunkte

Tabelle

Stand 22.10.2026 · Arbeitsgrundlage B3 (Variante B, nicht festgelegt)

VORLÄUFIGER ARBEITSSTAND – nicht freigegeben

Vergleichstabelle – Arbeitsgrundlage B3 gegenüber A, B und C (Version 2)

Spalte B3 ist die Arbeitsgrundlage dieser Runde (Variante B, nicht festgelegt). Alle Werte hypothetisch.

Kriterium	A (v2)	B (v2)	B3 Arbeitsgrundlage	C (v2)
Anbau 1. OG / Überstand Staffel	1,5 / 0 m	3,0 / 1,5 m	3,0 / 1,5 m	4,5 / 2,0 m
Mittelgang	y 8,0	y 8,0	y 9,5 (Tiefen 9,5 / 9,5 m)	y 9,0
Projizierte Fläche, GRZ-Zahl	618 m², 0,64	660 m², 0,69	660 m², 0,69	702 m², 0,73
Gastronomie brutto	440 m²	440 m²	440 m²	440 m²
Innenplätze	138 (Flächenregel)	138 (Flächenregel)	120 realistisch; 88 komfortabel; 128 dicht	138 (Flächenregel)
Terrassenplätze	60 (Annahme)	60 (Annahme)	44 (komfortabel 40, dicht 52)	60 (Annahme)
Büros netto, Zugang und WC	56 m², WC fehlt	56 m², WC fehlt	56 m² (Alt. K), WC im Foyer, Zugang rückseitig	56 m², WC fehlt
Wohnungen, Wohnfläche netto	16, 773 m²	16, 846 m²	16, 846 m²	16, 895 m²
Wohnungsgrößen netto	39, 43, 57, 58 m²	39, 43, 68, 69 m²	47, 52, 57, 59 m²	44, 49, 65, 71 m²
Tiefe/Breite höchstens	1,43	1,57	1,7	1,64
Dachterrasse	2,3 m	2,3 m	2,3 m, 3 Terrassen à 20,7 m²	3,3 m
Stellplätze: Bedarf / nachweislich / Hypothese	54 / 0 / 11	54 / 0 / 11	54 / 0 / 11	54 / 0 / 11
Überdeckt, Stützen	1,5 m, keine	3,0 m, keine	3,0 m, keine	4,5 m, 5 Stützen
Nachweisstatus	nicht nachweisbar	nicht nachweisbar	nicht nachweisbar	nicht nachweisbar

KENNZAHLEN

Zusätzliche Wohnfläche B3 gegen A	**+73 m²**
Innenplätze B3 gegen Flächenregel	**120 statt 138**

OFFENE PUNKTE (NICHT GELÖST)

- C-30 Zulässigkeit nicht nachgewiesen.
- C-28 Stellplatznachweis offen.
- C-37 Büros und Gastronomie kleiner als in der Excel: Wirtschaftlichkeit nicht neu gerechnet.
- C-29 Grundstücksgröße 32 × 30 m ist Annahme.

HINWEISE

A, B, C (v2) unverändert aus der letzten Runde; die Innenplätze dort sind eine Flächenregel (2,1 m² je Platz), nur B3 wurde möbliert.

Der Bedarf von 54 Stellplätzen folgt den groben Excel-Annahmen mit den neuen Flächen (Excel-Stand 61).