Variante E – 12 m und umlaufender Vorbau mit Parken (E1–E4)

VARIANTE E · NICHT FESTGELEGT

Entwurfsstudie Neue Mitte Werlte – Baufeld 3 · überarbeitet 24.10.2026 · keine Variante festgelegt

Ziel: Gebäudehöhe bis 12,00 m planerisch ausnutzen (drei Geschosse, keine zusätzlichen), umlaufender säulengestützter Vorbau, Zufahrt und Stellplätze unter und neben dem Vorbau. Keine Variante ist festgelegt; B3 (Variante A) und alle bestehenden Modelle bleiben unverändert. Alle Flächen sind vorläufig, bis Grundstücksgrenzen und Baugrenzen verlässlich geklärt sind.

	Bestätigt (Quelle)	Annahme / unbestätigt
Grundstück	ca. 960 m²; B-Plan 123 rechtskräftig 2023: Baufeld 3 vermutlich MI 3 / Flurstück 59/1 mit Baugrenzen 10,0 m West, 3 m übrige Seiten	Zuschnitt 32 × 30 m = Hypothese H1; Planausschnitt: ≈ 42,3 × 22,7 m (geschätzt), Baufenster ≈ 27,7 × 15,9 m (abgeleitet); Foto-Seiten fehlen
Höhe / Geschosse	Plan A rechtskräftig 2023 (MI 3): II–III, TH 9,80 m, H 15,00 m; Plan B Entwurf 2026 (MI 2/Änderung): II zwingend, TH 6,50 m, H 12,00 m; beide: Dach ≥ 38°, Bezug OK Fahrbahn	Baufeld 3 nicht bestätigt; Fahrbahnhöhe unbekannt; Befreiungen (Dach, Baugrenze, TH) offen
Stellplätze Wohnen	KEINE gesetzliche Pflicht seit 01.07.2024 (§ 47 Abs. 1 Satz 3 NBauO; FAQ Land Niedersachsen Stand 11.07.2025)	ob B-Plan/städtebaulicher Vertrag/Kaufvertrag Stellplätze für Wohnungen verlangt: unbekannt
Stellplätze Gastro/Büro	Pflicht besteht; Bemessung bedarfsorientiert (Richtzahlen Erlass: Gaststätte 1 je 8–12 Sitzplätze, Büro 1 je 30–40 m²)	Gaststättenart („örtliche Bedeutung“) und Sitzplatzzahl angenommen
Maße	–	Stellplatz 2,50 × 5,00 m, Fahrgasse 6,00 m, Säule Ø 0,40 m (Vorgaben/Annahmen), Zufahrtslage
Wohnfläche	B3: 846 m², 16 WE (Plan)	übrige Varianten aus Geschosskonturen geschätzt (0,88 × Wohnstreifen)

Grundstück, Baugrenzen und Quellenstatus

VARIANTE E · NICHT FESTGELEGT

Was gesichert ist, was nur aus Beschreibungen stammt und was Hypothese ist

Punkt	Stand	Herkunft / Bemerkung
Grundstücksfläche ca. 960 m²	GESICHERT (Projektangabe)	Projektunterlagen/Auftraggeber; nicht am Liegenschaftsnachweis geprüft
Zuschnitt 32 × 30 m (Variantenstudie E/F)	HYPOTHESE H1	nur aus 960 m² und B3-Annahme; widerspricht dem Planausschnitt: Flurstück 59/1 ≈ 42,3 × 22,7 m (geschätzt), Baufenster ≈ 27,7 × 15,9 m (abgeleitet)
B-Plan Nr. 123 „Ehemalige Grundschule“, 1. Änderung (Entwurf 25.09.2026): MI, GRZ 0,6, II zwingend, TH 6,50 m, H 12,00 m, SH 0,30 m, Baugrenze 3 m	GESICHERT (Entwurf)	amtliche Unterlagen der Stadt Werlte (sgwerlte.de), in quellen_stadt/ abgelegt; nicht rechtskräftig
Foto-Seiten 13/15/16 des Auftraggebers („zwei- bis dreigeschossig“)	FEHLEN	ZIP nicht angekommen; Seite 15/16 entsprechen vermutlich Abb. 2/3 der 1. Änderung (unbestätigt)
Zuordnung „Baufeld 3“ im Nutzungskonzept	INDIZ: MI 3 / Flurstück 59/1	Fläche ≈ 960 m² und Z II–III passen; Seite 13 fehlt (unbestätigt)
Baugrenzen / Baulinien, GRZ, Abstandsflächen	UNBEKANNT	keine Maße am Plan abgelesen; alle Konturen in den Plänen sind Hypothese
Erschließungsstraße, Zufahrt, Platzseite	ANNAHME	Platz an der Seite y = 0; Zufahrt von Osten (E) bzw. Süden (F) angenommen
Stellplatz 2,50 × 5,00 m, Fahrgasse 6,00 m	ANNAHME (Auftraggeber, vorläufig)	Abgleich mit Stellplatzsatzung/Garagenverordnung ausstehend

Die ZIP-Datei mit den Fotos der Seiten 13, 15 und 16 ist in dieser Sitzung nicht angekommen; der Ordner quellen_stadt/fotos_stadt_unterlagen/ ist leer. Grundlage sind die amtlichen Planunterlagen der Stadt (Entwurf B-Plan 123, 1. Änderung). Konturen aus den Plänen sind als ABGELEITET/GESCHÄTZT gekennzeichnet, gesicherte Maße getrennt (siehe Entscheidungs-PDF).

Die zwei Planstände im Vergleich

ENTSCHEIDUNGSGRUNDLAGE · NICHTS FESTGELEGT


Fundstellen: Planzeichnung und textliche Festsetzungen (P23 / E26), Begründung 3.2–3.3


Merkmal	P23 MI 3 (und MI 1) – RECHTSKRÄFTIG 2023	P23 MI 2 – rechtskräftig 2023	E26 – 1. Änderung ENTWURF 2026
Rechtsstand	in Kraft seit 14.04.2023	in Kraft seit 14.04.2023	Entwurf, kein Satzungsbeschluss
Geltungsbereich	ganzes Plangebiet (1,27 ha), MI 3 = Flurstück 59/1	östlicher Block	ca. 3.874 m²; MI 3 liegt NICHT darin
Gebietsart / GRZ	Mischgebiet / 0,6	Mischgebiet / 0,6	Mischgebiet / 0,6
Vollgeschosse	II–III (Mindest-/Höchstmaß)	II zwingend	II zwingend
Traufhöhe TH	max. 9,80 m	max. 6,50 m	max. 6,50 m
Gebäudehöhe H	max. 15,00 m	max. 12,00 m	max. 12,00 m
Sockelhöhe SH	FFB EG ≤ 0,30 m über Bezugspunkt	wie MI 3	wie P23
Bezugspunkt	OK Fahrbahn der nächsten ausgebauten Erschließungsstraße, Mitte vor dem Baukörper; oben: OK Baukörper (First/Hauptgesims)	wie MI 3	wie P23
Dachform	Hauptdächer geneigt ≥ 38°; Flachdach nur Verbindungsbauten (≥ 1,0 m unter First), Wintergärten/untergeordnete Dachflächen ≤ 70 m²	wie MI 3	wie P23 (örtl. Bauvorschrift)
Bauweise	offen (bis 50 m)	offen	offen
Baugrenzen (MI 3)	10,0 m zur Marktstraße (W); 3 m Planstraße (N), 3 m Ost, 3 m Süd	an Baumstandorte orientiert	3,0 m zu Planstraße und Parkplatz
Stellplätze/Nebenanlagen	Garagen/Gebäude-Nebenanlagen entlang öffentl. Verkehrsflächen unzulässig; Baumreihe Marktstraße: Kronentraufbereich ohne Versiegelung	wie MI 3	öffentlicher Parkplatz 63 Plätze; Überdachung von Stellplätzen dort unzulässig
Fassade	Ziegelsichtmauerwerk nicht glasiert (Rot/Rotbraun), andere Materialien ≤ 1/2	wie MI 3	wie P23

Welches Grundstück ist Baufeld 3? (Indizien, UNBESTÄTIGT)

ENTSCHEIDUNGSGRUNDLAGE · NICHTS FESTGELEGT

Ausschnitt rechtskräftiger Plan 2023 (links) und Nutzungskonzept 2026 (rechts, Markierung = vermutete Lage)

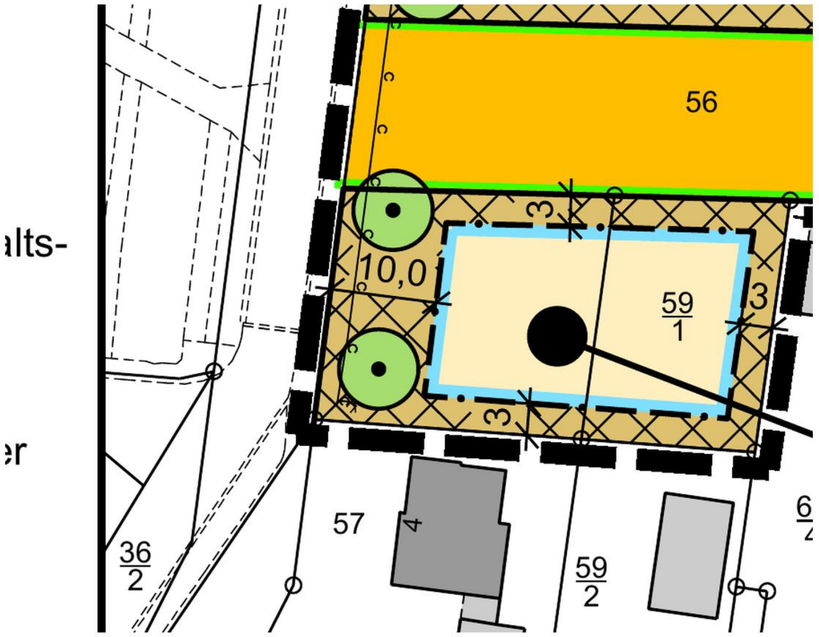

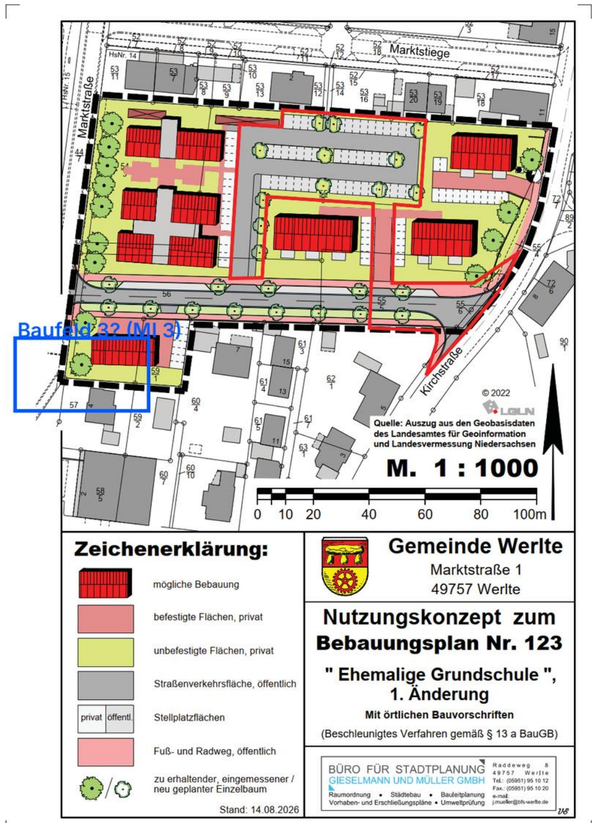

Indiz	Befund
Fläche	Flurstück 59/1 ≈ 960 m² (aus Planabbildung abgegriffen, ±3 %) = Projektangabe ca. 960 m²
Geschosse	MI 3: II–III = städtische Seite 13 „mindestens zwei, höchstens drei“ (MI 2: II zwingend – passt nicht)
Plan 2026	Änderungsbereich enthält MI 3 nicht → die „12,00 m“ der Seite 15 gelten für Baufeld 3 nicht
Gegenindiz	MI 1 hat ebenfalls II–III, H 15 m; die Baufeldnummern stehen in den geladenen Unterlagen nicht; Seite 13 fehlt
Folge	Bestätigung durch den Auftraggeber nötig (Foto Seite 13 / Baufeldplan)

Grundstücksmaße und Risiken: gesichert, abgeleitet, geschätzt

ENTSCHEIDUNGSGRUNDLAGE · NICHTS FESTGELEGT


Keine verbindlichen Grundstücksmaße aus einer abgebildeten/fotografierten Plankarte – amtlicher Lageplan erforderlich

Angabe	Wert	Status	Herkunft / Risiko
Baugrenzabstände MI 3	10,0 m W; 3 m N/O/S	GESICHERT (im Plan bemaßt)	Planzeichnung P23
Planstraße	16,0 m Querschnitt	GESICHERT	Begründung 3.3
Höhen, Z, GRZ, Dach, Bezugspunkt	siehe Planstände	GESICHERT (P23 rechtskräftig)	Textliche Festsetzungen 1.2, 2.2
Baufenster MI 3	≈ 27,7 × 15,9 m = 439 m²	ABGELEITET (Vektorplan 1:1000)	Polygon aus der PDF-Geometrie; Plan leicht gegen Nord gedreht; nicht vermessen
Flurstück 59/1	≈ 42,3 × 22,7 m ≈ 960 m²	GESCHÄTZT (±3 %)	aus der Planabbildung gemessen; Grenzen nur grafisch (Liegenschaftskarte Stand 08.06.2022)
Fahrbahnhöhe (Bezugspunkt)	unbekannt	FEHLT	Bauamt der Stadt Werlte (laut Festsetzung 1.2 erfragbar)
Amtlicher Lageplan / Vermessung	–	FEHLT	ÖbVI Dipl.-Ing. Jörg Jüngerink (Plan-Az. 22-7003); Gebäude in der Nutzung ist Stand 2022
Baumreihe Marktstraße	Kronen-/Wurzelschutz	GESICHERT (Festsetzung)	schränkt Stellplätze/Zufahrt im Westen ein; Kronendurchmesser unbekannt
Zufahrt/Ausfahrt zur Planstraße	–	ANNAHME	Lage, Sichtdreiecke, Gehwege (16 m Querschnitt) ungeklärt

Lageplan Flurstück 59/1: Baufenster und Fußabdrücke der Varianten

ENTSCHEIDUNGSGRUNDLAGE · NICHTS FESTGELEGT

Alle EG-Fußabdrücke aus F, E, B3 passen NICHT in das Baufenster · Umrisse an der Baufensterecke ausgerichtet · Maße abgeleitet/geschätzt

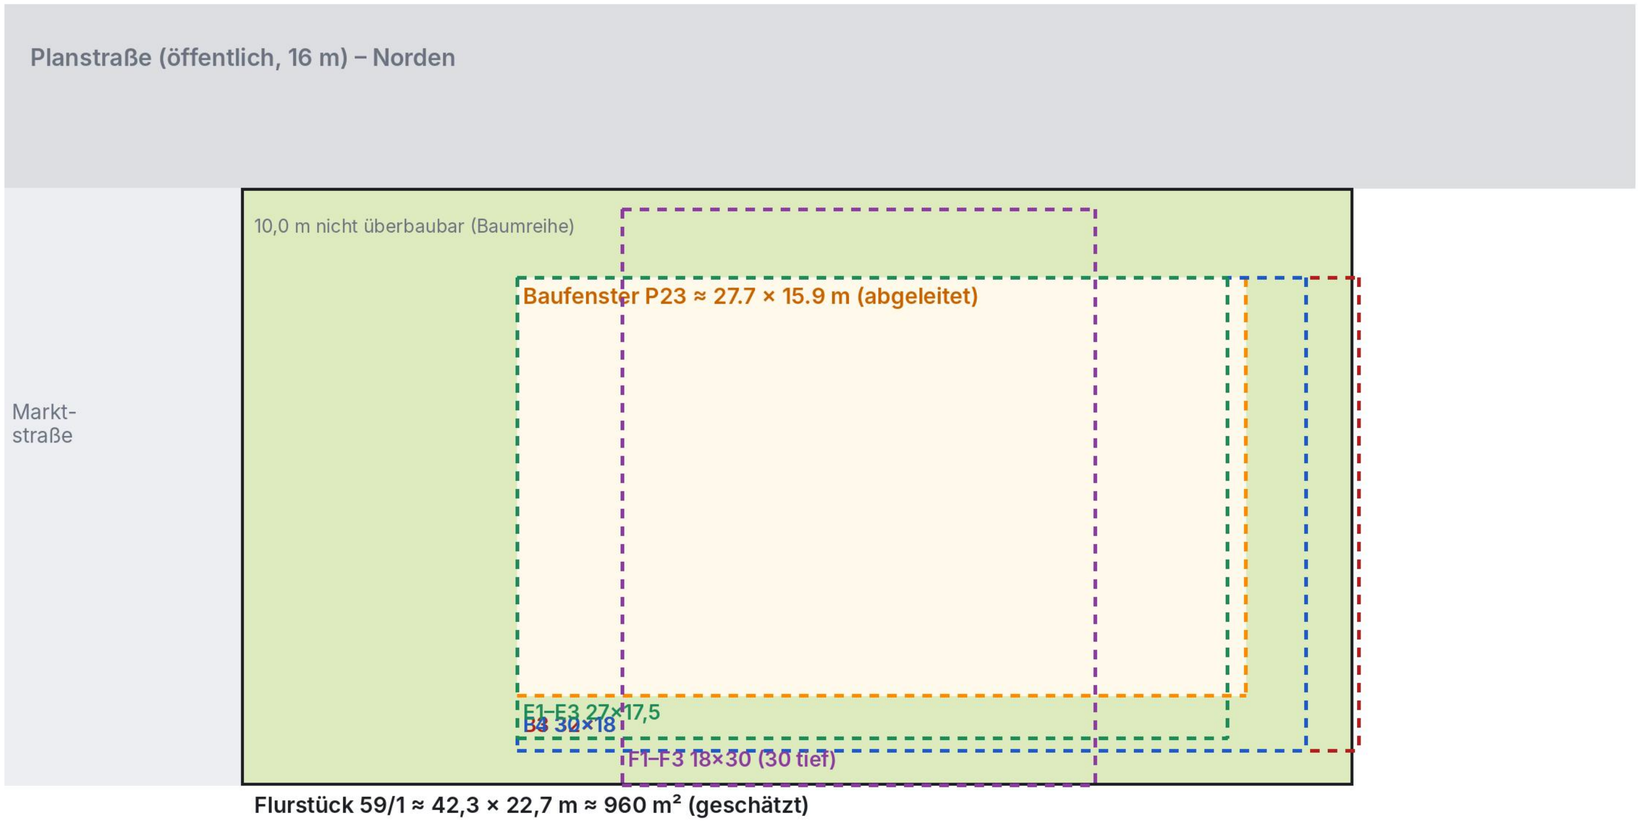


EG-Fußabdruck	Baufenster 27,7 × 15,9
B3 / A–D: 32 × 18 m	passt NICHT
E1–E3: 27 × 17,5 m	passt NICHT
E4: 27 × 12,5 m	passt
F1–F3: 18 × 30 m	passt NICHT
F4: 30 × 18 m	passt NICHT
G1: 27,7 × 15,9 m	passt

Zusätzlich: EG 540 m² übersteigt das Baufenster (439 m²) um 101 m² (+23 %). Die GRZ 0,6 erlaubt rechnerisch 576 m² Grundfläche – begrenzend wirkt die Baugrenze. Ein Vorbau über die Baugrenze hinaus ist unzulässig; ein umlaufender Vorbau müsste innerhalb des Baufensters bleiben.

Höhenrahmen: B3 (+9,90 m) und E/F (+12,00 m)

VARIANTE E · NICHT FESTGELEGT

Schnittschema · Plan A (2023): H 15 m/TH 9,80 m · Plan B (Entwurf 2026): H 12 m/TH 6,50 m · Bezugspunkt OK Fahrbahn

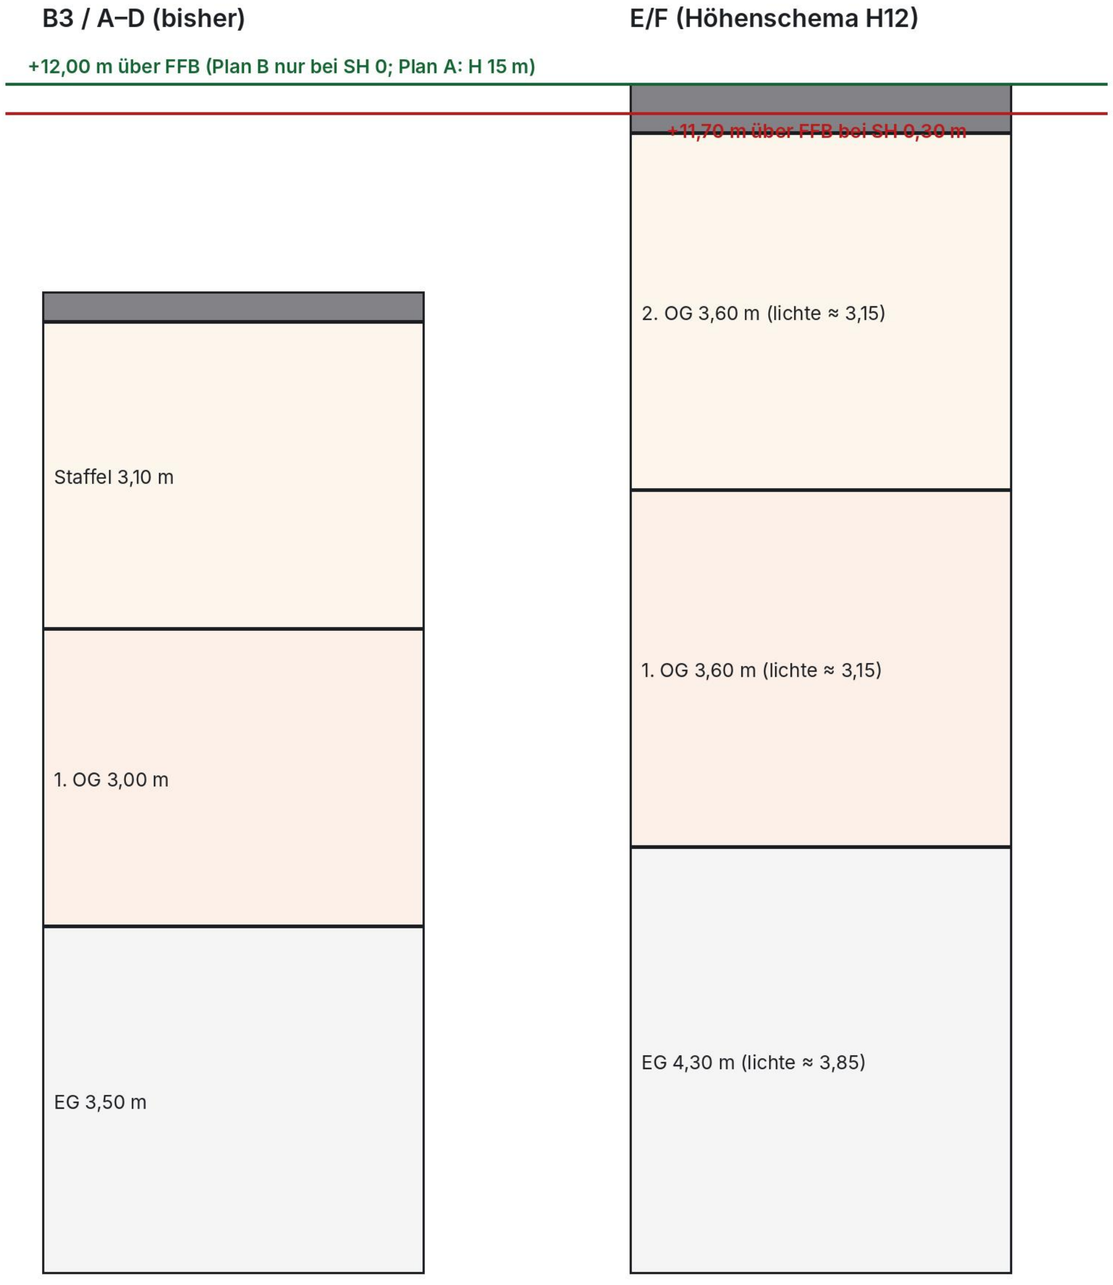

Aspekt	Aussage (Quelle: B-Plan Nr. 123 rechtskräftig 2023 und 1. Änderung Entwurf 2026)
Bezugspunkt (beide Pläne)	H über Oberkante Fahrbahn der nächsten ausgebauten Erschließungsstraße in der Mitte vor dem Baukörper (nicht über FFB); FFB EG max. 0,30 m darüber (SH). Fahrbahnhöhe unbekannt.
Plan A: rechtskräftig 2023 (MI 3 / MI 1)	II–III, TH max. 9,80 m, H max. 15,00 m. Attika +12,0 m über FFB passt zu H; die Wandhöhe ≈ +11,5 m überschreitet aber TH 9,80 m.
Plan B: Entwurf 2026 / MI 2	II zwingend, TH 6,50 m, H 12,00 m (max. +11,70 m über FFB bei SH 0,30 m). Für MI 3 nicht einschlägig; hier hypothetisch.
Dach (beide Pläne)	Hauptdach geneigt ≥ 38°; Flachdach nur Verbindungsbauten/≤ 70 m² → dreigeschossige Flachdachbauten brauchen Befreiung.
Nutzung der Reserve	Statt eines vierten Geschosses (nicht angenommen) fließt die Höhe in Geschosshöhen (lichte ≈ 3,15 m); Wohnfläche steigt dadurch nicht.

Überblick E1–E4

VARIANTE E · NICHT FESTGELEGT


Standardmix · alle Werte vorläufig · Referenz B3 (A)

Kennzahl	A B3	E1 Vorbau bis Attika (Staffel dec	E2 Staffel 1,50 m zurück	E3 Staffel 3,00 m zurück	E4 zweireihiges Parken, kleineres
Staffelrücksprung	0,8 m	0.0 m	1.5 m	3.0 m	1.5 m
Grundfläche EG / 1. OG / 2. OG (m²)	576 / 660 / 539	492 / 768 / 768	492 / 768 / 609	492 / 768 / 468	358 / 608 / 464
Wohnfläche netto (m²)	846	1.084	960	852	727
Δ Wohnfläche gg. A	±0	+238 (+28 %)	+114 (+13 %)	+6 (+1 %)	-119 (-14 %)
Wohnungen	16	18	16	15	16
Gastraum (m²) / Plätze innen	280 / 120	281 / 120	281 / 120	281 / 120	198 / 85
Stellplätze gezeichnet / nutzbar	11 / 11	9 / 9	9 / 9	9 / 9	21 / 21
erforderlich § 47 (Spanne / Mittel)	11,4–16,9 / 13,6	11,4–16,9 / 13,6	11,4–16,9 / 13,6	11,4–16,9 / 13,6	8,5–12,5 / 10,1
optional Wohnen (0,5–1,5 je WE)	8–24	9–27	8–24	8–22	8–24
Säulen	0	22	22	22	20
Höhe Attika	9,90 m	12,00 m (Bezug offen)	12,00 m (Bezug offen)	12,00 m (Bezug offen)	12,00 m (Bezug offen)

E1 – Vorbau bis Attika (Staffel deckungsgleich)

Entwurfsstudie Baufeld 3 · Konzeptvariante, keine Genehmigungsplanung

VARIANTE E · NICHT FESTGELEGT

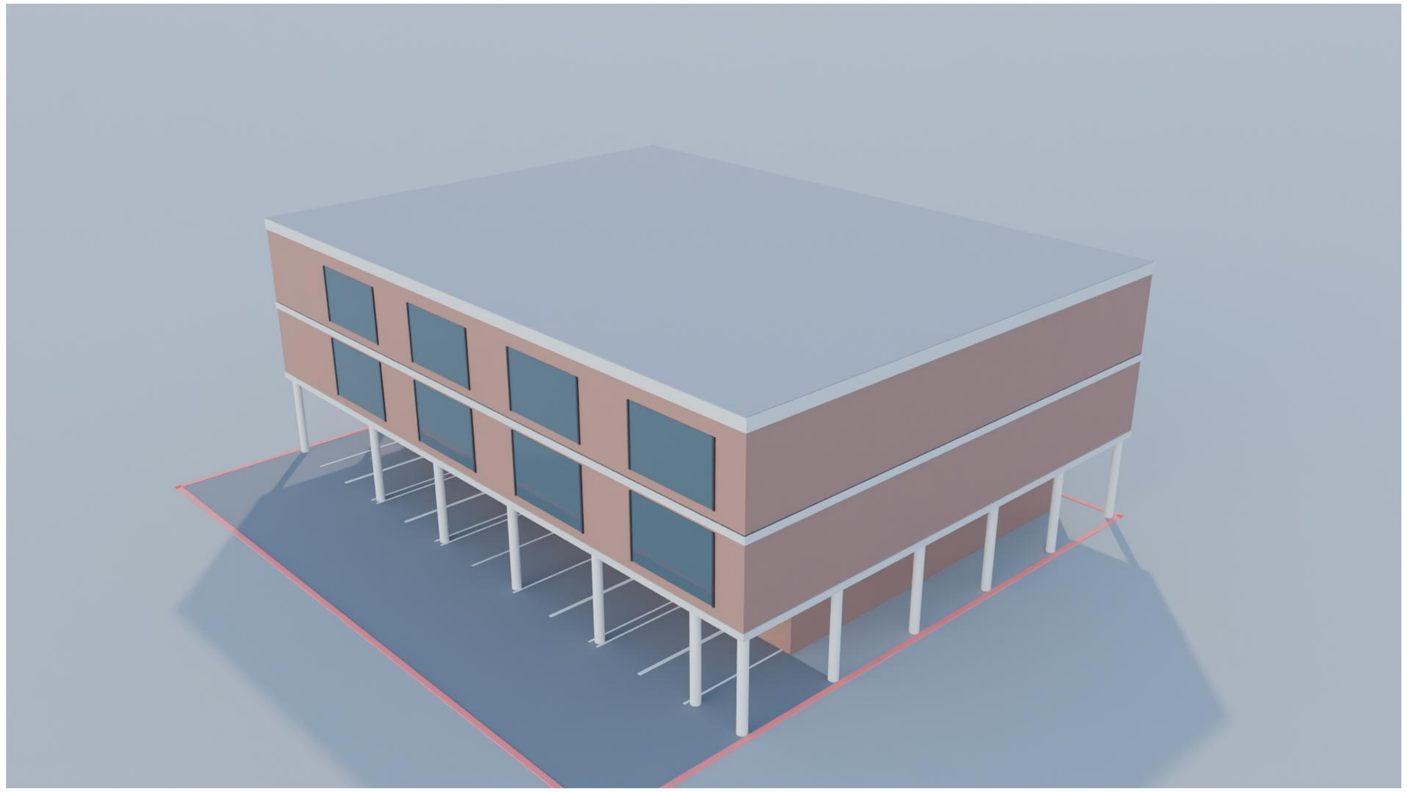

12,00 m Gesamthöhe, drei Geschosse; 1. und 2. OG kragen auf allen vier Seiten über das Erdgeschoss (vorn 1,50 m Arkade, seitlich 2,50 m, hinten 5,00 m über der Stellplatzreihe) und sind deckungsgleich bis zur Attika; Säulen am Rand.

Kennzahl	Wert (vorläufig)
Höhe	12,00 m Attika (EG 4,30 · 1. OG 3,60 · 2. OG 3,60 · Dach/Attika 0,50), 3 Geschosse – Höhenbezug offen
Grundfläche EG / 1. OG / 2. OG	492 / 768 / 768 m²
Außenmaße EG / 1. OG / 2. OG	29.5 × 17.5 / 32.0 × 24.0 / 32.0 × 24.0 m
Wohnfläche netto (geschätzt)	1.084 m²
Wohnungen Standardmix	18 WE (9 + 9), 54–68 m², Ø 60 m²
Gewerbe	EG 492 m²; Gastraum ca. 281 m² (≈ 120 Plätze), Terrasse/Arkade ≈ 28 Plätze, Büro 56 m²
Säulen	22 Säulen Ø 0,40 m; Paare 5,4 m (zwei Stellplätze + Säule)
Stellplätze gezeichnet	9: 9 voll nutzbar, 0 eingeschränkt, 0 Konflikt
Stellplätze erforderlich (§ 47 NBauO)	11,4–16,9, Mittel 13,6 (nur Gastro + Büro; Wohnen 0)
Stellplätze optional (Komfort/Markt)	Wohnen 0,5–1,5 je WE = 9–27; Komfortziel gesamt ≈ 32
Überstand über Grundstück H1	0,00 m

Alle Maße sind Planungsannahmen: Stellplatz 2,50 × 5,00 m, Fahrgasse 6,00 m, Säule Ø 0,40 m, Grundstück 32 × 30 m (Hypothese; die städtischen Unterlagen Seite 13/15/16 liegen nur als Beschreibung vor, nicht als Foto), Zufahrt = Annahme. Wohnfläche = 0,88 × Wohnstreifen, schematisch. Nichts ist genehmigt, bemessen oder abgestimmt.


E1: Lageplan mit Gebäude, Säulen, Zufahrt und Stellplätzen

VARIANTE E · NICHT FESTGELEGT

E1 – Vorbau bis Attika (Staffel deckungsgleich) · grün = Stellplatz funktioniert, orange = eingeschränkt, rot = Konflikt, rosa = nur rechnerisch verbleibende Fläche

Lageplan E1 – Gebäude, Säulen, Zufahrt, Stellplätze

Grundstück H1 32 × 30 m HYPOTHETISCH (Zuschnitt/Baugrenzen nicht belegt) · Stellplatz 2,50 × 5,00 m, Fahrgasse 6,00 m = Planungsannahmen · Zufahrt = Annahme

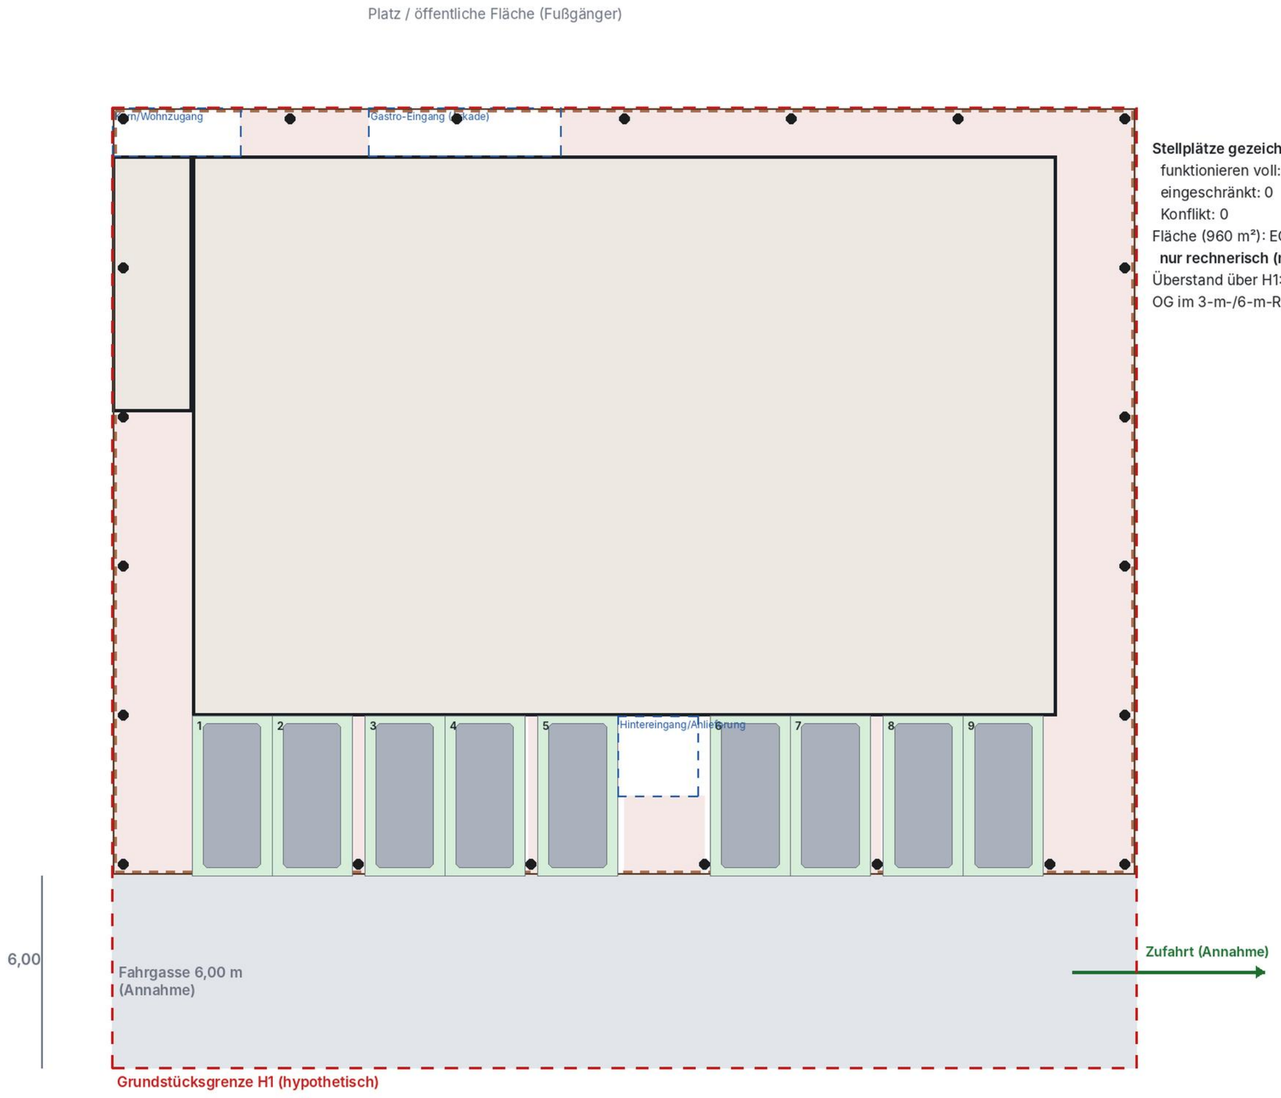

Stellplätze gezeichnet: 9
funktionieren voll: 9
eingeschränkt: 0
Konflikt: 0
Fläche (960 m²): EG 492 · Stellpl. 112 · Fahrgasse 192 · Zugänge 21
nur rechnerisch (nicht nutzbar): 142 m²
Überstand über H1: 0.00 m
OG im 3-m-/6-m-Randstreifen: 222 / 408 m²

braun gestrichelt: 1./2. OG über dem EG (Vorbau) · blau gestrichelt: Eingangszonen

Stellplatz funktioniert · eingeschränkt · Konflikt · Fahrgasse · nur rechnerisch verbleibend

Stellplatzprüfung	
Gezeichnet	9
funktionieren voll	9
eingeschränkt	0
Konflikt	0
Min. Nutzbreite 90°	2.50 m
Fahrgasse	6.0 m (frei)
Flächenbilanz 960 m²	
Erdgeschoss	492,5 m²
Stellplätze	112,5 m²
Fahrgasse	192,0 m²
Zugangszonen	21,2 m²
nur rechnerisch	141,8 m²

- Geometrische Prüfung ohne Schleppkurven; 90°-Stellplätze 2,50 × 5,00 m und Fahrgasse 6,00 m sind Planungsannahmen
- Zufahrt (Lage der Straße) ist Annahme
- Feuerwehrzufahrt/Aufstellflächen unter dem Vorbau nicht nachgewiesen (Prüfbedarf)


E1: Grundrisse EG, 1. OG, 2. OG

E1 – Vorbau bis Attika (Staffel deckungsgleich) · schematisch

VARIANTE E · NICHT FESTGELEGT

Erdgeschoss


E1: Erdgeschoss (schematisch)
Grundriss schematisch · Wohnungsaufteilung = Streifenmodell (Mittelgang 2,0 m), netto = 0,88 × brutto · Säulen Ø 0,40 m · Grundstück H1 hypothetisch

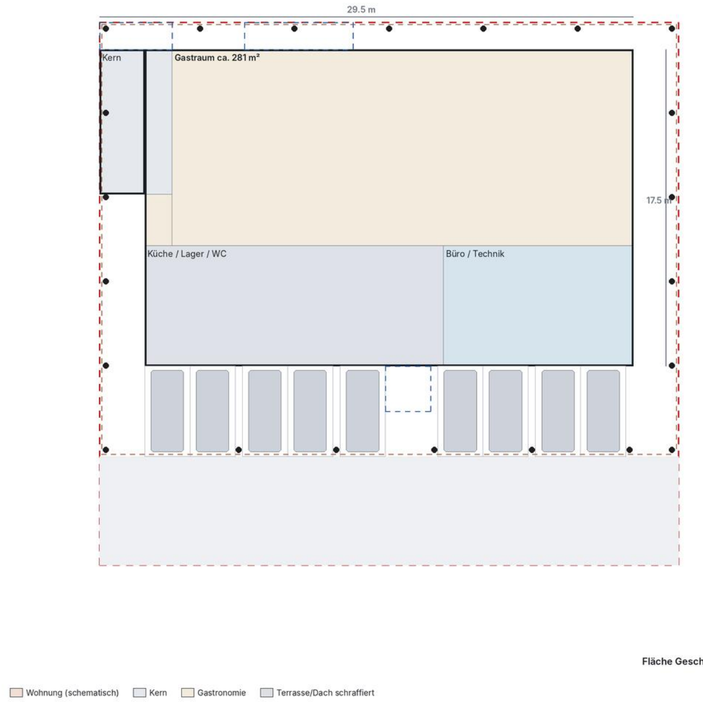

Fläche Geschoss 492 m²

1. Obergeschoss


E1: 1. Obergeschoss (schematisch)
Grundriss schematisch · Wohnungsaufteilung = Streifenmodell (Mittelgang 2,0 m), netto = 0,88 × brutto · Säulen Ø 0,40 m · Grundstück H1 hypothetisch

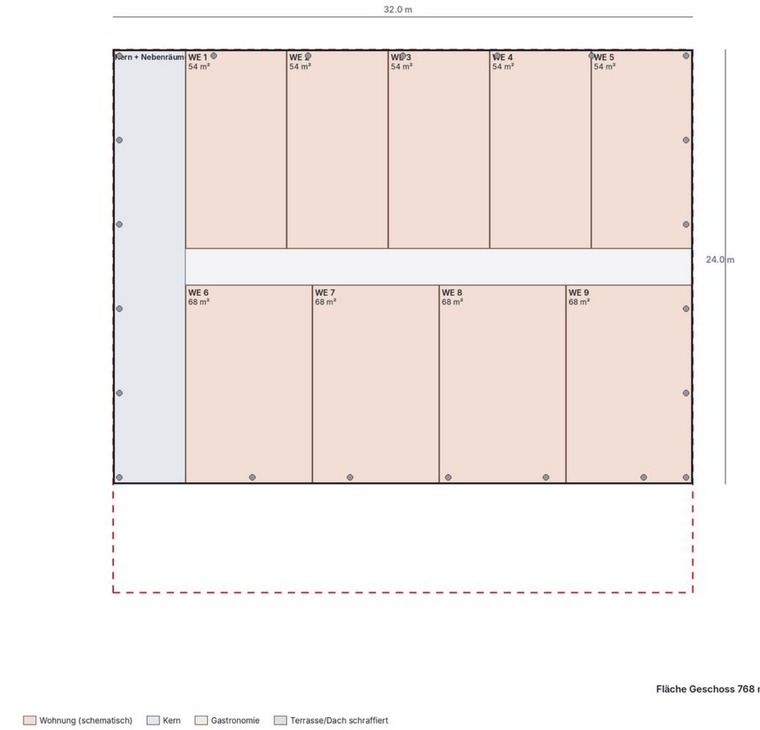

Fläche Geschoss 768 m²

2. Obergeschoss

E1: 2. Obergeschoss (schematisch)
Grundriss schematisch · Wohnungsaufteilung = Streifenmodell (Mittelgang 2,0 m), netto = 0,88 × brutto · Säulen Ø 0,40 m · Grundstück H1 hypothetisch

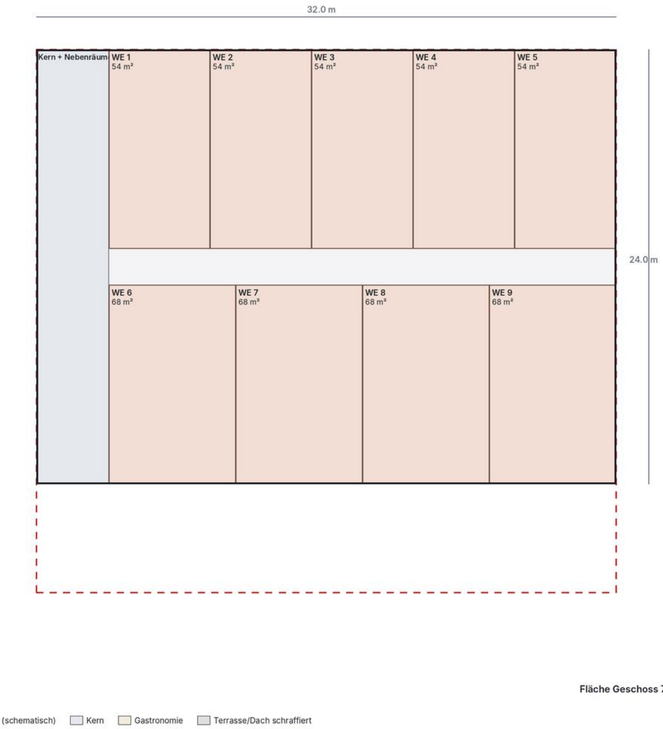

Fläche Geschoss 768 m²

Wohnung (schematisch) Kern Gastronomie Terrasse/Dach schraffiert

E1: vier Fassaden


VARIANTE E · NICHT FESTGELEGT

E1 – Vorbau bis Attika (Staffel deckungsgleich) · orthogonale Ansichten aus dem 3D-Modell

Vorderfassade (Platzseite)



Rückfassade

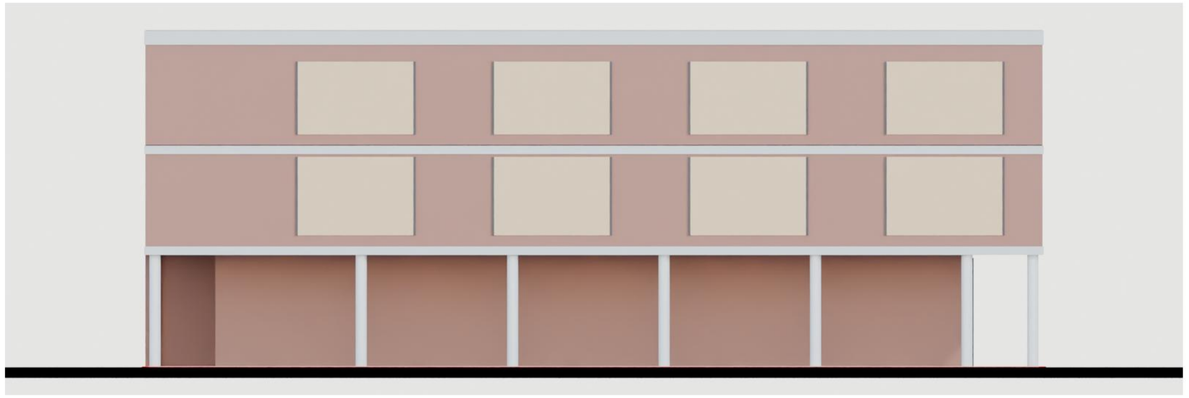

Seitenfassade West



Seitenfassade Ost



E1: Gebäudeschnitt mit Geschosshöhen und 3D-Ansichten

VARIANTE E · NICHT FESTGELEGT


E1 – Vorbau bis Attika (Staffel deckungsgleich)


E1: Gebäudeschnitt mit Geschosshöhen (schematisch)

Platzseite links, Rückseite rechts · Schnitt bei x = 16.25 m · Höhenbezug ±0,00 = OK Fertigfußboden EG (Planbezug Blatt 14) – Bezugspunkt der Stadt für die 12,00 m ist NICHT belegt



Geschosshöhen: EG 4,30 m · 1. OG 3,60 m · 2. OG 3,60 m · Dach/Attika 0,50 m = 12,00 m. Reserve 0,00 m. Die 12,00 m gelten erst als eingehalten, wenn der baurechtliche Höhenbezug geklärt ist.
Säulen im Schnittbereich: 2 · Säulen insgesamt: 22 · Vorbau-Unterkante +4,00 m (Decke 0,30 m)

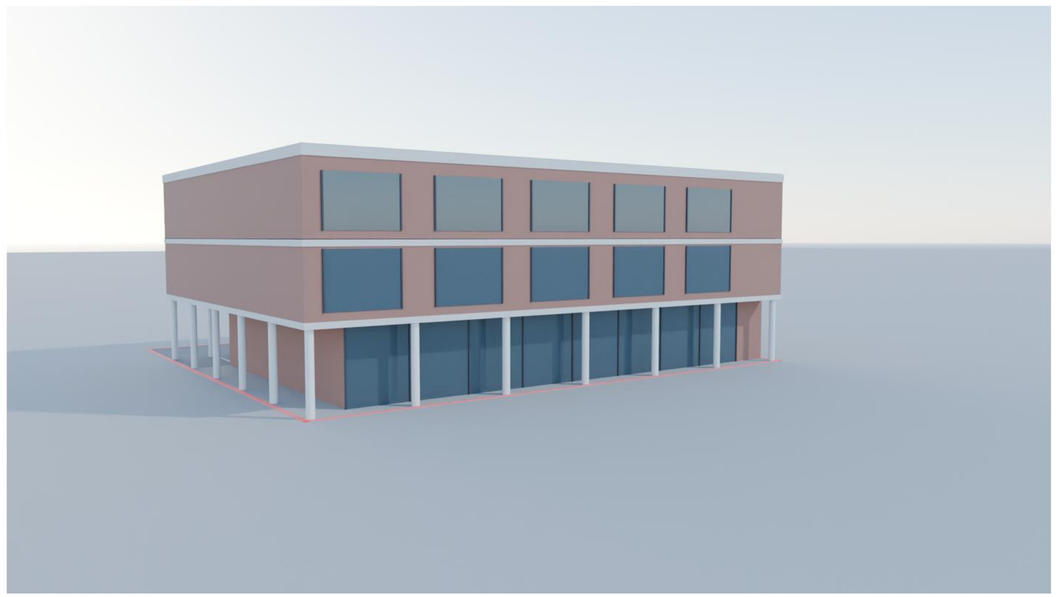


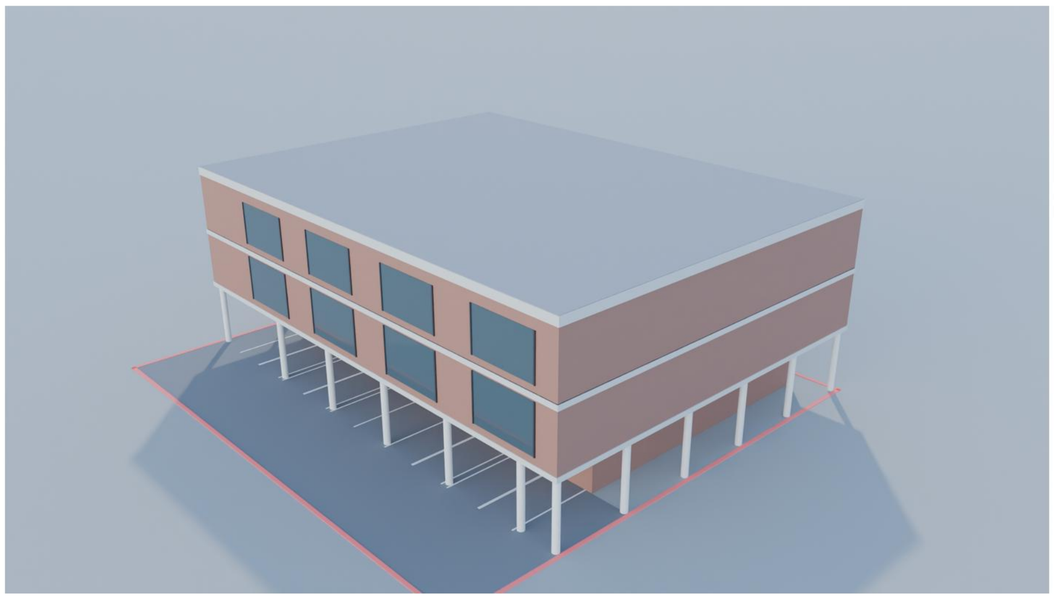

E2 – Staffel 1,50 m zurück

Entwurfsstudie Baufeld 3 · Konzeptvariante, keine Genehmigungsplanung

VARIANTE E · NICHT FESTGELEGT

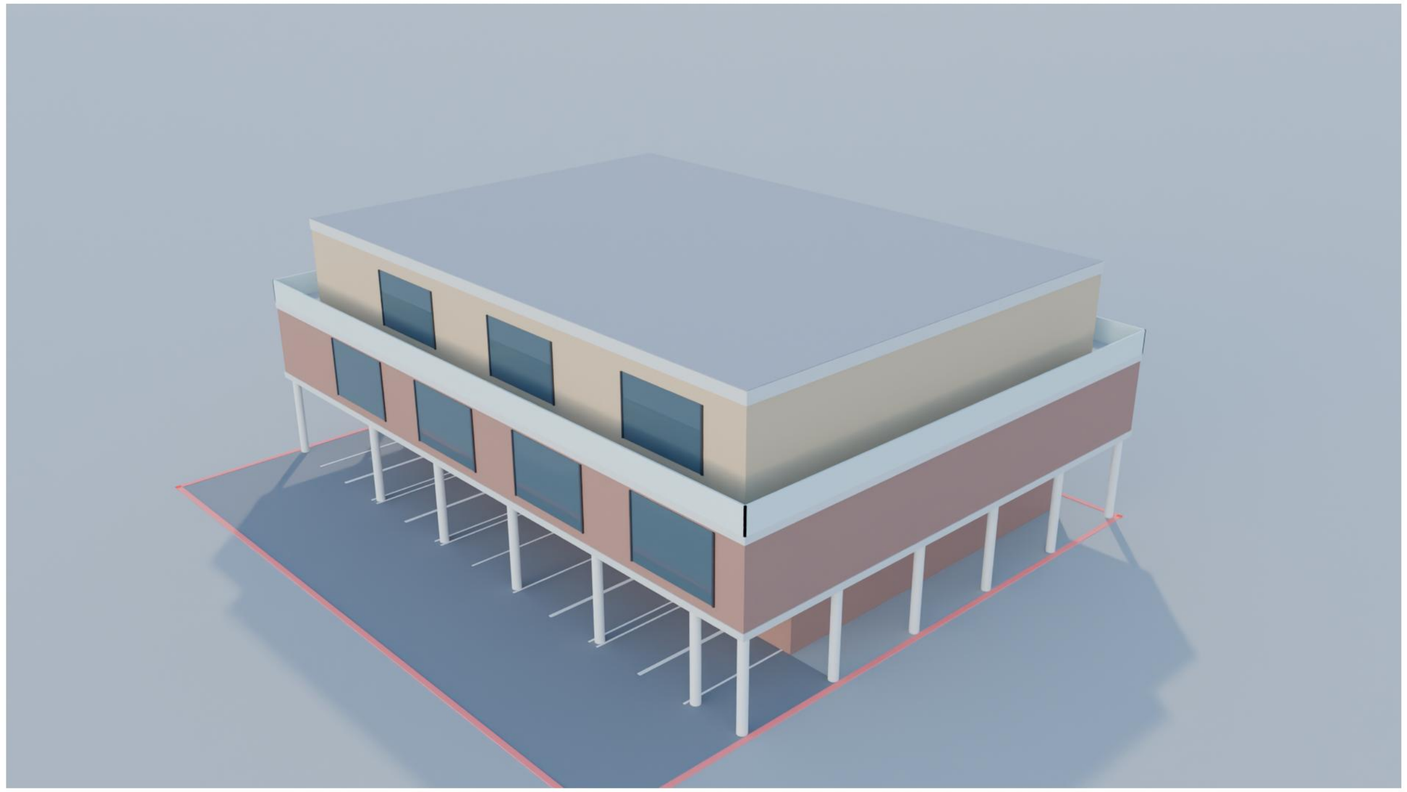

Wie E1, das 2. OG springt rundum 1,50 m hinter die Kante des 1. OG zurück (umlaufende Dachterrasse).

Kennzahl	Wert (vorläufig)
Höhe	12,00 m Attika (EG 4,30 · 1. OG 3,60 · 2. OG 3,60 · Dach/Attika 0,50), 3 Geschosse – Höhenbezug offen
Grundfläche EG / 1. OG / 2. OG	492 / 768 / 609 m²
Außenmaße EG / 1. OG / 2. OG	29.5 × 17.5 / 32.0 × 24.0 / 29.0 × 21.0 m
Wohnfläche netto (geschätzt)	960 m²
Wohnungen Standardmix	16 WE (9 + 7), 52–70 m², Ø 60 m²
Gewerbe	EG 492 m²; Gastraum ca. 281 m² (≈ 120 Plätze), Terrasse/Arkade ≈ 28 Plätze, Büro 56 m²
Säulen	22 Säulen Ø 0,40 m; Paare 5,4 m (zwei Stellplätze + Säule)
Stellplätze gezeichnet	9: 9 voll nutzbar, 0 eingeschränkt, 0 Konflikt
Stellplätze erforderlich (§ 47 NBauO)	11,4–16,9, Mittel 13,6 (nur Gastro + Büro; Wohnen 0)
Stellplätze optional (Komfort/Markt)	Wohnen 0,5–1,5 je WE = 8–24; Komfortziel gesamt ≈ 30
Überstand über Grundstück H1	0,00 m

Alle Maße sind Planungsannahmen: Stellplatz 2,50 × 5,00 m, Fahrgasse 6,00 m, Säule Ø 0,40 m, Grundstück 32 × 30 m (Hypothese; die städtischen Unterlagen Seite 13/15/16 liegen nur als Beschreibung vor, nicht als Foto), Zufahrt = Annahme. Wohnfläche = 0,88 × Wohnstreifen, schematisch. Nichts ist genehmigt, bemessen oder abgestimmt.


E2: Lageplan mit Gebäude, Säulen, Zufahrt und Stellplätzen

VARIANTE E · NICHT FESTGELEGT

E2 – Staffel 1,50 m zurück · grün = Stellplatz funktioniert, orange = eingeschränkt, rot = Konflikt, rosa = nur rechnerisch verbleibende Fläche

Lageplan E2 – Gebäude, Säulen, Zufahrt, Stellplätze

Grundstück H1 32 × 30 m HYPOTHETISCH (Zuschnitt/Baugrenzen nicht belegt) · Stellplatz 2,50 × 5,00 m, Fahrgasse 6,00 m = Planungsannahmen · Zufahrt = Annahme

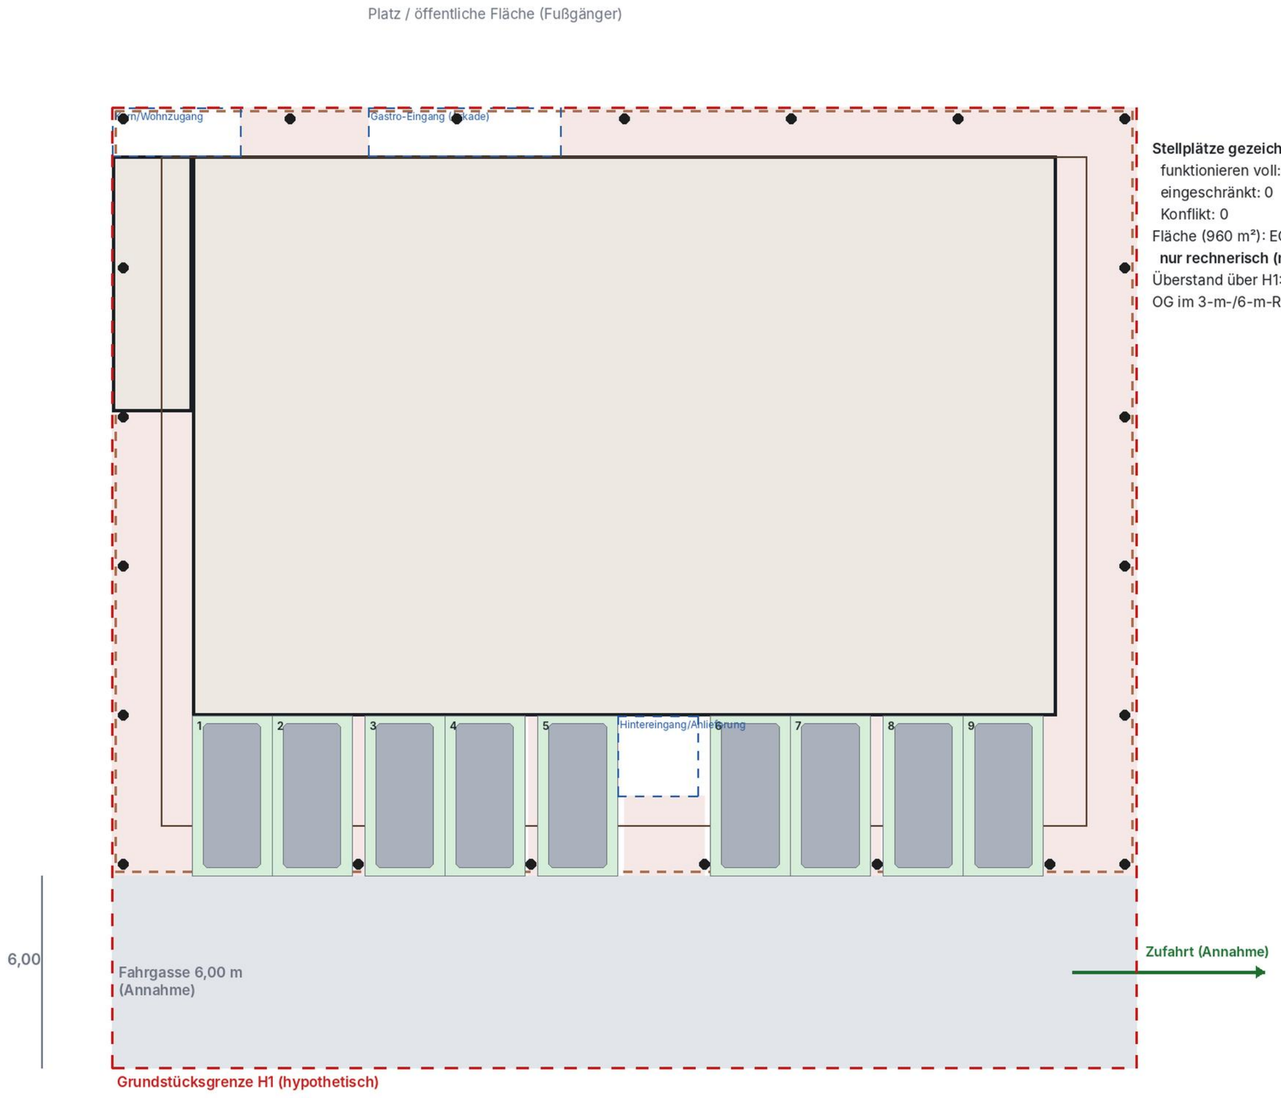

Stellplätze gezeichnet: 9
funktionieren voll: 9
eingeschränkt: 0
Konflikt: 0
Fläche (960 m²): EG 492 · Stellpl. 112 · Fahrgasse 192 · Zugänge 21
nur rechnerisch (nicht nutzbar): 142 m²
Überstand über H1: 0.00 m
OG im 3-m-/6-m-Randstreifen: 222 / 408 m²

braun gestrichelt: 1./2. OG über dem EG (Vorbau) · blau gestrichelt: Eingangszonen

Stellplatz funktioniert · eingeschränkt · Konflikt · Fahrgasse · nur rechnerisch verbleibend

Stellplatzprüfung	
Gezeichnet	9
funktionieren voll	9
eingeschränkt	0
Konflikt	0
Min. Nutzbreite 90°	2.50 m
Fahrgasse	6.0 m (frei)
Flächenbilanz 960 m²	
Erdgeschoss	492,5 m²
Stellplätze	112,5 m²
Fahrgasse	192,0 m²
Zugangszonen	21,2 m²
nur rechnerisch	141,8 m²

- Geometrische Prüfung ohne Schleppkurven; 90°-Stellplätze 2,50 × 5,00 m und Fahrgasse 6,00 m sind Planungsannahmen
- Zufahrt (Lage der Straße) ist Annahme
- Feuerwehrzufahrt/Aufstellflächen unter dem Vorbau nicht nachgewiesen (Prüfbedarf)


E2: Grundrisse EG, 1. OG, 2. OG

E2 – Staffel 1,50 m zurück · schematisch

VARIANTE E · NICHT FESTGELEGT

Erdgeschoss


E2: Erdgeschoss (schematisch)
Grundriss schematisch · Wohnungsaufteilung = Streifenmodell (Mittelgang 2,0 m), netto = 0,88 × brutto · Säulen Ø 0,40 m · Grundstück H1 hypothetisch

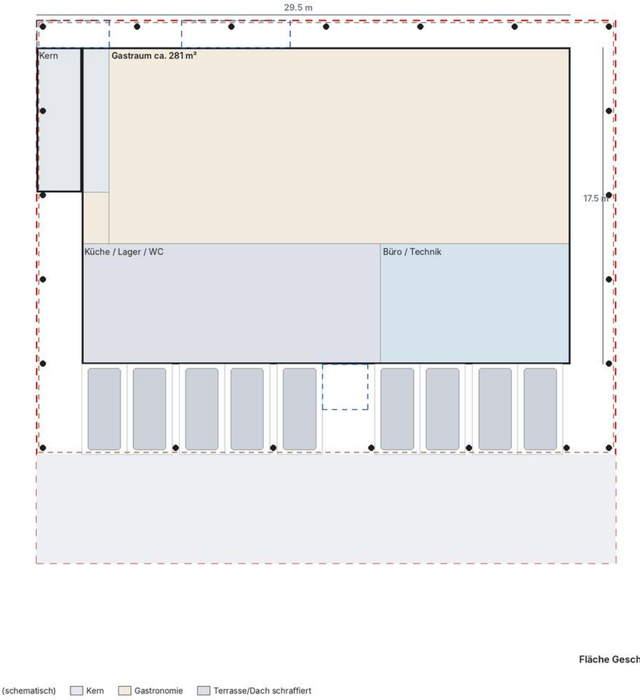

Fläche Geschoss 492 m²

1. Obergeschoss


E2: 1. Obergeschoss (schematisch)
Grundriss schematisch · Wohnungsaufteilung = Streifenmodell (Mittelgang 2,0 m), netto = 0,88 × brutto · Säulen Ø 0,40 m · Grundstück H1 hypothetisch

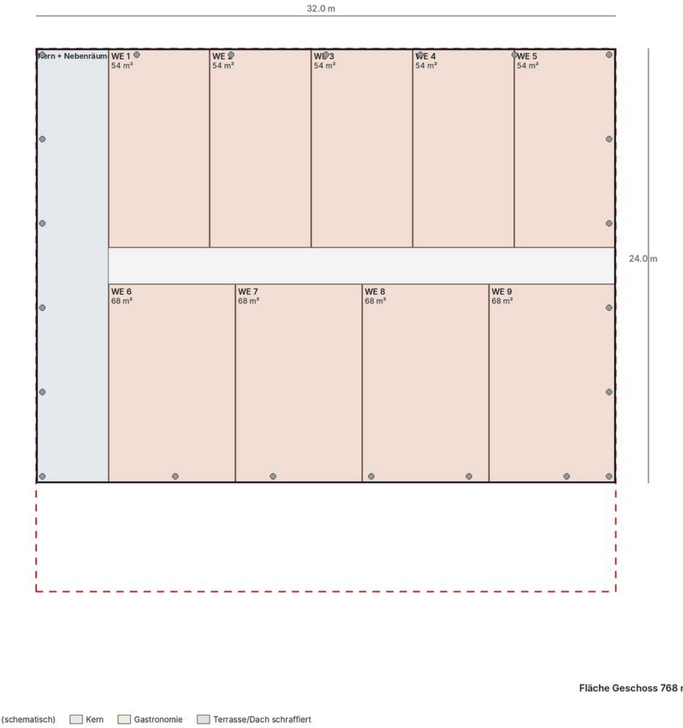

Fläche Geschoss 768 m²

2. Obergeschoss

E2: 2. Obergeschoss (Staffel) (schematisch)
Grundriss schematisch · Wohnungsaufteilung = Streifenmodell (Mittelgang 2,0 m), netto = 0,88 × brutto · Säulen Ø 0,40 m · Grundstück H1 hypothetisch

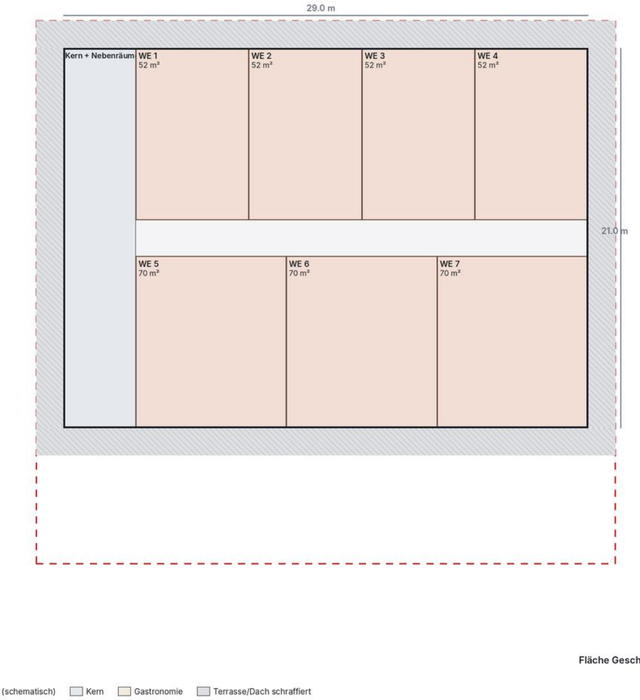

Fläche Geschoss 609 m²

Wohnung (schematisch) Kern Gastronomie Terrasse/Dach schraffiert

E2: vier Fassaden


VARIANTE E · NICHT FESTGELEGT

E2 – Staffel 1,50 m zurück · orthogonale Ansichten aus dem 3D-Modell

Vorderfassade (Platzseite)



Rückfassade

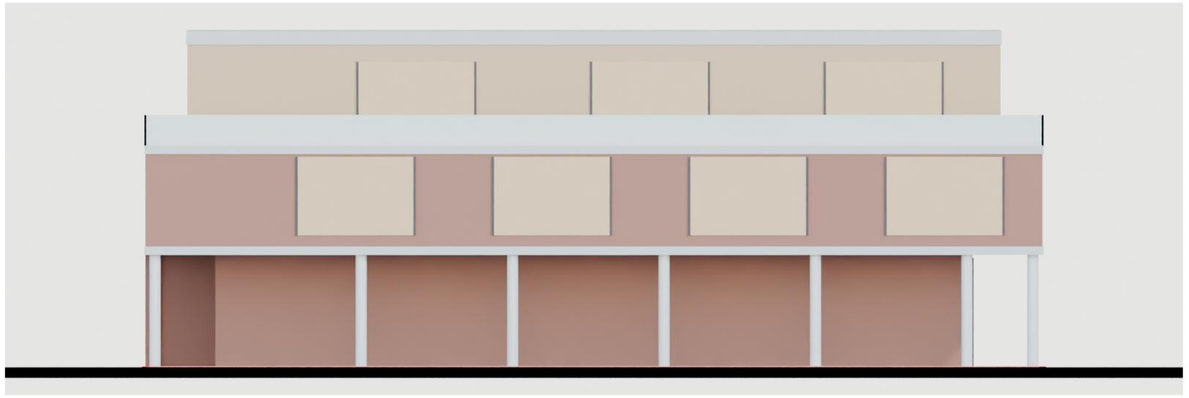

Seitenfassade West



Seitenfassade Ost



E2: Gebäudeschnitt mit Geschosshöhen und 3D-Ansichten

E2 – Staffel 1,50 m zurück


VARIANTE E · NICHT FESTGELEGT


E2: Gebäudeschnitt mit Geschosshöhen (schematisch)

Platzseite links, Rückseite rechts · Schnitt bei x = 16.25 m · Höhenbezug ±0,00 = OK Fertigfußboden EG (Planbezug Blatt 14) – Bezugspunkt der Stadt für die 12,00 m ist NICHT belegt



Geschosshöhen: EG 4,30 m · 1. OG 3,60 m · 2. OG 3,60 m · Dach/Attika 0,50 m = 12,00 m. Reserve 0,00 m. Die 12,00 m gelten erst als eingehalten, wenn der baurechtliche Höhenbezug geklärt ist.
Säulen im Schnittbereich: 2 · Säulen insgesamt: 22 · Vorbau-Unterkante +4,00 m (Decke 0,30 m)

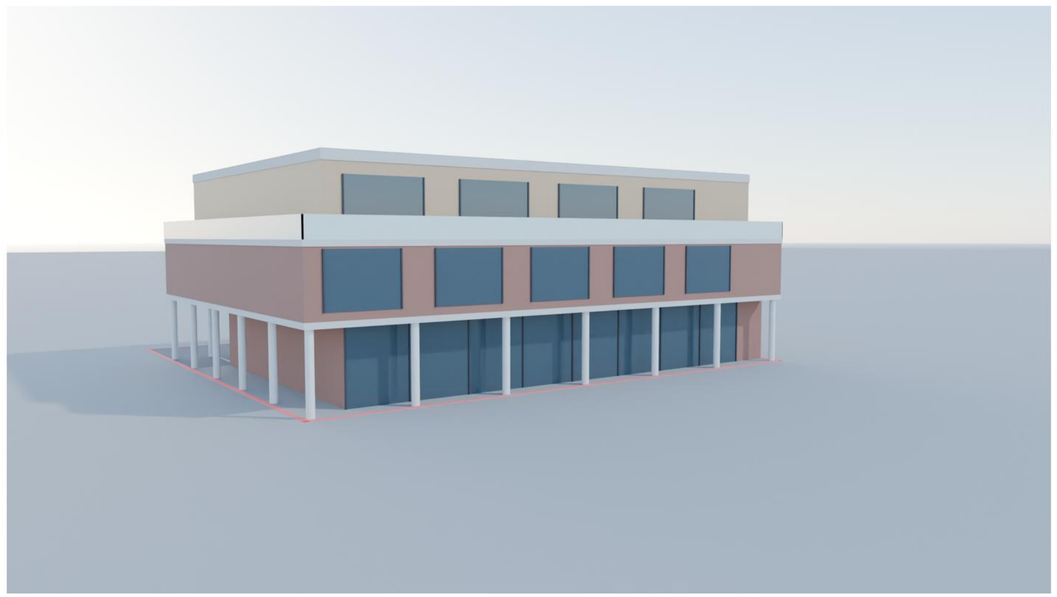


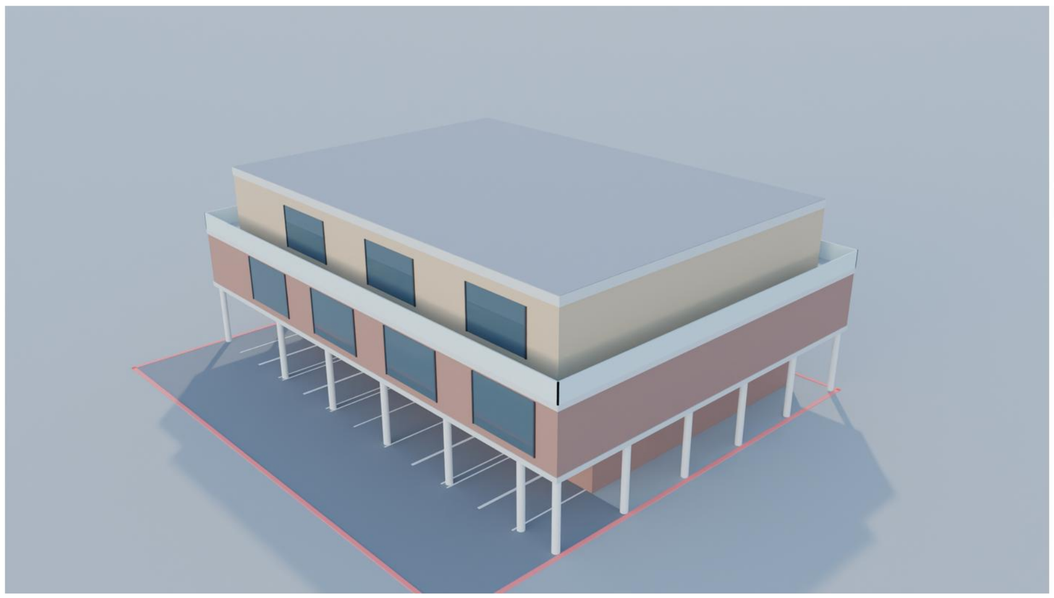

E3 – Staffel 3,00 m zurück

Entwurfsstudie Baufeld 3 · Konzeptvariante, keine Genehmigungsplanung

VARIANTE E · NICHT FESTGELEGT

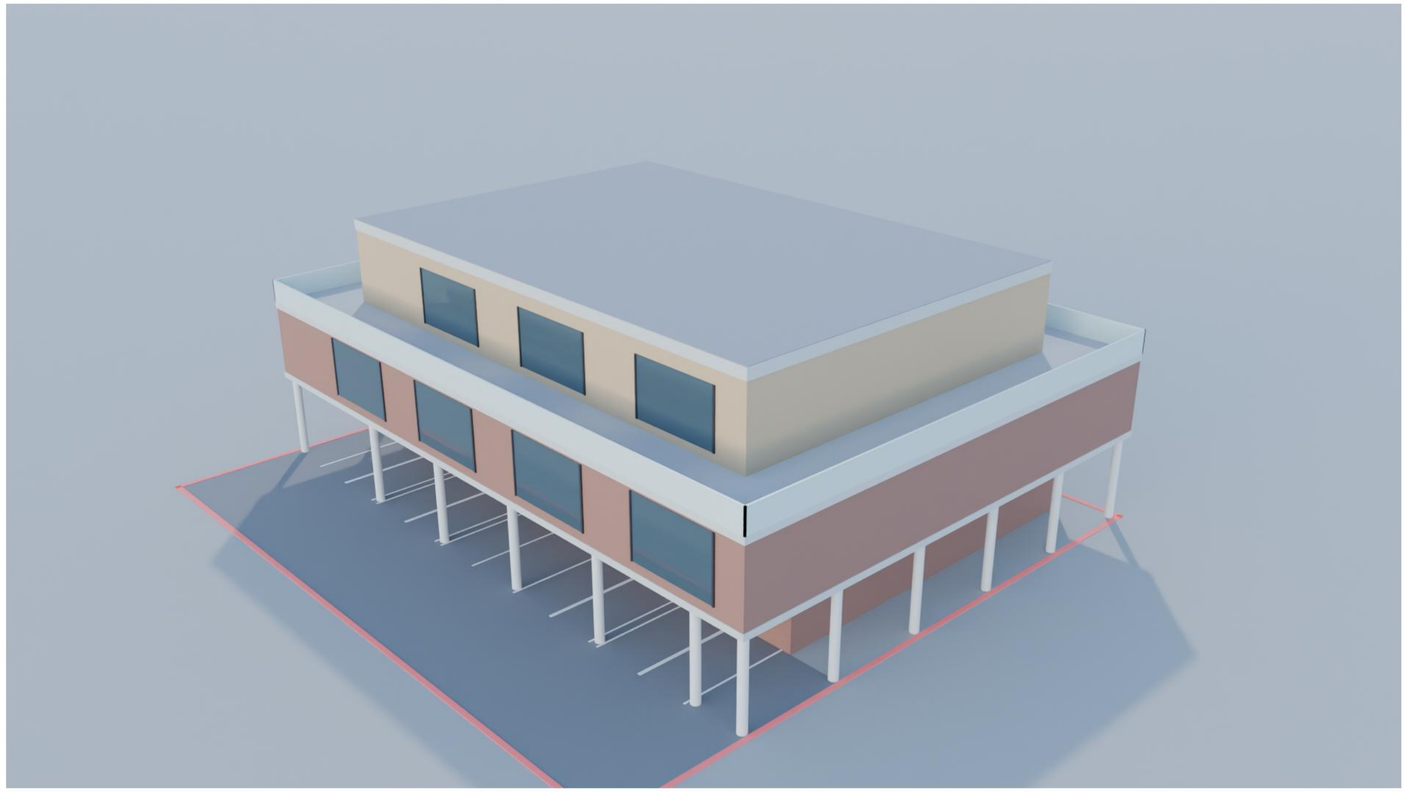

Wie E1, das 2. OG springt rundum 3,00 m zurück (breite umlaufende Dachterrasse, kleineres Staffelgeschoss).

Kennzahl	Wert (vorläufig)
Höhe	12,00 m Attika (EG 4,30 · 1. OG 3,60 · 2. OG 3,60 · Dach/Attika 0,50), 3 Geschosse – Höhenbezug offen
Grundfläche EG / 1. OG / 2. OG	492 / 768 / 468 m²
Außenmaße EG / 1. OG / 2. OG	29.5 × 17.5 / 32.0 × 24.0 / 26.0 × 18.0 m
Wohnfläche netto (geschätzt)	852 m²
Wohnungen Standardmix	15 WE (9 + 6), 52–68 m², Ø 57 m²
Gewerbe	EG 492 m²; Gastraum ca. 281 m² (≈ 120 Plätze), Terrasse/Arkade ≈ 28 Plätze, Büro 56 m²
Säulen	22 Säulen Ø 0,40 m; Paare 5,4 m (zwei Stellplätze + Säule)
Stellplätze gezeichnet	9: 9 voll nutzbar, 0 eingeschränkt, 0 Konflikt
Stellplätze erforderlich (§ 47 NBauO)	11,4–16,9, Mittel 13,6 (nur Gastro + Büro; Wohnen 0)
Stellplätze optional (Komfort/Markt)	Wohnen 0,5–1,5 je WE = 8–22; Komfortziel gesamt ≈ 29
Überstand über Grundstück H1	0,00 m

Alle Maße sind Planungsannahmen: Stellplatz 2,50 × 5,00 m, Fahrgasse 6,00 m, Säule Ø 0,40 m, Grundstück 32 × 30 m (Hypothese; die städtischen Unterlagen Seite 13/15/16 liegen nur als Beschreibung vor, nicht als Foto), Zufahrt = Annahme. Wohnfläche = 0,88 × Wohnstreifen, schematisch. Nichts ist genehmigt, bemessen oder abgestimmt.


E3: Lageplan mit Gebäude, Säulen, Zufahrt und Stellplätzen

VARIANTE E · NICHT FESTGELEGT

E3 – Staffel 3,00 m zurück · grün = Stellplatz funktioniert, orange = eingeschränkt, rot = Konflikt, rosa = nur rechnerisch verbleibende Fläche

Lageplan E3 – Gebäude, Säulen, Zufahrt, Stellplätze

Grundstück H1 32 × 30 m HYPOTHETISCH (Zuschnitt/Baugrenzen nicht belegt) · Stellplatz 2,50 × 5,00 m, Fahrgasse 6,00 m = Planungsannahmen · Zufahrt = Annahme

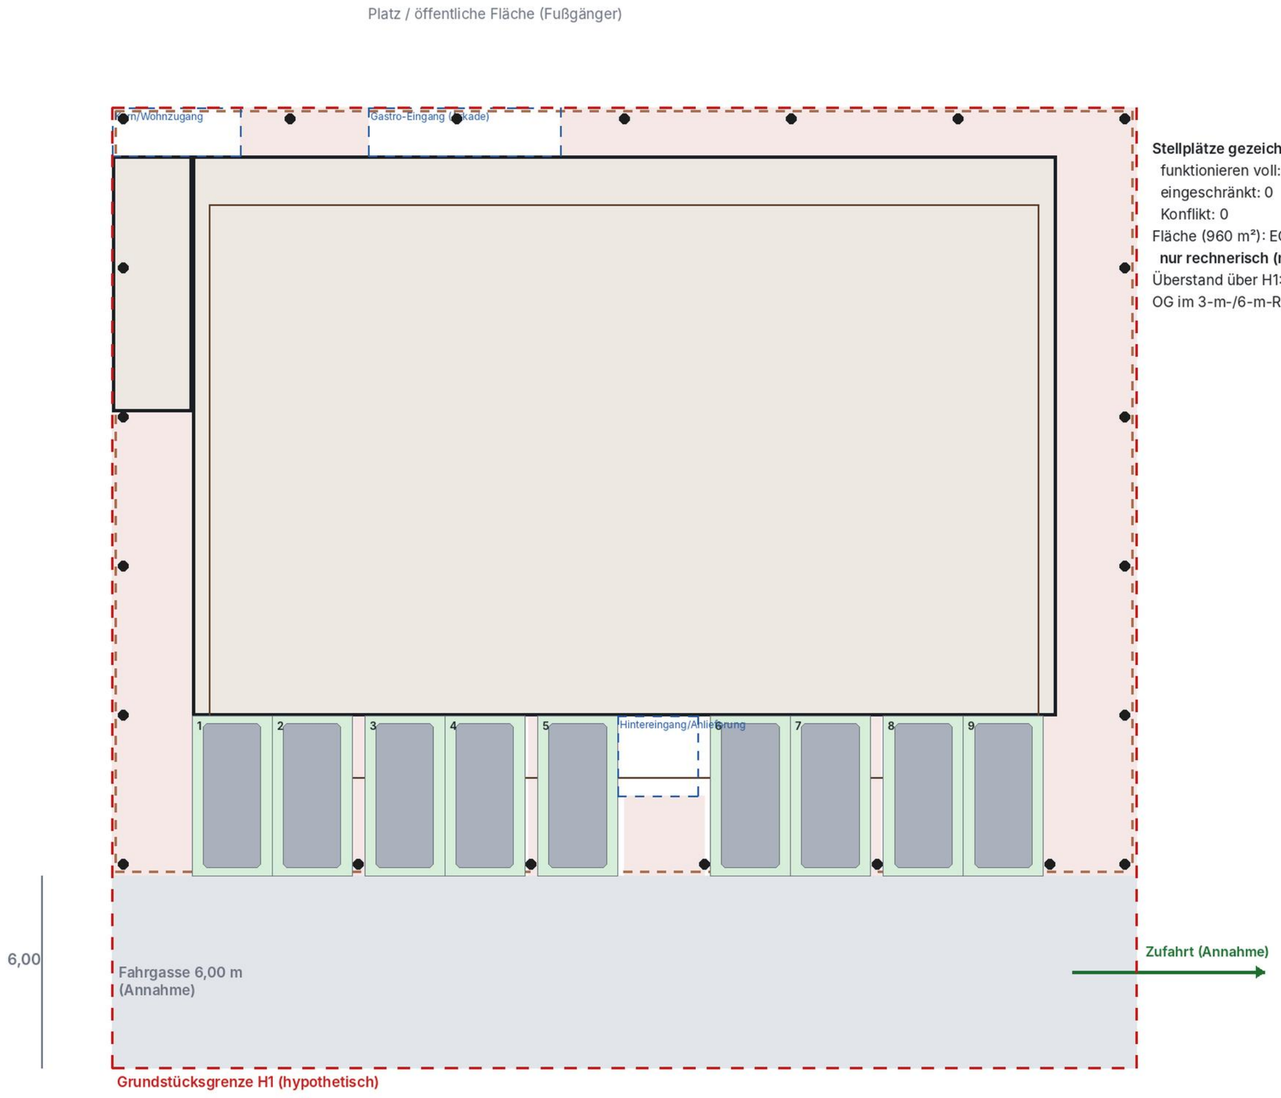

Stellplätze gezeichnet: 9
funktionieren voll: 9
eingeschränkt: 0
Konflikt: 0
Fläche (960 m²): EG 492 · Stellpl. 112 · Fahrgasse 192 · Zugänge 21
nur rechnerisch (nicht nutzbar): 142 m²
Überstand über H1: 0.00 m
OG im 3-m-/6-m-Randstreifen: 222 / 408 m²

Stellplatzprüfung	
Gezeichnet	9
funktionieren voll	9
eingeschränkt	0
Konflikt	0
Min. Nutzbreite 90°	2.50 m
Fahrgasse	6.0 m (frei)
Flächenbilanz 960 m²	
Erdgeschoss	492,5 m²
Stellplätze	112,5 m²
Fahrgasse	192,0 m²
Zugangszonen	21,2 m²
nur rechnerisch	141,8 m²

- Geometrische Prüfung ohne Schleppkurven; 90°-Stellplätze 2,50 × 5,00 m und Fahrgasse 6,00 m sind Planungsannahmen
- Zufahrt (Lage der Straße) ist Annahme
- Feuerwehrzufahrt/Aufstellflächen unter dem Vorbau nicht nachgewiesen (Prüfbedarf)

Stellplatz funktioniert · eingeschränkt · Konflikt · Fahrgasse · nur rechnerisch verbleibend

braun gestrichelt: 1./2. OG über dem EG (Vorbau) · blau gestrichelt: Eingangszonen


E3: Grundrisse EG, 1. OG, 2. OG

E3 – Staffel 3,00 m zurück · schematisch

VARIANTE E · NICHT FESTGELEGT

Erdgeschoss


E3: Erdgeschoss (schematisch)
Grundriss schematisch · Wohnungsaufteilung = Streifenmodell (Mittelgang 2,0 m), netto = 0,88 × brutto · Säulen Ø 0,40 m · Grundstück H1 hypothetisch

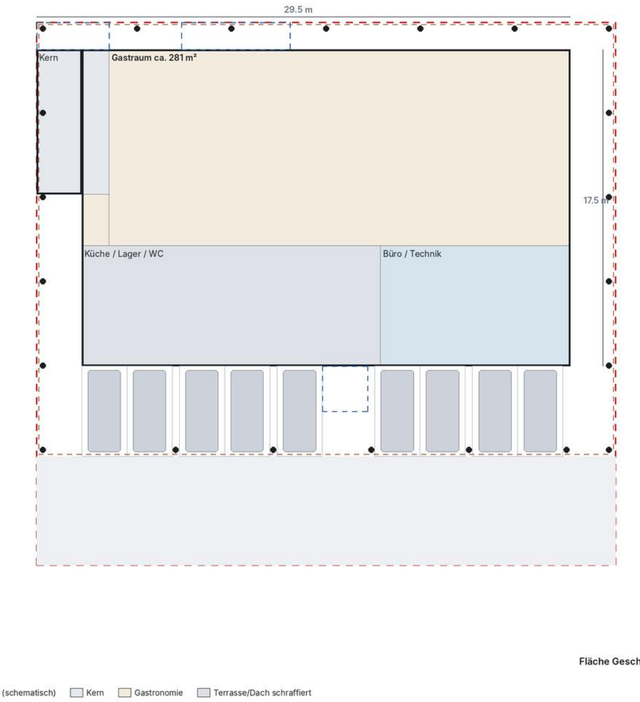

Fläche Geschoss 492 m²

1. Obergeschoss


E3: 1. Obergeschoss (schematisch)
Grundriss schematisch · Wohnungsaufteilung = Streifenmodell (Mittelgang 2,0 m), netto = 0,88 × brutto · Säulen Ø 0,40 m · Grundstück H1 hypothetisch

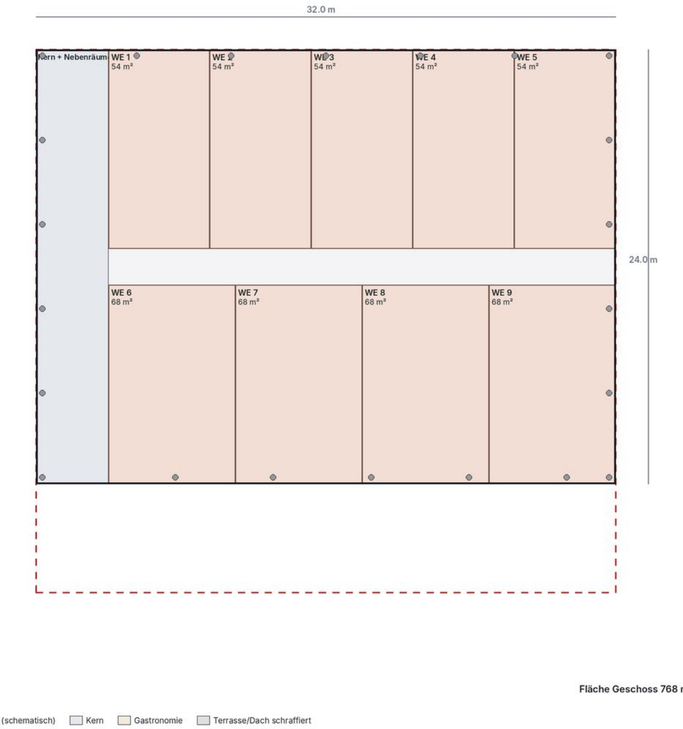

Fläche Geschoss 768 m²

2. Obergeschoss

E3: 2. Obergeschoss (Staffel) (schematisch)
Grundriss schematisch · Wohnungsaufteilung = Streifenmodell (Mittelgang 2,0 m), netto = 0,88 × brutto · Säulen Ø 0,40 m · Grundstück H1 hypothetisch

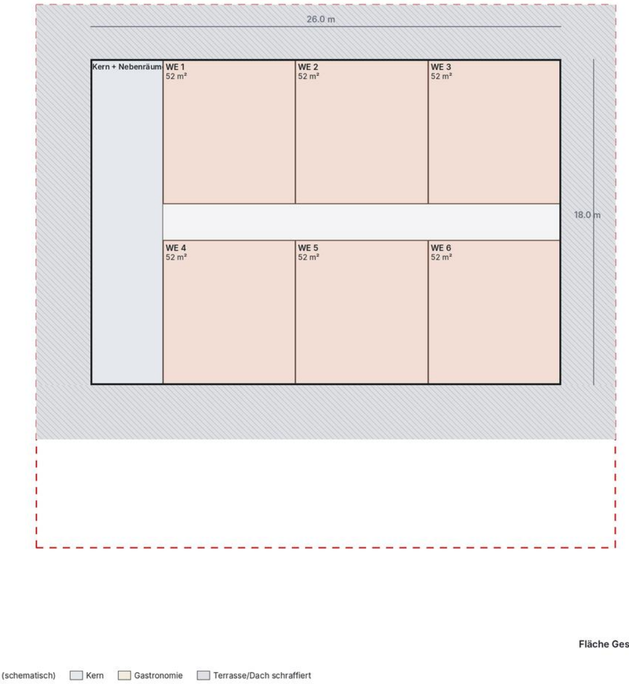

Fläche Geschoss 468 m²

Wohnung (schematisch) · Kern · Gastronomie · Terrasse/Dach schraffiert

E3: vier Fassaden


VARIANTE E · NICHT FESTGELEGT

E3 – Staffel 3,00 m zurück · orthogonale Ansichten aus dem 3D-Modell

Vorderfassade (Platzseite)



Rückfassade

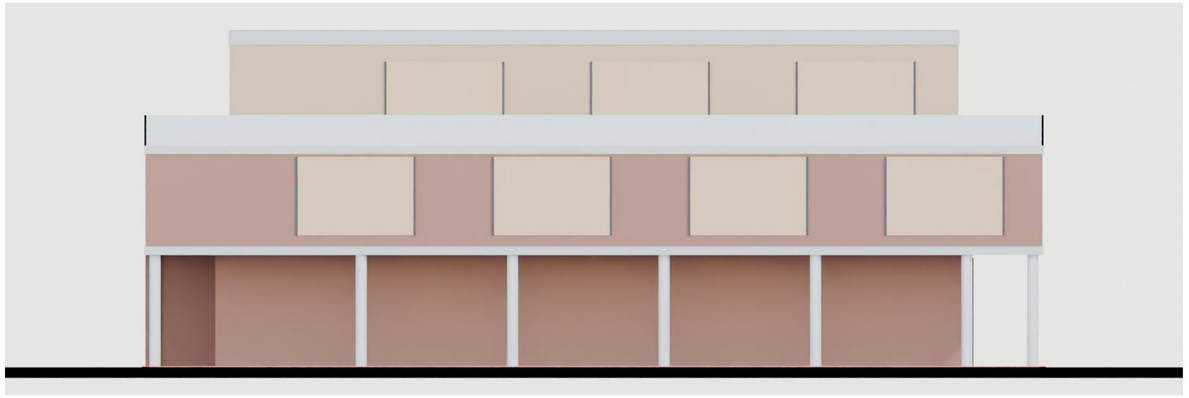

Seitenfassade West



Seitenfassade Ost




E3: Gebäudeschnitt mit Geschosshöhen und 3D-Ansichten

E3 – Staffel 3,00 m zurück


VARIANTE E · NICHT FESTGELEGT


E3: Gebäudeschnitt mit Geschosshöhen (schematisch)

Platzseite links, Rückseite rechts · Schnitt bei x = 16.25 m · Höhenbezug ±0,00 = OK Fertigfußboden EG (Planbezug Blatt 14) – Bezugspunkt der Stadt für die 12,00 m ist NICHT belegt

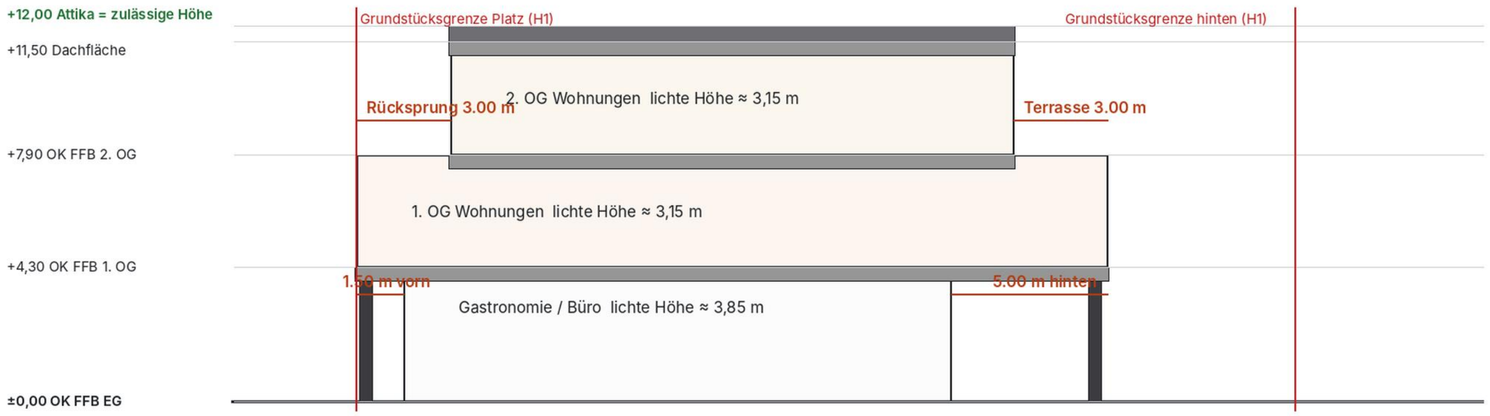

Geschosshöhen: EG 4,30 m · 1. OG 3,60 m · 2. OG 3,60 m · Dach/Attika 0,50 m = 12,00 m. Reserve 0,00 m. Die 12,00 m gelten erst als eingehalten, wenn der baurechtliche Höhenbezug geklärt ist.
Säulen im Schnittbereich: 2 · Säulen insgesamt: 22 · Vorbau-Unterkante +4,00 m (Decke 0,30 m)

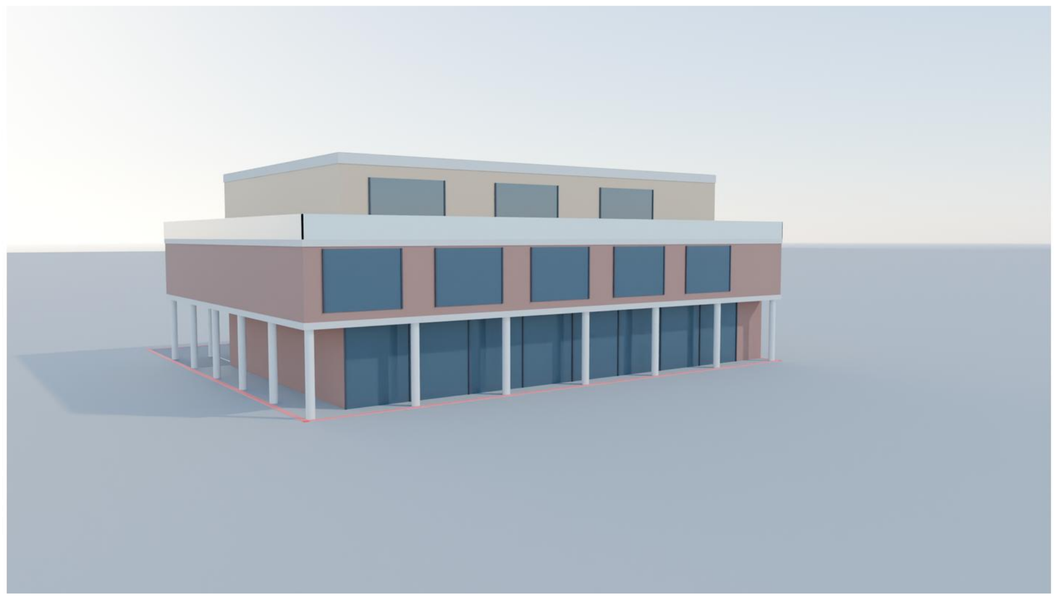


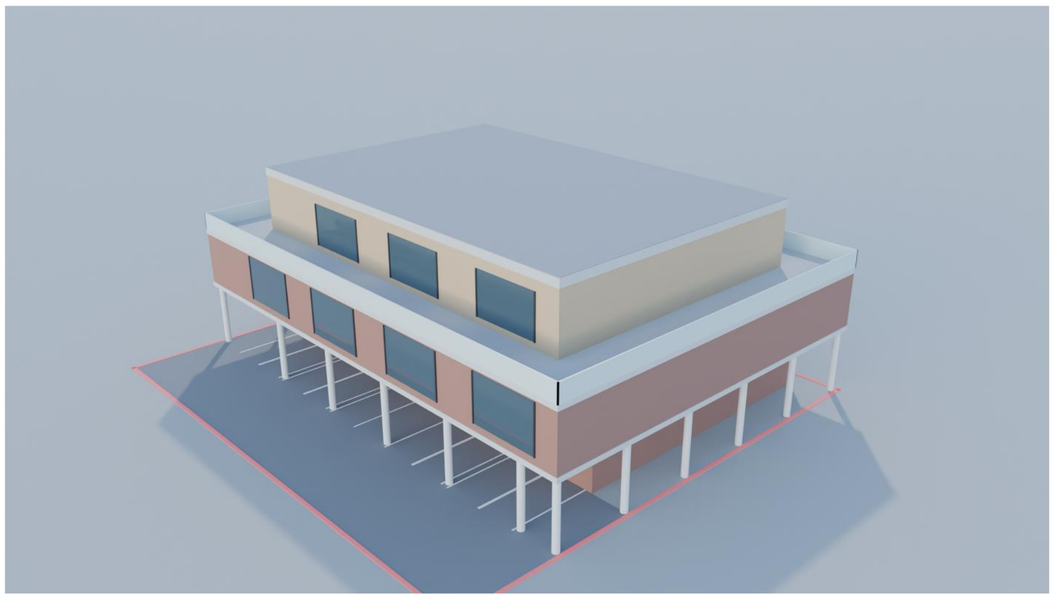

E4 – zweireihiges Parken, kleineres EG

Entwurfsstudie Baufeld 3 · Konzeptvariante, keine Genehmigungsplanung

VARIANTE E · NICHT FESTGELEGT

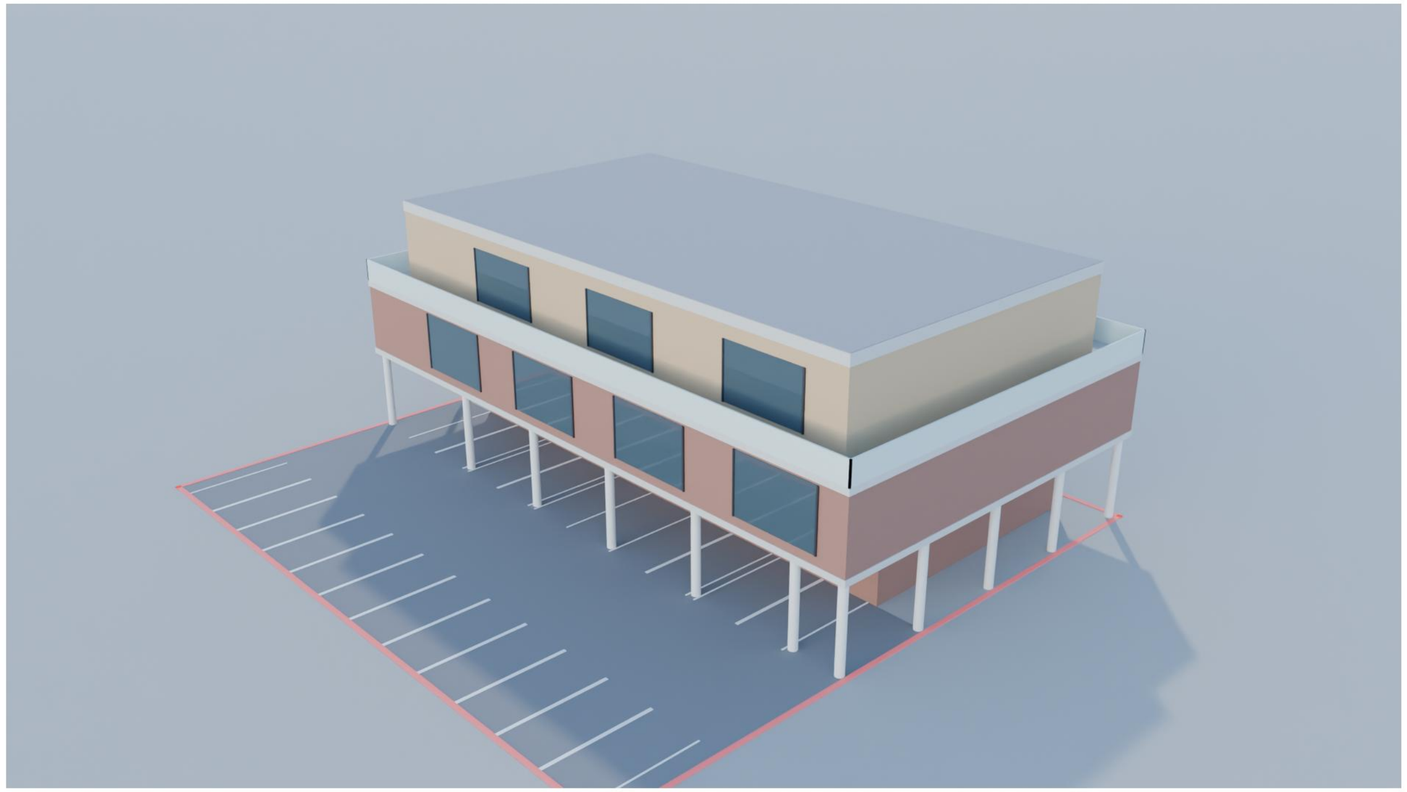

Wie E2, aber Erdgeschoss nur 14 m tief: zwei Stellplatzreihen (eine unter dem 5-m-Vorbau hinten, eine frei) mit 6-m-Fahrgasse dazwischen; dafür weniger Gewerbefläche.

Kennzahl	Wert (vorläufig)
Höhe	12,00 m Attika (EG 4,30 · 1. OG 3,60 · 2. OG 3,60 · Dach/Attika 0,50), 3 Geschosse – Höhenbezug offen
Grundfläche EG / 1. OG / 2. OG	358 / 608 / 464 m²
Außenmaße EG / 1. OG / 2. OG	29.5 × 12.5 / 32.0 × 19.0 / 29.0 × 16.0 m
Wohnfläche netto (geschätzt)	727 m²
Wohnungen Standardmix	16 WE (9 + 7), 38–52 m², Ø 45 m²
Gewerbe	EG 358 m²; Gastraum ca. 198 m² (≈ 85 Plätze), Terrasse/Arkade ≈ 28 Plätze, Büro 56 m²
Säulen	20 Säulen Ø 0,40 m; Paare 5,4 m (zwei Stellplätze + Säule)
Stellplätze gezeichnet	21: 21 voll nutzbar, 0 eingeschränkt, 0 Konflikt
Stellplätze erforderlich (§ 47 NBauO)	8,5–12,5, Mittel 10,1 (nur Gastro + Büro; Wohnen 0)
Stellplätze optional (Komfort/Markt)	Wohnen 0,5–1,5 je WE = 8–24; Komfortziel gesamt ≈ 26
Überstand über Grundstück H1	0,00 m

Alle Maße sind Planungsannahmen: Stellplatz 2,50 × 5,00 m, Fahrgasse 6,00 m, Säule Ø 0,40 m, Grundstück 32 × 30 m (Hypothese; die städtischen Unterlagen Seite 13/15/16 liegen nur als Beschreibung vor, nicht als Foto), Zufahrt = Annahme. Wohnfläche = 0,88 × Wohnstreifen, schematisch. Nichts ist genehmigt, bemessen oder abgestimmt.


E4: Lageplan mit Gebäude, Säulen, Zufahrt und Stellplätzen

VARIANTE E · NICHT FESTGELEGT

E4 – zweireihiges Parken, kleineres EG · grün = Stellplatz funktioniert, orange = eingeschränkt, rot = Konflikt, rosa = nur rechnerisch verbleibende Fläche

Lageplan E4 – Gebäude, Säulen, Zufahrt, Stellplätze

Grundstück H1 32 × 30 m HYPOTHETISCH (Zuschnitt/Baugrenzen nicht belegt) · Stellplatz 2,50 × 5,00 m, Fahrgasse 6,00 m = Planungsannahmen · Zufahrt = Annahme

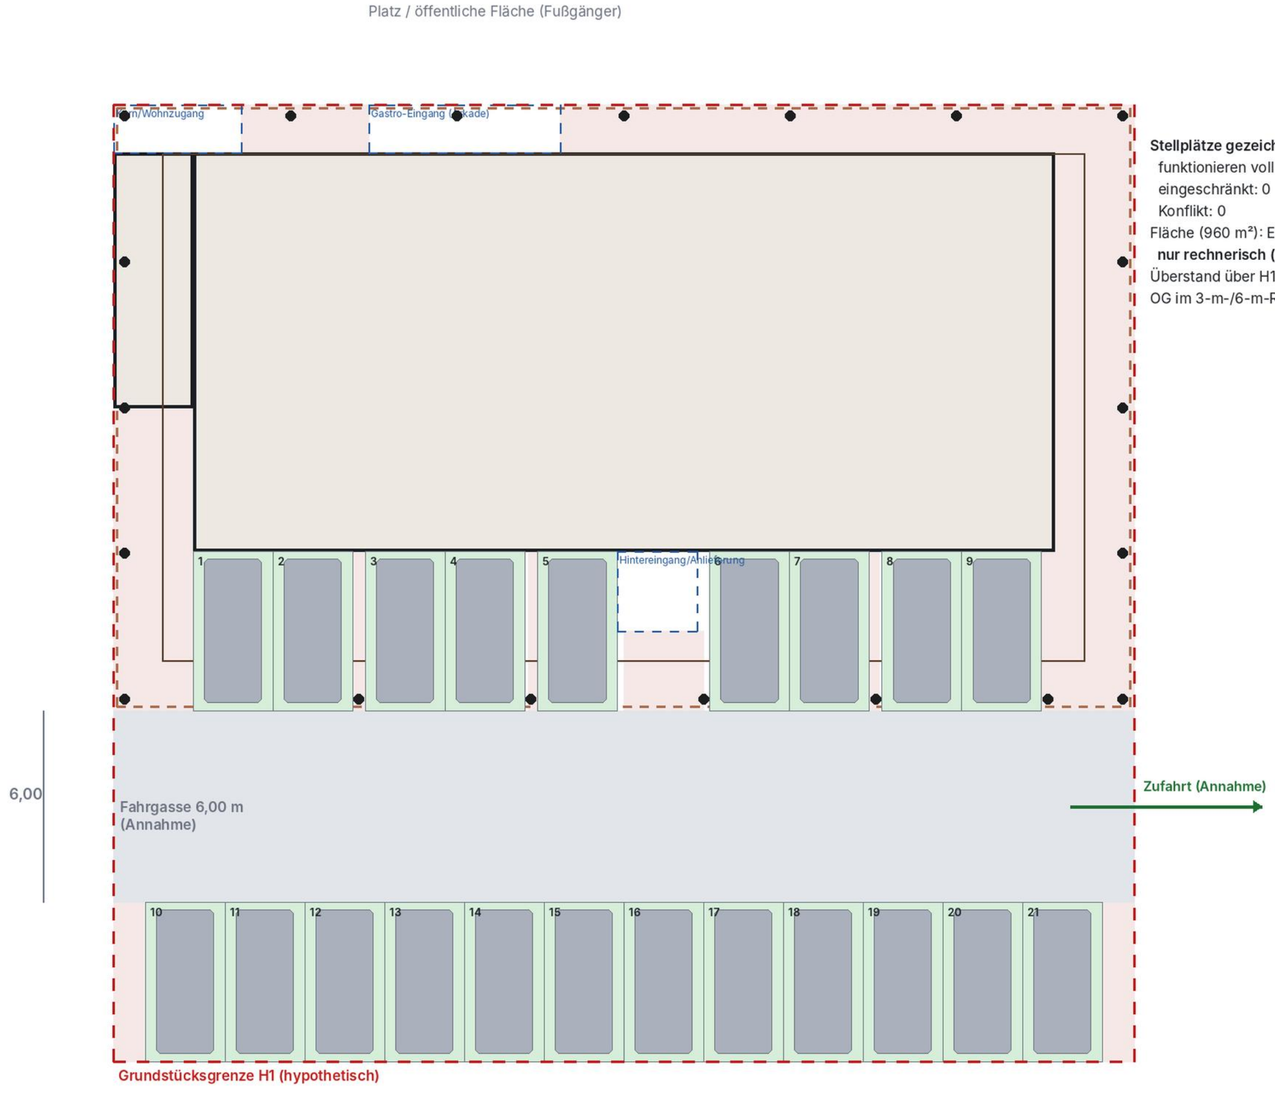

Stellplätze gezeichnet: 21
funktionieren voll: 21
eingeschränkt: 0
Konflikt: 0
Fläche (960 m²): EG 358 · Stellpl. 262 · Fahrgasse 192 · Zugänge 21
nur rechnerisch (nicht nutzbar): 127 m²
Überstand über H1: 0.00 m
OG im 3-m-/6-m-Randstreifen: 192 / 348 m²

Stellplatzprüfung	
Gezeichnet	21
funktionieren voll	21
eingeschränkt	0
Konflikt	0
Min. Nutzbreite 90°	2.50 m
Fahrgasse	6.0 m (frei)
Flächenbilanz 960 m²	
Erdgeschoss	357,5 m²
Stellplätze	262,5 m²
Fahrgasse	192,0 m²
Zugangszonen	21,2 m²
nur rechnerisch	126,8 m²

- Geometrische Prüfung ohne Schleppkurven; 90°-Stellplätze 2,50 × 5,00 m und Fahrgasse 6,00 m sind Planungsannahmen
- Zufahrt (Lage der Straße) ist Annahme
- Feuerwehrzufahrt/Aufstellflächen unter dem Vorbau nicht nachgewiesen (Prüfbedarf)

Stellplatz funktioniert · eingeschränkt · Konflikt · Fahrgasse · nur rechnerisch verbleibend

braun gestrichelt: 1./2. OG über dem EG (Vorbau) · blau gestrichelt: Eingangszonen


E4: Grundrisse EG, 1. OG, 2. OG

E4 – zweireihiges Parken, kleineres EG · schematisch

VARIANTE E · NICHT FESTGELEGT

Erdgeschoss

E4: Erdgeschoss (schematisch)
Grundriss schematisch · Wohnungsaufteilung = Streifenmodell (Mittelgang 2,0 m), netto = 0,88 × brutto · Säulen Ø 0,40 m · Grundstück H1 hypothetisch

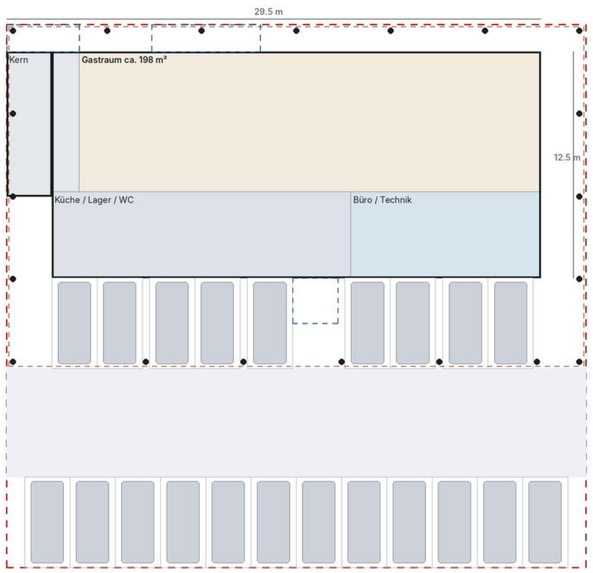


Fläche Geschoss 358 m²

Wohnung (schematisch) Kern Gastronomie Terrasse/Dach schraffiert

1. Obergeschoss

E4: 1. Obergeschoss (schematisch)
Grundriss schematisch · Wohnungsaufteilung = Streifenmodell (Mittelgang 2,0 m), netto = 0,88 × brutto · Säulen Ø 0,40 m · Grundstück H1 hypothetisch

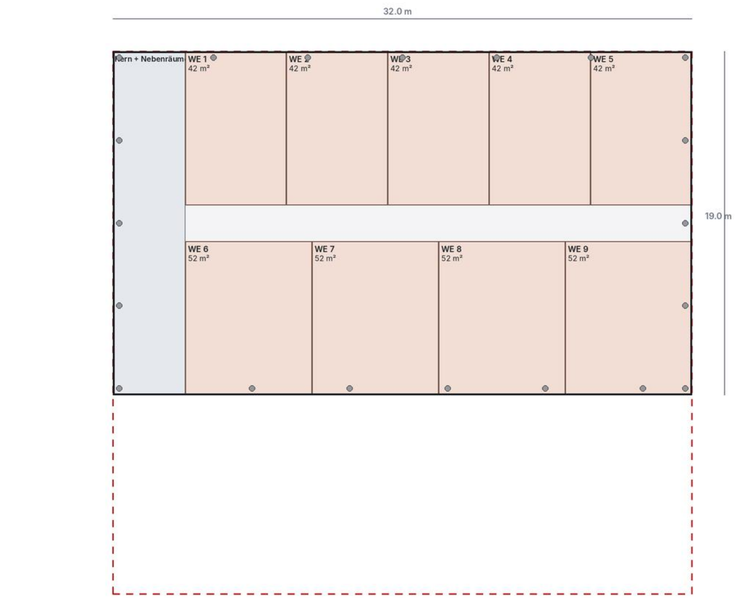


Fläche Geschoss 608 m²

Wohnung (schematisch) Kern Gastronomie Terrasse/Dach schraffiert

2. Obergeschoss

E4: 2. Obergeschoss (Staffel) (schematisch)
Grundriss schematisch · Wohnungsaufteilung = Streifenmodell (Mittelgang 2,0 m), netto = 0,88 × brutto · Säulen Ø 0,40 m · Grundstück H1 hypothetisch

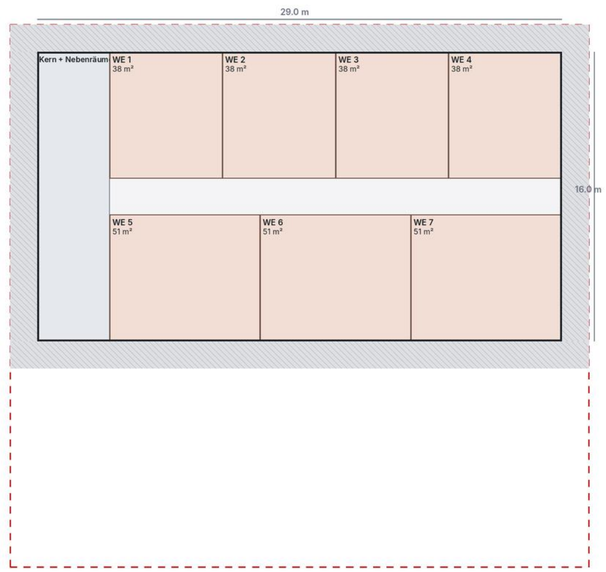

Fläche Geschoss 464 m²

Wohnung (schematisch) Kern Gastronomie Terrasse/Dach schraffiert

E4: vier Fassaden


VARIANTE E · NICHT FESTGELEGT

E4 – zweireihiges Parken, kleineres EG · orthogonale Ansichten aus dem 3D-Modell

Vorderfassade (Platzseite)



Rückfassade

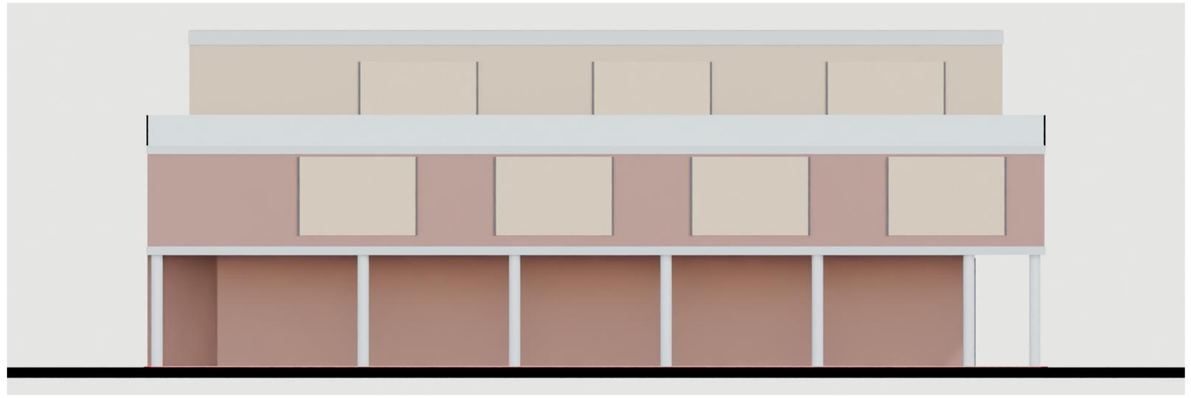

Seitenfassade West



Seitenfassade Ost




E4: Gebäudeschnitt mit Geschosshöhen und 3D-Ansichten

E4 – zweireihiges Parken, kleineres EG


VARIANTE E · NICHT FESTGELEGT


E4: Gebäudeschnitt mit Geschosshöhen (schematisch)

Platzseite links, Rückseite rechts · Schnitt bei x = 16.25 m · Höhenbezug ±0,00 = OK Fertigfußboden EG (Planbezug Blatt 14) – Bezugspunkt der Stadt für die 12,00 m ist NICHT belegt

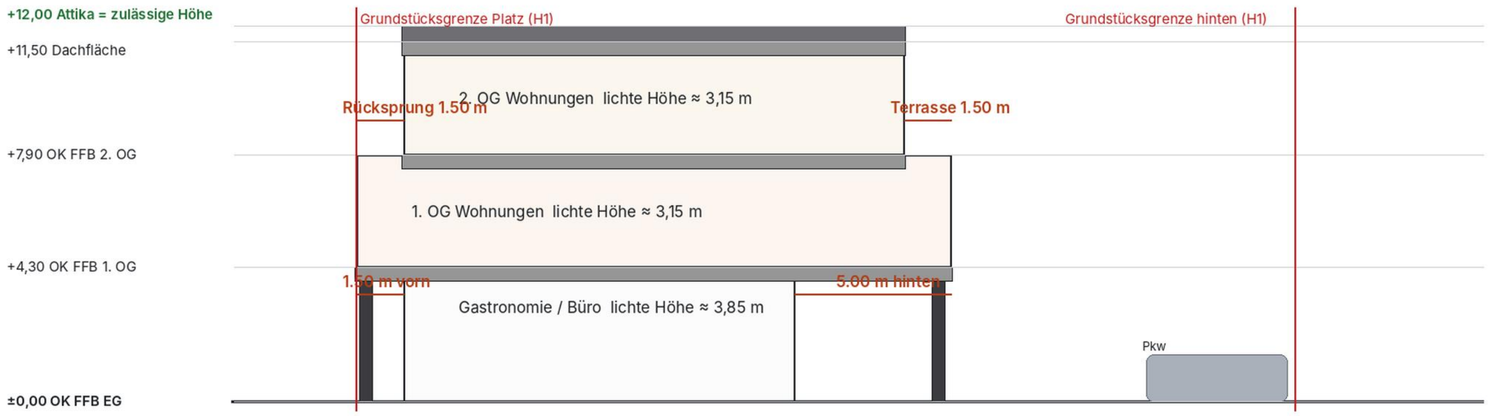

Geschosshöhen: EG 4,30 m · 1. OG 3,60 m · 2. OG 3,60 m · Dach/Attika 0,50 m = 12,00 m. Reserve 0,00 m. Die 12,00 m gelten erst als eingehalten, wenn der baurechtliche Höhenbezug geklärt ist.
Säulen im Schnittbereich: 2 · Säulen insgesamt: 20 · Vorbau-Unterkante +4,00 m (Decke 0,30 m)

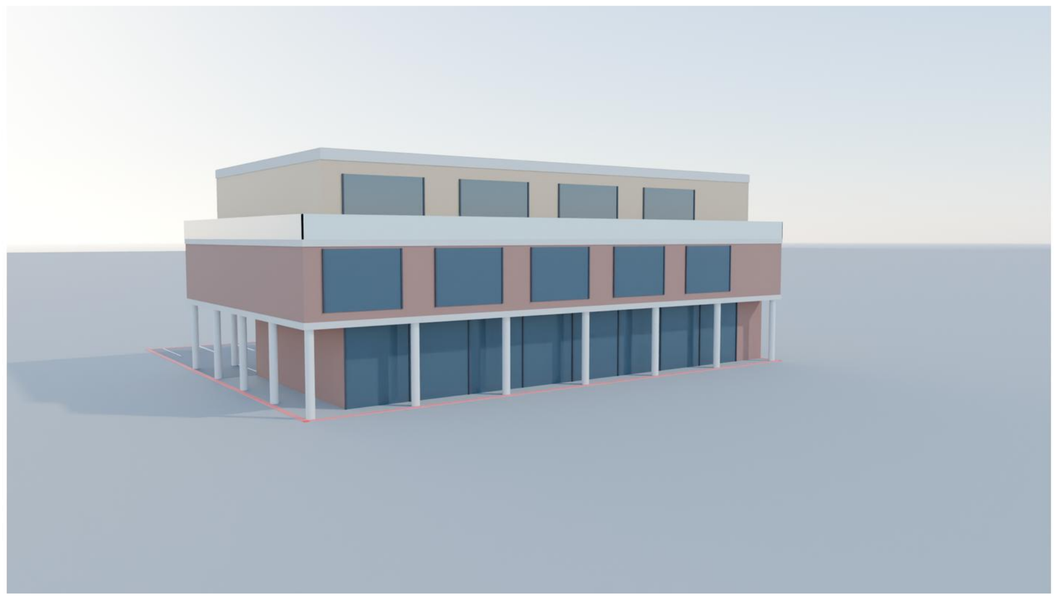

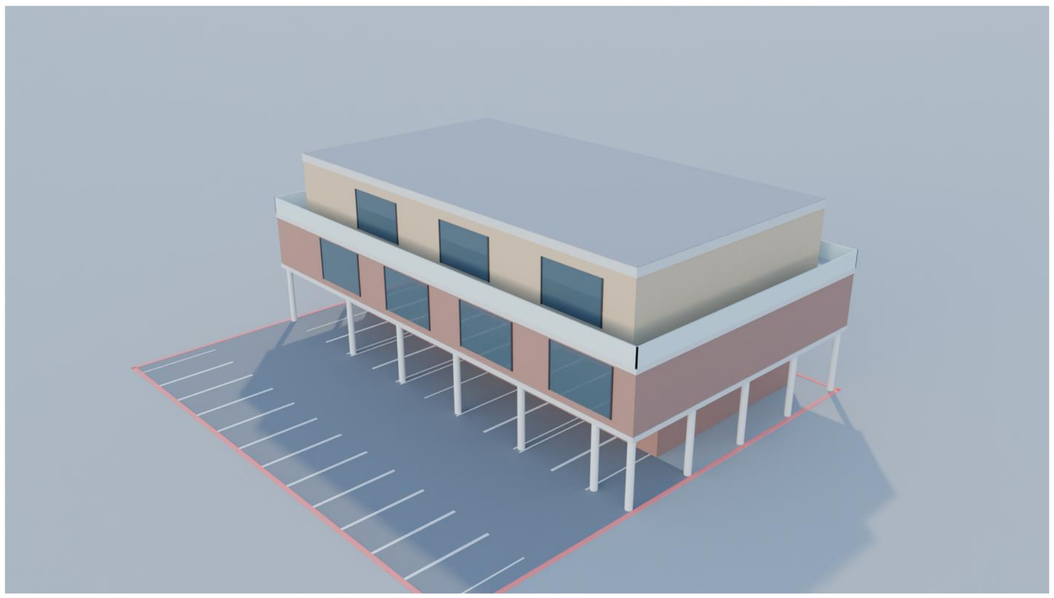

Baurechtliche Ampel (vorläufig)

VARIANTE E · NICHT FESTGELEGT

Keine Rechtsprüfung · bis zur Klärung von Grundstück, Baugrenzen und Satzungen offen

Kriterium	E1	E2	E3	E4
Gebäudehöhe / Traufe	kritisch / offen: Attika +12,00 m über FFB, Wandhöhe ≈ +11,50 m. Plan A (rechtskräftig 2023, MI 3): H 15,00 m ok, aber TH 9,80 m überschritten. Plan B (Entwurf 2026, nicht einschlägig): H 12,00 m über OK Fahrbahn (FFB max. +0,30 m → Baukörper max. +11,70 m über FFB), TH 6,50 m überschritten. Fahrbahnhöhe unbekannt.	kritisch / offen: Attika +12,00 m über FFB, Wandhöhe ≈ +11,50 m. Plan A (rechtskräftig 2023, MI 3): H 15,00 m ok, aber TH 9,80 m überschritten. Plan B (Entwurf 2026, nicht einschlägig): H 12,00 m über OK Fahrbahn (FFB max. +0,30 m → Baukörper max. +11,70 m über FFB), TH 6,50 m überschritten. Fahrbahnhöhe unbekannt.	kritisch / offen: Attika +12,00 m über FFB, Wandhöhe ≈ +11,50 m. Plan A (rechtskräftig 2023, MI 3): H 15,00 m ok, aber TH 9,80 m überschritten. Plan B (Entwurf 2026, nicht einschlägig): H 12,00 m über OK Fahrbahn (FFB max. +0,30 m → Baukörper max. +11,70 m über FFB), TH 6,50 m überschritten. Fahrbahnhöhe unbekannt.	kritisch / offen: Attika +12,00 m über FFB, Wandhöhe ≈ +11,50 m. Plan A (rechtskräftig 2023, MI 3): H 15,00 m ok, aber TH 9,80 m überschritten. Plan B (Entwurf 2026, nicht einschlägig): H 12,00 m über OK Fahrbahn (FFB max. +0,30 m → Baukörper max. +11,70 m über FFB), TH 6,50 m überschritten. Fahrbahnhöhe unbekannt.
Geschosse / Dach	kritisch / offen: Plan A: II–III, drei Geschosse zulässig; Plan B: II zwingend (×). Beide Pläne: Hauptdach geneigt ≥ 38°, Flachdach nur untergeordnet → alle Flachdach-Entwürfe benötigen Befreiung; 2. OG = 100 % des 1. OG.	kritisch / offen: Plan A: II–III, drei Geschosse zulässig; Plan B: II zwingend (×). Beide Pläne: Hauptdach geneigt ≥ 38°, Flachdach nur untergeordnet → alle Flachdach-Entwürfe benötigen Befreiung; 2. OG = 79 % des 1. OG.	kritisch / offen: Plan A: II–III, drei Geschosse zulässig; Plan B: II zwingend (×). Beide Pläne: Hauptdach geneigt ≥ 38°, Flachdach nur untergeordnet → alle Flachdach-Entwürfe benötigen Befreiung; 2. OG = 61 % des 1. OG.	kritisch / offen: Plan A: II–III, drei Geschosse zulässig; Plan B: II zwingend (×). Beide Pläne: Hauptdach geneigt ≥ 38°, Flachdach nur untergeordnet → alle Flachdach-Entwürfe benötigen Befreiung; 2. OG = 76 % des 1. OG.
GRZ / Überdeckung	zu prüfen: größte Geschossprojektion 768 m² = 80 % von 960 m² (GRZ 0,6 = 576 m² nur Annahme).	zu prüfen: größte Geschossprojektion 768 m² = 80 % von 960 m² (GRZ 0,6 = 576 m² nur Annahme).	zu prüfen: größte Geschossprojektion 768 m² = 80 % von 960 m² (GRZ 0,6 = 576 m² nur Annahme).	zu prüfen: größte Geschossprojektion 608 m² = 63 % von 960 m² (GRZ 0,6 = 576 m² nur Annahme).
Grenzen / Baugrenzen	kritisch / offen: Baufenster MI 3 (P23) ≈ 27,7 × 15,9 m (abgeleitet), Baugrenzen 10,0 m West / 3 m übrige Seiten; EG-Fußabdruck und Vorbau über die Baugrenze passen nicht (siehe Entscheidungs-PDF).	kritisch / offen: Baufenster MI 3 (P23) ≈ 27,7 × 15,9 m (abgeleitet), Baugrenzen 10,0 m West / 3 m übrige Seiten; EG-Fußabdruck und Vorbau über die Baugrenze passen nicht (siehe Entscheidungs-PDF).	kritisch / offen: Baufenster MI 3 (P23) ≈ 27,7 × 15,9 m (abgeleitet), Baugrenzen 10,0 m West / 3 m übrige Seiten; EG-Fußabdruck und Vorbau über die Baugrenze passen nicht (siehe Entscheidungs-PDF).	kritisch / offen: Baufenster MI 3 (P23) ≈ 27,7 × 15,9 m (abgeleitet), Baugrenzen 10,0 m West / 3 m übrige Seiten; EG-Fußabdruck und Vorbau über die Baugrenze passen nicht (siehe Entscheidungs-PDF).
Stellplätze (gesetzlich)	kritisch / offen: 9 nutzbar < erforderlich Mittel 13,6 (11,4–16,9): Ablöse/Mitbenutzung nötig	kritisch / offen: 9 nutzbar < erforderlich Mittel 13,6 (11,4–16,9): Ablöse/Mitbenutzung nötig	kritisch / offen: 9 nutzbar < erforderlich Mittel 13,6 (11,4–16,9): Ablöse/Mitbenutzung nötig	voraussichtlich ok: 21 nutzbar ≥ erforderlich bis 12,5
Gewerbe im EG	zu prüfen: EG 492 m² (B3: 576 m²); Gastraum ca. 281 m².	zu prüfen: EG 492 m² (B3: 576 m²); Gastraum ca. 281 m².	zu prüfen: EG 492 m² (B3: 576 m²); Gastraum ca. 281 m².	zu prüfen: EG 358 m² (B3: 576 m²); Gastraum ca. 198 m².
Brandschutz / Feuerwehr	zu prüfen: Vorbau über Stellplätzen/Fahrgasse, Aufstellflächen und Feuerwehrzufahrt, Rettungswege – Konzept erforderlich.	zu prüfen: Vorbau über Stellplätzen/Fahrgasse, Aufstellflächen und Feuerwehrzufahrt, Rettungswege – Konzept erforderlich.	zu prüfen: Vorbau über Stellplätzen/Fahrgasse, Aufstellflächen und Feuerwehrzufahrt, Rettungswege – Konzept erforderlich.	zu prüfen: Vorbau über Stellplätzen/Fahrgasse, Aufstellflächen und Feuerwehrzufahrt, Rettungswege – Konzept erforderlich.

Offene Fragen und Prüfbedarf

VARIANTE E · NICHT FESTGELEGT

Vor jeder Weiterentwicklung zu klären

• Fotos der städtischen Unterlagen (S. 13, 15, 16) in den Projektordner; daraus Grundstückszuschnitt, Baugrenzen, GRZ, Höhenbezugspunkt, Traufhöhe, Dachform, Abstände, Festsetzungen zu Stellplätzen/Zufahrten.
• Bebauungsplan-Stand: Entwurf (S. 15) – rechtskräftige Fassung; örtliche Bauvorschrift/Stellplatzsatzung für Nicht-Wohnungen; städtebaulicher Vertrag/Kaufvertrag (Stellplätze auch für Wohnungen möglich).
• Einstufung der Gaststätte („örtliche“ oder „überörtliche Bedeutung“), Sitzplatzzahl innen/außen, Büro mit/ohne Besucherverkehr.
• Höhenbezug der 12,00 m; Vollgeschoss-Definition für das 2. OG; Traufhöhe 6,50 m.
• Überbauung des Platzes (F1–F3: 1,5 m), Grenz- und Abstandsflächen, GRZ-Anrechnung überdeckter Stellplätze.
• Zufahrt: Straße, Gefälle, Sichtdreiecke; Feuerwehrzufahrt/Aufstellflächen unter dem Vorbau; Wendemöglichkeit in der Sackgasse (F1–F3).
• Stellplatzmaße/Garagenverordnung für Stellplätze neben Säulen und Parallelparker; Schleppkurven.
• Statik: Kragarme 1,0–5,0 m, Säulenraster 5,4 m, Fundamente; Brandschutz Vorbau.

Keine Variante ist ausgewählt.