Neue Mitte Werlte – Baufeld 3 – Variante A – B3-Referenz (unverändert)

VORLÄUFIGER ENTWURF – NICHT GENEHMIGT – technische Zeichnungen für PDF-Import, keine Präsentation, keine Genehmigungsunterlage

Beschreibung

EG 32,00 × 18,00 m = 576 m² (Gastro EG, Büros rückseitig); 1. OG mit 3,00 m rückseitigem Anbau (ohne Stützen); Staffelgeschoss; fünf Balkone zum Platz; rückseitig teilweise überdeckte Stellplätze. Daten aus dem bestehenden B3-Modell (v4, Planstand Blatt 14), nicht neu gezeichnet.
Datenquelle: geometry/variant_B3.json (Alt. K), scripts/modell_b3.py v4

Maße und Kennwerte

EG-Außenmaß 32,00 × 18,00 m = 576,0 m²
1. Obergeschoss (OG1): Umriss 32,00 × 21,00 m, Fläche 660,0 m²
Staffelgeschoss: Umriss 30,40 × 17,90 m, Fläche 539,1 m²
Höhen über ±0,00: OK FFB 1. OG +3,50; OK FFB oberstes Geschoss +6,50; OK Dach +9,60; OK Attika +9,90 m
Höhenstatus: aus B3-Modell v4 (Planstand B14); Höhenbezug zur Stadt NOCH OFFEN
Decken: ANNAHME 0,30 m (B3: Unterseite überdeckte Stellplätze +3,20 bei OK 3,50)
Außenwand: Darstellung als Doppellinie 0,30 m = ANNAHME (Wandstärke NOCH OFFEN)
Säulen: keine (Referenz B3: Auskragung ohne Stützen)

Maßstab / Bezug

Alle Blätter 1:100 auf A2 quer. Maßstabsbalken unten: 10,00 m = 100 mm auf dem Blatt. Maße in Metern.
Grundrisse: x = West→Ost, y = von der Platzseite (unten) zur Rückseite (oben). Nordrichtung NOCH OFFEN.
Bezugshöhe ±0,00 = OK Fertigfußboden Erdgeschoss; Bezug zur OK Fahrbahn der Stadt NOCH OFFEN.

Blattverzeichnis

Blatt 1: Übersichtsblatt
Blatt 2: Grundriss Erdgeschoss (EG) – OK Fertigfußboden ±0,00 m (Höhenbezug ANNAHME)
Blatt 3: Grundriss 1. Obergeschoss (OG1) – OK Fertigfußboden +3,50 m (Höhenbezug ANNAHME)
Blatt 4: Grundriss Staffelgeschoss – OK Fertigfußboden +6,50 m (Höhenbezug ANNAHME)
Blatt 5: Vorderansicht
Blatt 6: Rückansicht
Blatt 7: Westansicht
Blatt 8: Ostansicht
Blatt 9: Schnitt A–A mit Höhenkoten
Blatt 10: Stellplätze / Erschließung (getrennt)
Blatt 11: Rechtsebenen und offene Punkte
Blatt 12: Konsistenzprotokoll
Blätter 1–10 sind Zeichnungen (Vektor); Blätter 11–12 sind reine Textblätter (für den Import-Test entbehrlich).

Raumliste (Koordinaten m, Status laut B3-Modell)

EG LOBBY-GF: Eingang/Lobby x 0,00–4,00, y 0,00–4,50 [ASSUMED]
EG STAIR-GF: Treppenhaus x 0,00–4,00, y 4,50–9,50 [ASSUMED]
EG LANDING-GF: Podest x 0,00–4,00, y 9,50–11,50 [ASSUMED]
EG LIFT-GF: Aufzug x 0,80–3,00, y 11,50–14,10 [ASSUMED]
EG TECH-GF: Technik x 3,00–4,00, y 11,50–14,10 [ASSUMED]
EG WAND-LIFT-GF: Wandscheibe x 0,00–0,80, y 11,50–14,10 [ASSUMED]
EG BUERO-WC-GF: WC (Büro) x 0,00–2,30, y 14,10–16,20 [ASSUMED]
EG BUERO-FOYER-GF: Foyer (Büro) x 2,30–4,00, y 14,10–16,20 [ASSUMED]
EG BUERO-FOYER2-GF: Foyer (Büro) x 0,00–4,00, y 16,20–18,00 [ASSUMED]
EG DINING-GF: Gastraum x 4,00–32,00, y 0,00–10,00 [PROVISIONAL]
EG BAR-GF: Bar x 5,00–15,00, y 8,60–10,00 [PROVISIONAL]
EG WC-GF: WC x 4,00–10,00, y 10,00–14,00 [PROVISIONAL]
EG PERSONAL-GF: Personal x 10,00–15,00, y 10,00–14,00 [PROVISIONAL]
EG FLUR-GF: Flur x 15,00–20,00, y 10,00–14,00 [PROVISIONAL]
EG KITCHEN-GF: Küche x 20,00–32,00, y 10,00–15,00 [PROVISIONAL]
EG STORE-GF: Lager x 20,00–29,00, y 15,00–18,00 [PROVISIONAL]
EG ANLIEF-GF: Anlieferung x 29,00–32,00, y 15,00–18,00 [HYPOTHETICAL]
EG OFFICE-1-GF: Büro x 4,00–12,00, y 14,00–18,00 [ASSUMED]
EG OFFICE-2-GF: Büro x 12,00–20,00, y 14,00–18,00 [ASSUMED]
OG1 STAIR-L1: Treppenhaus x 0,00–4,00, y 4,50–9,50 [ASSUMED]
OG1 LANDING-L1: Podest x 0,00–4,00, y 9,50–11,50 [ASSUMED]
OG1 LIFT-L1: Aufzug x 0,80–3,00, y 11,50–14,10 [ASSUMED]
OG1 TECH-L1: Technik x 3,00–4,00, y 11,50–14,10 [ASSUMED]
OG1 ABSTELL-L1: Abstell x 0,00–4,00, y 14,10–18,00 [ASSUMED]
OG1 VORRAUM-L1: Vorraum x 0,00–4,00, y 0,00–4,50 [ASSUMED]
OG1 WAND-LIFT-L1: Wandscheibe x 0,00–0,80, y 11,50–14,10 [ASSUMED]
OG1 WE-L1-V1: Wohnung x 4,00–9,60, y 0,00–9,50 [PROVISIONAL]
OG1 WE-L1-V2: Wohnung x 9,60–15,20, y 0,00–9,50 [PROVISIONAL]
OG1 WE-L1-V3: Wohnung x 15,20–20,80, y 0,00–9,50 [PROVISIONAL]
OG1 WE-L1-V4: Wohnung x 20,80–26,40, y 0,00–9,50 [PROVISIONAL]
OG1 WE-L1-V5: Wohnung x 26,40–32,00, y 0,00–9,50 [PROVISIONAL]
OG1 CORR-L1: Flur x 4,00–32,00, y 9,50–11,50 [PROVISIONAL]
OG1 WE-L1-H1: Wohnung x 4,00–11,00, y 11,50–21,00 [PROVISIONAL]
OG1 WE-L1-H2: Wohnung x 11,00–18,00, y 11,50–21,00 [PROVISIONAL]
OG1 WE-L1-H3: Wohnung x 18,00–25,00, y 11,50–21,00 [PROVISIONAL]
OG1 WE-L1-H4: Wohnung x 25,00–32,00, y 11,50–21,00 [PROVISIONAL]
ST STAIR-L2: Treppenhaus x 0,80–4,20, y 4,50–9,50 [ASSUMED]
ST LANDING-L2: Podest x 0,80–4,20, y 9,50–11,50 [ASSUMED]
ST LIFT-L2: Aufzug x 0,80–3,00, y 11,50–14,10 [ASSUMED]
ST TECH-L2: Technik x 3,00–4,20, y 11,50–14,10 [ASSUMED]
ST ABSTELL-L2: Abstell x 0,80–4,20, y 14,10–17,20 [ASSUMED]
ST VORRAUM-L2: Vorraum x 0,80–4,20, y 0,80–4,50 [ASSUMED]
ST WE-L2-V1: Wohnung x 4,20–10,95, y 0,80–9,50 [PROVISIONAL]
ST WE-L2-V2: Wohnung x 10,95–17,70, y 0,80–9,50 [PROVISIONAL]
ST WE-L2-V3: Wohnung x 17,70–24,45, y 0,80–9,50 [PROVISIONAL]
ST WE-L2-V4: Wohnung x 24,45–31,20, y 0,80–9,50 [PROVISIONAL]
ST CORR-L2: Flur x 4,20–31,20, y 9,50–11,50 [PROVISIONAL]
ST WE-L2-H1: Wohnung x 4,20–13,20, y 11,50–18,70 [PROVISIONAL]
ST WE-L2-H2: Wohnung x 13,20–22,20, y 11,50–18,70 [PROVISIONAL]
ST WE-L2-H3: Wohnung x 22,20–31,20, y 11,50–18,70 [PROVISIONAL]

Konsistenz (Kurzfassung)

[KONFLIKT] Balkon: 5 Bauteil(e) ragen über die Hypothese-Grenze zum Platz (y < 0) bis y = -1,50 m – Grenze/Baulinie NOCH OFFEN
[KONFLIKT] Vordach: 1 Bauteil(e) ragen über die Hypothese-Grenze zum Platz (y < 0) bis y = -3,60 m – Grenze/Baulinie NOCH OFFEN
Vollständiges Protokoll: letztes Blatt.

Legende (Linienarten)

- Außenwand (Doppellinie, grau gefüllt)
- Raumgrenze (dünn, grau)
- Säule Ø 0,40 m (voll)
- Fenster/Verglasung (3 Linien in der Wand)
- Tür (Linie in der Wandöffnung, ohne Anschlag)
- Maßlinie mit Schrägstrich (blau)
- Umriss darunterliegendes Geschoss / überdeckend
- Schnittlinie A–A
- Grundstücksgrenze HYPOTHESE (rot gestrichelt)
- Geschnittenes Bauteil (Schnitt, schwarz)

0 m — 5 m — 10 m
Maßstabsbalken 1:100 (10 m = 100 mm Blattmaß)

PROJEKT
Neue Mitte Werlte – Baufeld 3

VARIANTE
Variante A – B3-Referenz (unverändert)

ZEICHNUNG
Übersichtsblatt

MASSSTAB
1:100 (Blattgröße A2 quer)

DATUM
27.10.2026

BLATT
1 / 12 – Übersichtsblatt

HÖHEN
aus B3-Modell v4 (Planstand B14); Höhenbezug zur Stadt NOCH OFFEN

STATUS
VORLÄUFIGER ENTWURF – NICHT GENEHMIGT

ANMERKUNGEN
Maße in m.
Höhen: aus B3-Modell v4 (Planstand B14); Höhenbezug zur Stadt NOCH OFFEN

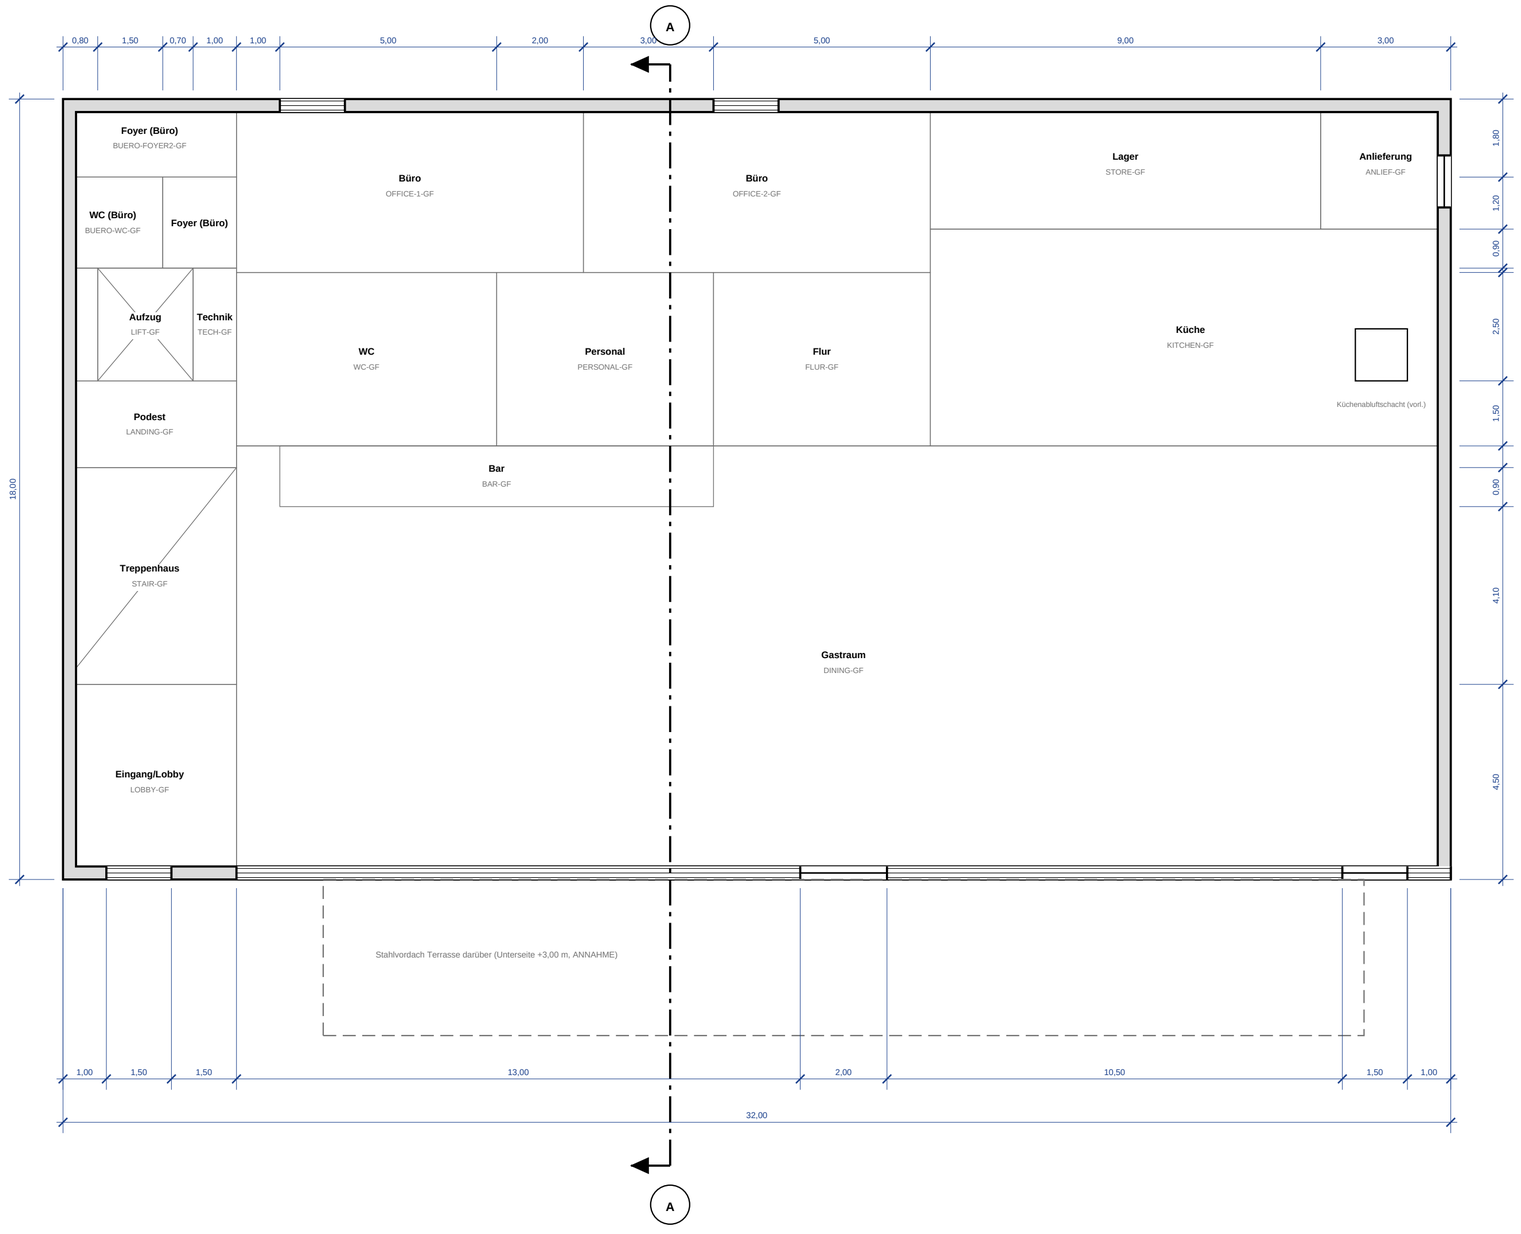

PROJEKT
Neue Mitte Werlte – Baufeld 3

VARIANTE
Variante A – B3-Referenz (unverändert)

ZEICHNUNG
Grundriss Erdgeschoss (EG) – OK Fertigfußboden ±0,00 m (Höhenbezug ANNAHME)

MASSSTAB
1:100 (Blattgröße A2 quer)

DATUM
27.10.2026

BLATT
2 / 12 – Grundriss Erdgeschoss (EG) – OK Fertigfußboden ±0,00 m (Höhenbezug ANNAHME)

HÖHEN
aus B3-Modell v4 (Planstand B14); Höhenbezug zur Stadt NOCH OFFEN

STATUS
VORLÄUFIGER ENTWURF – NICHT GENEHMIGT

ANMERKUNGEN
Wandstärke 0,30 m = ANNAHME (Darstellung).

Innentüren und Türanschläge NOCH OFFEN – nicht gezeichnet.

Maße in m. Maßketten blau, Bauteilkanten schwarz.

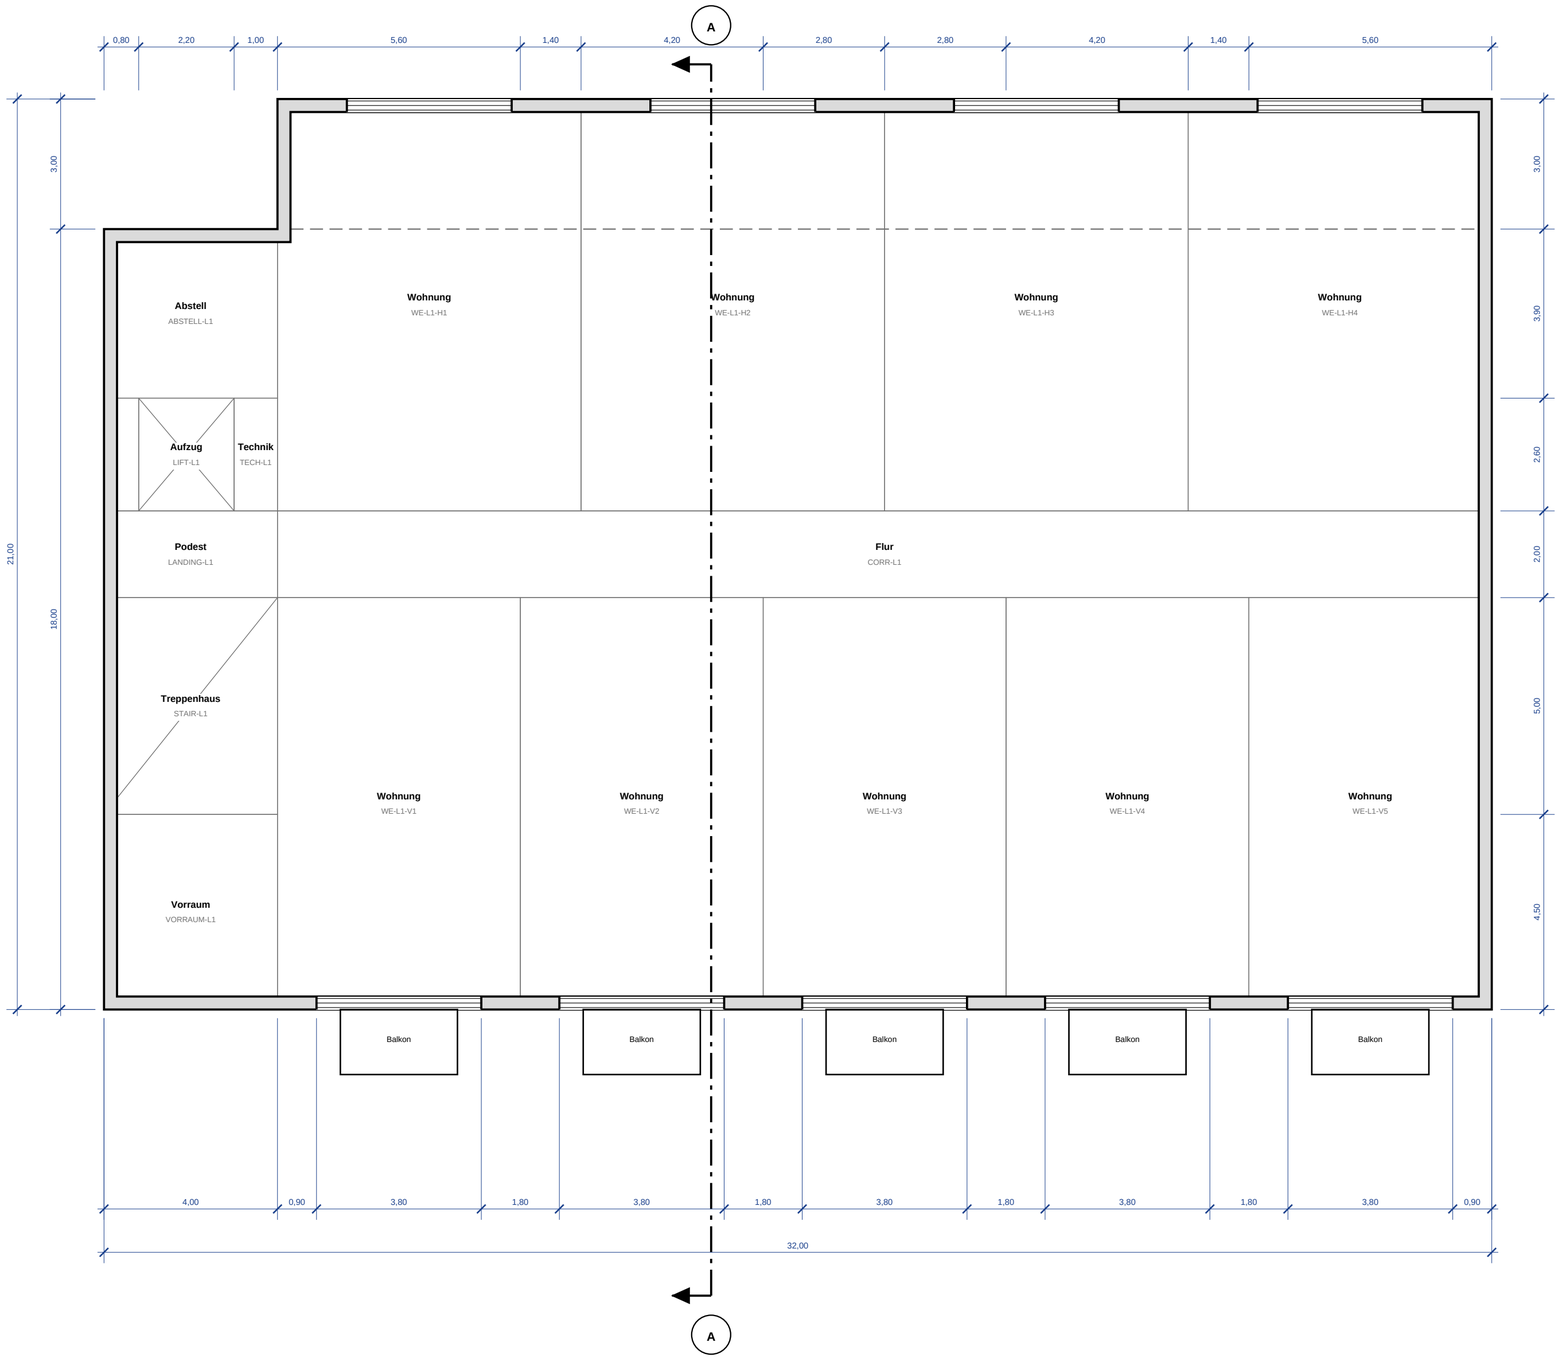

PROJEKT

Neue Mitte Werlte – Baufeld 3

VARIANTE

Variante A – B3-Referenz (unverändert)

ZEICHNUNG

Grundriss 1. Obergeschoss (OG1) – OK Fertigfußboden +3,50 m (Höhenbezug ANNAHME)

MASSSTAB

1:100 (Blattgröße A2 quer)

DATUM

27.10.2026

BLATT

3 / 12 – Grundriss 1. Obergeschoss (OG1) – OK Fertigfußboden +3,50 m (Höhenbezug ANNAHME)

HÖHEN

aus B3-Modell v4 (Planstand B14); Höhenbezug zur Stadt NOCH OFFEN

STATUS

VORLÄUFIGER ENTWURF – NICHT GENEHMIGT

ANMERKUNGEN

Wandstärke 0,30 m = ANNAHME (Darstellung).

Innentüren und Türanschläge NOCH OFFEN – nicht gezeichnet.

Maße in m. Maßketten blau, Bauteilkanten schwarz.

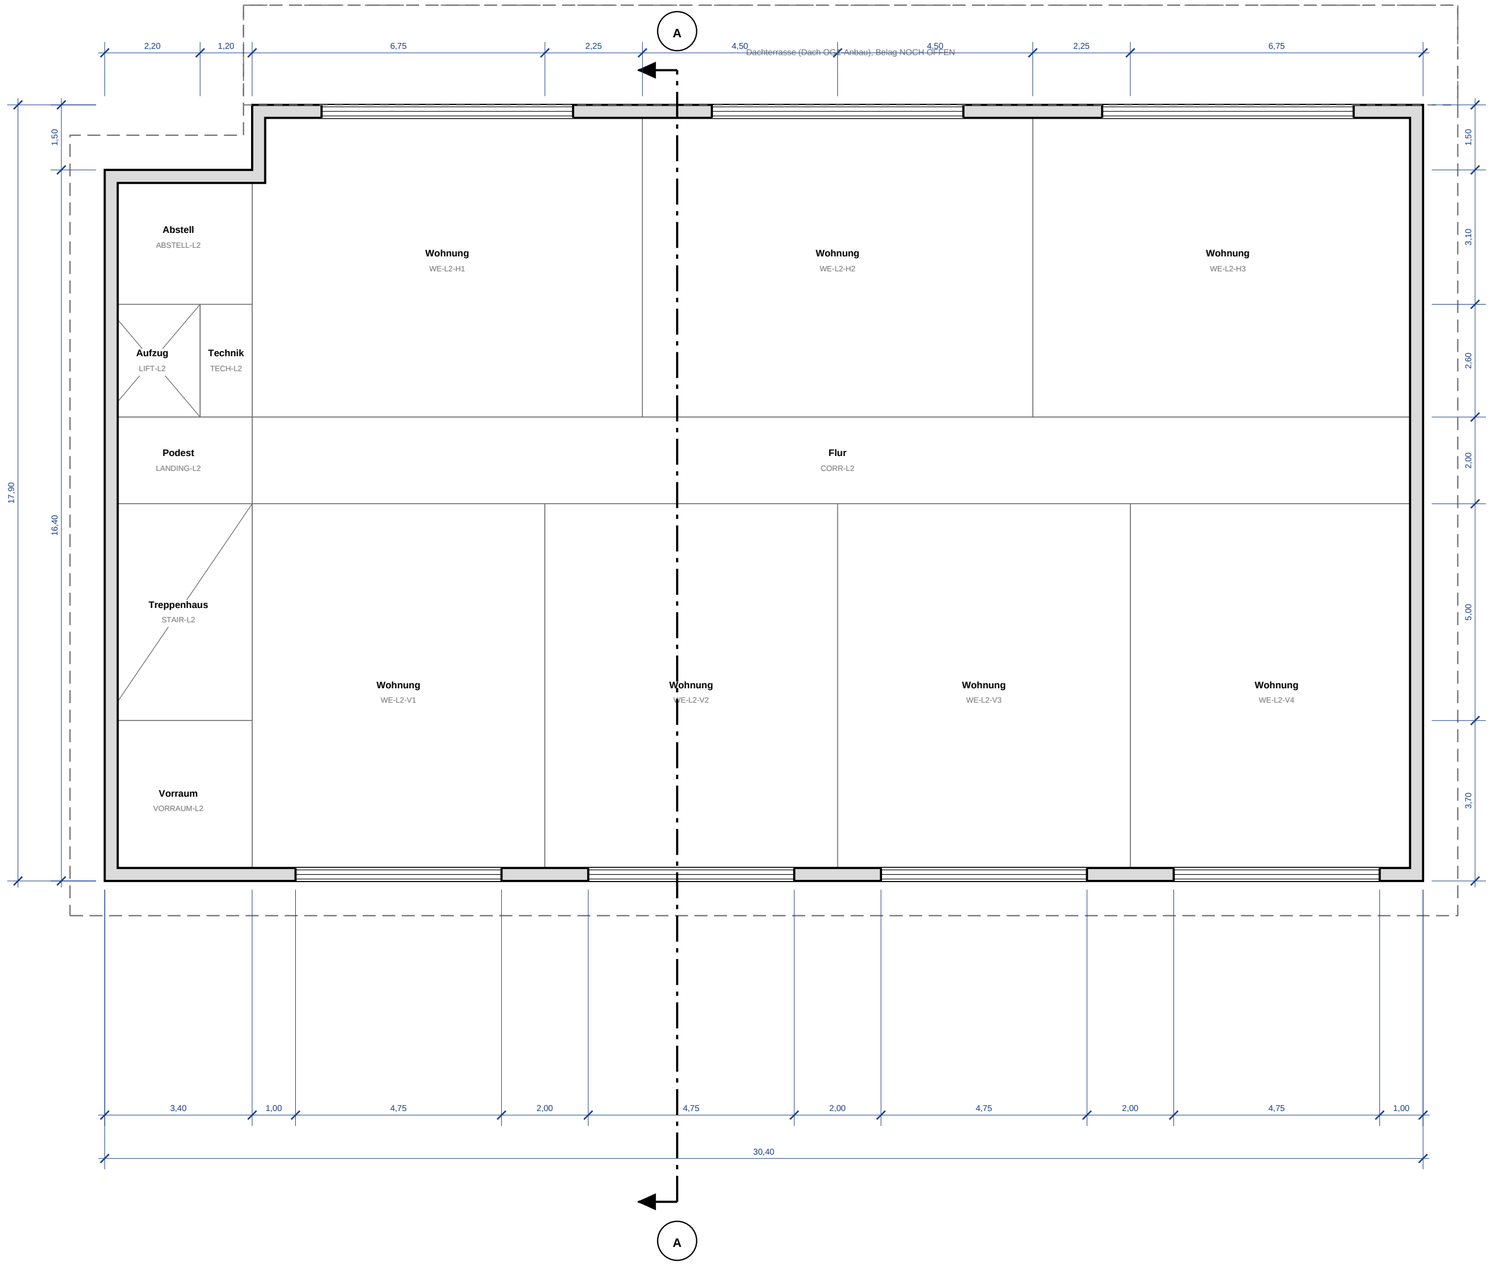

PROJEKT
Neue Mitte Werlte – Baufeld 3

VARIANTE
Variante A – B3-Referenz (unverändert)

ZEICHNUNG
Grundriss Staffelgeschoss – OK Fertigfußboden +6,50 m (Höhenbezug ANNAHME)

MASSSTAB
1:100 (Blattgröße A2 quer)

DATUM
27.10.2026

BLATT
4 / 12 – Grundriss Staffelgeschoss – OK Fertigfußboden +6,50 m (Höhenbezug ANNAHME)

HÖHEN
aus B3-Modell v4 (Planstand B14); Höhenbezug zur Stadt NOCH OFFEN

STATUS
VORLÄUFIGER ENTWURF – NICHT GENEHMIGT

ANMERKUNGEN
Wandstärke 0,30 m = ANNAHME (Darstellung).

Innentüren und Türanschläge NOCH OFFEN – nicht gezeichnet.

Maße in m. Maßketten blau, Bauteilkanten schwarz.

Vorderansicht (Platzseite, Blick von Platz)

Geschosshöhen: aus B3-Modell v4 (Planstand B14); Höhenbezug zur Stadt NOCH OFFEN

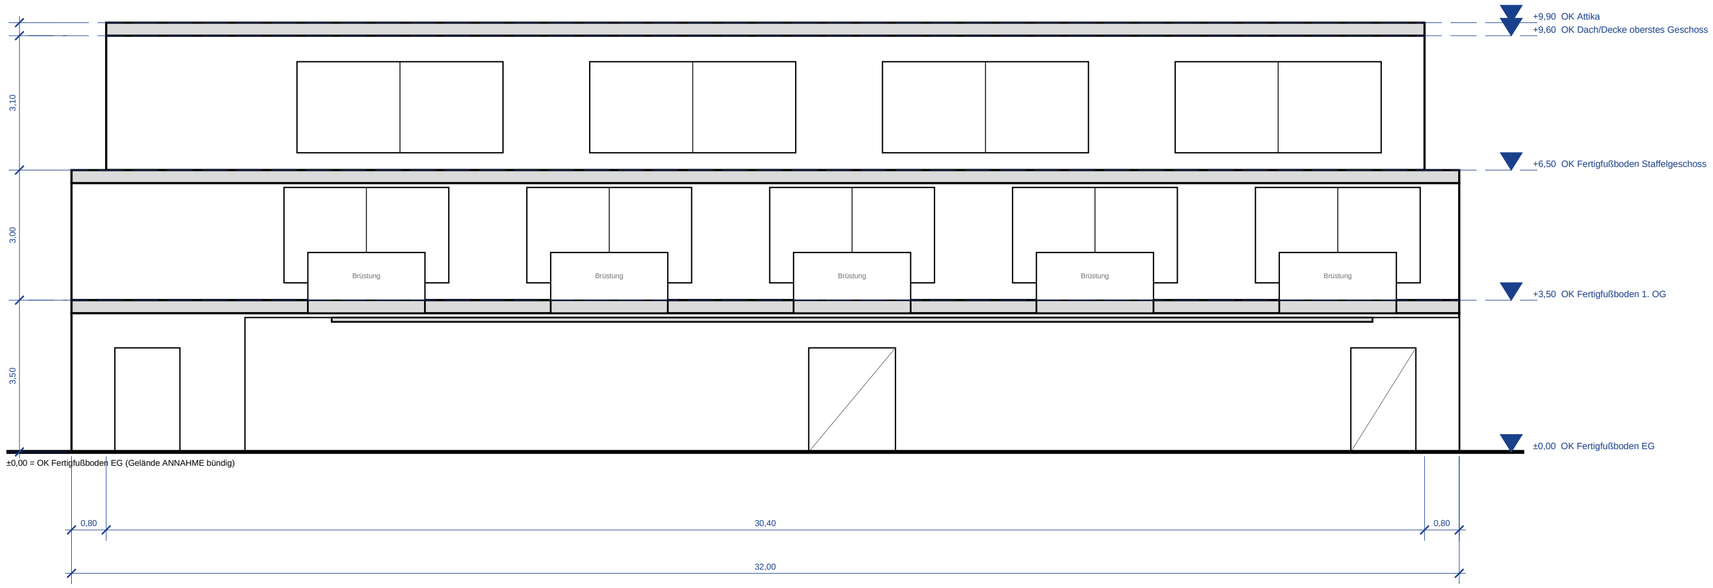

PROJEKT
Neue Mitte Werlte – Baufeld 3

VARIANTE
Variante A – B3-Referenz (unverändert)

ZEICHNUNG
Vorderansicht

MASSSTAB
1:100 (Blattgröße A2 quer)

DATUM
27.10.2026

BLATT
5 / 12 – Vorderansicht

HÖHEN
aus B3-Modell v4 (Planstand B14); Höhenbezug zur Stadt NOCH OFFEN

STATUS
VORLÄUFIGER ENTWURF – NICHT GENEHMIGT

ANMERKUNGEN
Maße in m.
Höhen: aus B3-Modell v4 (Planstand B14); Höhenbezug zur Stadt NOCH OFFEN

Rückansicht (Blick von der Rückseite)

Geschosshöhen: aus B3-Modell v4 (Planstand B14); Höhenbezug zur Stadt NOCH OFFEN

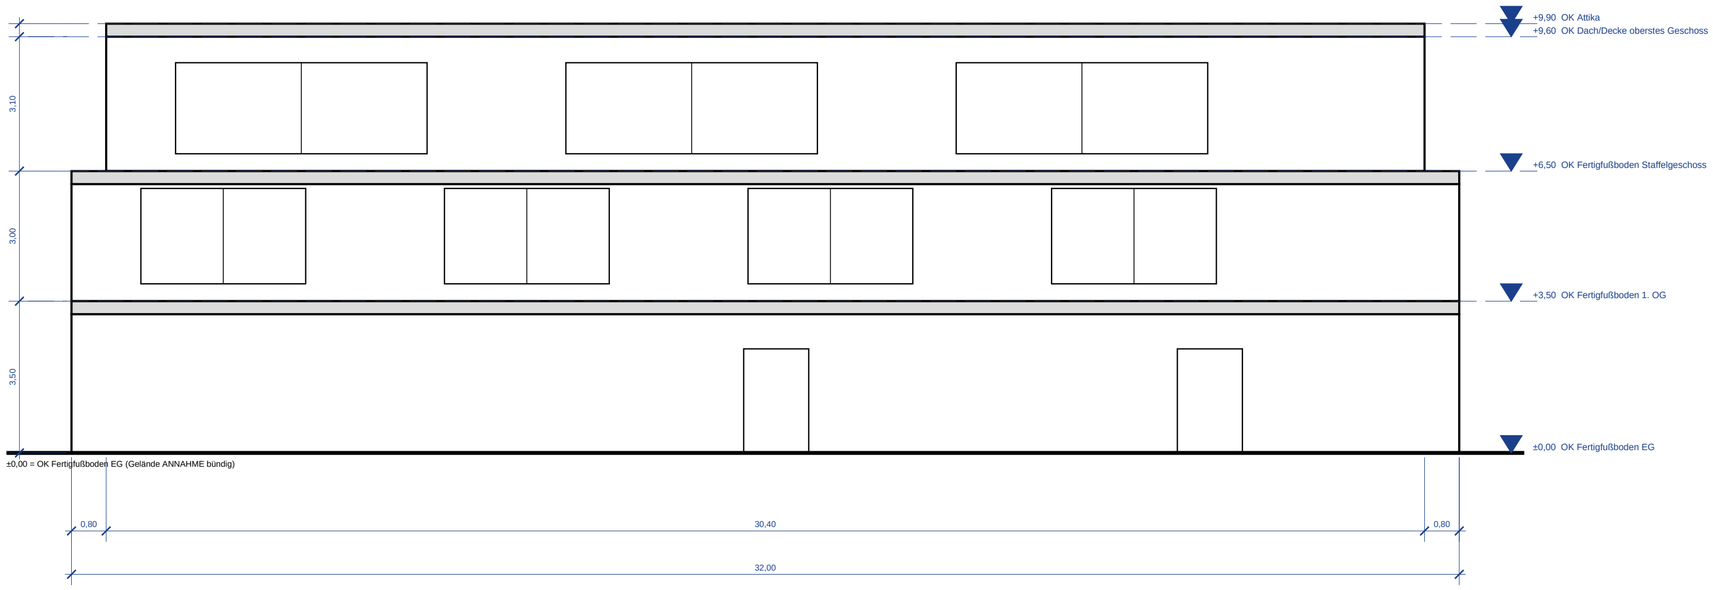

PROJEKT
Neue Mitte Werlte – Baufeld 3

VARIANTE
Variante A – B3-Referenz (unverändert)

ZEICHNUNG
Rückansicht

MASSSTAB
1:100 (Blattgröße A2 quer)

DATUM
27.10.2026

BLATT
6 / 12 – Rückansicht

HÖHEN
aus B3-Modell v4 (Planstand B14); Höhenbezug zur Stadt NOCH OFFEN

STATUS
VORLÄUFIGER ENTWURF – NICHT GENEHMIGT

ANMERKUNGEN
Maße in m.
Höhen: aus B3-Modell v4 (Planstand B14); Höhenbezug zur Stadt NOCH OFFEN

Westansicht (Seite x = 0; Nordrichtung NOCH OFFEN)

Geschosshöhen: aus B3-Modell v4 (Planstand B14); Höhenbezug zur Stadt NOCH OFFEN

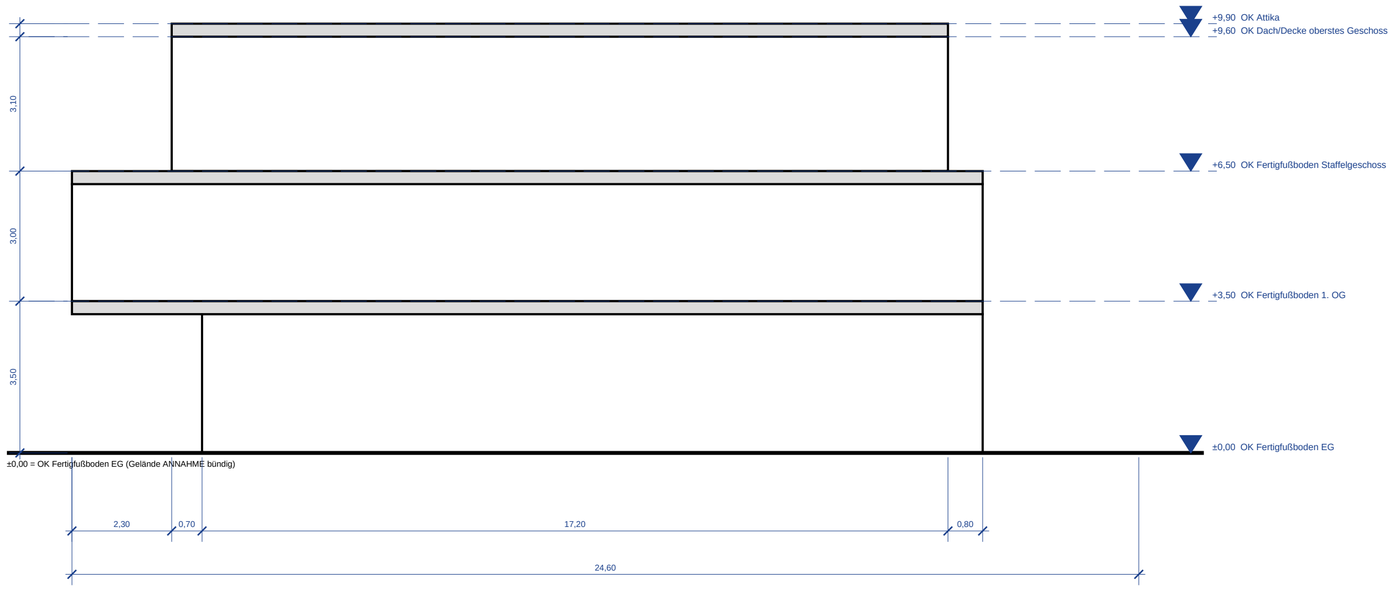

PROJEKT
Neue Mitte Werlte – Baufeld 3

VARIANTE
Variante A – B3-Referenz (unverändert)

ZEICHNUNG
Westansicht

MASSSTAB
1:100 (Blattgröße A2 quer)

DATUM
27.10.2026

BLATT
7 / 12 – Westansicht

HÖHEN
aus B3-Modell v4 (Planstand B14); Höhenbezug zur Stadt NOCH OFFEN

STATUS
VORLÄUFIGER ENTWURF – NICHT GENEHMIGT

ANMERKUNGEN
Maße in m.
Höhen: aus B3-Modell v4 (Planstand B14); Höhenbezug zur Stadt NOCH OFFEN

Ostansicht (Seite Ost; Nordrichtung NOCH OFFEN)

Geschosshöhen: aus B3-Modell v4 (Planstand B14); Höhenbezug zur Stadt NOCH OFFEN

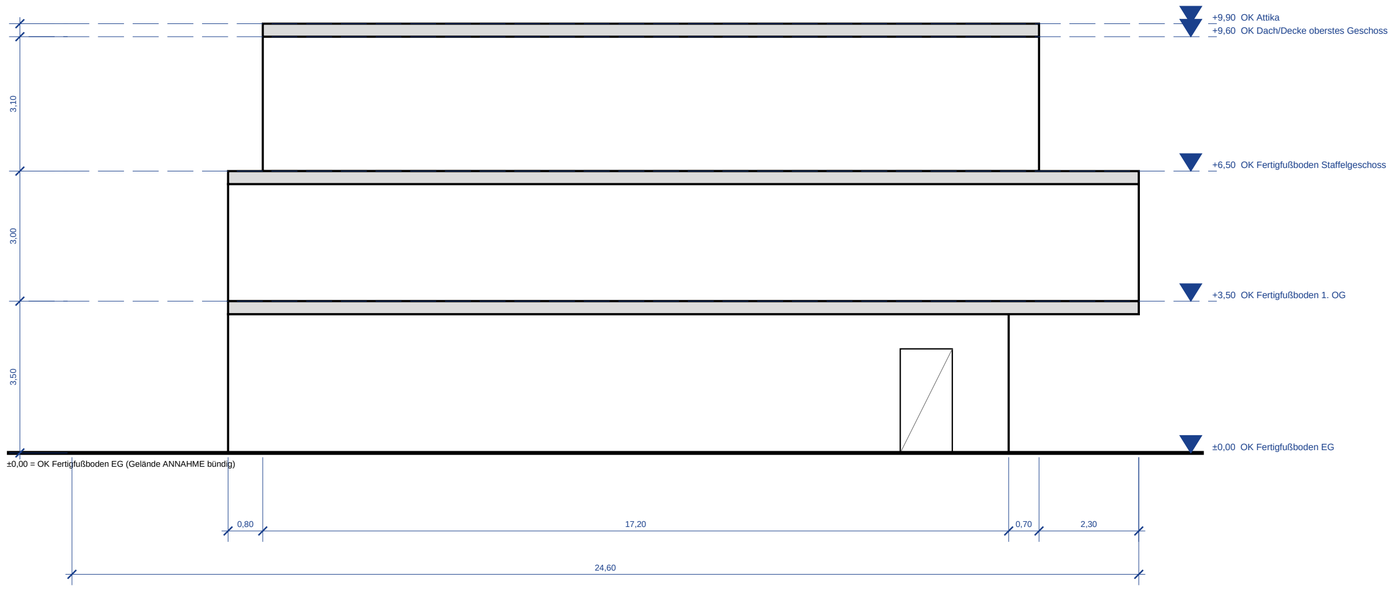

PROJEKT
Neue Mitte Werlte – Baufeld 3

VARIANTE
Variante A – B3-Referenz (unverändert)

ZEICHNUNG
Ostansicht

MASSSTAB
1:100 (Blattgröße A2 quer)

DATUM
27.10.2026

BLATT
8 / 12 – Ostansicht

HÖHEN
aus B3-Modell v4 (Planstand B14); Höhenbezug zur Stadt NOCH OFFEN

STATUS
VORLÄUFIGER ENTWURF – NICHT GENEHMIGT

ANMERKUNGEN
Maße in m.
Höhen: aus B3-Modell v4 (Planstand B14); Höhenbezug zur Stadt NOCH OFFEN

Schnitt A–A (Schnittlinie x = 14,00 m, Blick nach Westen; Platzseite links)

Geschossdecken ANNAHME 0,30 m (B3: Unterseite überdeckte Stellplätze +3,20 bei OK 3,50); Höhen: aus B3-Modell v4 (Planstand B14); Höhenbezug zur Stadt NOCH OFFEN

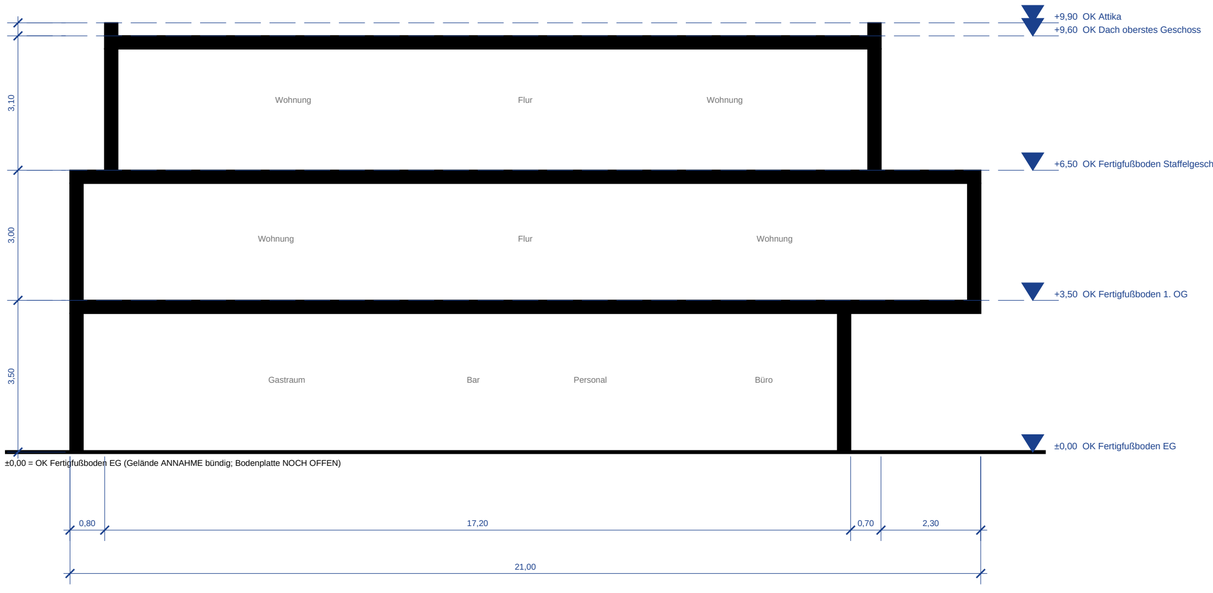

PROJEKT
Neue Mitte Werlte – Baufeld 3

VARIANTE
Variante A – B3-Referenz (unverändert)

ZEICHNUNG
Schnitt A–A mit Höhenkoten

MASSSTAB
1:100 (Blattgröße A2 quer)

DATUM
27.10.2026

BLATT
9 / 12 – Schnitt A–A mit Höhenkoten

HÖHEN
aus B3-Modell v4 (Planstand B14); Höhenbezug zur Stadt NOCH OFFEN

STATUS
VORLÄUFIGER ENTWURF – NICHT GENEHMIGT

ANMERKUNGEN
Maße in m.
Höhen: aus B3-Modell v4 (Planstand B14); Höhenbezug zur Stadt NOCH OFFEN

Stellplatz 2,50 × 5,00 m und Fahrgasse 6,00 m = ANNAHMEN (Quelle: parken.py); Gesamtzahl = Zeichnung, kein Stellplatznachweis

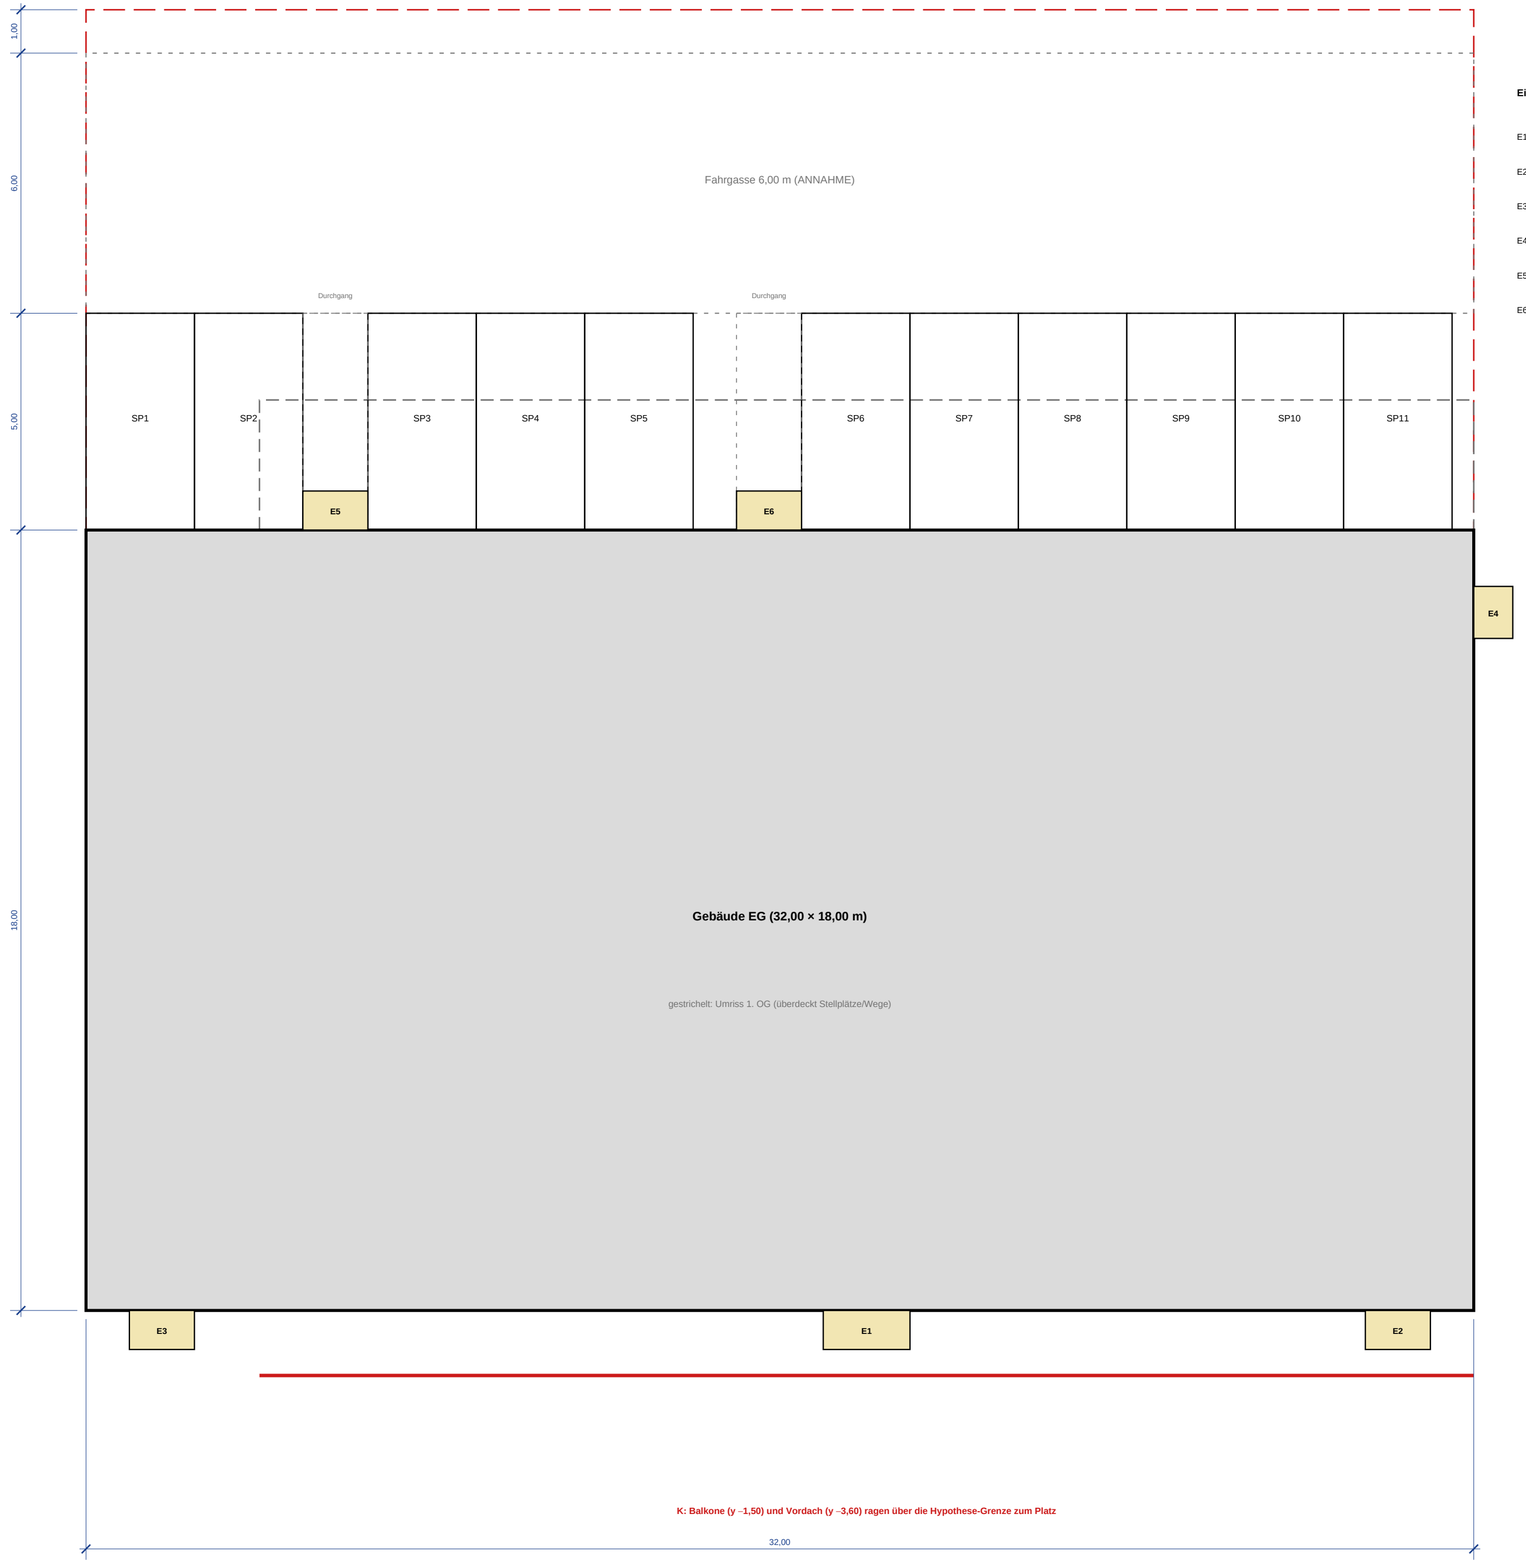

Eingänge (Lage/Breite ANNAHME):

- E1 Doppeltür Gastro
- E2 Tür Gastro Ost
- E3 Eingang Kern
- E4 Tür Ost
- E5 EG-Tür hinten 1
- E6 EG-Tür hinten 2

PROJEKT
Neue Mitte Werlte – Baufeld 3

VARIANTE
Variante A – B3-Referenz (unverändert)

ZEICHNUNG
Stellplätze / Erschließung (getrennt)

MASSSTAB
1:100 (Blattgröße A2 quer)

DATUM
27.10.2026

BLATT
10 / 12 – Stellplätze / Erschließung (getrennt)

HÖHEN
aus B3-Modell v4 (Planstand B14); Höhenbezug zur Stadt NOCH OFFEN

STATUS
VORLÄUFIGER ENTWURF – NICHT GENEHMIGT

ANMERKUNGEN
Maße in m.
Höhen: aus B3-Modell v4 (Planstand B14); Höhenbezug zur Stadt NOCH OFFEN

Rechtsebenen und Datenstände – getrennt zu lesen (keine Aussage zur Zulässigkeit)

EBENE 1 – Alter B3-Geometriestand (Modell v4, Planstand Blatt 14): in DIESEM PDF verwendet, unverändert aus geometry/variant_B3.json.
EBENE 2 – Neue Entwurfsannahmen (Planungsziel 24.10.2026: EG 18 × 30 m = 540 m², Vorbau, Säulen, Zielhöhe 12,00 m nicht bindend): in diesem PDF nicht verwendet.
EBENE 3 – B-Plan Nr. 123 (14.04.2023, rechtskräftig, wahrscheinlich MI 3 / Flurstück 59/1): MI 3 – II bis III Vollgeschosse, GRZ 0,6, Traufhöhe 9,80 m, Gebäudehöhe 15,00 m, Sockel 0,30 m; Hauptdach ≥ 38° (Flachdach nur untergeordnet); Höhenbezug OK Fahrbahn. Zuordnung Baufeld 3 = MI 3 ist NICHT bestätigt.
EBENE 4 – Änderungsentwurf 2026 (kein Beschluss, nicht rechtskräftig): II Vollgeschosse zwingend, Traufhöhe 6,50 m, Gebäudehöhe 12,00 m; erfasst MI 3 nach vorliegendem Stand nicht.
EBENE 5 – Offener Höhenbezug: ±0,00 = OK Fertigfußboden EG ist eine Zeichnungsannahme; Anbindung an OK Fahrbahn und Gelände NOCH OFFEN. Geschosshöhen dieses PDFs: aus B3-Modell v4 (Planstand B14); Höhenbezug zur Stadt NOCH OFFEN.
Die Zeichnungen enthalten KEINE Aussage, ob eine Variante baurechtlich zulässig ist; kein Geschossvergleich mit den Ebenen 3 und 4 wurde als Ergebnis eingetragen.

Nicht gesichert / NOCH OFFEN in diesem PDF

- Wandstärken (Darstellung 0,30 m ist ANNAHME)
- Deckenstärken (0,30 m ANNAHME)
- Innentüren und Türanschläge (nicht im Datenbestand) – nicht gezeichnet
- Treppenlauf/Stufen und Aufzugsgröße (nur Raumrechteck vorhanden)
- Fenstermaße OG/Staffel: Lage laut B14/B4, Brüstungs- und Sturzhöhen NOCH OFFEN
- Zufahrt/Fahrgasse-Anbindung an öffentliche Straße
- Grundstückszuschnitt (32 × 30 m = Hypothese H1)
- Höhenbezug (OK Fahrbahn) der Stadt

PROJEKT
Neue Mitte Werlte – Baufeld 3

VARIANTE
Variante A – B3-Referenz (unverändert)

ZEICHNUNG
Rechtsebenen und offene Punkte

MASSSTAB
1:100 (Blattgröße A2 quer)

DATUM
27.10.2026

BLATT
11 / 12 – Rechtsebenen und offene Punkte

HÖHEN
aus B3-Modell v4 (Planstand B14); Höhenbezug zur Stadt NOCH OFFEN

STATUS
VORLÄUFIGER ENTWURF – NICHT GENEHMIGT

ANMERKUNGEN
Maße in m.
Höhen: aus B3-Modell v4 (Planstand B14); Höhenbezug zur Stadt NOCH OFFEN

Konsistenzprotokoll (automatisch aus dem gemeinsamen Modell; Widersprüche sind dokumentiert, NICHT stillschweigend korrigiert)

[OK] EG-Außenmaß 32,00 × 18,00 m = 576 m² (Vorgabe 32 × 18 = 576 m²)
[HINWEIS] Restfläche Grundstück (Hypothese 960 m²): 384 m² – 960 m² Grundstück ist NICHT bestätigt
[OK] Höhenfolge +0,00 < +3,50 < +6,50 < +9,60 < +9,90 m
[HINWEIS] Gesamthöhe Attika-OK 9,90 m über ±0,00 (OK FFB EG); Bezug zur Stadt (OK Fahrbahn) NOCH OFFEN – keine Aussage zur Zulässigkeit
[OK] 23 von 23 Öffnungen liegen auf einer Fassadenlinie des zugehörigen Geschosses
[KONFLIKT] Balkon: 5 Bauteil(e) ragen über die Hypothese-Grenze zum Platz (y < 0) bis y = -1,50 m – Grenze/Baulinie NOCH OFFEN
[KONFLIKT] Vordach: 1 Bauteil(e) ragen über die Hypothese-Grenze zum Platz (y < 0) bis y = -3,60 m – Grenze/Baulinie NOCH OFFEN
[HINWEIS] Stahlvordach Terrasse (Unterseite +3,00 m): Stützen/Abhängung nicht belegt – keine ergänzt
[HINWEIS] EG: 19 Räume; verschachtelt (Raum liegt im Rechteck eines anderen): [('DINING-GF', 'BAR-GF')] – Flächensumme dadurch größer als Geschossfläche
[HINWEIS] EG: Raumflächensumme 590,0 m² (brutto) gegen Geschossumriss 576,0 m²
[OK] OG1: 17 Räume, keine Überschneidungen
[OK] OG1: Raumflächensumme 660,0 m² (brutto) gegen Geschossumriss 660,0 m²
[OK] ST: 14 Räume, keine Überschneidungen
[OK] ST: Raumflächensumme 539,1 m² (brutto) gegen Geschossumriss 539,1 m²
[HINWEIS] 11 Stellplätze; Rechteckmaße in x × y [(2.5, 5.0)] – 2,50 × 5,00 m und 6,00 m Fahrgasse sind ANNAHMEN
[OK] Stellplätze überschneiden sich nicht
[OK] kein Stellplatz liegt im EG-Gebäude
[OK] alle Stellplätze innerhalb der Hypothese-Grundstücksgrenze
[HINWEIS] 10 von 11 Stellplätzen teilweise überdeckt (OG1-Anbau y 18–21, Stellplatztiefe y 18–23, ca. 3,00 m von 5,00 m); Stellplätze x 0–4 unbedeckt
[HINWEIS] Fahrgasse 32,00 × 6,00 m (Annahme)

Ableitung

Alle Grundrisse, Ansichten, der Schnitt und der Lageplan dieses PDFs werden aus demselben Modell-Dict gezeichnet (Umrisse, Höhen, Säulen, Öffnungen, Stellplätze). Abweichungen zwischen Blättern sind dadurch ausgeschlossen; die Widersprüche liegen in den Eingangsdaten.

PROJEKT
Neue Mitte Werlte – Baufeld 3

VARIANTE
Variante A – B3-Referenz (unverändert)

ZEICHNUNG
Konsistenzprotokoll

MASSSTAB
1:100 (Blattgröße A2 quer)

DATUM
27.10.2026

BLATT
12 / 12 – Konsistenzprotokoll

HÖHEN
aus B3-Modell v4 (Planstand B14); Höhenbezug zur Stadt NOCH OFFEN

STATUS
VORLÄUFIGER ENTWURF – NICHT GENEHMIGT

ANMERKUNGEN
Maße in m.
Höhen: aus B3-Modell v4 (Planstand B14); Höhenbezug zur Stadt NOCH OFFEN