

Variante B – Wohngeschosse 3,00 m nach hinten ausgekragt

Grundrisse und Schnitt M 1:250 · HYPOTHETISCH: Grundstücksform, Baufenster und Rechtsfragen sind nicht belegt


Erdgeschoss 32 × 18 m mit Stellplätzen

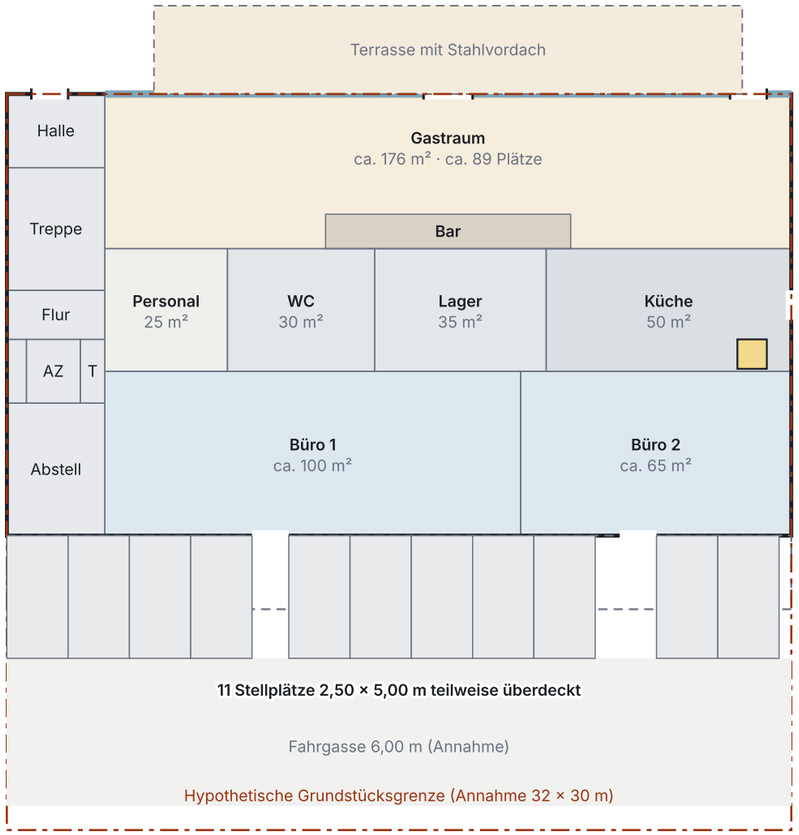

Schnitt bei x = 17,00 m

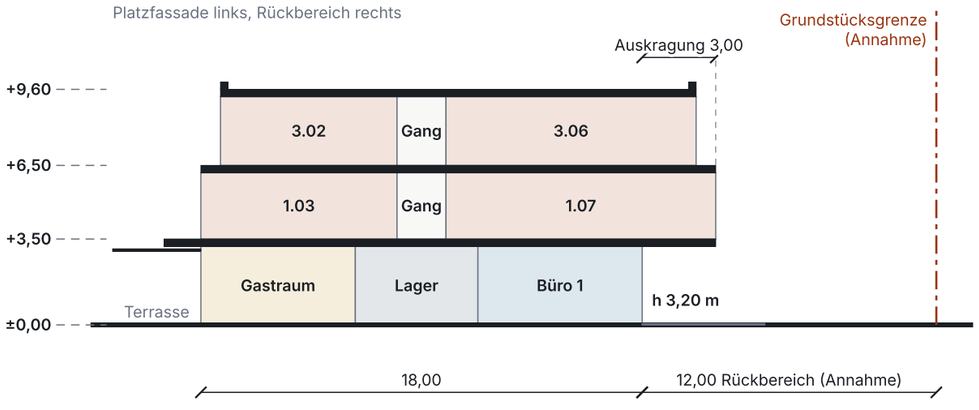


1. Obergeschoss (nur Wohnungen)

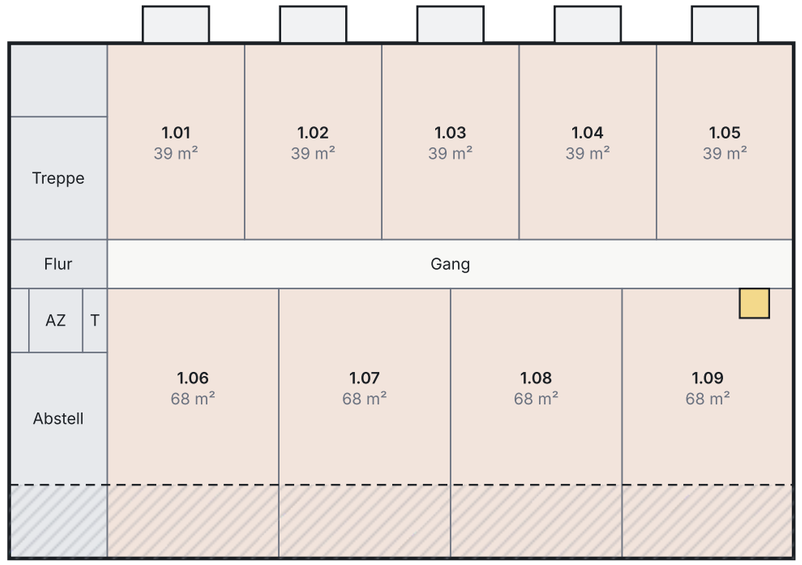

Auskragung 3,00 m (hypothetisch, schraffiert)

3. Geschoss, Staffel (nur Wohnungen)

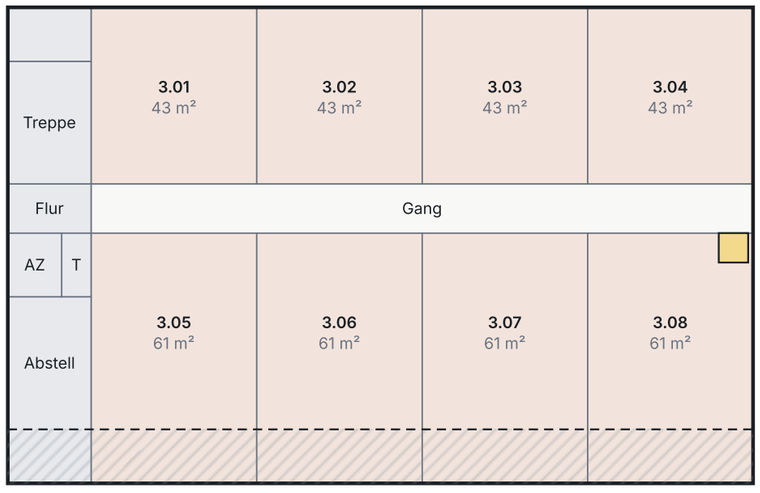

Auskragung 3,00 m (hypothetisch, schraffiert)

KENNZAHLEN

Außenmaß Erdgeschoss	**32,00 × 18,00 m**
Außenmaß 1. Obergeschoss	**32,00 × 21,00 m**
Außenmaß 3. Geschoss	**30,40 × 19,40 m**
Auskragung hinten	**3,00 m**
Geschossflächen EG/1.OG/3.G	**576 / 672 / 590 m²**
Wohnungen (1. OG + 3. Geschoss)	**9 + 8 = 17**
Wohnfläche netto gesamt	**ca. 882 m²**
Gastronomie brutto	**ca. 316 m²**
Innenplätze (geschätzt)	**ca. 89**
Büros hinten im EG, netto	**ca. 165 m²**
Stellplätze (Annahme)	**11 von 61 Bedarf**

LEGENDE

- Wohnung, Nummer nach Geschoss (1.xx, 3.xx), Wohnfläche netto
- Büro (EG, hinten)
- Gastraum und Bar
- Küche, Lager, WC, Personal
- Kern: Halle, Treppe, Flur, Abstell (AZ Aufzug, T Technik)
- Auskragung (hypothetisch)
- Stellplatz 2,50 × 5,00 m (Annahme)
- hypothetische Grundstücksgrenze
- Küchenabluft-Schacht, alle Geschosse

OFFENE PUNKTE (NICHT GELÖST)

- C-30 Baufenster, GRZ und Zählung der Auskragungen unbekannt: Projektion 672 m², nicht nachweisbar zulässig.
- C-28 Stellplatzbedarf 61 laut Excel, hier nur 11 Stellplätze nachweisbar.
- C-29 Grundstückszuschnitt, Zufahrt und Anlieferung unbekannt.
- C-31 Gastro 316 m² statt 504 m²: Umsatz und Pacht nicht neu gerechnet.
- C-22 Küchenabluft-Schacht läuft durch Wohnungen.
- C-35 Tragwerk: Kragarm
- C-36 Fluchtwege EG nur als Annahme.

HINWEISE

Erdgeschoss in allen Varianten gleich; Büros liegen hinter der Gastronomie, Wohnungen nur im 1. Obergeschoss und im 3. Geschoss.

Flächen netto = Brutto × 0,88 (Annahme). Fenster, Türen und Wandstärken sind nicht festgelegt.

Keine Variante ist festgelegt, keine Rendering-Erzeugung.

Neue Mitte Werlte · Baufeld 3

Bauvorhaben: Restaurant und Bar, Büros, Wohnungen

Variante B – Grundrisse und Schnitt

Maßstab 1:250 (A3)

Stand 22.10.2026 · Modell NEUE_MITTE_MASTER_DRAFT_A_003

VORLÄUFIGER ARBEITSSTAND – nicht freigegeben