

Variante C – Wohngeschosse 6,00 m ausgekragt, Stellplätze überdeckt

Grundrisse und Schnitt M 1:250 · HYPOTHETISCH: Grundstücksform, Baufenster und Rechtsfragen sind nicht belegt


Erdgeschoss 32 × 18 m mit Stellplätzen

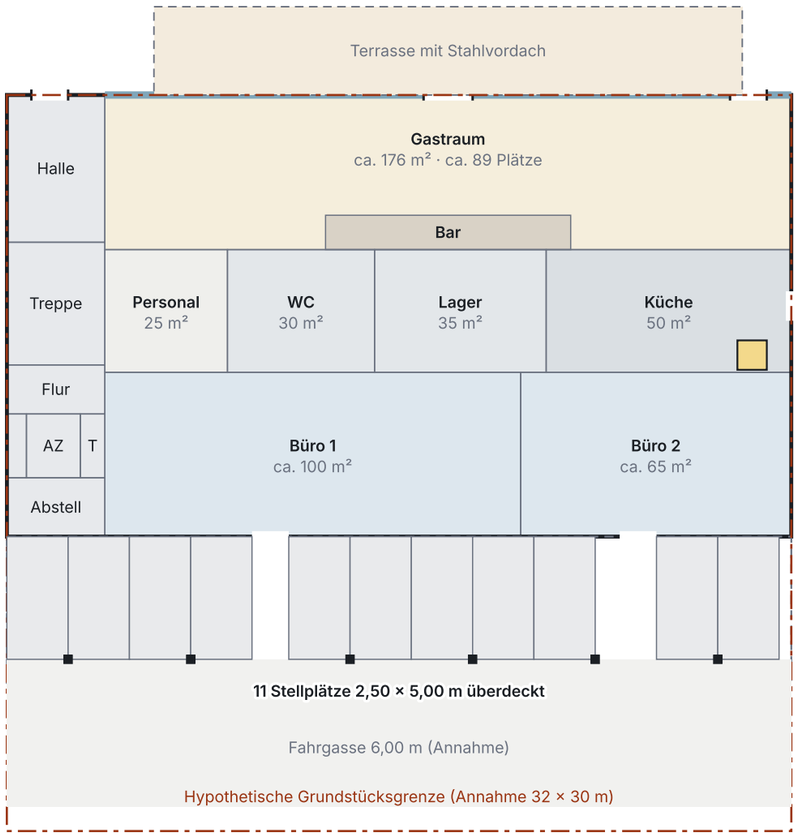

Schnitt bei x = 17,00 m

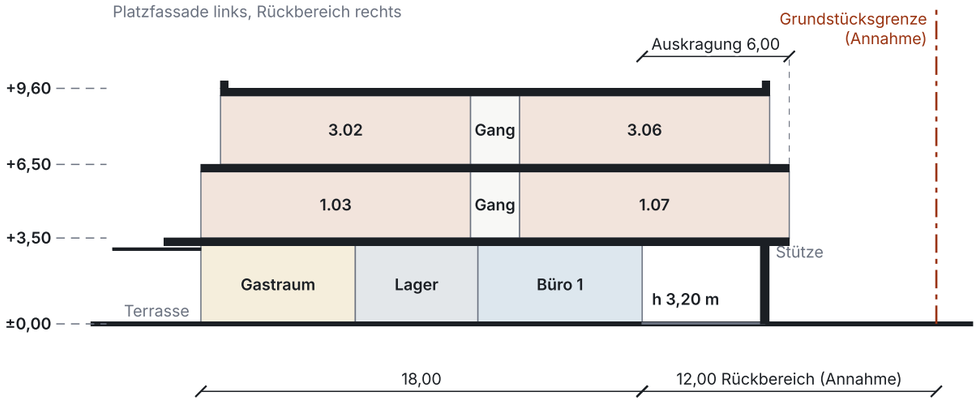


1. Obergeschoss (nur Wohnungen)

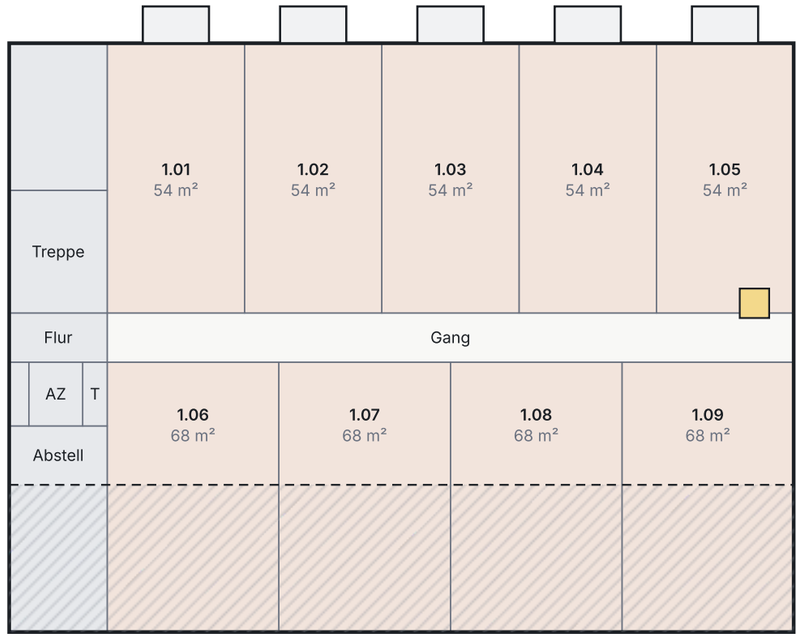

Auskragung 6,00 m (hypothetisch, schraffiert)

3. Geschoss, Staffel (nur Wohnungen)

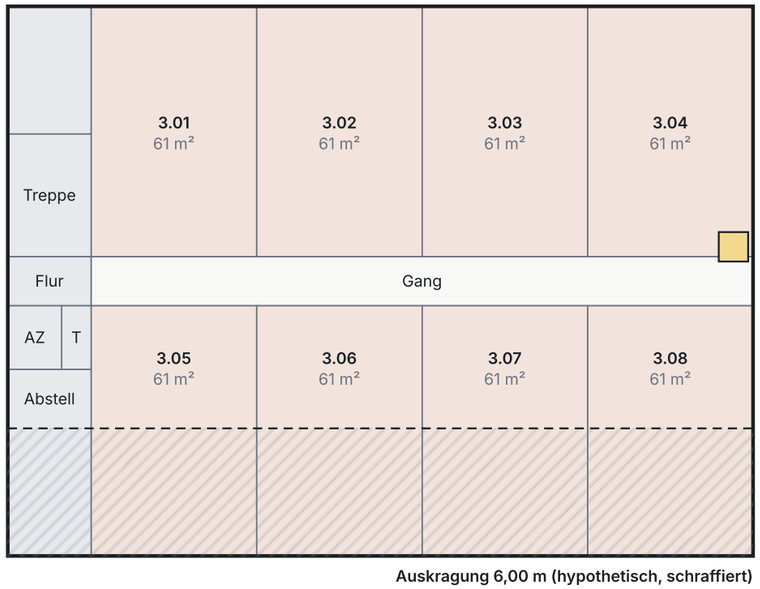

Auskragung 6,00 m (hypothetisch, schraffiert)

KENNZAHLEN

Außenmaß Erdgeschoss	32,00 × 18,00 m
Außenmaß 1. Obergeschoss	32,00 × 24,00 m
Außenmaß 3. Geschoss	30,40 × 22,40 m
Auskragung hinten	6,00 m
Geschossflächen EG/1.OG/3.G	576 / 768 / 681 m²
Wohnungen (1. OG + 3. Geschoss)	9 + 8 = 17
Wohnfläche netto gesamt	ca. 1027 m²
Gastronomie brutto	ca. 316 m²
Innenplätze (geschätzt)	ca. 89
Büros hinten im EG, netto	ca. 165 m²
Stellplätze (Annahme)	11 von 61 Bedarf

LEGENDE

- Wohnung, Nummer nach Geschoss (1.xx, 3.xx), Wohnfläche netto
- Büro (EG, hinten)
- Gastraum und Bar
- Küche, Lager, WC, Personal
- Kern: Halle, Treppe, Flur, Abstell (AZ Aufzug, T Technik)
- Auskragung (hypothetisch)
- Stellplatz 2,50 × 5,00 m (Annahme)
- hypothetische Grundstücksgrenze
- Küchenabluft-Schacht, alle Geschosse

OFFENE PUNKTE (NICHT GELÖST)

- C-30 Baufenster, GRZ und Zählung der Auskragungen unbekannt: Projektion 768 m², nicht nachweisbar zulässig.
- C-28 Stellplatzbedarf 61 laut Excel, hier nur 11 Stellplätze nachweisbar.
- C-29 Grundstückszuschnitt, Zufahrt und Anlieferung unbekannt.
- C-31 Gastro 316 m² statt 504 m²: Umsatz und Pacht nicht neu gerechnet.
- C-22 Küchenabluft-Schacht läuft durch Wohnungen.
- C-35 Tragwerk: Raster 5,6 m gegen 5,0 m Stützenraster Stellplätze, 6 Stützen.
- C-36 Fluchtwege EG nur als Annahme.

HINWEISE

Variante C ist die Obergrenze der Untersuchung, kein Vorschlag. Vordere Wohnungen sind 11 m tief bei 5,6 m Breite (Verhältnis 1,96).

Erdgeschoss in allen Varianten gleich; Büros liegen hinter der Gastronomie, Wohnungen nur im 1. Obergeschoss und im 3. Geschoss.

Flächen netto = Brutto × 0,88 (Annahme). Fenster, Türen und Wandstärken sind nicht festgelegt.

Keine Variante ist festgelegt, keine Rendering-Erzeugung.

Neue Mitte Werlte · Baufeld 3

Bauvorhaben: Restaurant und Bar, Büros, Wohnungen

Variante C – Grundrisse und Schnitt

Maßstab 1:250 (A3)

Stand 22.10.2026 · Modell NEUE_MITTE_MASTER_DRAFT_A_003

VORLÄUFIGER ARBEITSSTAND – nicht freigegeben