

Variante A – Erdgeschoss 32 × 18 m, Obergeschosse wie bisher

Grundrisse und Schnitt M 1:250 · HYPOTHETISCH: Grundstücksform, Baufenster und Rechtsfragen sind nicht belegt

Erdgeschoss 32 × 18 m mit Stellplätzen

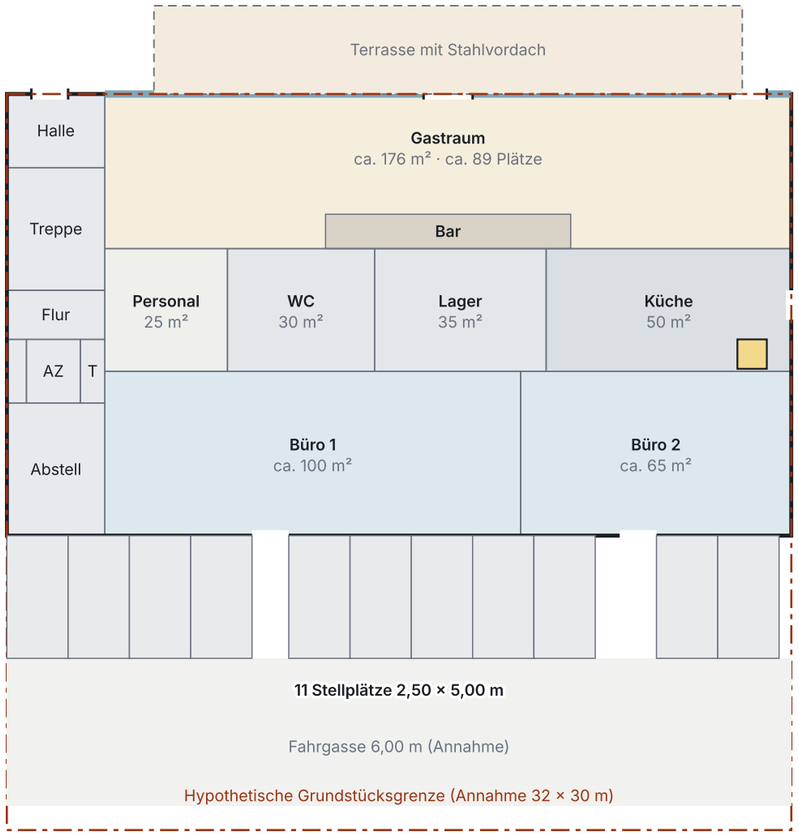


Schnitt bei x = 17,00 m

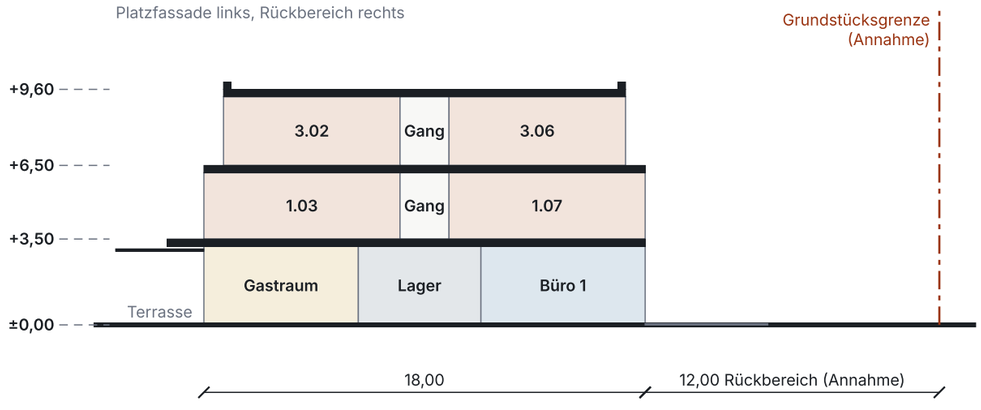

1. Obergeschoss (nur Wohnungen)



3. Geschoss, Staffel (nur Wohnungen)

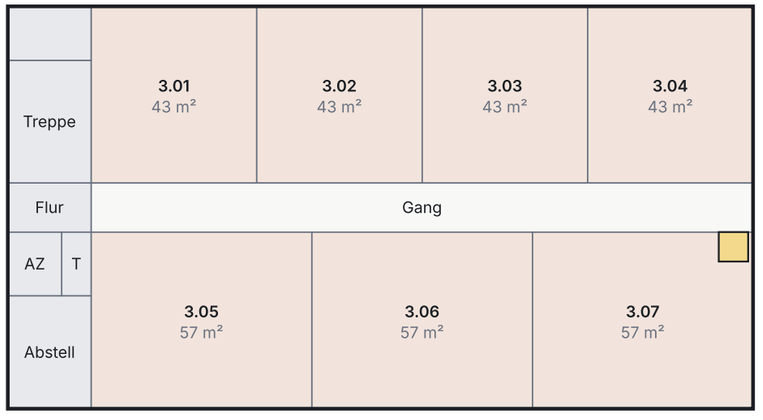

KENNZAHLEN

Außenmaß Erdgeschoss	**32,00 × 18,00 m**
Außenmaß 1. Obergeschoss	**32,00 × 18,00 m**
Außenmaß 3. Geschoss	**30,40 × 16,40 m**
Auskragung hinten	**0,00 m**
Geschossflächen EG/1.OG/3.G	**576 / 576 / 499 m²**
Wohnungen (1. OG + 3. Geschoss)	**8 + 7 = 15**
Wohnfläche netto gesamt	**ca. 736 m²**
Gastronomie brutto	**ca. 316 m²**
Innenplätze (geschätzt)	**ca. 89**
Büros hinten im EG, netto	**ca. 165 m²**
Stellplätze (Annahme)	**11 von 61 Bedarf**

LEGENDE

- Wohnung, Nummer nach Geschoss (1.xx, 3.xx), Wohnfläche netto
- Büro (EG, hinten)
- Gastraum und Bar
- Küche, Lager, WC, Personal
- Kern: Halle, Treppe, Flur, Abstell (AZ Aufzug, T Technik)
- Auskragung (hypothetisch)
- Stellplatz 2,50 × 5,00 m (Annahme)
- hypothetische Grundstücksgrenze
- Küchenabluft-Schacht, alle Geschosse

OFFENE PUNKTE (NICHT GELÖST)

- C-30 Baufenster, GRZ und Zählung der Auskragungen unbekannt: Variante ohne Überschreitung der 576 m².
- C-28 Stellplatzbedarf 61 laut Excel, hier nur 11 Stellplätze nachweisbar.
- C-29 Grundstückszuschnitt, Zufahrt und Anlieferung unbekannt.
- C-31 Gastro 316 m² statt 504 m²: Umsatz und Pacht nicht neu gerechnet.
- C-22 Küchenabluft-Schacht läuft durch Wohnungen.
- C-35 Tragwerk: keine Auskragung.
- C-36 Fluchtwege EG nur als Annahme.

HINWEISE

Erdgeschoss in allen Varianten gleich; Büros liegen hinter der Gastronomie, Wohnungen nur im 1. Obergeschoss und im 3. Geschoss.

Flächen netto = Brutto × 0,88 (Annahme). Fenster, Türen und Wandstärken sind nicht festgelegt.

Keine Variante ist festgelegt, keine Rendering-Erzeugung.

Neue Mitte Werlte · Baufeld 3

Bauvorhaben: Restaurant und Bar, Büros, Wohnungen

Variante A – Grundrisse und Schnitt

Maßstab 1:250 (A3)


Stand 22.10.2026 · Modell NEUE_MITTE_MASTER_DRAFT_A_003

VORLÄUFIGER ARBEITSSTAND – nicht freigegeben


Variante B – Wohngeschosse 3,00 m nach hinten ausgekragt

Grundrisse und Schnitt M 1:250 · HYPOTHETISCH: Grundstücksform, Baufenster und Rechtsfragen sind nicht belegt


Erdgeschoss 32 × 18 m mit Stellplätzen

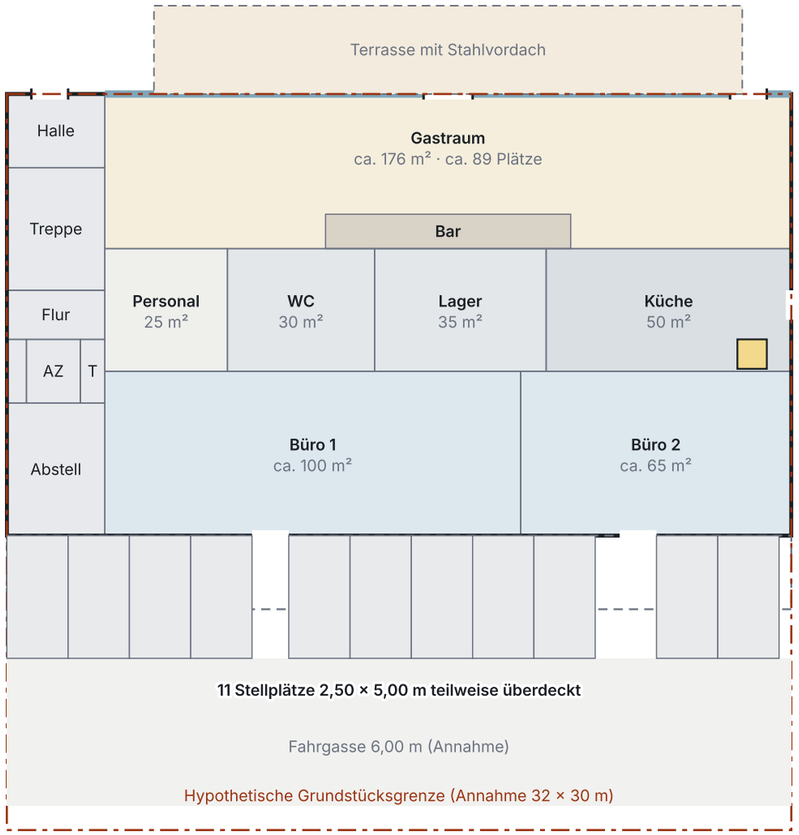

Schnitt bei x = 17,00 m

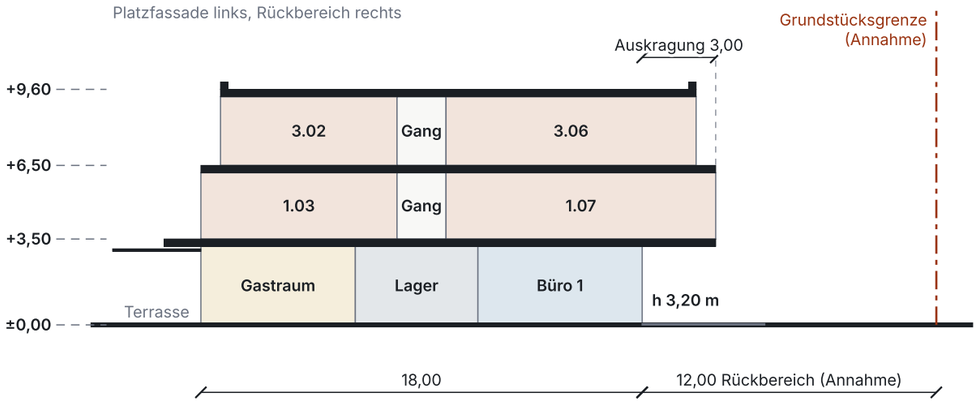


1. Obergeschoss (nur Wohnungen)

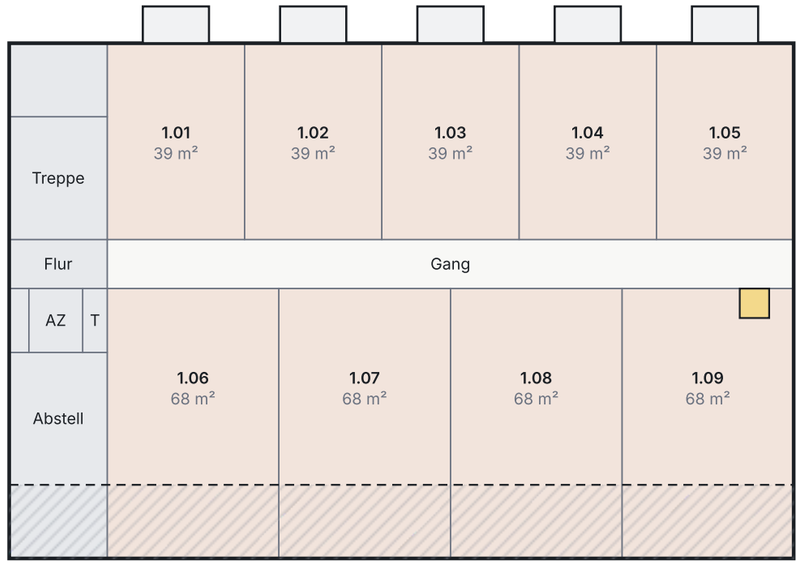

Auskragung 3,00 m (hypothetisch, schraffiert)

3. Geschoss, Staffel (nur Wohnungen)

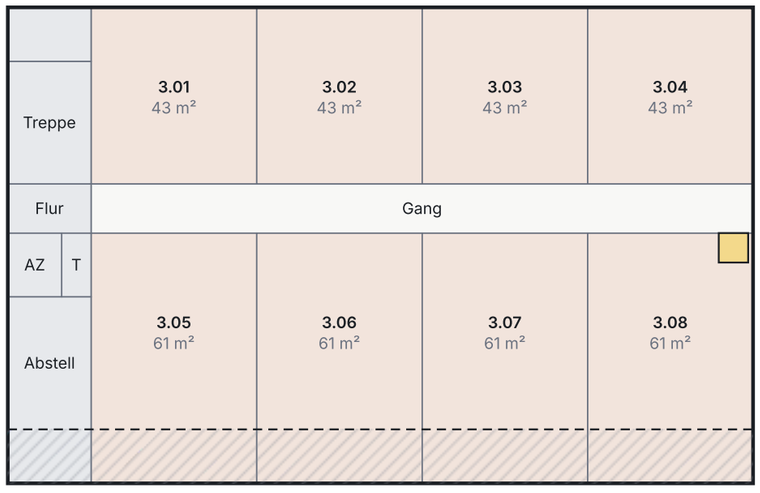

Auskragung 3,00 m (hypothetisch, schraffiert)

KENNZAHLEN

Außenmaß Erdgeschoss	**32,00 × 18,00 m**
Außenmaß 1. Obergeschoss	**32,00 × 21,00 m**
Außenmaß 3. Geschoss	**30,40 × 19,40 m**
Auskragung hinten	**3,00 m**
Geschossflächen EG/1.OG/3.G	**576 / 672 / 590 m²**
Wohnungen (1. OG + 3. Geschoss)	**9 + 8 = 17**
Wohnfläche netto gesamt	**ca. 882 m²**
Gastronomie brutto	**ca. 316 m²**
Innenplätze (geschätzt)	**ca. 89**
Büros hinten im EG, netto	**ca. 165 m²**
Stellplätze (Annahme)	**11 von 61 Bedarf**

LEGENDE

- Wohnung, Nummer nach Geschoss (1.xx, 3.xx), Wohnfläche netto
- Büro (EG, hinten)
- Gastraum und Bar
- Küche, Lager, WC, Personal
- Kern: Halle, Treppe, Flur, Abstell (AZ Aufzug, T Technik)
- Auskragung (hypothetisch)
- Stellplatz 2,50 × 5,00 m (Annahme)
- hypothetische Grundstücksgrenze
- Küchenabluft-Schacht, alle Geschosse

OFFENE PUNKTE (NICHT GELÖST)

- C-30 Baufenster, GRZ und Zählung der Auskragungen unbekannt: Projektion 672 m², nicht nachweisbar zulässig.
- C-28 Stellplatzbedarf 61 laut Excel, hier nur 11 Stellplätze nachweisbar.
- C-29 Grundstückszuschnitt, Zufahrt und Anlieferung unbekannt.
- C-31 Gastro 316 m² statt 504 m²: Umsatz und Pacht nicht neu gerechnet.
- C-22 Küchenabluft-Schacht läuft durch Wohnungen.
- C-35 Tragwerk: Kragarm
- C-36 Fluchtwege EG nur als Annahme.

HINWEISE

Erdgeschoss in allen Varianten gleich; Büros liegen hinter der Gastronomie, Wohnungen nur im 1. Obergeschoss und im 3. Geschoss.

Flächen netto = Brutto × 0,88 (Annahme). Fenster, Türen und Wandstärken sind nicht festgelegt.

Keine Variante ist festgelegt, keine Rendering-Erzeugung.

Neue Mitte Werlte · Baufeld 3

Bauvorhaben: Restaurant und Bar, Büros, Wohnungen

Variante B – Grundrisse und Schnitt

Maßstab 1:250 (A3)


Stand 22.10.2026 · Modell NEUE_MITTE_MASTER_DRAFT_A_003

VORLÄUFIGER ARBEITSSTAND – nicht freigegeben


Variante C – Wohngeschosse 6,00 m ausgekragt, Stellplätze überdeckt

Grundrisse und Schnitt M 1:250 · HYPOTHETISCH: Grundstücksform, Baufenster und Rechtsfragen sind nicht belegt


Erdgeschoss 32 × 18 m mit Stellplätzen

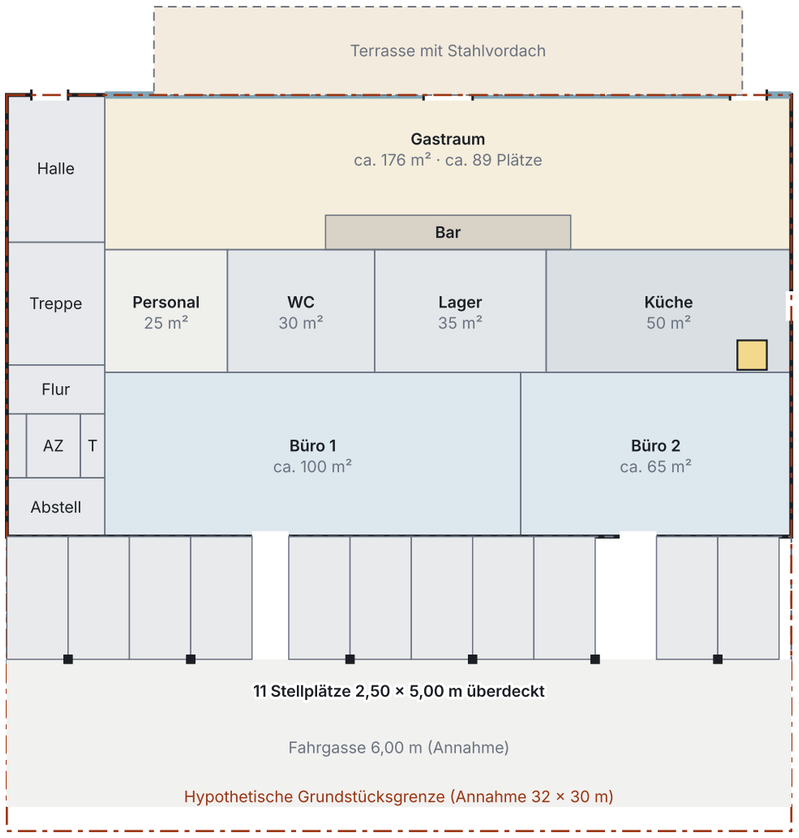

Schnitt bei x = 17,00 m

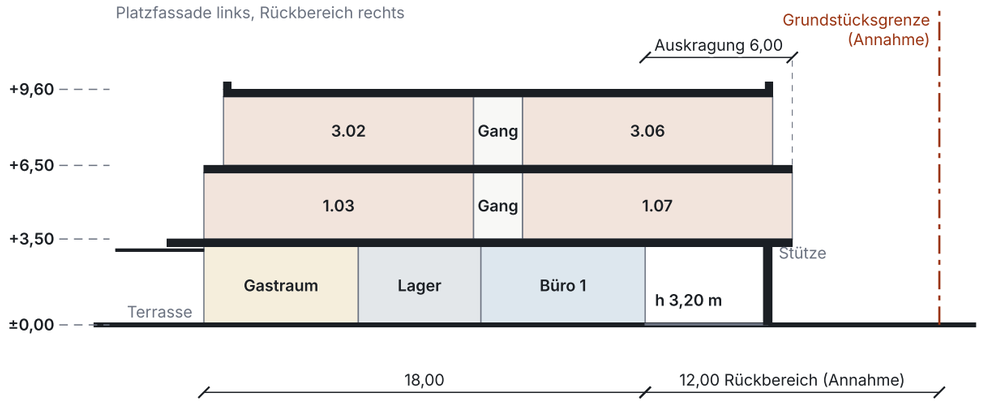


1. Obergeschoss (nur Wohnungen)

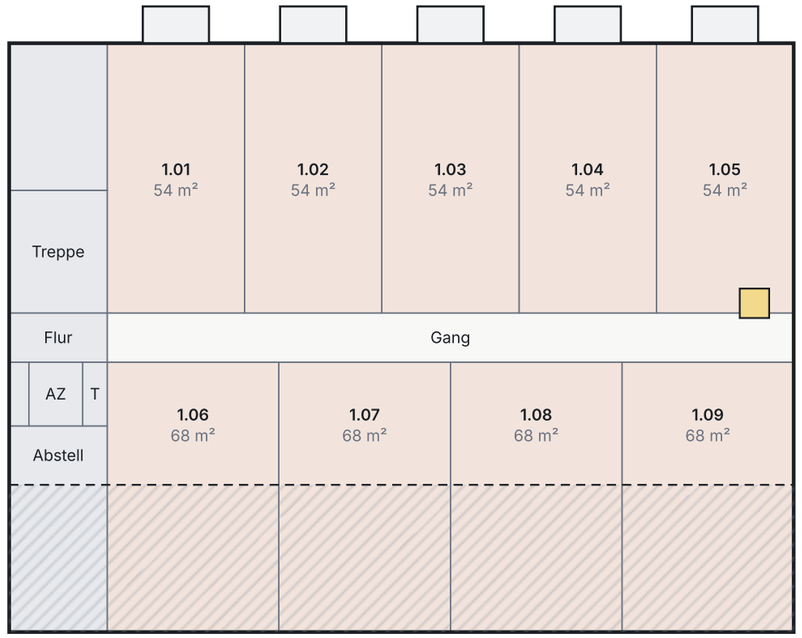

Auskragung 6,00 m (hypothetisch, schraffiert)

3. Geschoss, Staffel (nur Wohnungen)

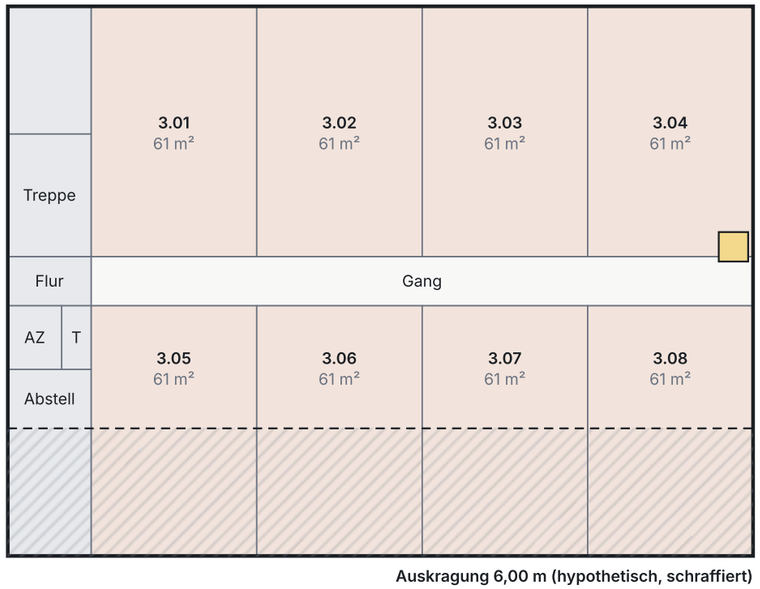

Auskragung 6,00 m (hypothetisch, schraffiert)

KENNZAHLEN

Außenmaß Erdgeschoss	32,00 × 18,00 m
Außenmaß 1. Obergeschoss	32,00 × 24,00 m
Außenmaß 3. Geschoss	30,40 × 22,40 m
Auskragung hinten	6,00 m
Geschossflächen EG/1.OG/3.G	576 / 768 / 681 m²
Wohnungen (1. OG + 3. Geschoss)	9 + 8 = 17
Wohnfläche netto gesamt	ca. 1027 m²
Gastronomie brutto	ca. 316 m²
Innenplätze (geschätzt)	ca. 89
Büros hinten im EG, netto	ca. 165 m²
Stellplätze (Annahme)	11 von 61 Bedarf

LEGENDE

- Wohnung, Nummer nach Geschoss (1.xx, 3.xx), Wohnfläche netto
- Büro (EG, hinten)
- Gastraum und Bar
- Küche, Lager, WC, Personal
- Kern: Halle, Treppe, Flur, Abstell (AZ Aufzug, T Technik)
- Auskragung (hypothetisch)
- Stellplatz 2,50 × 5,00 m (Annahme)
- hypothetische Grundstücksgrenze
- Küchenabluft-Schacht, alle Geschosse

OFFENE PUNKTE (NICHT GELÖST)

- C-30 Baufenster, GRZ und Zählung der Auskragungen unbekannt: Projektion 768 m², nicht nachweisbar zulässig.
- C-28 Stellplatzbedarf 61 laut Excel, hier nur 11 Stellplätze nachweisbar.
- C-29 Grundstückszuschnitt, Zufahrt und Anlieferung unbekannt.
- C-31 Gastro 316 m² statt 504 m²: Umsatz und Pacht nicht neu gerechnet.
- C-22 Küchenabluft-Schacht läuft durch Wohnungen.
- C-35 Tragwerk: Raster 5,6 m gegen 5,0 m Stützenraster Stellplätze, 6 Stützen.
- C-36 Fluchtwege EG nur als Annahme.

HINWEISE

Variante C ist die Obergrenze der Untersuchung, kein Vorschlag. Vordere Wohnungen sind 11 m tief bei 5,6 m Breite (Verhältnis 1,96).

Erdgeschoss in allen Varianten gleich; Büros liegen hinter der Gastronomie, Wohnungen nur im 1. Obergeschoss und im 3. Geschoss.

Flächen netto = Brutto × 0,88 (Annahme). Fenster, Türen und Wandstärken sind nicht festgelegt.

Keine Variante ist festgelegt, keine Rendering-Erzeugung.

Neue Mitte Werlte · Baufeld 3

Bauvorhaben: Restaurant und Bar, Büros, Wohnungen

Variante C – Grundrisse und Schnitt

Maßstab 1:250 (A3)

Stand 22.10.2026 · Modell NEUE_MITTE_MASTER_DRAFT_A_003

VORLÄUFIGER ARBEITSSTAND – nicht freigegeben

Vergleich der Varianten A, B und C

Alle Werte hypothetisch und aus der Geometrie berechnet. Keine Variante ist festgelegt.

Kriterium	A: Obergeschosse wie bisher	B: Auskragung 3,00 m	C: Auskragung 6,00 m
Außenmaße	EG 32 × 18 · 1. OG 32 × 18,00 · 3. Geschoss 30,4 × 16,40 m	EG 32 × 18 · 1. OG 32 × 21,00 · 3. Geschoss 30,4 × 19,40 m	EG 32 × 18 · 1. OG 32 × 24,00 · 3. Geschoss 30,4 × 22,40 m
Auskragung und projizierte Fläche	0,00 m · 576 m² = GRZ 0,60	3,00 m · 672 m² = GRZ 0,70	6,00 m · 768 m² = GRZ 0,80
Geschossflächen und Kubatur (Näherung)	BGF 1.651 m² · BRI ca. 5.290 m³	BGF 1.838 m² · BRI ca. 5.860 m³	BGF 2.025 m² · BRI ca. 6.431 m³
Gastronomie (EG vorn und Mitte)	ca. 316 m² brutto, Gastraum und Bar 176 m²	ca. 316 m² brutto, Gastraum und Bar 176 m²	ca. 316 m² brutto, Gastraum und Bar 176 m²
Sitzplätze (geschätzt)	ca. 89 innen (2,1 m² je Platz) + 60 Terrasse	ca. 89 innen (2,1 m² je Platz) + 60 Terrasse	ca. 89 innen (2,1 m² je Platz) + 60 Terrasse
Büros im hinteren EG	ca. 165 m² netto (100 + 65)	ca. 165 m² netto (100 + 65)	ca. 165 m² netto (100 + 65)
Wohnungen (1. OG + 3. Geschoss)	8 + 7 = 15	9 + 8 = 17	9 + 8 = 17
Wohnungsgrößen netto (m²)	39, 43, 57, 79	39, 43, 61, 68	54, 61, 68
Wohnfläche netto gesamt	ca. 736 m² (Excel-Stand 655 m²)	ca. 882 m² (Excel-Stand 655 m²)	ca. 1.027 m² (Excel-Stand 655 m²)
Wohnfläche je Geschossfläche (BGF)	45 %	48 %	51 %
Zusätzliche Wohnfläche gegenüber A	–	+146 m² (+20 %)	+291 m² (+40 %)
Wohnqualität	Vorn 5 Studios mit Balkon, hinten 1 Studio und 2 Dreizimmerwohnungen ohne Außenraum	Vorn wie A, hinten 4 Wohnungen 68 m², Tiefe 11 m, ohne Außenraum	Vorn 5 Wohnungen 54 m², Tiefe 11 m bei 5,6 m Breite (1,96), hinten wie B
Stellplätze, Rangierfläche (Annahme)	11 Plätze, Fahrgasse 6,00 m, 192 m²; Bedarf 61	11 Plätze, Fahrgasse 6,00 m, 192 m²; Bedarf 61	11 Plätze, Fahrgasse 6,00 m, 192 m²; Bedarf 61
Überdachung und Stützen	keine	3,00 m der 5,00 m Stelltiefe, keine Stützen	voll überdeckt, 6 Stützen an der Stellplatzvorderkante
Durchfahrtshöhe unter Auskragung	–	3,20 m (Plattenunterseite)	3,20 m (Plattenunterseite)
Nachweisstatus	GRZ-Grenze erreicht, Baufenster ungeklärt	Projektion 672 m², nicht nachweisbar	Projektion 768 m², nicht nachweisbar

KENNZAHLEN

Erdgeschoss	**in allen Varianten 32 × 18 m**

OFFENE PUNKTE (NICHT GELÖST)

- C-30 Baufenster, GRZ und Zählung von Auskragungen sind unbekannt: B und C nicht nachweisbar.
- C-28 Stellplätze: Bedarf 61, nachweisbar nur 11 (Annahme).
- C-29 Grundstückszuschnitt (hier 32 × 30 m angenommen), Zufahrt, Anlieferung unbekannt.
- C-31 Gastronomie 316 m² statt 504 m²: Wirtschaftlichkeit nicht neu gerechnet.
- C-35 Tragwerk der Auskragungen offen.
- C-33 Hintere Wohnungen ohne Außenraum.

HINWEISE

Gastronomie-Fläche aus Rest nach Kern (72 m²) und Büros (188 m² brutto): 316 m². Plätze: (Gastraum − Bar) / 2,1 m² + 12 Barhocker.

Wohnungsgrößen netto = Brutto × 0,88 (Annahme).

Fördertechnische Aspekte und neue Renderings sind nicht Teil dieses Blatts.