
1. Obergeschoss – Arbeitsgrundlage OG-2

Grundriss M 1:125 · OG-2 ist vorläufige Arbeitsgrundlage, keine endgültige Entscheidung

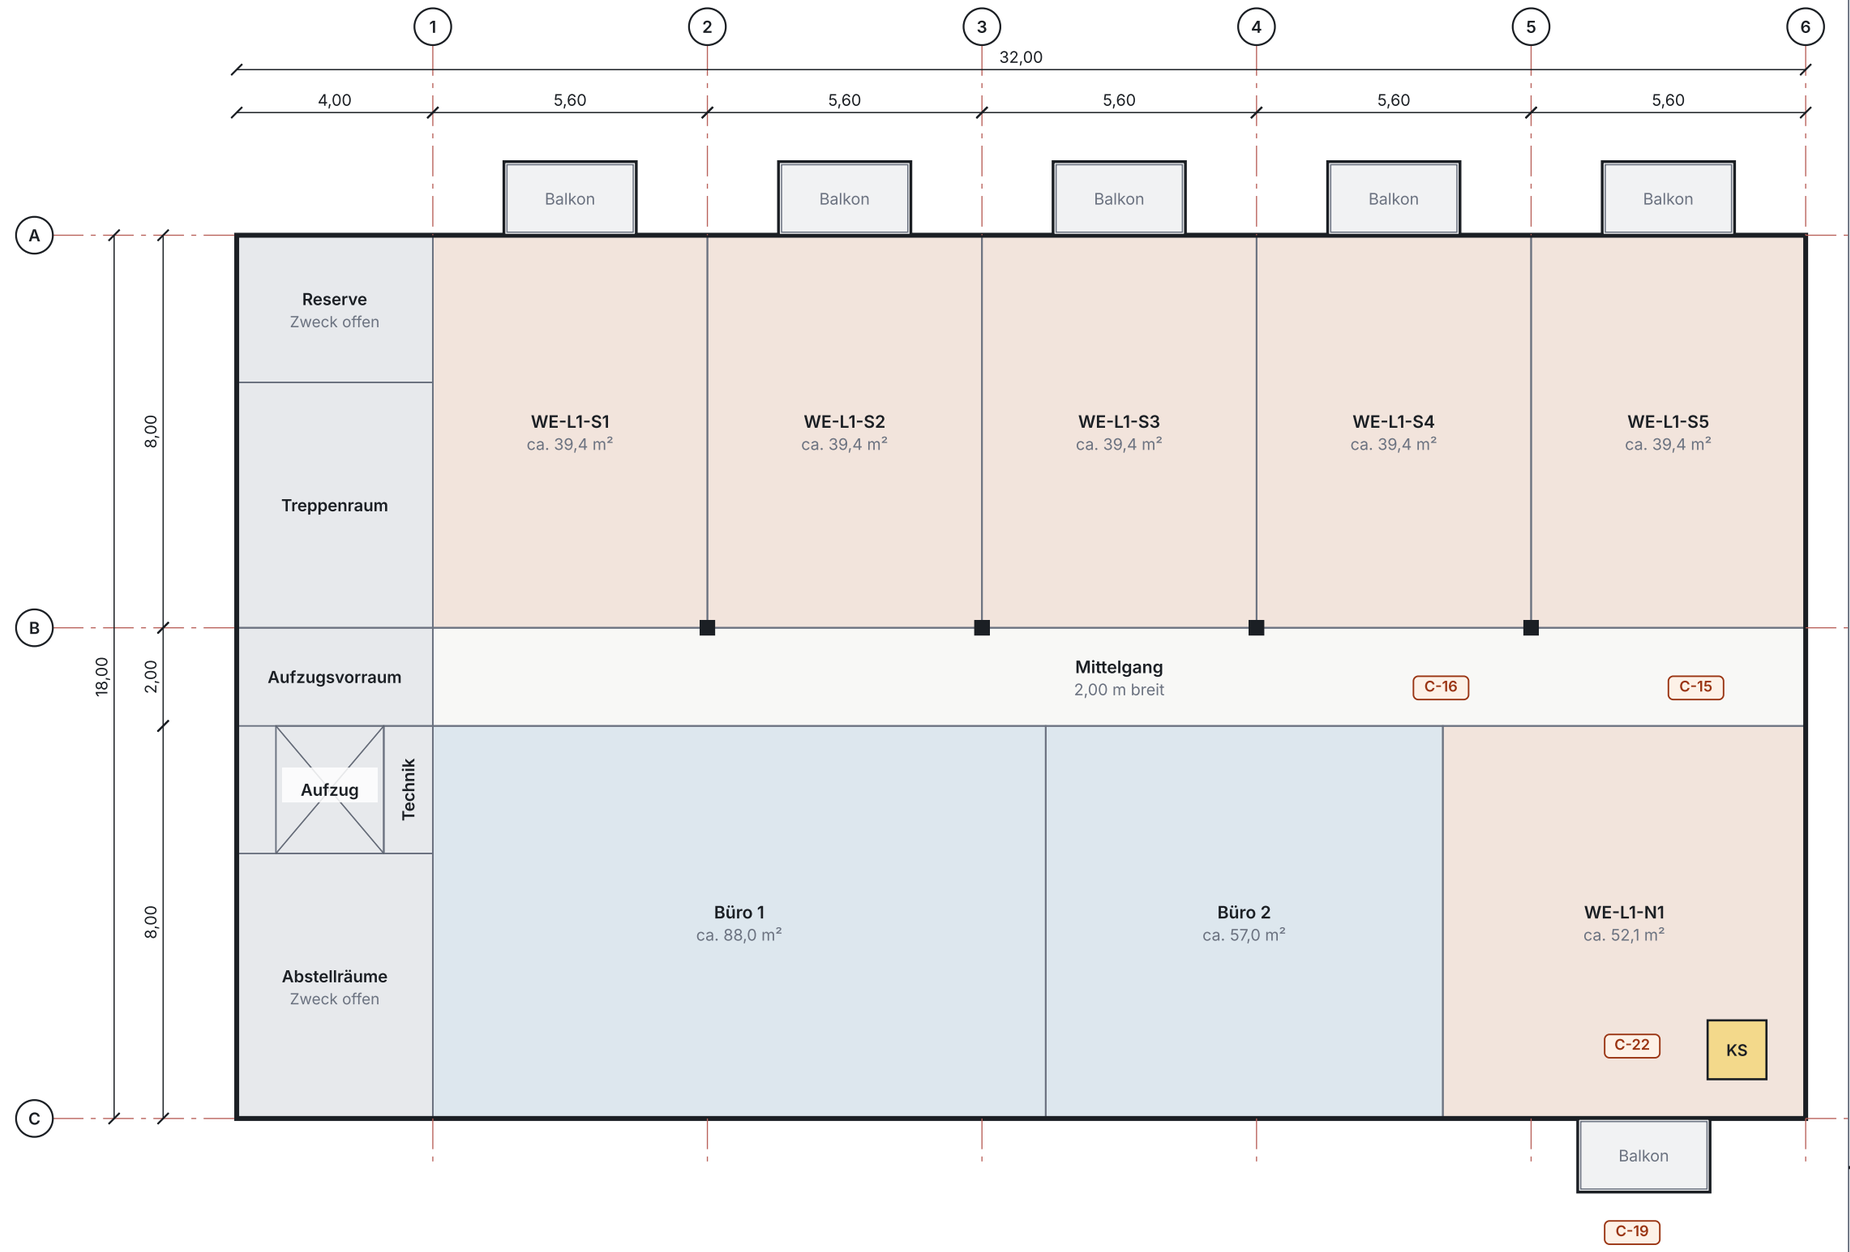

0 5 m

Maßstab 1:125

KENNZAHLEN

Grundfläche Gebäude	**32,00 × 18,00 m = 576 m²**
Wohnungen im 1. OG	**6**
Wohnfläche netto	**ca. 249 m²**
Bürofläche netto	**ca. 145 m²**

LEGENDE

- Wohnung (Wohnfläche netto)
- Büro (Nutzfläche netto)
- Erschließung: Treppenraum, Aufzug, Technik
- Mittelgang
- Balkon (2,70 × 1,50 m)
- Stütze (Annahme, Raster R2)
- KS: Küchenabluft-Schacht
- Rasterachse (vorläufig)

OFFENE PUNKTE (NICHT GELÖST)

- **C-01** Baufenster: Nachweis der 576 m² Grundfläche fehlt.
- **C-15** Rettungswege: Mittelgang ca. 28 m lang, zweiter Rettungsweg offen.
- **C-16** Stützen oder Träger in der Platzfassade nicht nachgewiesen.
- **C-19** Rückseitiger Balkon: Grenzabstand unbekannt.
- **C-22** Küchenabluft-Schacht läuft durch Wohnung WE-L1-N1.
- **C-25** Aufzug: Überfahrt über die Attika offen.

HINWEISE

OG-2: fünf Wohnungen vorn mit je einem Balkon zum Platz (Platzfassade oben), eine Wohnung und zwei Büros hinten.

Flächen netto = Brutto × 0,88 (Annahme).

Fenster, Türen und Wandstärken sind noch nicht festgelegt und daher nicht dargestellt.

Himmelsrichtung unbekannt (C-13). Förderthemen sind nicht Gegenstand dieses Blatts.

Neue Mitte Werlte · Baufeld 3

Bauvorhaben: Restaurant und Bar, Büros, Wohnungen

1. Obergeschoss – Arbeitsgrundlage OG-2

Maßstab 1:125 (A3)

Stand 22.10.2026 · Modell NEUE_MITTE_MASTER_DRAFT_A_003

VORLÄUFIGER ARBEITSSTAND – nicht freigegeben