
Staffelgeschoss – Arbeitsstand S-1

Grundriss M 1:125 · Staffel 0,80 m zurückgesetzt, Geschoss darunter gestrichelt

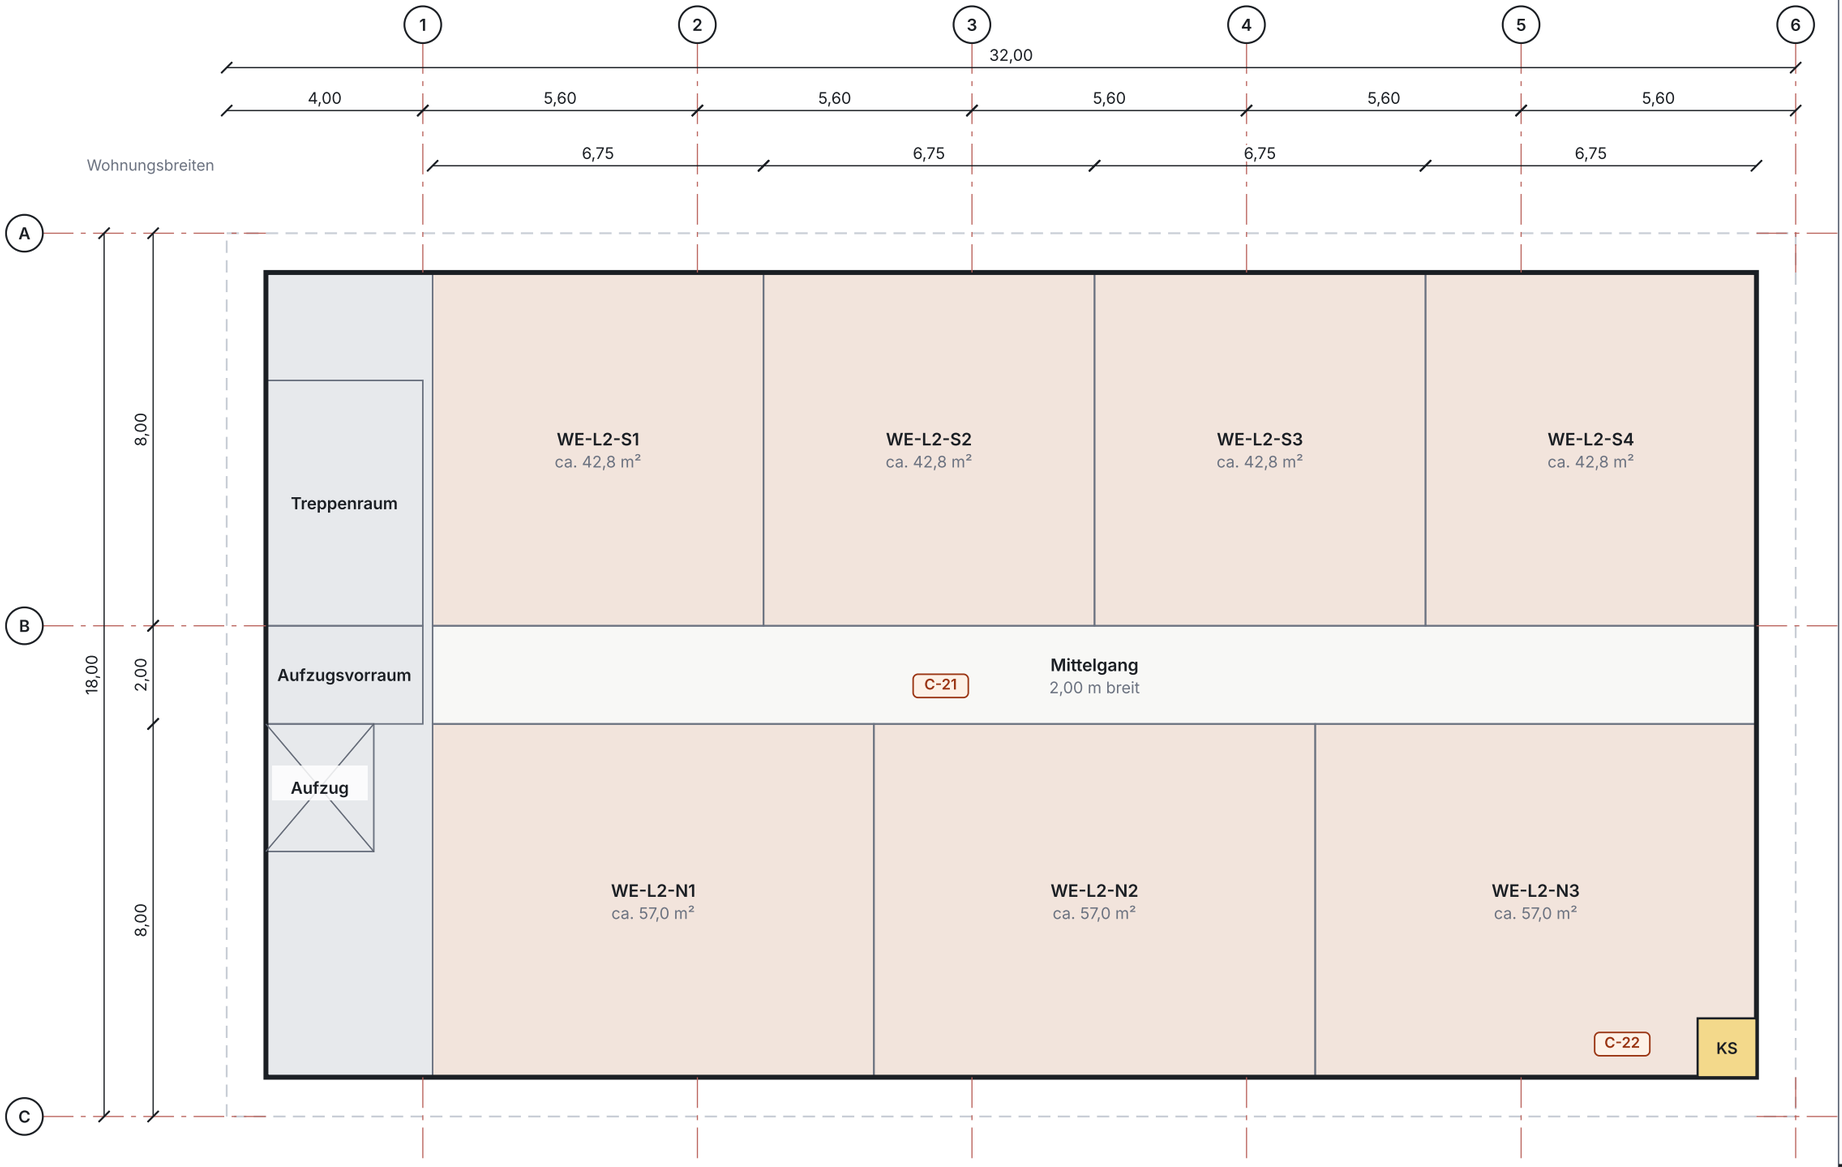

0 5 m

Maßstab 1:125

KENNZAHLEN

Grundfläche Gebäude	**32,00 × 18,00 m = 576 m²**
Wohnungen im Staffelgeschoss	**7**
Wohnfläche netto	**ca. 342 m²**
Staffel gegen Geschoss darunter	**87 %**

LEGENDE

- Wohnung (Wohnfläche netto)
- Büro (Nutzfläche netto)
- Erschließung: Treppenraum, Aufzug, Technik
- Mittelgang
- Stütze (Annahme, Raster R2)
- KS: Küchenabluft-Schacht
- Rasterachse (vorläufig)

OFFENE PUNKTE (NICHT GELÖST)

- **C-02** Staffel gilt voraussichtlich als Vollgeschoss (87 % der Fläche darunter).
- **C-21** Achsen: Entwurf 4, 1. OG 5, Renderings 7 – offen.
- **C-15** Rettungswege und Anleiterung: offen.
- **C-22** Küchenabluft-Schacht läuft durch Wohnung WE-L2-N3.
- **C-25** Aufzug: Überfahrt über die Attika offen.

HINWEISE

Rückversatz 0,80 m umlaufend (Umlauf). Die Wohnungstrennwände vorn liegen nicht auf dem Raster R2.

Flächen netto = Brutto × 0,88 (Annahme).

Fenster, Türen und Wandstärken sind noch nicht festgelegt und daher nicht dargestellt.

Himmelsrichtung unbekannt (C-13). Förderthemen sind nicht Gegenstand dieses Blatts.

Neue Mitte Werlte · Baufeld 3

Bauvorhaben: Restaurant und Bar, Büros, Wohnungen

Staffelgeschoss – Arbeitsstand S-1

Maßstab 1:125 (A3)

Stand 22.10.2026 · Modell NEUE_MITTE_MASTER_DRAFT_A_003

VORLÄUFIGER ARBEITSSTAND – nicht freigegeben