
Erdgeschoss – Restaurant, Bar und Wohnungseingang

Grundriss M 1:125 · Arbeitsstand der Variante A

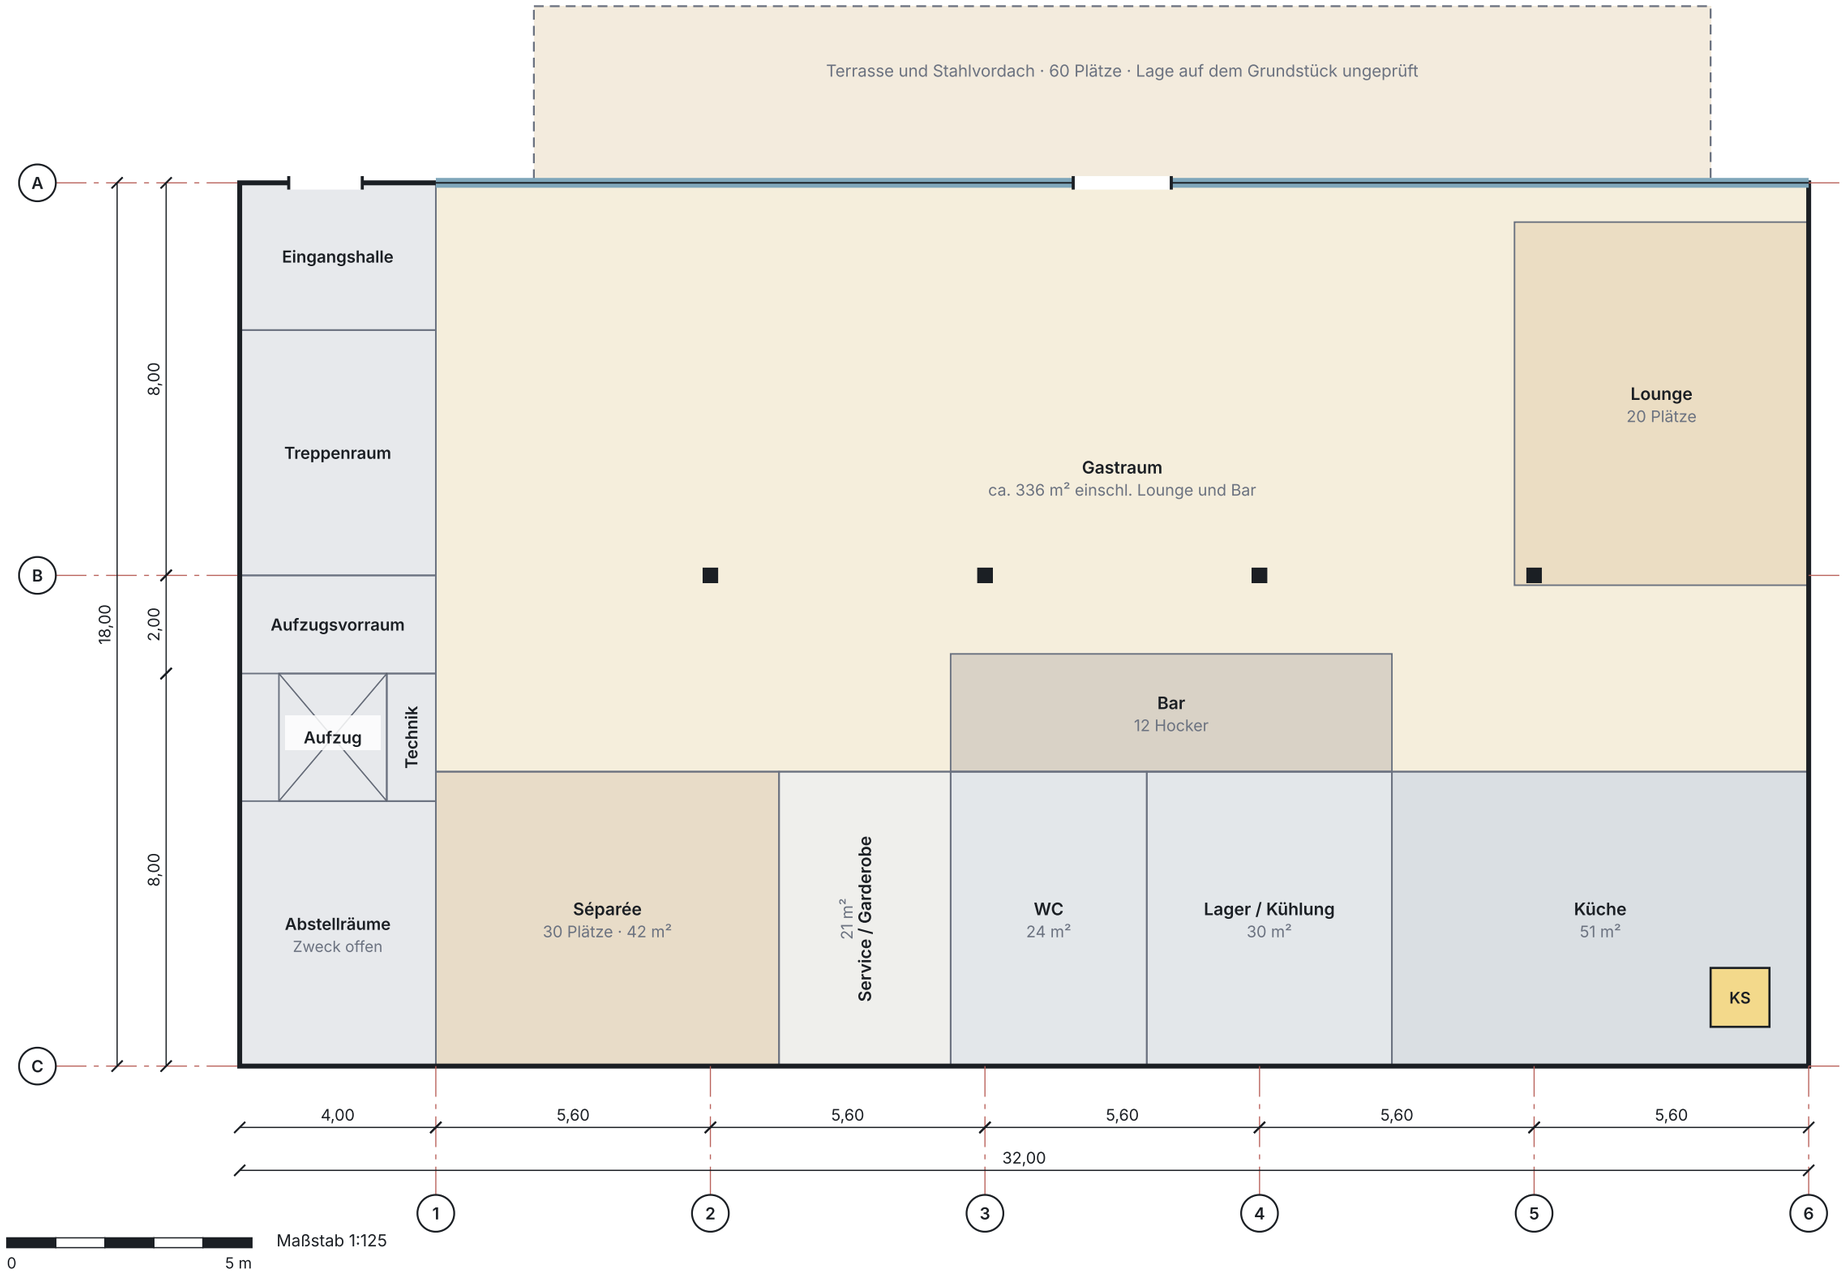

KENNZAHLEN

Grundfläche Gebäude	**32,00 × 18,00 m = 576 m²**
Gastrofläche ohne Lounge und Bar	**504 m² (Ziel 510 m²)**
Innenplätze	**190**
Terrassenplätze	**60**

LEGENDE

- Gastraum
- Lounge, Bar, Séparée
- Küche, Lager, WC, Service
- Erschließung Wohnen: Halle, Treppenraum, Aufzug, Technik
- Glasfront zum Platz (Annahme)
- Terrasse und Vordach
- Stütze (Annahme, Raster R2)
- KS: Küchenabluft-Schacht
- Rasterachse (vorläufig)

OFFENE PUNKTE (NICHT GELÖST)

- **C-01** Baufenster: Nachweis der 576 m² Grundfläche fehlt.
- **C-16** Platzfassade: 28 m Glasfront ohne nachgewiesene Stützen oder Träger.
- **C-18** Stahlvordach liegt unter den Balkonplatten des 1. OG.
- **C-20** Gaststätte mit 190 + 60 Plätzen: Einstufung als Sonderbau offen.
- **C-22** Küchenabluft-Schacht durchläuft darüberliegende Wohnungen.
- **C-13** Platzseite und Himmelsrichtung unbekannt.

HINWEISE

Wohnungseingang am Westende (Eingangshalle). Zugang Restaurant über die Doppeltür in Feldmitte (x 17–19 m).

Terrasse 24,0 × 3,6 m: Lage auf dem Grundstück ungeprüft.

Flächen netto = Brutto × 0,88 (Annahme).

Fenster, Türen und Wandstärken sind noch nicht festgelegt und daher nicht dargestellt.

Himmelsrichtung unbekannt (C-13). Förderthemen sind nicht Gegenstand dieses Blatts.

Neue Mitte Werlte · Baufeld 3

Bauvorhaben: Restaurant und Bar, Büros, Wohnungen

Erdgeschoss – Restaurant, Bar und Wohnungseingang

Maßstab 1:125 (A3)

Stand 22.10.2026 · Modell NEUE_MITTE_MASTER_DRAFT_A_003

VORLÄUFIGER ARBEITSSTAND – nicht freigegeben