
Schnitt A–A bei x = 18,00 m – Arbeitsstand OG-2

Schnitt M 1:100 · Platzfassade links, Rückseite rechts · Schnittebene schneidet Wohnung WE-L1-S3, Büro 2, Bar und WC

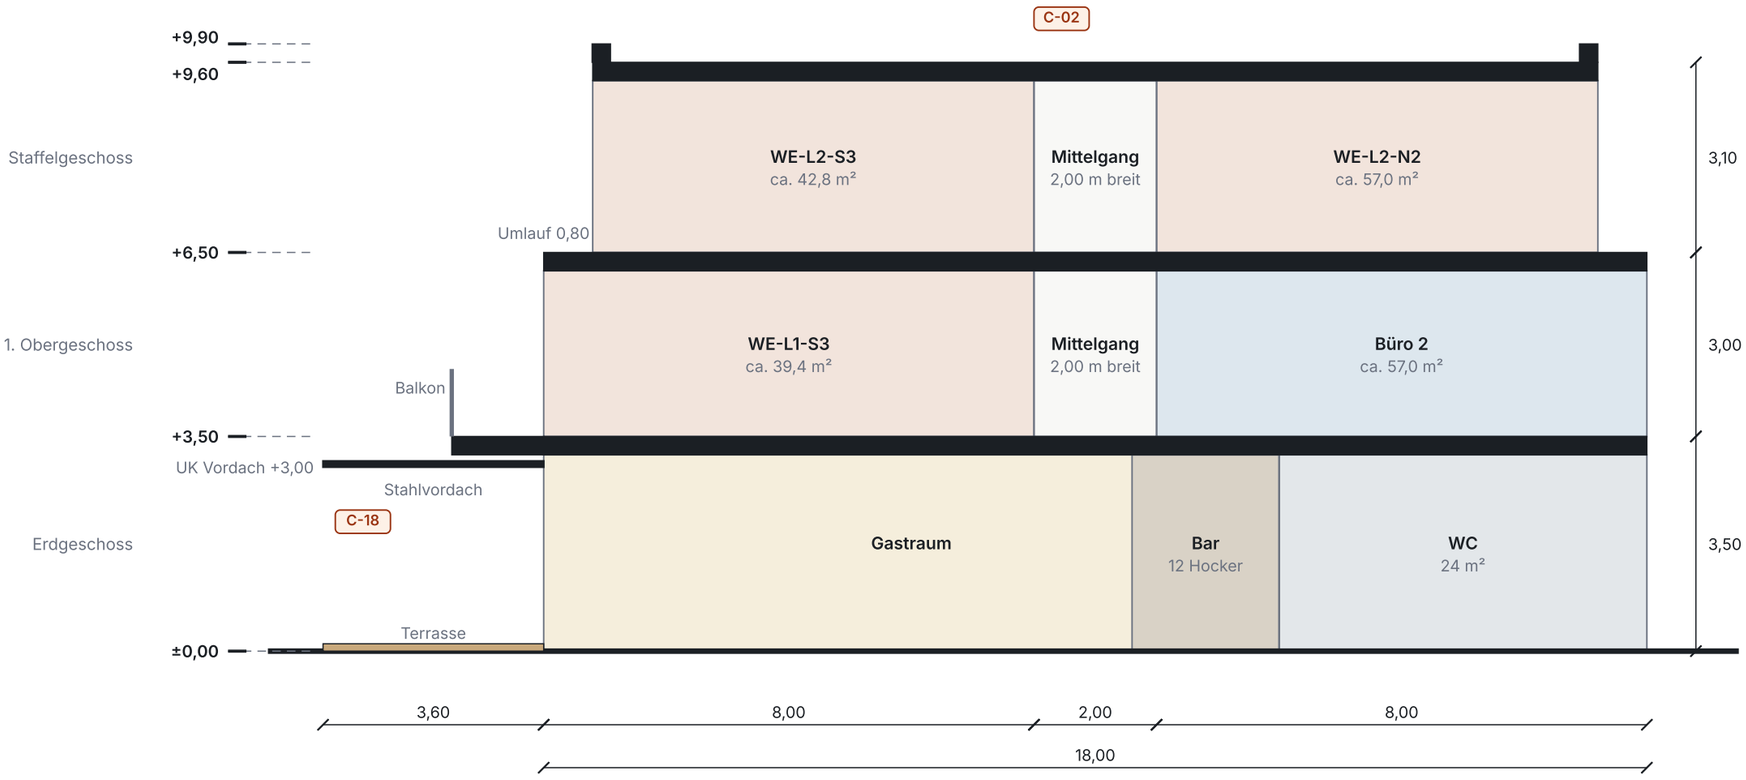

0 5 m Maßstab 1:100

KENNZAHLEN

Geschosshöhen	**3,50 / 3,00 / 3,10 m**
Höhe Attika	**9,90 m**
Deckendicke	**0,30 m (Annahme)**

LEGENDE

- Wohnung
- Büro
- Gastraum, Bar (Gastronomie)
- WC und Nebenräume
- Mittelgang
- Geschossdecke, Dicke 0,30 m
- Gelände

OFFENE PUNKTE (NICHT GELÖST)

- C-18 Balkonplatte (Unterseite +3,20) und Vordach (Unterseite +3,00) überlappen.
- C-02 Staffelgeschoss gilt voraussichtlich als Vollgeschoss.
- C-19 Rückseitiger Balkon liegt nicht in dieser Schnittebene.
- C-22 Küchenabluft-Schacht liegt nicht in dieser Schnittebene.

HINWEISE

Wände sind nur als Raumgrenzen dargestellt, Wandstärken sind noch nicht festgelegt.

Die Schnittebene liegt auf Balkon 3 (Mitte). Terrasse und Vordach nach Annahme (Lage ungeprüft).

Flächen netto = Brutto × 0,88 (Annahme).

Himmelsrichtung unbekannt (C-13). Förderthemen sind nicht Gegenstand dieses Blatts.

Neue Mitte Werlte · Baufeld 3

Bauvorhaben: Restaurant und Bar, Büros, Wohnungen

Schnitt A–A bei x = 18,00 m – Arbeitsstand OG-2

Maßstab 1:100 (A3)

Stand 22.10.2026 · Modell NEUE_MITTE_MASTER_DRAFT_A_003

VORLÄUFIGER ARBEITSSTAND – nicht freigegeben