
Wohnung WE-L1-S (1. OG, vorn) – Nutzbarkeitsprobe

Grundriss M 1:45 · Möblierungsprobe zur Prüfung der Eigenständigkeit, keine Optimierung der Wohnungszahl

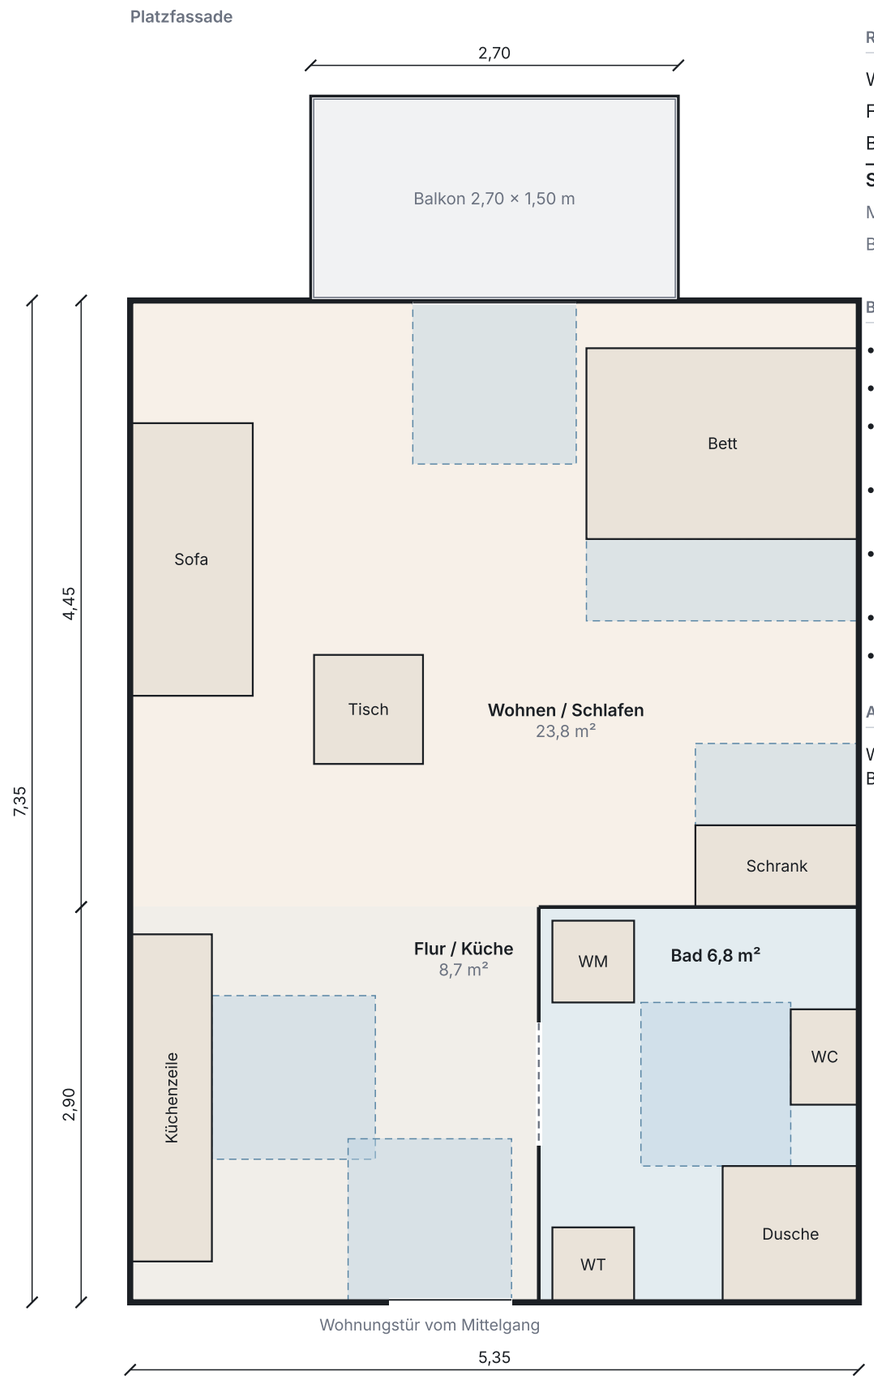

RAUMPROGRAMM (INNENMASS)

Wohnen / Schlafen (vorn, an der Platzfassade)	**23,8 m²**
Flur / Küche (innenliegend)	**8,7 m²**
Bad (innenliegend)	**6,8 m²**
Summe Innenmaß 5,35 × 7,35 m	**39,3 m²**
Modellwert Wohnfläche netto (Brutto 44,8 m² × 0,88)	39,4 m²
Balkon (nicht in der Wohnfläche)	4,05 m²

BEFUND DER NUTZBARKEITSPROBE (KEIN RECHTSURTEIL)

- Eigenständig nutzbar als Studio-Wohnung für 1 Person, mit Einschränkung für 2 Personen.
- Alle Möbel und Bewegungsflächen der Probe passen ohne Überlappung in den Grundriss.
- Ein separates Schlafzimmer ist nicht möglich: zwei Räume an der Fassade wären nur ca. 2,6 m breit.
- Einseitige Belichtung über eine Fassadenachse, keine Querlüftung. Küche und Bad liegen innen und brauchen mechanische Lüftung.
- Balkon und Schlafplatz liegen über der Gastro-Terrasse: Schall und Betriebszeiten sind nicht geprüft (C-26).
- Kein Abstellraum in der Wohnung; Abstellräume nur im Kern, Zweck offen.
- Als rollstuhlgerechte Wohnung kommt dieser Typ voraussichtlich nicht in Frage (C-27).

ANNAHMEN

Wandstärken: Fassade 0,45 m, Wohnungstrennwand 0,25 m, Flurwand 0,20 m. Möbelmaße und Bewegungsflächen sind übliche Planungswerte, keine Rechtsvorgaben.

KENNZAHLEN

Wohnungen dieses Typs	**WE-L1-S1 bis S5**
Wohnfläche netto (Modell)	**ca. 39,4 m²**
Innenmaß	**5,35 × 7,35 m**

LEGENDE

- Möbel (WT Waschtisch, WM Waschmaschine)
- freizuhaltende Bewegungsfläche, 1,20 × 1,20 m bzw. 0,60 m seitlich
- Balkon
- Wand (Annahme)
- Schiebetür Bad

OFFENE PUNKTE (NICHT GELÖST)

- C-26 Einseitig belichtet, Lage über Gastro-Terrasse, kein Abstellraum.
- C-27 Rollstuhlgerechte Wohnung: Kandidaten sind nur die größeren Typen.
- C-07 Wohnungsgrundrisse sind noch keine Planung, nur Probe.

HINWEISE

Fenster- und Türmaße sind nicht festgelegt; Balkontür 1,20 m und Wohnungstür 0,90 m sind Annahmen der Probe.

Himmelsrichtung unbekannt (C-13). Förderthemen sind nicht Gegenstand dieses Blatts.

Neue Mitte Werlte · Baufeld 3

Bauvorhaben: Restaurant und Bar, Büros, Wohnungen

Wohnung WE-L1-S – Nutzbarkeitsprobe

Maßstab 1:45 (A3)

Stand 22.10.2026 · Modell NEUE_MITTE_MASTER_DRAFT_A_003

VORLÄUFIGER ARBEITSSTAND – nicht freigegeben