
1. Obergeschoss – Arbeitsgrundlage OG-2

Grundriss M 1:125 · OG-2 ist vorläufige Arbeitsgrundlage, keine endgültige Entscheidung

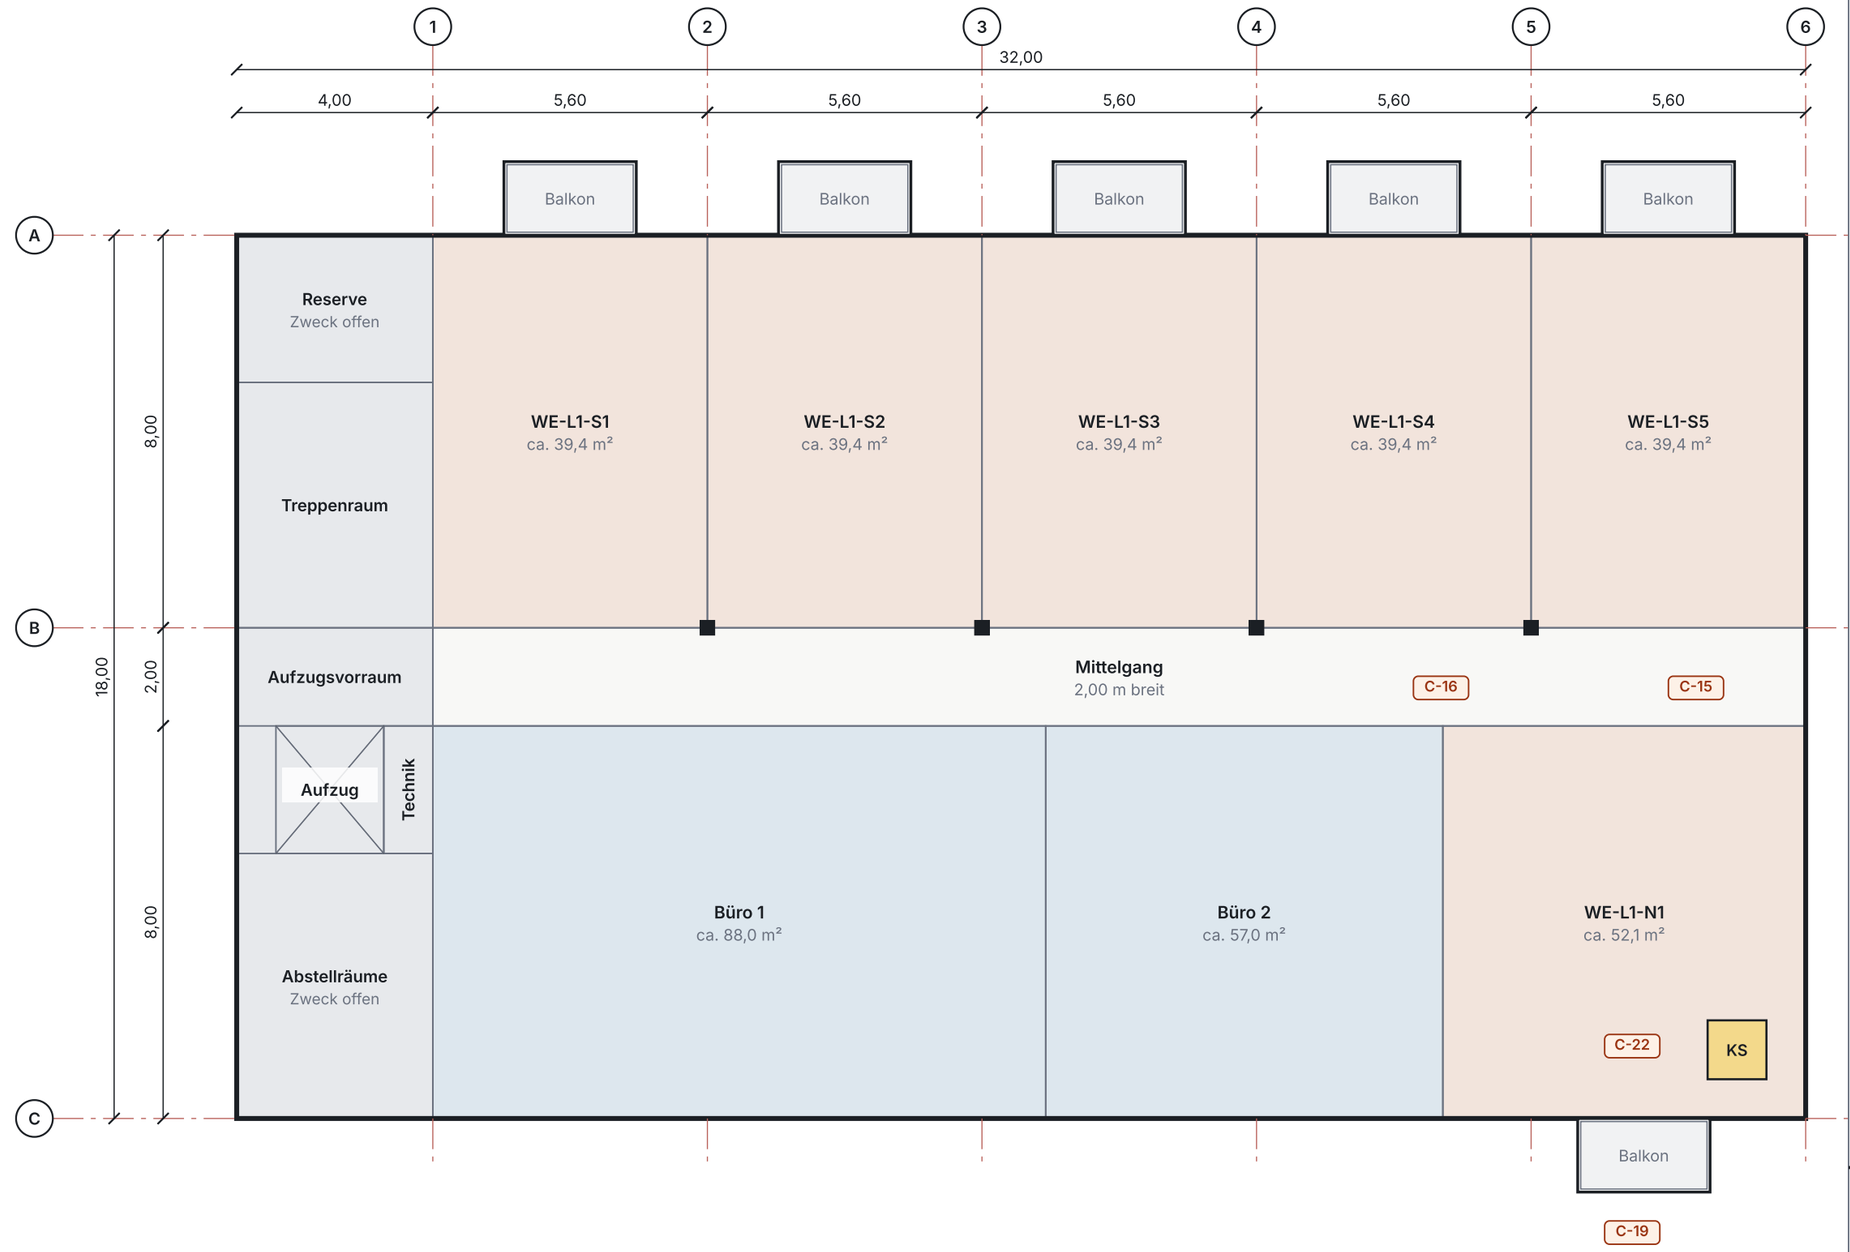

0 5 m

Maßstab 1:125

KENNZAHLEN

Grundfläche Gebäude	**32,00 × 18,00 m = 576 m²**
Wohnungen im 1. OG	**6**
Wohnfläche netto	**ca. 249 m²**
Bürofläche netto	**ca. 145 m²**

LEGENDE

- Wohnung (Wohnfläche netto)
- Büro (Nutzfläche netto)
- Erschließung: Treppenraum, Aufzug, Technik
- Mittelgang
- Balkon (2,70 × 1,50 m)
- Stütze (Annahme, Raster R2)
- KS: Küchenabluft-Schacht
- Rasterachse (vorläufig)

OFFENE PUNKTE (NICHT GELÖST)

- **C-01** Baufenster: Nachweis der 576 m² Grundfläche fehlt.
- **C-15** Rettungswege: Mittelgang ca. 28 m lang, zweiter Rettungsweg offen.
- **C-16** Stützen oder Träger in der Platzfassade nicht nachgewiesen.
- **C-19** Rückseitiger Balkon: Grenzabstand unbekannt.
- **C-22** Küchenabluft-Schacht läuft durch Wohnung WE-L1-N1.
- **C-25** Aufzug: Überfahrt über die Attika offen.

HINWEISE

OG-2: fünf Wohnungen vorn mit je einem Balkon zum Platz (Platzfassade oben), eine Wohnung und zwei Büros hinten.

Flächen netto = Brutto × 0,88 (Annahme).

Fenster, Türen und Wandstärken sind noch nicht festgelegt und daher nicht dargestellt.

Himmelsrichtung unbekannt (C-13). Förderthemen sind nicht Gegenstand dieses Blatts.

Neue Mitte Werlte · Baufeld 3

Bauvorhaben: Restaurant und Bar, Büros, Wohnungen

1. Obergeschoss – Arbeitsgrundlage OG-2


Maßstab 1:125 (A3)

Stand 22.10.2026 · Modell NEUE_MITTE_MASTER_DRAFT_A_003

VORLÄUFIGER ARBEITSSTAND – nicht freigegeben

Staffelgeschoss – Arbeitsstand S-1

Grundriss M 1:125 · Staffel 0,80 m zurückgesetzt, Geschoss darunter gestrichelt

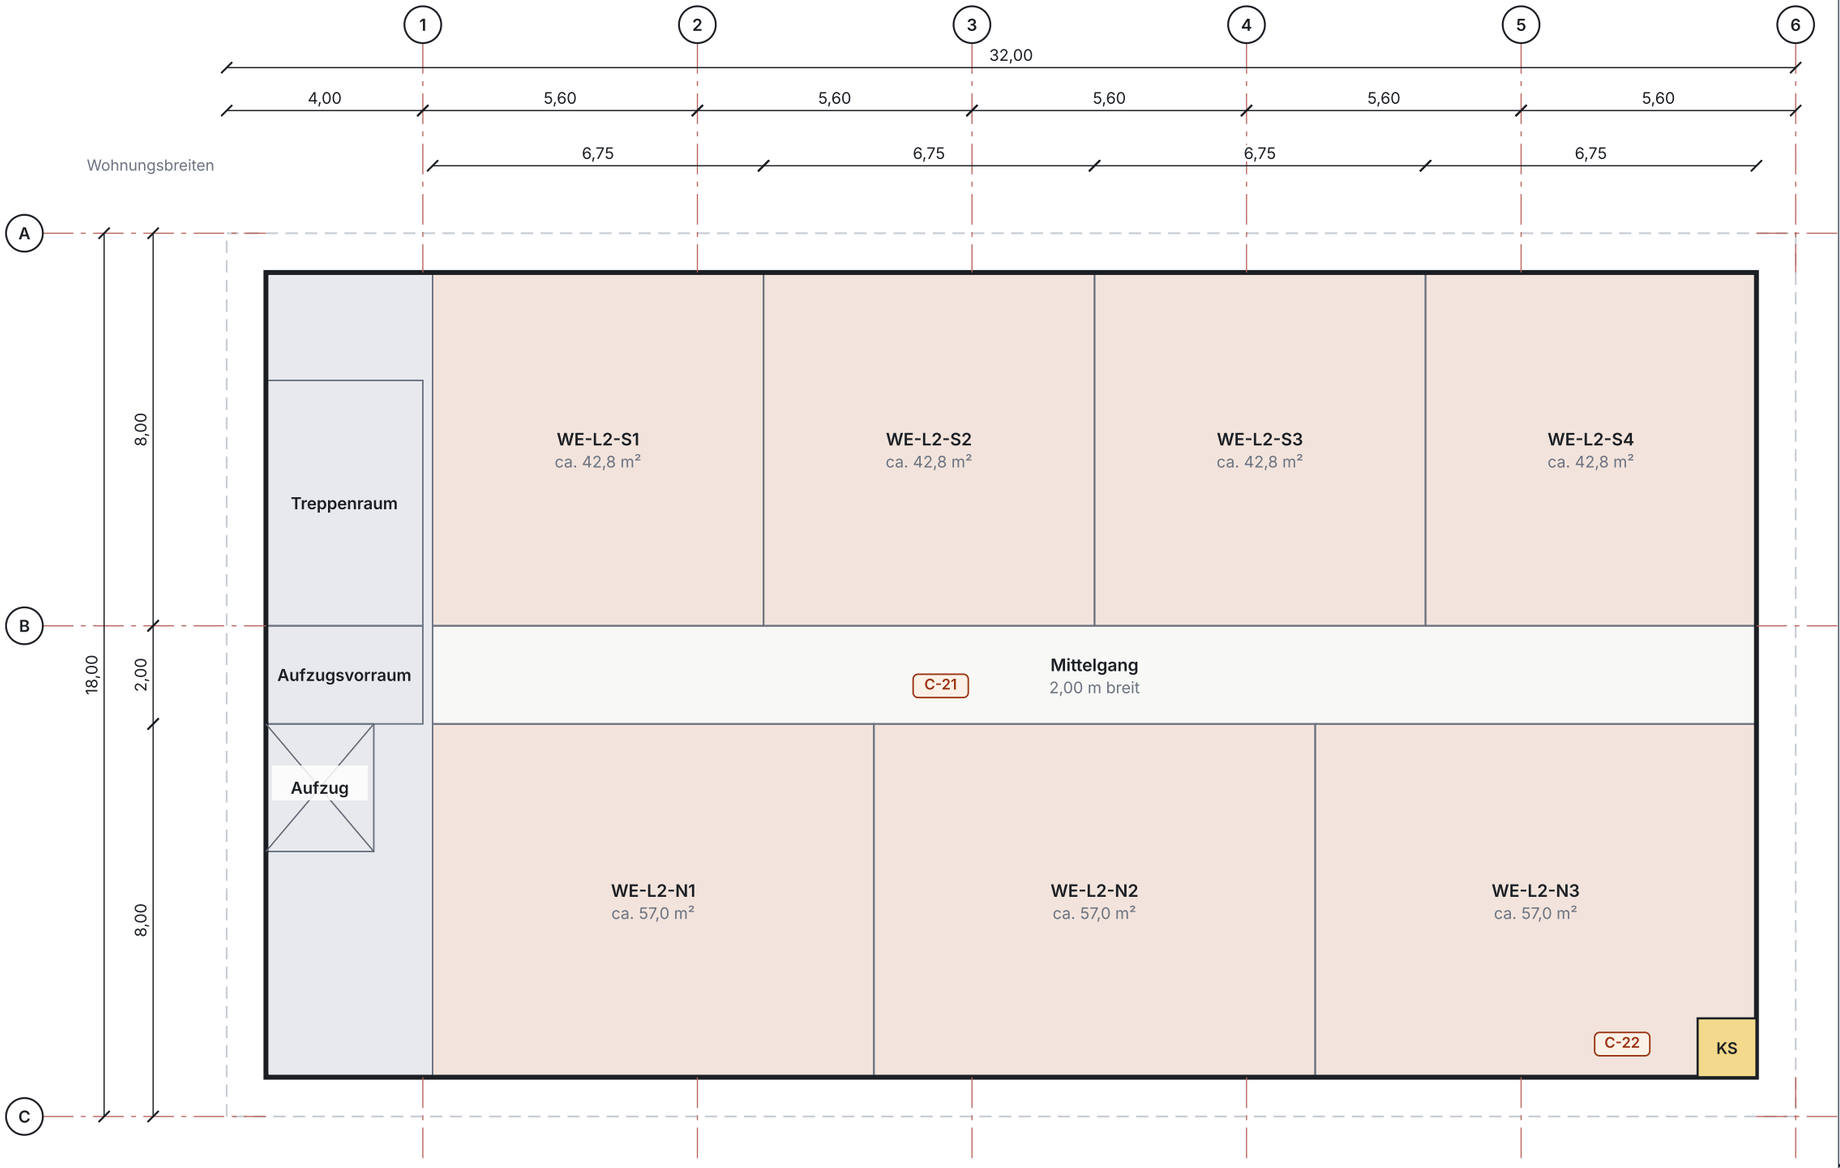

0 5 m

Maßstab 1:125

KENNZAHLEN

Grundfläche Gebäude	**32,00 × 18,00 m = 576 m²**
Wohnungen im Staffelgeschoss	**7**
Wohnfläche netto	**ca. 342 m²**
Staffel gegen Geschoss darunter	**87 %**

LEGENDE

- Wohnung (Wohnfläche netto)
- Büro (Nutzfläche netto)
- Erschließung: Treppenraum, Aufzug, Technik
- Mittelgang
- Stütze (Annahme, Raster R2)
- KS: Küchenabluft-Schacht
- Rasterachse (vorläufig)

OFFENE PUNKTE (NICHT GELÖST)

- **C-02** Staffel gilt voraussichtlich als Vollgeschoss (87 % der Fläche darunter).
- **C-21** Achsen: Entwurf 4, 1. OG 5, Renderings 7 – offen.
- **C-15** Rettungswege und Anleiterung: offen.
- **C-22** Küchenabluft-Schacht läuft durch Wohnung WE-L2-N3.
- **C-25** Aufzug: Überfahrt über die Attika offen.

HINWEISE

Rückversatz 0,80 m umlaufend (Umlauf). Die Wohnungstrennwände vorn liegen nicht auf dem Raster R2.

Flächen netto = Brutto × 0,88 (Annahme).

Fenster, Türen und Wandstärken sind noch nicht festgelegt und daher nicht dargestellt.

Himmelsrichtung unbekannt (C-13). Förderthemen sind nicht Gegenstand dieses Blatts.

Neue Mitte Werlte · Baufeld 3

Bauvorhaben: Restaurant und Bar, Büros, Wohnungen

Staffelgeschoss – Arbeitsstand S-1


Maßstab 1:125 (A3)

Stand 22.10.2026 · Modell NEUE_MITTE_MASTER_DRAFT_A_003

VORLÄUFIGER ARBEITSSTAND – nicht freigegeben

Erdgeschoss – Restaurant, Bar und Wohnungseingang

Grundriss M 1:125 · Arbeitsstand der Variante A

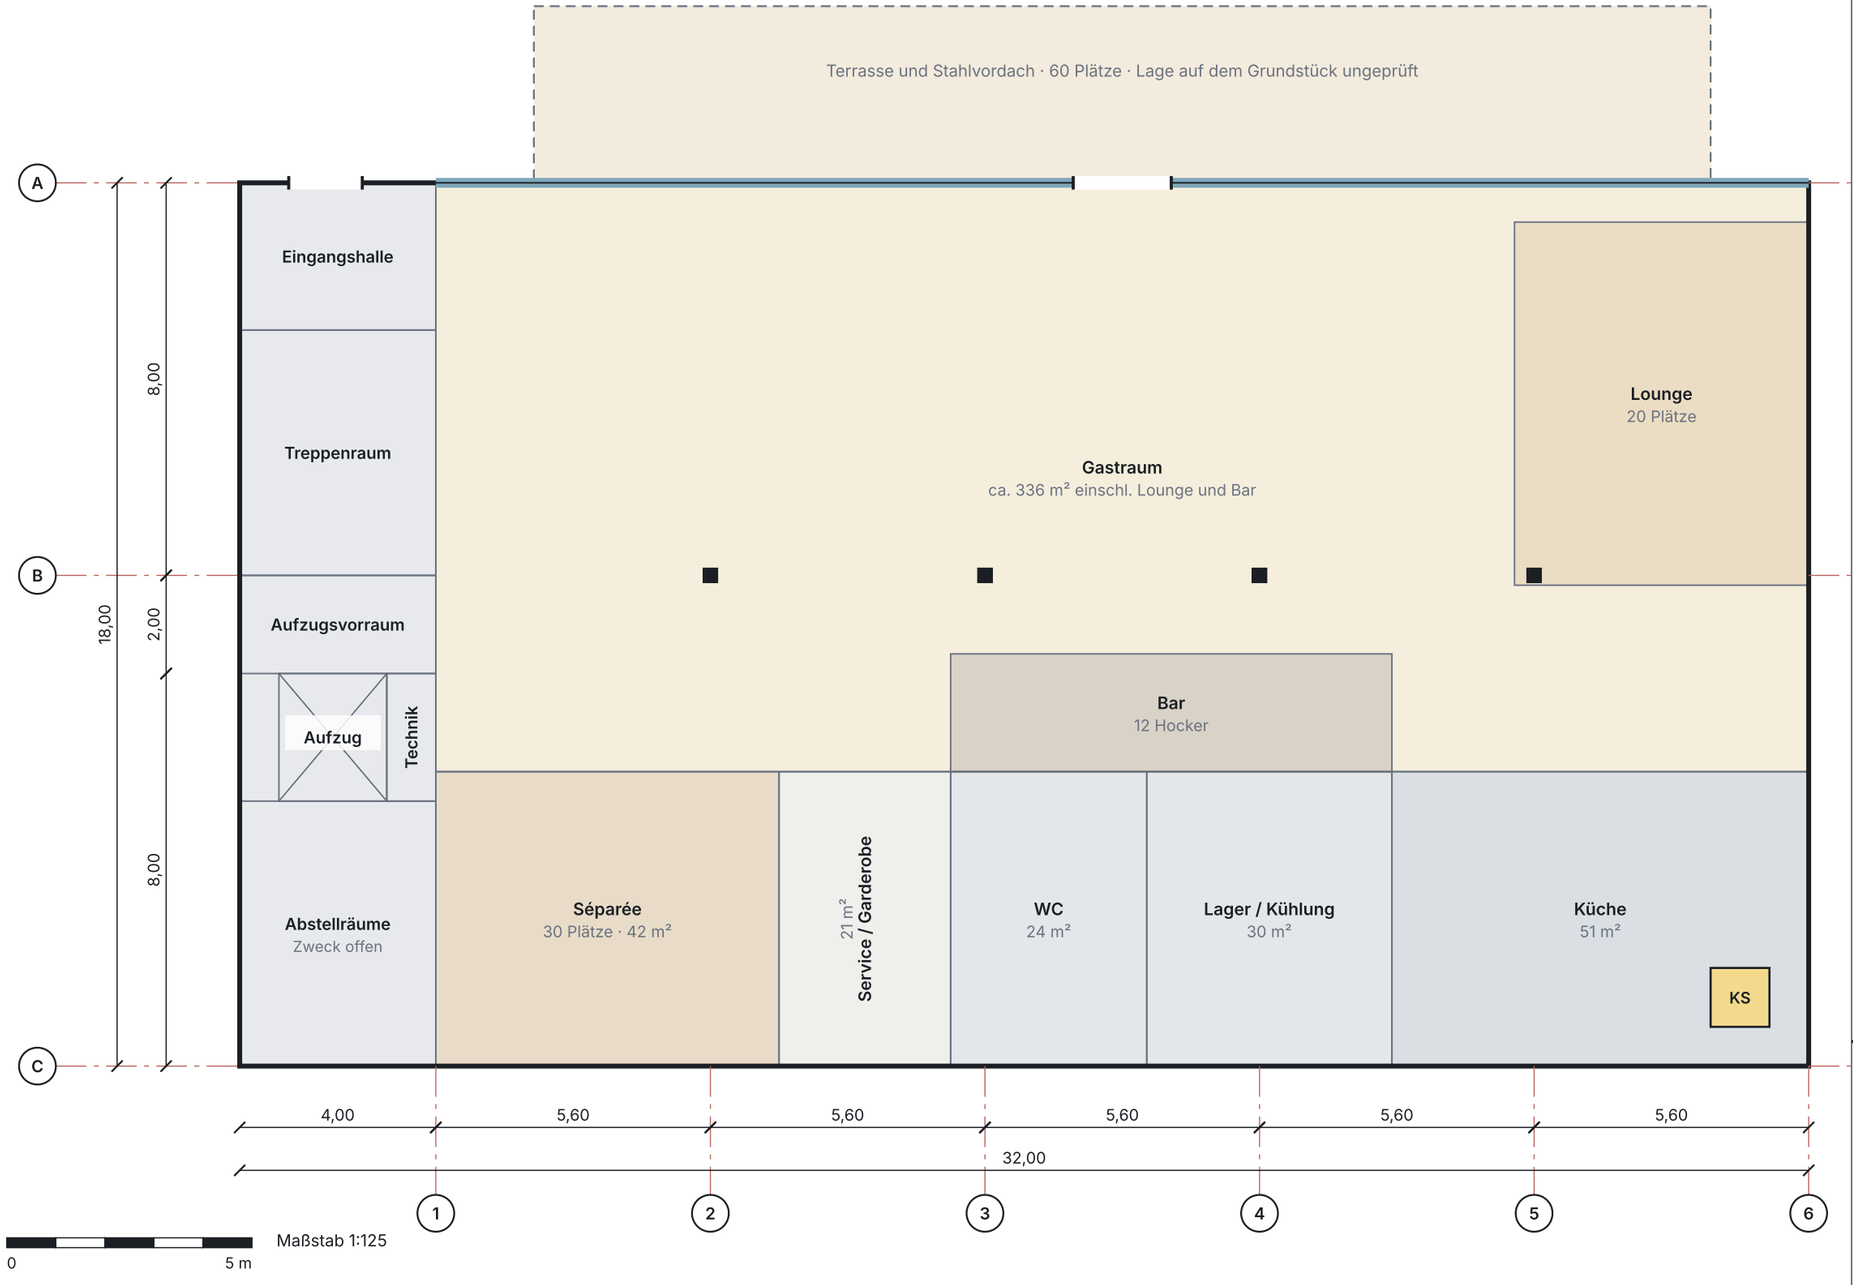

KENNZAHLEN

Grundfläche Gebäude	**32,00 × 18,00 m = 576 m²**
Gastrofläche ohne Lounge und Bar	**504 m² (Ziel 510 m²)**
Innenplätze	**190**
Terrassenplätze	**60**

LEGENDE

- Gastraum
- Lounge, Bar, Séparée
- Küche, Lager, WC, Service
- Erschließung Wohnen: Halle, Treppenraum, Aufzug, Technik
- Glasfront zum Platz (Annahme)
- Terrasse und Vordach
- Stütze (Annahme, Raster R2)
- KS: Küchenabluft-Schacht
- Rasterachse (vorläufig)

OFFENE PUNKTE (NICHT GELÖST)

- **C-01** Baufenster: Nachweis der 576 m² Grundfläche fehlt.
- **C-16** Platzfassade: 28 m Glasfront ohne nachgewiesene Stützen oder Träger.
- **C-18** Stahlvordach liegt unter den Balkonplatten des 1. OG.
- **C-20** Gaststätte mit 190 + 60 Plätzen: Einstufung als Sonderbau offen.
- **C-22** Küchenabluft-Schacht durchläuft darüberliegende Wohnungen.
- **C-13** Platzseite und Himmelsrichtung unbekannt.

HINWEISE

Wohnungseingang am Westende (Eingangshalle). Zugang Restaurant über die Doppeltür in Feldmitte (x 17–19 m).

Terrasse 24,0 × 3,6 m: Lage auf dem Grundstück ungeprüft.

Flächen netto = Brutto × 0,88 (Annahme).

Fenster, Türen und Wandstärken sind noch nicht festgelegt und daher nicht dargestellt.

Himmelsrichtung unbekannt (C-13). Förderthemen sind nicht Gegenstand dieses Blatts.

Neue Mitte Werlte · Baufeld 3

Bauvorhaben: Restaurant und Bar, Büros, Wohnungen

Erdgeschoss – Restaurant, Bar und Wohnungseingang


Maßstab 1:125 (A3)

Stand 22.10.2026 · Modell NEUE_MITTE_MASTER_DRAFT_A_003

VORLÄUFIGER ARBEITSSTAND – nicht freigegeben

Ansicht Platzfassade – Arbeitsstand OG-2

Ansicht M 1:150 · Fensterlage schematisch, Fenstermaße sind noch nicht festgelegt

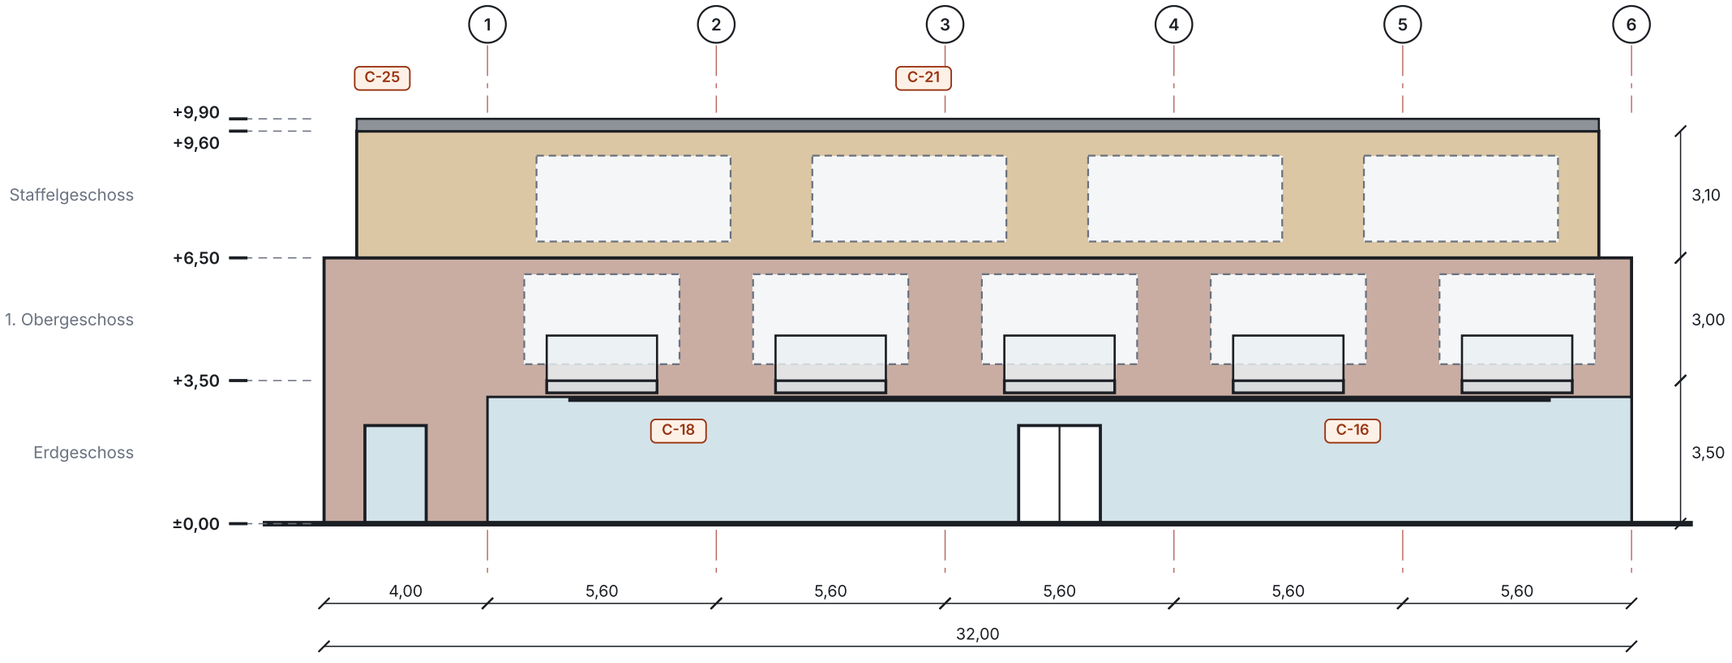

Maßstab 1:150

0 5 m

KENNZAHLEN

Gebäudebreite	**32,00 m**
Höhe Attika	**9,90 m**
Traufhöhe nach B-Plan	**6,50 m**

LEGENDE

- Klinker (dunkelrotbraun, hier aufgehellt dargestellt)
- Betonbalkonplatte
- Milchglas-Brüstung, 1,10 m
- Glasfront und Türen im Erdgeschoss
- Lärchenholz Staffelgeschoss
- Fensterlage schematisch (Maße offen)
- Stahlvordach (Annahme, Unterseite +3,00)

OFFENE PUNKTE (NICHT GELÖST)

- C-16 Stützen oder Träger in der 28 m langen Glasfront nicht nachgewiesen.
- C-18 Stahlvordach liegt unter den Balkonplatten.
- C-21 Staffel: Entwurf 4 Achsen, 1. OG 5, Renderings 7.
- C-25 Aufzug: Überfahrt über die Attika offen.
- C-03 Höhenmessregel der Stadt unbestätigt.

HINWEISE

Platzfassade mit fünf Balkonen im 1. OG. Staffelgeschoss 0,80 m zurückgesetzt, hier nicht sichtbar.

Flächen netto = Brutto × 0,88 (Annahme).

Himmelsrichtung unbekannt (C-13). Förderthemen sind nicht Gegenstand dieses Blatts.

Neue Mitte Werlte · Baufeld 3

Bauvorhaben: Restaurant und Bar, Büros, Wohnungen

Ansicht Platzfassade – Arbeitsstand OG-2


Maßstab 1:150 (A3)

Stand 22.10.2026 · Modell NEUE_MITTE_MASTER_DRAFT_A_003

VORLÄUFIGER ARBEITSSTAND – nicht freigegeben

Schnitt A–A bei x = 18,00 m – Arbeitsstand OG-2

Schnitt M 1:100 · Platzfassade links, Rückseite rechts · Schnittebene schneidet Wohnung WE-L1-S3, Büro 2, Bar und WC

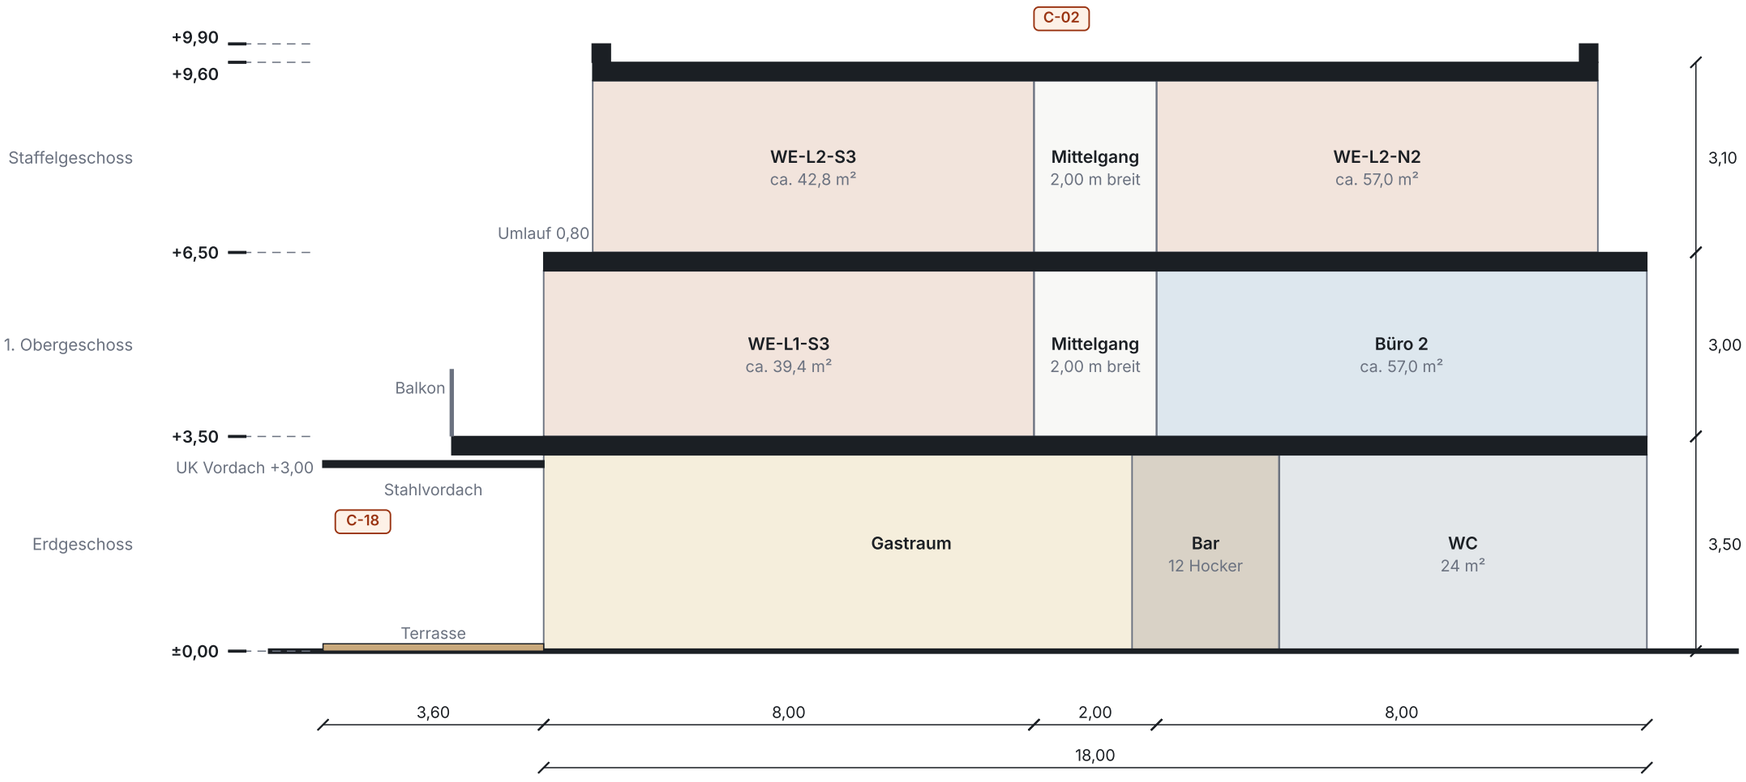

0 5 m Maßstab 1:100

KENNZAHLEN

Geschosshöhen	**3,50 / 3,00 / 3,10 m**
Höhe Attika	**9,90 m**
Deckendicke	**0,30 m (Annahme)**

LEGENDE

- Wohnung
- Büro
- Gastraum, Bar (Gastronomie)
- WC und Nebenräume
- Mittelgang
- Geschossdecke, Dicke 0,30 m
- Gelände

OFFENE PUNKTE (NICHT GELÖST)

- C-18 Balkonplatte (Unterseite +3,20) und Vordach (Unterseite +3,00) überlappen.
- C-02 Staffelgeschoss gilt voraussichtlich als Vollgeschoss.
- C-19 Rückseitiger Balkon liegt nicht in dieser Schnittebene.
- C-22 Küchenabluft-Schacht liegt nicht in dieser Schnittebene.

HINWEISE

Wände sind nur als Raumgrenzen dargestellt, Wandstärken sind noch nicht festgelegt.

Die Schnittebene liegt auf Balkon 3 (Mitte). Terrasse und Vordach nach Annahme (Lage ungeprüft).

Flächen netto = Brutto × 0,88 (Annahme).

Himmelsrichtung unbekannt (C-13). Förderthemen sind nicht Gegenstand dieses Blatts.

Neue Mitte Werlte · Baufeld 3

Bauvorhaben: Restaurant und Bar, Büros, Wohnungen

Schnitt A–A bei x = 18,00 m – Arbeitsstand OG-2


Maßstab 1:100 (A3)

Stand 22.10.2026 · Modell NEUE_MITTE_MASTER_DRAFT_A_003

VORLÄUFIGER ARBEITSSTAND – nicht freigegeben

Wohnung WE-L1-S (1. OG, vorn) – Nutzbarkeitsprobe

Grundriss M 1:45 · Möblierungsprobe zur Prüfung der Eigenständigkeit, keine Optimierung der Wohnungszahl

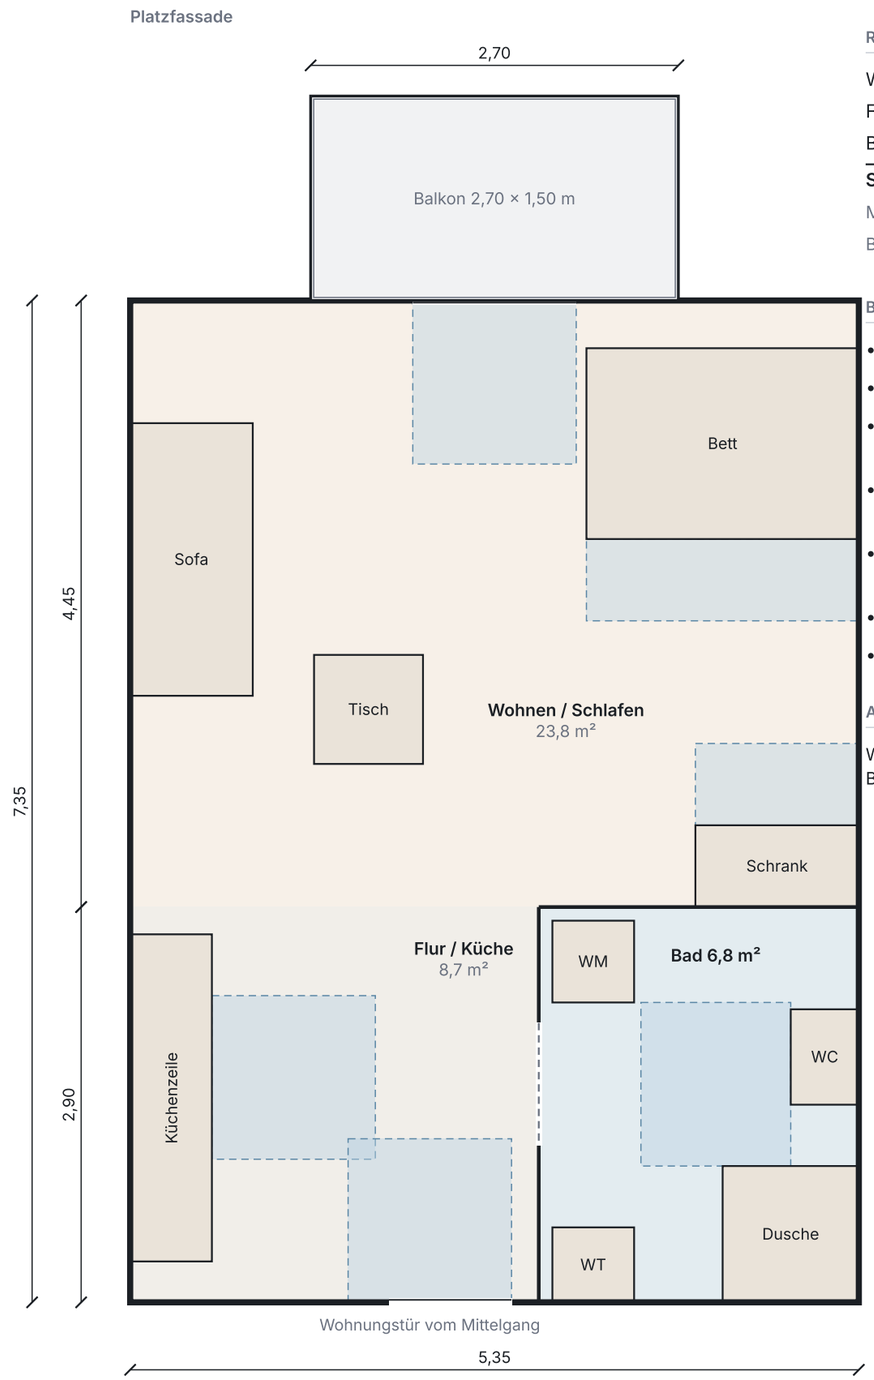

RAUMPROGRAMM (INNENMASS)

Wohnen / Schlafen (vorn, an der Platzfassade)	**23,8 m²**
Flur / Küche (innenliegend)	**8,7 m²**
Bad (innenliegend)	**6,8 m²**
Summe Innenmaß 5,35 × 7,35 m	**39,3 m²**
Modellwert Wohnfläche netto (Brutto 44,8 m² × 0,88)	39,4 m²
Balkon (nicht in der Wohnfläche)	4,05 m²

BEFUND DER NUTZBARKEITSPROBE (KEIN RECHTSURTEIL)

- Eigenständig nutzbar als Studio-Wohnung für 1 Person, mit Einschränkung für 2 Personen.
- Alle Möbel und Bewegungsflächen der Probe passen ohne Überlappung in den Grundriss.
- Ein separates Schlafzimmer ist nicht möglich: zwei Räume an der Fassade wären nur ca. 2,6 m breit.
- Einseitige Belichtung über eine Fassadenachse, keine Querlüftung. Küche und Bad liegen innen und brauchen mechanische Lüftung.
- Balkon und Schlafplatz liegen über der Gastro-Terrasse: Schall und Betriebszeiten sind nicht geprüft (C-26).
- Kein Abstellraum in der Wohnung; Abstellräume nur im Kern, Zweck offen.
- Als rollstuhlgerechte Wohnung kommt dieser Typ voraussichtlich nicht in Frage (C-27).

ANNAHMEN

Wandstärken: Fassade 0,45 m, Wohnungstrennwand 0,25 m, Flurwand 0,20 m. Möbelmaße und Bewegungsflächen sind übliche Planungswerte, keine Rechtsvorgaben.

KENNZAHLEN

Wohnungen dieses Typs	**WE-L1-S1 bis S5**
Wohnfläche netto (Modell)	**ca. 39,4 m²**
Innenmaß	**5,35 × 7,35 m**

LEGENDE

- Möbel (WT Waschtisch, WM Waschmaschine)
- freizuhaltende Bewegungsfläche, 1,20 × 1,20 m bzw. 0,60 m seitlich
- Balkon
- Wand (Annahme)
- Schiebetür Bad

OFFENE PUNKTE (NICHT GELÖST)

- C-26 Einseitig belichtet, Lage über Gastro-Terrasse, kein Abstellraum.
- C-27 Rollstuhlgerechte Wohnung: Kandidaten sind nur die größeren Typen.
- C-07 Wohnungsgrundrisse sind noch keine Planung, nur Probe.

HINWEISE

Fenster- und Türmaße sind nicht festgelegt; Balkontür 1,20 m und Wohnungstür 0,90 m sind Annahmen der Probe.

Himmelsrichtung unbekannt (C-13). Förderthemen sind nicht Gegenstand dieses Blatts.

Neue Mitte Werlte · Baufeld 3

Bauvorhaben: Restaurant und Bar, Büros, Wohnungen

Wohnung WE-L1-S – Nutzbarkeitsprobe

Maßstab 1:45 (A3)

Stand 22.10.2026 · Modell NEUE_MITTE_MASTER_DRAFT_A_003

VORLÄUFIGER ARBEITSSTAND – nicht freigegeben