
Variante A – Obergeschosse moderat vergrößert (1,50 m)

Grundrisse und Schnitt M 1:250 · HYPOTHETISCH: Grundstücksform, Baufenster und Rechtsfragen sind nicht belegt


Erdgeschoss 32 × 18 m mit Stellplätzen

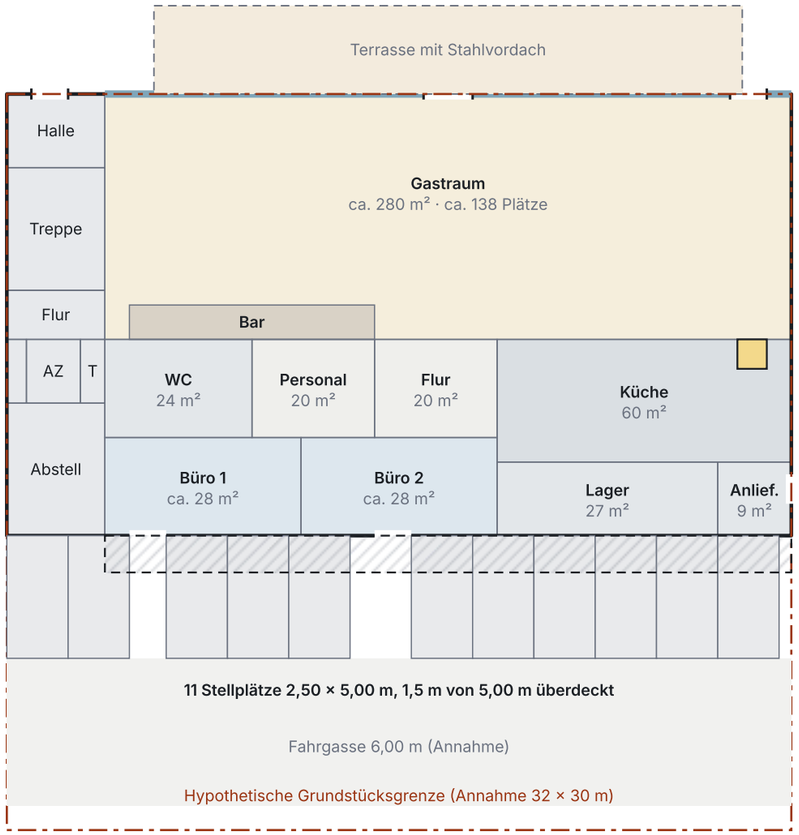


1. Obergeschoss (nur Wohnungen)



Schnitt bei x = 17,00 m

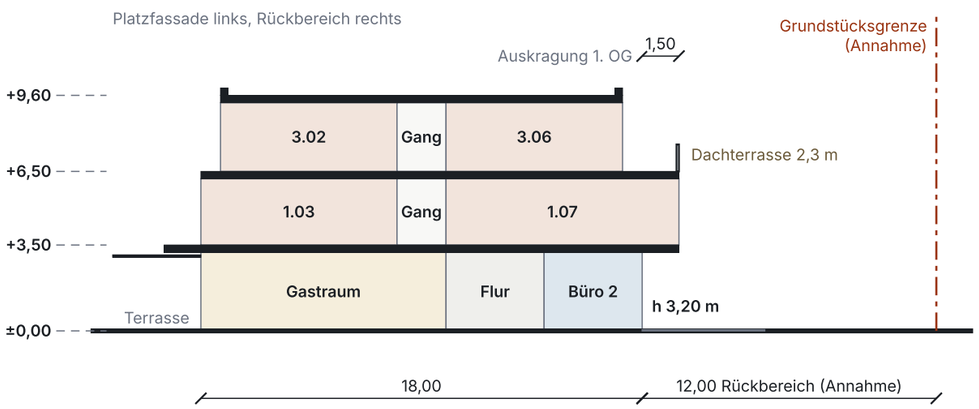

3. Geschoss, Staffel (nur Wohnungen)

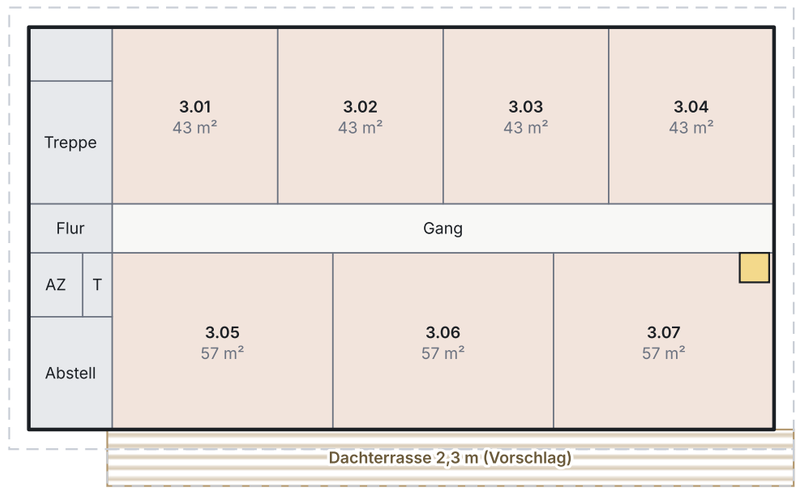

KENNZAHLEN

Außenmaß EG / 1. OG / 3. Geschoss	**32×18 / 32×19,5 / 30,4×16,4 m**
Auskragung 1. OG / Überstand Staffel	**1,50 / 0,00 m**
Gastronomie brutto, Innenplätze	**ca. 440 m², ca. 138**
Büros hinten, netto	**ca. 56 m²**
Wohnungen, Wohnfläche netto	**16, ca. 773 m²**
Stellplätze, überdeckt	**11, 1,5 von 5,0 m Tiefe**

LEGENDE

- Wohnung, Nummer nach Geschoss (1.xx, 3.xx), Wohnfläche netto
- Büro (EG, hinten)
- Gastraum und Bar
- Küche, Lager, WC, Personal, Anlieferung (Anlief.)
- Kern: Halle, Treppe, Flur, Abstell (AZ Aufzug, T Technik)
- Auskragung über Stellplätzen (hypothetisch)
- Dachterrasse auf dem 1. OG (Vorschlag)
- Küchenabluft-Schacht, alle Geschosse

OFFENE PUNKTE (NICHT GELÖST)

- **C-30** Baufenster, GRZ und Zählung von Auskragungen unbekannt; Projektion 618 m² gegen theoretisch 576 m²: nicht nachweisbar zulässig.
- **C-28** Stellplatzbedarf 61 laut Excel, hier 11 nachweisbar (Annahme).
- **C-29** Grundstückszuschnitt, Zufahrt und Anlieferung unbekannt (hier 32 × 30 m angenommen).
- **C-37** Büros 56 m² statt 165 m²: Mieteinnahmen und Gastro-Pacht nicht neu gerechnet.
- **C-35** Tragwerk der Auskragung.

HINWEISE

Erdgeschoss in allen Varianten gleich. Der Anbau ist abgestuft: 1. OG weiter ausgekragt als die Staffel, dazwischen eine Dachterrasse.

Flächen netto = Brutto × 0,88 (Annahme). Fenster, Türen und Wandstärken sind nicht festgelegt. Keine Variante ist festgelegt.

Neue Mitte Werlte · Baufeld 3

Bauvorhaben: Restaurant und Bar, Büros, Wohnungen

Variante A – Grundrisse und Schnitt

Maßstab 1:250 (A3)


Stand 22.10.2026 · Modell NEUE_MITTE_MASTER_DRAFT_A_003

VORLÄUFIGER ARBEITSSTAND – nicht freigegeben


Ansichten Variante A – Obergeschosse moderat vergrößert (1,50 m)

Schematische Ansichten M 1:250 · Fenster- und Türlage schematisch, Maße nicht definiert · Material und Farbe unverändert

Ansicht Platzseite

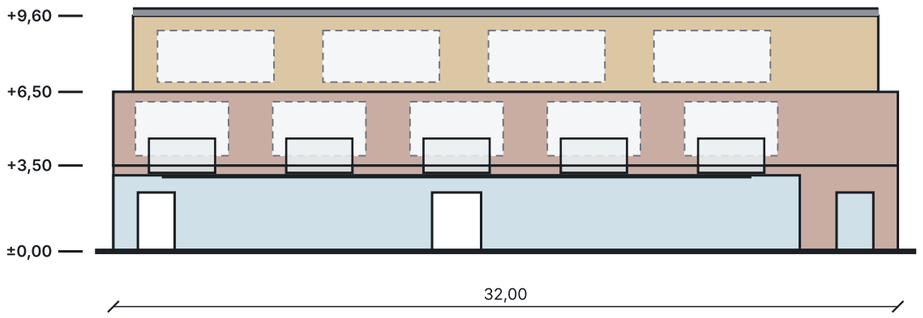


Ansicht Rückseite

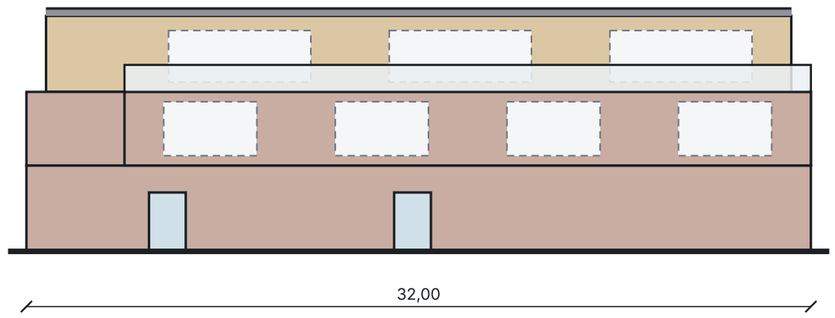


Höhen: ±0,00 Oberkante Erdgeschoss, +3,50 1. OG, +6,50 Traufe nach B-Plan und Staffel, +9,60 Staffeldecke, +9,90 Attika

Seitenansicht Kernseite (x = 0)

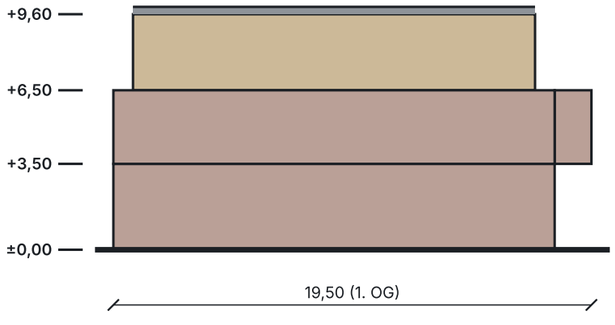

Seitenansicht Ostseite (x = 32)

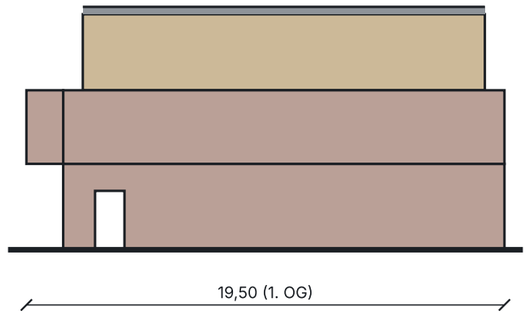

Kernseite: Platzfassade links, Rückseite rechts. Ostseite: Platzfassade rechts, Rückseite links. Himmelsrichtung unbekannt (C-13).

KENNZAHLEN

Gebäudetiefe Erdgeschoss	**18,00 m**
Tiefe 1. OG / Staffel	**19,50 / 16,40 m**
Höhe Attika	**9,90 m**
Dachterrasse hinten	**2,3 m tief**

LEGENDE

- Klinker, dunkelrotbraun (hier aufgehellt)
- Lärchenholz im Staffelgeschoss
- Betonbalkonplatte
- Milchglas-Brüstung, 1,10 m
- Glas und Türen
- Fensterlage schematisch (Maße offen)

OFFENE PUNKTE (NICHT GELÖST)

- **C-13** Himmelsrichtung und Platzseite unbekannt; Seiten sind nach dem Kern benannt.
- **C-19** Rückfassade, Seitenfassaden und Dachterrasse sind nicht Teil des eingefrorenen Designs.
- **C-30** Auskragung und Staffelung: Baufenster, GRZ und Abstände unbekannt.
- **C-35** Tragwerk der Auskragung.
- **C-22** Abluftführung über Dach (Austritt) ist nicht dargestellt.

HINWEISE

Der Anbau ist abgestuft: 1. OG weiter ausgekragt als die Staffel, dazwischen eine Dachterrasse. Die Rückseite folgt dem Material der Platzfassade (Klinker, Lärchenholz).

Die Seitenfassaden zeigen die Stufung von Erdgeschoss, 1. OG und Staffel.

Die bestehende Platzfassade (dunkler Klinker, Holz, fünf Balkone) bleibt die Grundlage.

Neue Mitte Werlte · Baufeld 3

Bauvorhaben: Restaurant und Bar, Büros, Wohnungen

Ansichten Variante A

Maßstab 1:250 (A3)


Stand 22.10.2026 · Modell NEUE_MITTE_MASTER_DRAFT_A_003

VORLÄUFIGER ARBEITSSTAND – nicht freigegeben


Variante B – nach hinten erweitert und abgestuft (3,00 m / 1,50 m)

Grundrisse und Schnitt M 1:250 · HYPOTHETISCH: Grundstücksform, Baufenster und Rechtsfragen sind nicht belegt


Erdgeschoss 32 × 18 m mit Stellplätzen

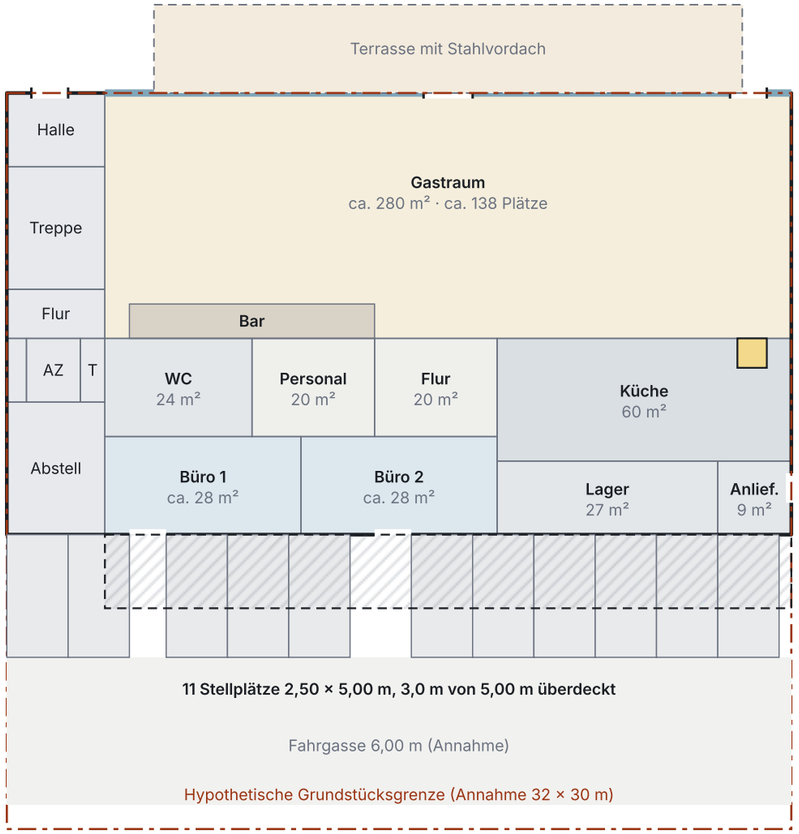


1. Obergeschoss (nur Wohnungen)

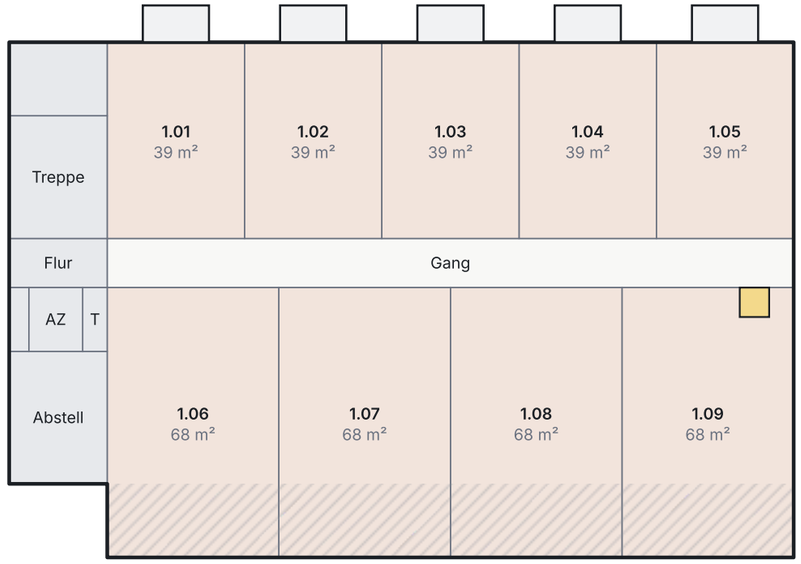

Schnitt bei x = 17,00 m

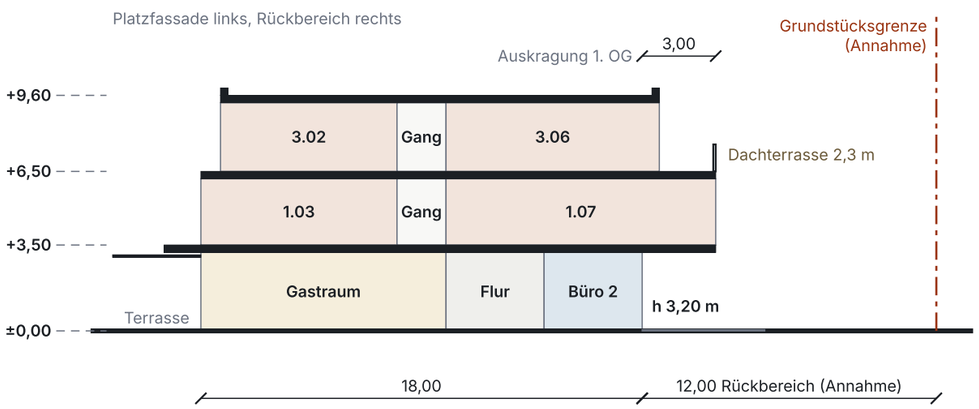

3. Geschoss, Staffel (nur Wohnungen)

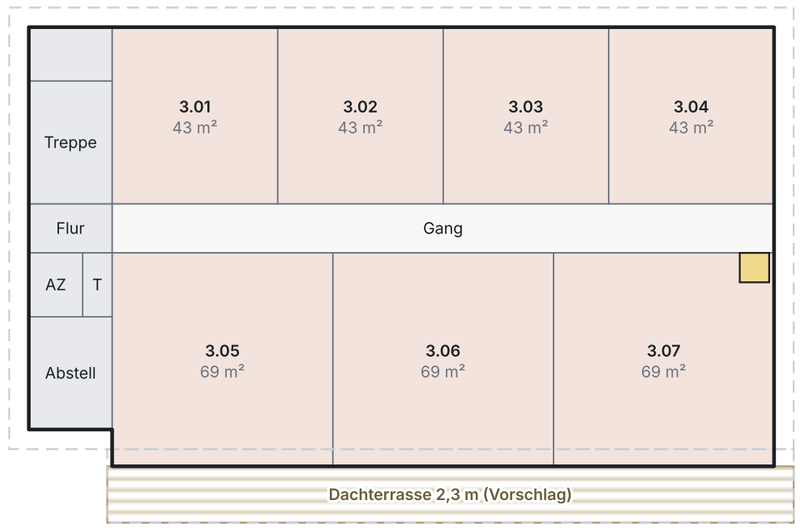

KENNZAHLEN

Außenmaß EG / 1. OG / 3. Geschoss	**32×18 / 32×21,0 / 30,4×17,9 m**
Auskragung 1. OG / Überstand Staffel	**3,00 / 1,50 m**
Gastronomie brutto, Innenplätze	**ca. 440 m², ca. 138**
Büros hinten, netto	**ca. 56 m²**
Wohnungen, Wohnfläche netto	**16, ca. 846 m²**
Stellplätze, überdeckt	**11, 3,0 von 5,0 m Tiefe**

LEGENDE

- Wohnung, Nummer nach Geschoss (1.xx, 3.xx), Wohnfläche netto
- Büro (EG, hinten)
- Gastraum und Bar
- Küche, Lager, WC, Personal, Anlieferung (Anlief.)
- Kern: Halle, Treppe, Flur, Abstell (AZ Aufzug, T Technik)
- Auskragung über Stellplätzen (hypothetisch)
- Dachterrasse auf dem 1. OG (Vorschlag)
- Küchenabluft-Schacht, alle Geschosse

OFFENE PUNKTE (NICHT GELÖST)

- **C-30** Baufenster, GRZ und Zählung von Auskragungen unbekannt; Projektion 660 m² gegen theoretisch 576 m²: nicht nachweisbar zulässig.
- **C-28** Stellplatzbedarf 61 laut Excel, hier 11 nachweisbar (Annahme).
- **C-29** Grundstückszuschnitt, Zufahrt und Anlieferung unbekannt (hier 32 × 30 m angenommen).
- **C-37** Büros 56 m² statt 165 m²: Mieteinnahmen und Gastro-Pacht nicht neu gerechnet.
- **C-35** Tragwerk der Auskragung.

HINWEISE

Erdgeschoss in allen Varianten gleich. Der Anbau ist abgestuft: 1. OG weiter ausgekragt als die Staffel, dazwischen eine Dachterrasse.

Flächen netto = Brutto × 0,88 (Annahme). Fenster, Türen und Wandstärken sind nicht festgelegt. Keine Variante ist festgelegt.

Neue Mitte Werlte · Baufeld 3

Bauvorhaben: Restaurant und Bar, Büros, Wohnungen

Variante B – Grundrisse und Schnitt

Maßstab 1:250 (A3)


Stand 22.10.2026 · Modell NEUE_MITTE_MASTER_DRAFT_A_003

VORLÄUFIGER ARBEITSSTAND – nicht freigegeben


Ansichten Variante B – nach hinten erweitert und abgestuft (3,00 m / 1,50 m)

Schematische Ansichten M 1:250 · Fenster- und Türlage schematisch, Maße nicht definiert · Material und Farbe unverändert

Ansicht Platzseite

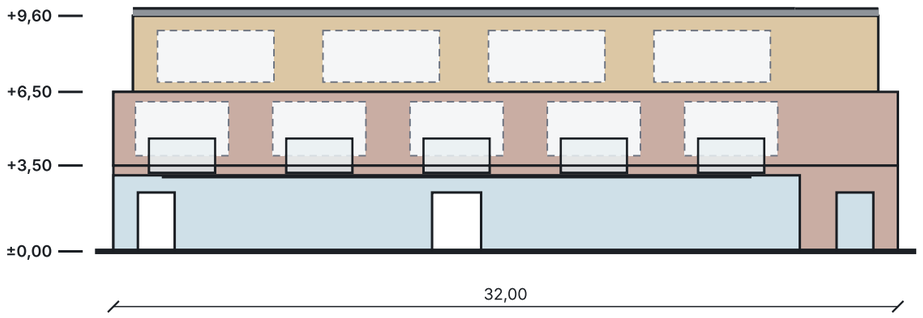


Ansicht Rückseite

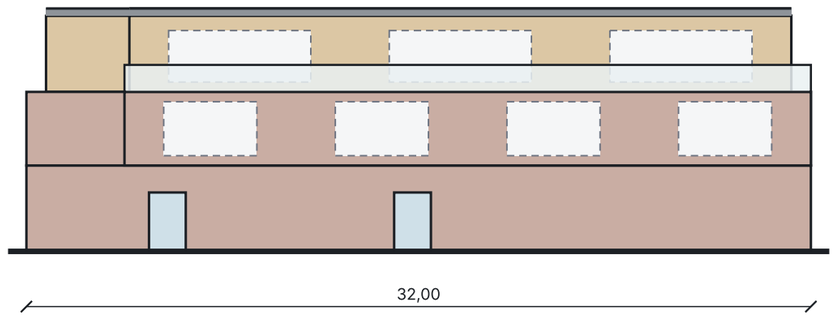


Höhen: ±0,00 Oberkante Erdgeschoss, +3,50 1. OG, +6,50 Traufe nach B-Plan und Staffel, +9,60 Staffeldecke, +9,90 Attika

Seitenansicht Kernseite (x = 0)

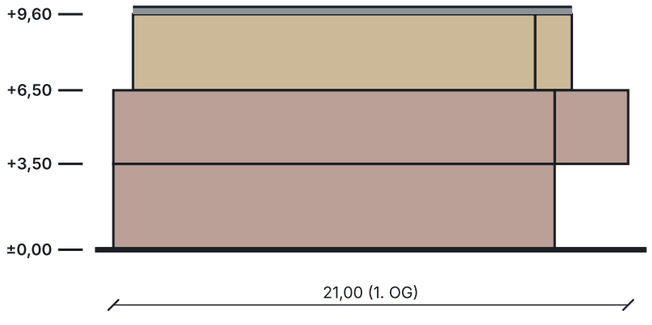

Seitenansicht Ostseite (x = 32)

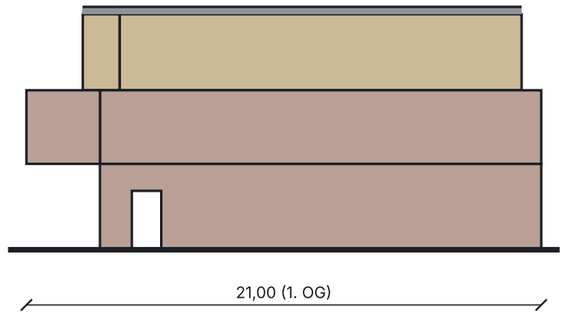

Kernseite: Platzfassade links, Rückseite rechts. Ostseite: Platzfassade rechts, Rückseite links. Himmelsrichtung unbekannt (C-13).

KENNZAHLEN

Gebäudetiefe Erdgeschoss	**18,00 m**
Tiefe 1. OG / Staffel	**21,00 / 17,90 m**
Höhe Attika	**9,90 m**
Dachterrasse hinten	**2,3 m tief**

LEGENDE

- Klinker, dunkelrotbraun (hier aufgehellt)
- Lärchenholz im Staffelgeschoss
- Betonbalkonplatte
- Milchglas-Brüstung, 1,10 m
- Glas und Türen
- Fensterlage schematisch (Maße offen)

OFFENE PUNKTE (NICHT GELÖST)

- **C-13** Himmelsrichtung und Platzseite unbekannt; Seiten sind nach dem Kern benannt.
- **C-19** Rückfassade, Seitenfassaden und Dachterrasse sind nicht Teil des eingefrorenen Designs.
- **C-30** Auskragung und Staffelung: Baufenster, GRZ und Abstände unbekannt.
- **C-35** Tragwerk der Auskragung.
- **C-22** Abluftführung über Dach (Austritt) ist nicht dargestellt.

HINWEISE

Der Anbau ist abgestuft: 1. OG weiter ausgekragt als die Staffel, dazwischen eine Dachterrasse. Die Rückseite folgt dem Material der Platzfassade (Klinker, Lärchenholz).

Die Seitenfassaden zeigen die Stufung von Erdgeschoss, 1. OG und Staffel.

Die bestehende Platzfassade (dunkler Klinker, Holz, fünf Balkone) bleibt die Grundlage.

Neue Mitte Werlte · Baufeld 3

Bauvorhaben: Restaurant und Bar, Büros, Wohnungen

Ansichten Variante B

Maßstab 1:250 (A3)


Stand 22.10.2026 · Modell NEUE_MITTE_MASTER_DRAFT_A_003

VORLÄUFIGER ARBEITSSTAND – nicht freigegeben

Variante C – maximal sinnvoll erweitert, abgestuft (4,50 m / 2,00 m)

Grundrisse und Schnitt M 1:250 · HYPOTHETISCH: Grundstücksform, Baufenster und Rechtsfragen sind nicht belegt


Erdgeschoss 32 × 18 m mit Stellplätzen

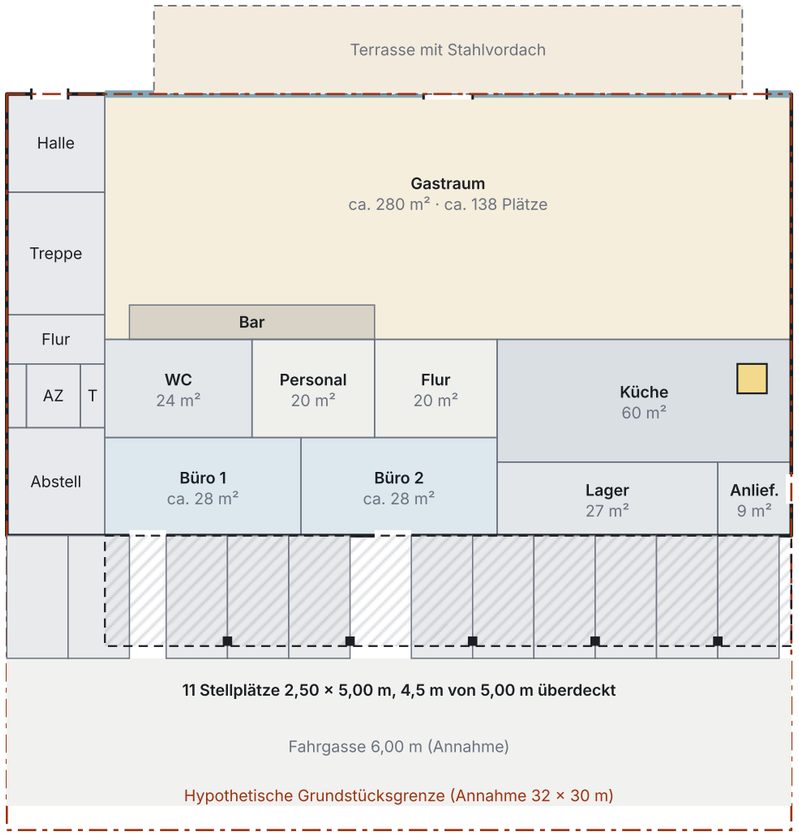


1. Obergeschoss (nur Wohnungen)



Schnitt bei x = 17,00 m

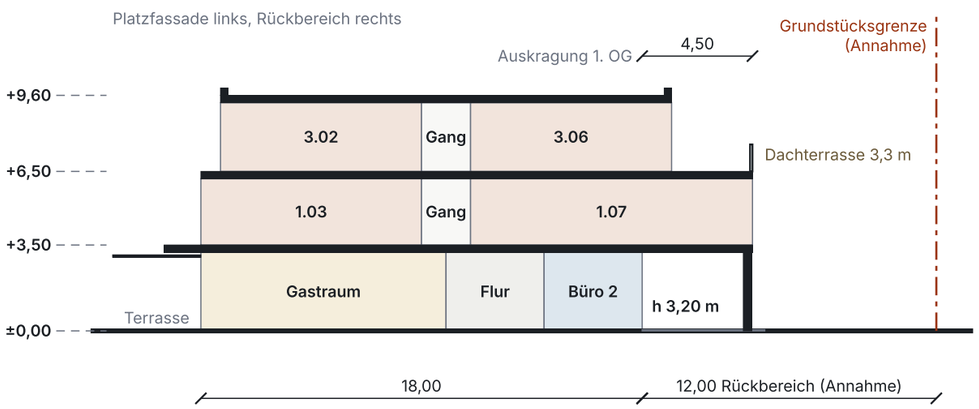

3. Geschoss, Staffel (nur Wohnungen)

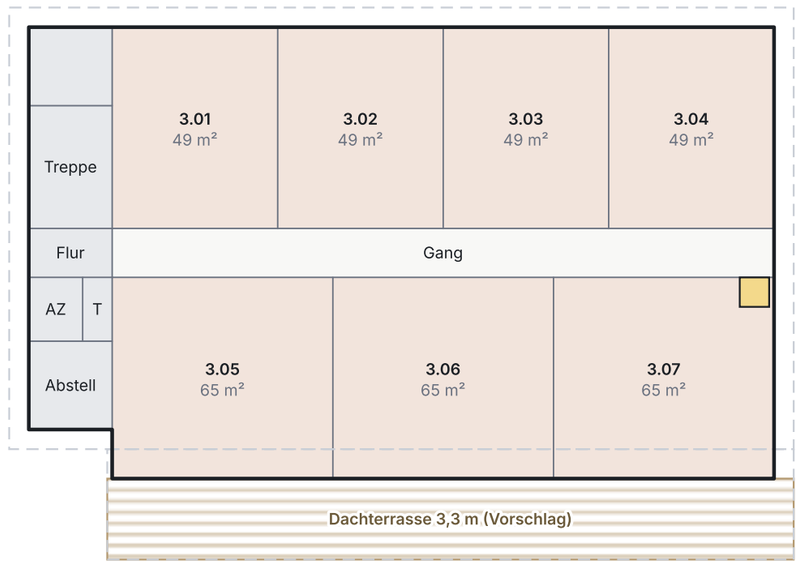

KENNZAHLEN

Außenmaß EG / 1. OG / 3. Geschoss	**32×18 / 32×22,5 / 30,4×18,4 m**
Auskragung 1. OG / Überstand Staffel	**4,50 / 2,00 m**
Gastronomie brutto, Innenplätze	**ca. 440 m², ca. 138**
Büros hinten, netto	**ca. 56 m²**
Wohnungen, Wohnfläche netto	**16, ca. 895 m²**
Stellplätze, überdeckt	**11, 4,5 von 5,0 m Tiefe**

LEGENDE

- Wohnung, Nummer nach Geschoss (1.xx, 3.xx), Wohnfläche netto
- Büro (EG, hinten)
- Gastraum und Bar
- Küche, Lager, WC, Personal, Anlieferung (Anlief.)
- Kern: Halle, Treppe, Flur, Abstell (AZ Aufzug, T Technik)
- Auskragung über Stellplätzen (hypothetisch)
- Dachterrasse auf dem 1. OG (Vorschlag)
- Küchenabluft-Schacht, alle Geschosse

OFFENE PUNKTE (NICHT GELÖST)

- **C-30** Baufenster, GRZ und Zählung von Auskragungen unbekannt; Projektion 702 m² gegen theoretisch 576 m²: nicht nachweisbar zulässig.
- **C-28** Stellplatzbedarf 61 laut Excel, hier 11 nachweisbar (Annahme).
- **C-29** Grundstückszuschnitt, Zufahrt und Anlieferung unbekannt (hier 32 × 30 m angenommen).
- **C-37** Büros 56 m² statt 165 m²: Mieteinnahmen und Gastro-Pacht nicht neu gerechnet.
- **C-35** Tragwerk der Auskragung und der 5 Stützen.

HINWEISE

Erdgeschoss in allen Varianten gleich. Der Anbau ist abgestuft: 1. OG weiter ausgekragt als die Staffel, dazwischen eine Dachterrasse.

Flächen netto = Brutto × 0,88 (Annahme). Fenster, Türen und Wandstärken sind nicht festgelegt. Keine Variante ist festgelegt.

Neue Mitte Werlte · Baufeld 3

Bauvorhaben: Restaurant und Bar, Büros, Wohnungen

Variante C – Grundrisse und Schnitt

Maßstab 1:250 (A3)


Stand 22.10.2026 · Modell NEUE_MITTE_MASTER_DRAFT_A_003

VORLÄUFIGER ARBEITSSTAND – nicht freigegeben


Ansichten Variante C – maximal sinnvoll erweitert, abgestuft (4,50 m / 2,00 m)

Schematische Ansichten M 1:250 · Fenster- und Türlage schematisch, Maße nicht definiert · Material und Farbe unverändert

Ansicht Platzseite

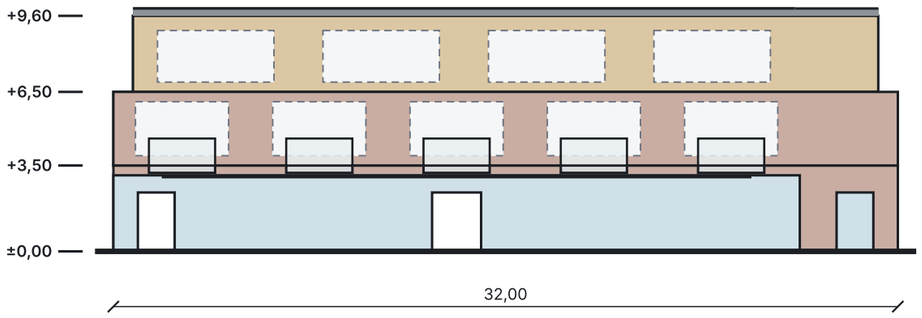


Ansicht Rückseite

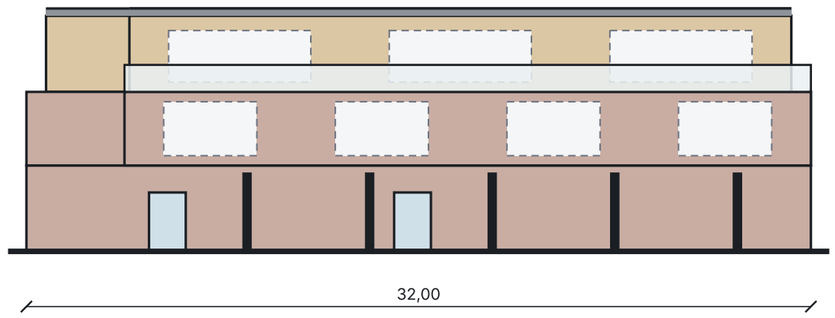


Höhen: ±0,00 Oberkante Erdgeschoss, +3,50 1. OG, +6,50 Traufe nach B-Plan und Staffel, +9,60 Staffeldecke, +9,90 Attika

Seitenansicht Kernseite (x = 0)

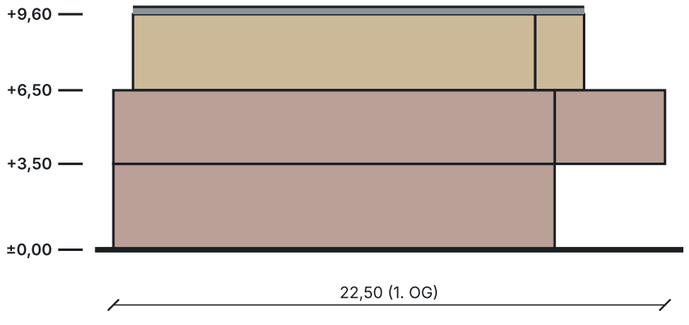

Seitenansicht Ostseite (x = 32)

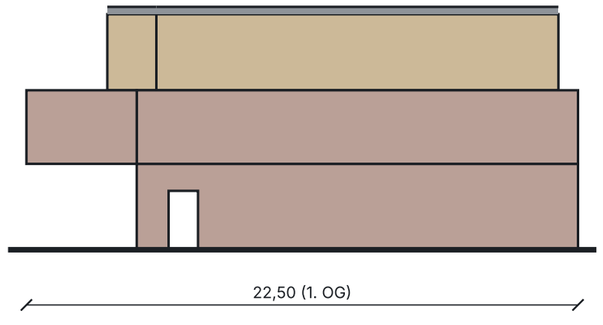

Kernseite: Platzfassade links, Rückseite rechts. Ostseite: Platzfassade rechts, Rückseite links. Himmelsrichtung unbekannt (C-13).

KENNZAHLEN

Gebäudetiefe Erdgeschoss	**18,00 m**
Tiefe 1. OG / Staffel	**22,50 / 18,40 m**
Höhe Attika	**9,90 m**
Dachterrasse hinten	**3,3 m tief**

LEGENDE

- Klinker, dunkelrotbraun (hier aufgehellt)
- Lärchenholz im Staffelgeschoss
- Betonbalkonplatte
- Milchglas-Brüstung, 1,10 m
- Glas und Türen
- Fensterlage schematisch (Maße offen)

OFFENE PUNKTE (NICHT GELÖST)

- **C-13** Himmelsrichtung und Platzseite unbekannt; Seiten sind nach dem Kern benannt.
- **C-19** Rückfassade, Seitenfassaden und Dachterrasse sind nicht Teil des eingefrorenen Designs.
- **C-30** Auskragung und Staffelung: Baufenster, GRZ und Abstände unbekannt.
- **C-35** Tragwerk der Auskragung und der Stützen.
- **C-22** Abluftführung über Dach (Austritt) ist nicht dargestellt.

HINWEISE

Der Anbau ist abgestuft: 1. OG weiter ausgekragt als die Staffel, dazwischen eine Dachterrasse. Die Rückseite folgt dem Material der Platzfassade (Klinker, Lärchenholz).

Die Seitenfassaden zeigen die Stufung von Erdgeschoss, 1. OG und Staffel.

Die bestehende Platzfassade (dunkler Klinker, Holz, fünf Balkone) bleibt die Grundlage.

Neue Mitte Werlte · Baufeld 3

Bauvorhaben: Restaurant und Bar, Büros, Wohnungen

Ansichten Variante C

Maßstab 1:250 (A3)

Stand 22.10.2026 · Modell NEUE_MITTE_MASTER_DRAFT_A_003

VORLÄUFIGER ARBEITSSTAND – nicht freigegeben

Vergleich der Varianten A, B und C (Version 2)

Gastronomie großzügig, Büros kompakt, Wohngeschosse abgestuft. Alle Werte hypothetisch und aus der Geometrie berechnet; keine Variante ist festgelegt.

Kriterium	A: moderat vergrößert	B: erweitert und abgestuft	C: maximal sinnvoll, abgestuft
Gebäudeform	Anbau 1,50 m; Staffel bündig mit EG-Rückwand; Dachterrasse 2,3 m	Anbau 3,00 m; Staffel 1,50 m kürzer; Treppenform mit Dachterrasse 2,3 m	Anbau 4,50 m; Staffel 2,00 m; Treppenform mit Dachterrasse 3,3 m; 5 Stützen
Außenmaße EG / 1. OG / 3. Geschoss	32 × 18 / 32 × 19,5 / 30,4 × 16,4 m	32 × 18 / 32 × 21,0 / 30,4 × 17,9 m	32 × 18 / 32 × 22,5 / 30,4 × 18,4 m
Projizierte Fläche (1. OG), GRZ-Zahl	618 m², 0,64 (Grenze theoretisch 576 m²)	660 m², 0,69 (Grenze theoretisch 576 m²)	702 m², 0,73 (Grenze theoretisch 576 m²)
Geschossfläche gesamt, Kubatur (Näherung)	BGF 1.693 m², BRI ca. 5.416 m³	BGF 1.775 m², BRI ca. 5.667 m³	BGF 1.831 m², BRI ca. 5.835 m³
Gastronomie brutto (Erdgeschoss)	ca. 440 m², davon Gastraum mit Bar 280 m²	ca. 440 m², davon Gastraum mit Bar 280 m²	ca. 440 m², davon Gastraum mit Bar 280 m²
Innenplätze (geschätzt) und Terrasse	ca. 138 innen (2,1 m² je Platz + 12 Barhocker), 60 Terrasse	ca. 138 innen (2,1 m² je Platz + 12 Barhocker), 60 Terrasse	ca. 138 innen (2,1 m² je Platz + 12 Barhocker), 60 Terrasse
Büros hinten im EG	2 Büros, ca. 56 m² netto (64 m² brutto)	2 Büros, ca. 56 m² netto (64 m² brutto)	2 Büros, ca. 56 m² netto (64 m² brutto)
Wohnungen (1. OG + 3. Geschoss)	9 + 7 = 16	9 + 7 = 16	9 + 7 = 16
Wohnungsgrößen netto (m²)	39, 43, 57, 58	39, 43, 68, 69	44, 49, 65, 71
Wohnfläche netto gesamt	ca. 773 m² (Excel-Stand 655 m²)	ca. 846 m² (Excel-Stand 655 m²)	ca. 895 m² (Excel-Stand 655 m²)
Zusätzliche Wohnfläche gegenüber A	–	+73 m² (+9 %)	+122 m² (+16 %)
Überdachte Stellplätze	11 Plätze, 1,5 von 5,0 m Tiefe überdeckt	11 Plätze, 3,0 von 5,0 m Tiefe überdeckt	11 Plätze, 4,5 von 5,0 m Tiefe überdeckt
Stützen, Rangierfläche, Durchfahrt	keine Stütze; Fahrgasse 6,00 m (192 m²); h 3,20 m	keine Stütze; Fahrgasse 6,00 m (192 m²); h 3,20 m	5 Stützen an der Auskragungskante; Fahrgasse 6,00 m; h 3,20 m
Wohnqualität	Vorn 5 Studios mit Balkon, hinten 4 Wohnungen 58 m²; Terrasse nur 2,3 m	Vorn wie A, hinten 4 Wohnungen 68 m², Staffel hinten 69 m²	Vorn 5 Wohnungen 44 m², hinten 71 m², Staffel 49 und 65 m²; Tiefe/Breite höchstens 1,64
Nachweisstatus	Projektion über 576 m²: nicht nachweisbar	Projektion über 576 m²: nicht nachweisbar	Projektion über 576 m²: nicht nachweisbar

KENNZAHLEN

Erdgeschoss **in allen Varianten 32 × 18 m**

OFFENE PUNKTE (NICHT GELÖST)

- C-30 Baufenster, GRZ und Zählung von Auskragungen sind unbekannt: alle drei Varianten übersteigen die theoretische GRZ-Fläche.
- C-28 Stellplätze: Bedarf 61, nachweisbar nur 11 (Annahme).
- C-29 Grundstückszuschnitt (hier 32 × 30 m angenommen), Zufahrt, Anlieferung unbekannt.
- C-37 Büros 56 m² statt 165 m²: Mieteinnahmen und Gastro-Pacht nicht neu gerechnet.
- C-35 Tragwerk der Auskragungen offen.

HINWEISE

Erdgeschoss in allen Varianten gleich. Gastronomie: Gastraum 280 m², Küche 60, Lager 27, WC 24, Personal 20, Flur 20, Anlieferung 9.

Wohnungsgrößen netto = Brutto × 0,88 (Annahme).

Keine Renderings, keine Förderthemen.

Neue Mitte Werlte · Baufeld 3

Bauvorhaben: Restaurant und Bar, Büros, Wohnungen

Vergleich der Varianten A, B und C

Tabelle

Stand 22.10.2026 · Modell NEUE_MITTE_MASTER_DRAFT_A_003

VORLÄUFIGER ARBEITSSTAND – nicht freigegeben