
Gastronomie – maßstäbliche Möblierung, Layout normal

Grundriss M 1:100 · Tische 1,20 × 0,80 m (4 Plätze), Stühle 0,45 × 0,45 m, 12 Barhocker · Maße ASSUMED

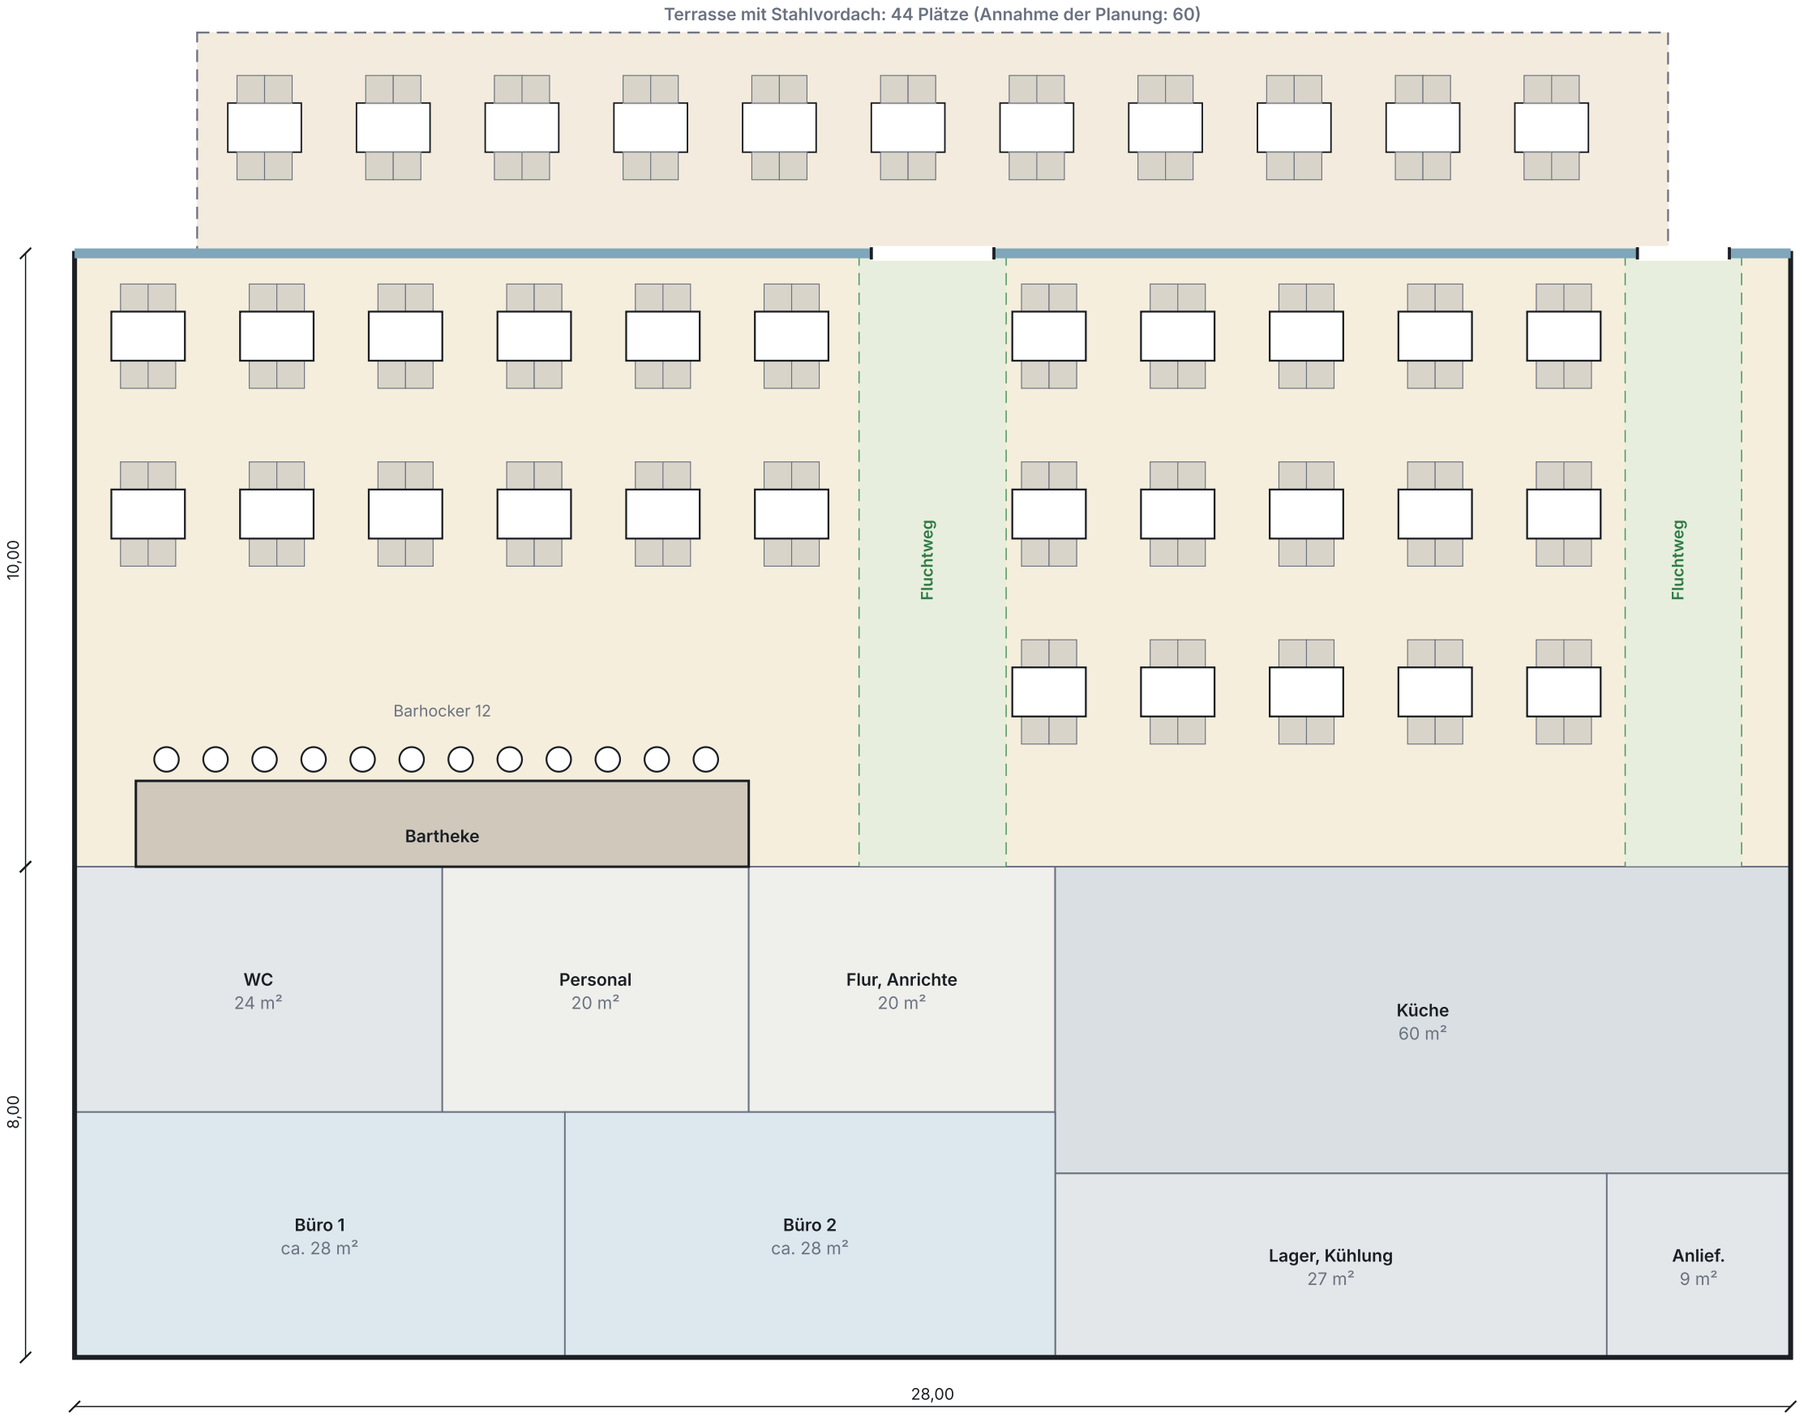

KENNZAHLEN

Gastraum und Bar	**280 m²**
Innenplätze realistisch (normal)	**120**
davon Barhocker	**12**
komfortabel / dicht	**88 / 128**
Flächenregel der letzten Fassung	**138**
Terrasse (normal)	**44**
Fläche je Platz (normal)	**2,3 m²**

LEGENDE

- Tisch 1,20 × 0,80 m, 4 Plätze
- Stuhl 0,45 × 0,45 m
- Barhocker
- Fluchtweg vor den Ausgängen, 2,40 und 1,90 m breit
- Terrasse

OFFENE PUNKTE (NICHT GELÖST)

- **C-20** Gaststätte mit über 120 + 44 Plätzen: Einstufung als Sonderbau, Zahl der Ausgänge und Rettungsbreiten offen.
- **C-36** Fluchtwege nur als Annahme; Küche und Personal über Flur und Anlieferung Ost.
- **C-38** Barrierefreie Plätze und Fahrbahn für Rollstühle noch nicht nachgewiesen.

HINWEISE

Die 138 Plätze der letzten Fassung waren eine Flächenregel (2,1 m² je Platz). Die Möblierung zeigt: realistisch sind etwa 120, komfortabel 88, sehr dicht 128. Die Gastronomie wird nicht weiter verkleinert.

Reihen im Layout normal: Reihe 1: 11 Tische, Reihe 2: 11 Tische, Reihe 3: 5 Tische.

Neue Mitte Werlte · Baufeld 3

Bauvorhaben: Restaurant und Bar, Büros, Wohnungen

Gastronomie – Möblierung

Maßstab 1:100 (A3)

Stand 22.10.2026 · Arbeitsgrundlage B3 (Variante B, nicht festgelegt)

VORLÄUFIGER ARBEITSSTAND – nicht freigegeben

Blatt 21