

Arbeitsgrundlage B3 – Grundrisse und Schnitt (Variante B, nicht festgelegt)

M 1:250 · Mittelgang bei y 9,50 m für ausgeglichene Wohnungstiefen · HYPOTHETISCH: Grundstücksform, Baufenster und Rechtsfragen nicht belegt


Erdgeschoss 32 × 18 m (Alternative K, Büro-Foyer im Kern)

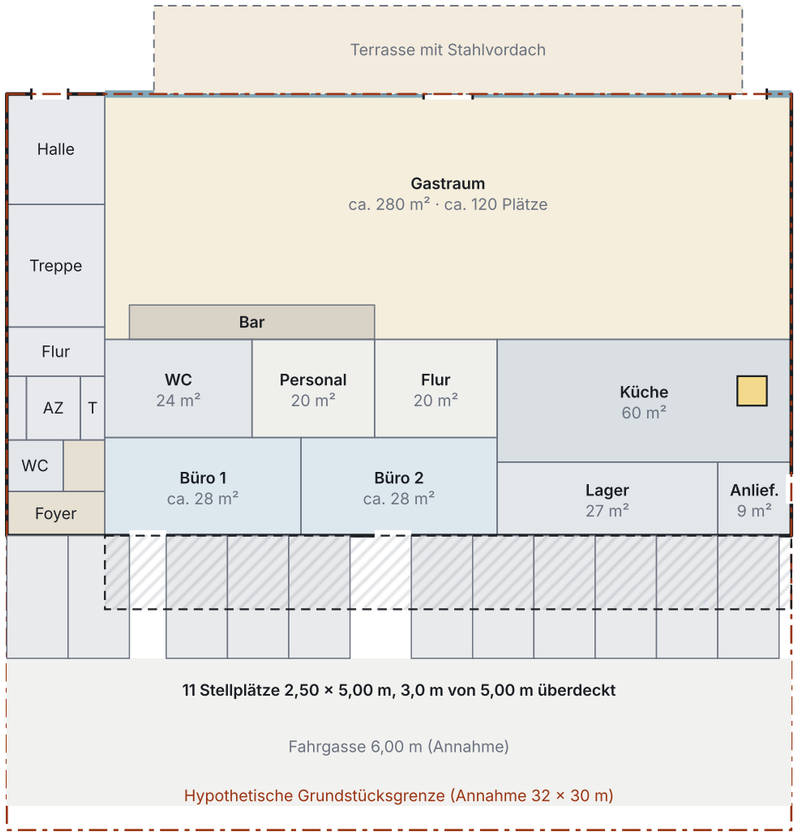


1. Obergeschoss (nur Wohnungen)

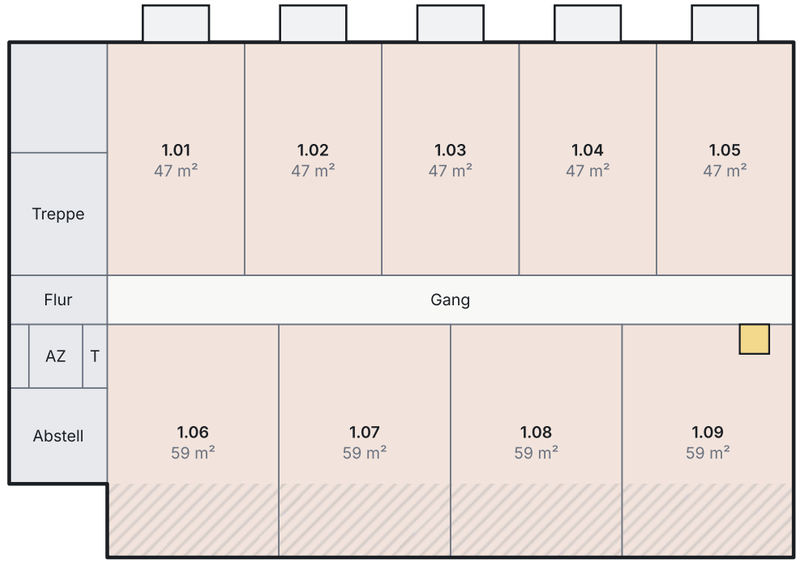

Schnitt bei x = 17,00 m

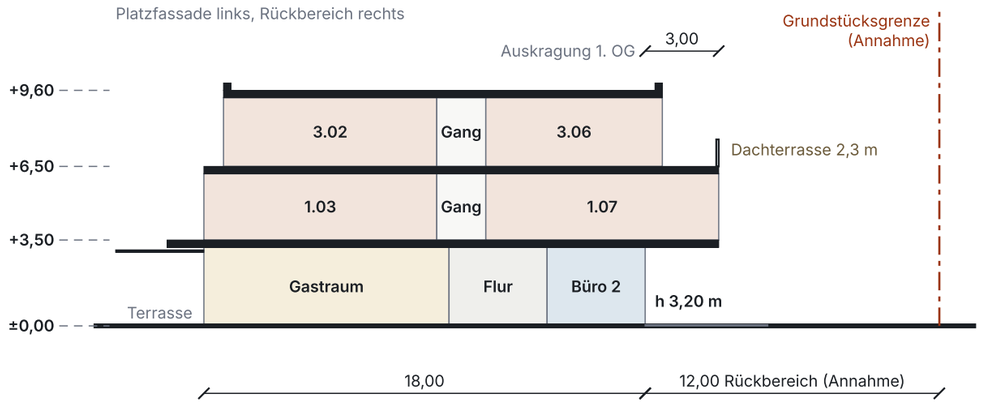

3. Geschoss, Staffel (nur Wohnungen)

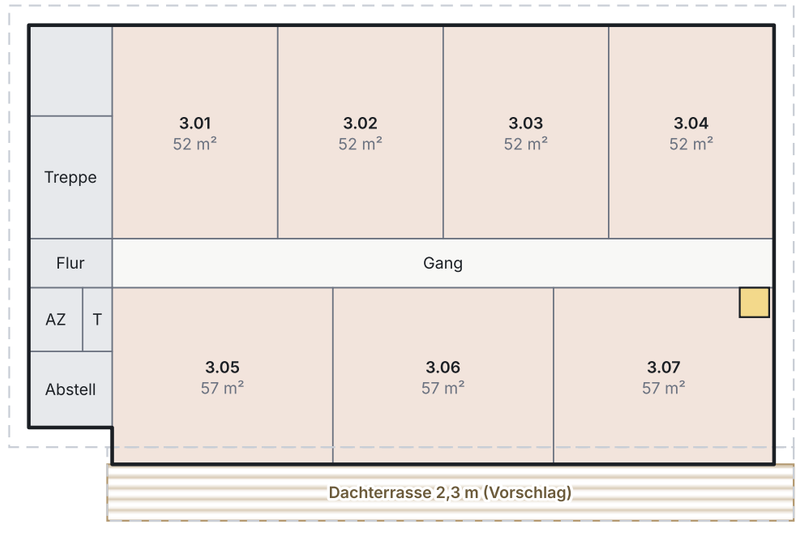

KENNZAHLEN

Außenmaß EG / 1. OG / 3. Geschoss	**32×18 / 32×21,0 / 30,4×17,9 m**
Anbau 1. OG / Überstand Staffel	**3,00 / 1,50 m**
Gastronomie, Innenplätze realistisch	**440 m², 120**
Büros, netto	**2 × 28 = 56 m²**
Wohnungen, Wohnfläche netto	**16, ca. 846 m²**
Dachterrasse hinten	**2,3 m tief**

LEGENDE

- Wohnung, Nummer nach Geschoss, Wohnfläche netto
- Büro
- Gastraum und Bar
- Küche, Lager, WC, Personal, Anlieferung
- Büro-Foyer
- Kern (AZ Aufzug, T Technik)
- Auskragung 1. OG über Stellplätzen
- Dachterrasse (Vorschlag)
- Küchenabluft-Schacht

OFFENE PUNKTE (NICHT GELÖST)

- **C-30** Baufenster, GRZ, Abstände, Zählung der Auskragung unbekannt; Projektion 660 m² gegen theoretisch 576 m².
- **C-28** Stellplatzbedarf und nachweisbare Stellplätze getrennt: siehe Blatt 26.
- **C-38** Abstell- und Fahrradraum Wohnen im EG entfällt (Alternative K).
- **C-22** Küchenabluft-Schacht läuft durch Wohnungen.

HINWEISE

Variante B ist nur Arbeitsgrundlage, nicht festgelegt. Gegenüber Version 2 liegt der Mittelgang bei y 9,50 m; die Wohnfläche ist unverändert.

Flächen netto = Brutto × 0,88 (Annahme). Fenster, Türen und Wandstärken nicht festgelegt.

Neue Mitte Werlte · Baufeld 3

Bauvorhaben: Restaurant und Bar, Büros, Wohnungen

Arbeitsgrundlage B3 – Grundrisse und Schnitt

Maßstab 1:250 (A3)

Stand 22.10.2026 · Arbeitsgrundlage B3 (Variante B, nicht festgelegt)

VORLÄUFIGER ARBEITSSTAND – nicht freigegeben