

Fassadenkonzept rundum – schematische Ansichten, Arbeitsgrundlage B3

Ansichten M 1:250 · Material und Farbe der Platzfassade unverändert · Fensterformate Vorschlag (ASSUMED), nicht freigegeben

Ansicht Platzseite (unverändert)

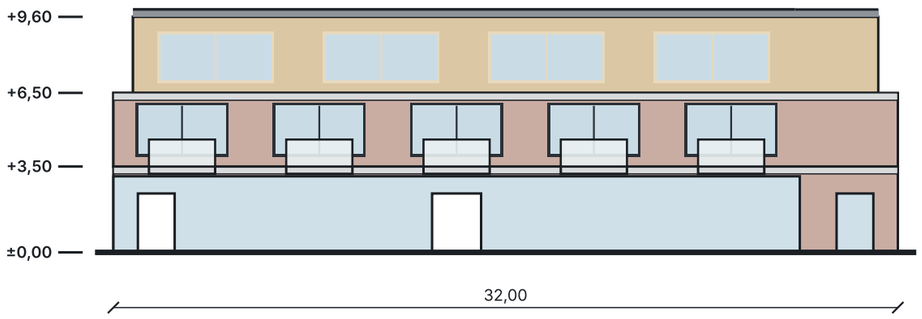


Ansicht Rückseite

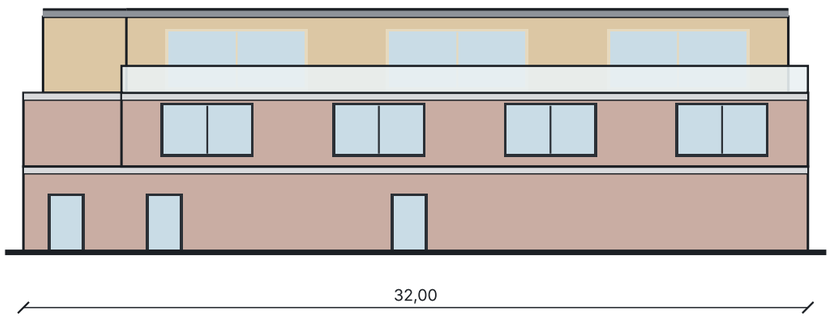


Höhen: ±0,00 Oberkante Erdgeschoss, +3,50 1. OG, +6,50 Traufe nach B-Plan und Staffel, +9,60 Staffeldecke, +9,90 Attika

Seitenansicht Kernseite (x = 0)

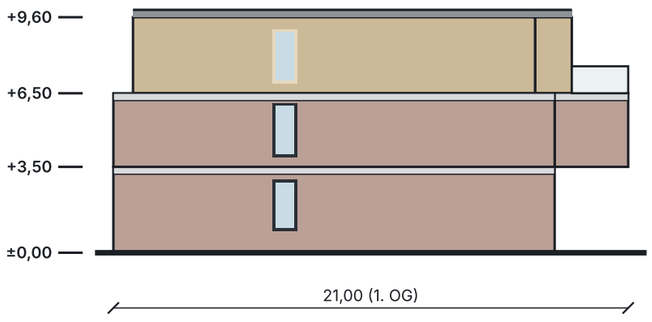

Seitenansicht Ostseite (x = 32)

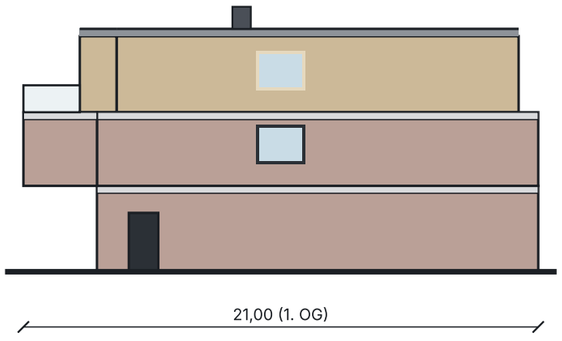

Kernseite: Platzfassade links, Rückseite rechts. Ostseite: Platzfassade rechts, Rückseite links. Himmelsrichtung unbekannt (C-13).

KENNZAHLEN

Tiefe EG / 1. OG / Staffel	**18,00 / 21,00 / 17,90 m**
Höhe Attika	**9,90 m**
Dachterrasse hinten	**2,3 m tief**

LEGENDE

- Klinker, dunkelrotbraun (hier aufgehellt)
- Betonbänder und Balkonplatten
- Lärchenholz Staffelgeschoss
- Milchglas-Brüstung, 1,10 m
- Glas, Türen
- schwarzer Stahlrahmen (Wohngeschoss, EG)
- helles Holzfenster (Staffel)

OFFENE PUNKTE (NICHT GELÖST)

- C-13 Himmelsrichtung und Platzseite unbekannt.
- C-19 Rückseite, Seiten und Dachterrasse sind nicht Teil des eingefrorenen Designs; hier ein Entwurfsvorschlag.
- C-30 Auskragung und Stufung: Baufenster, GRZ, Abstände und Höhen offen.
- C-35 Tragwerk der Auskragung (3,00 m, Sichtbeton-Untersicht).
- C-22 Abluftstutzen über dem Dach (Position offen).

HINWEISE

Gestaltungsregeln: Die Betonbänder der Platzfassade laufen um alle vier Seiten. Fensterachsen der Rückseite folgen den Wohnungsachsen, die Staffel hinten öffnet sich mit raumhohen Holzfenstern zur Dachterrasse.

Die Stufung ist ausgebildet: Auskragung mit Betonband, Dachterrasse mit Milchglas-Brüstung, Staffel in Lärchenholz. Kernseite mit Treppenhausschlitz, Ostseite mit Fenster am Gangende.

Neue Mitte Werlte · Baufeld 3

Bauvorhaben: Restaurant und Bar, Büros, Wohnungen

Fassadenkonzept rundum

Maßstab 1:250 (A3)

Stand 22.10.2026 · Arbeitsgrundlage B3 (Variante B, nicht festgelegt)

VORLÄUFIGER ARBEITSSTAND – nicht freigegeben