

# Büros hinten – Zugang, Büro-WC und Flur (drei Alternativen)

Grundrisse hinterer Erdgeschoss-Bereich M 1:150 · unabhängige Erreichbarkeit nur über die Rückseite, Fußweg vom Platz ungeklärt (C-29)


### Alternative K: Büro-Foyer im Kern

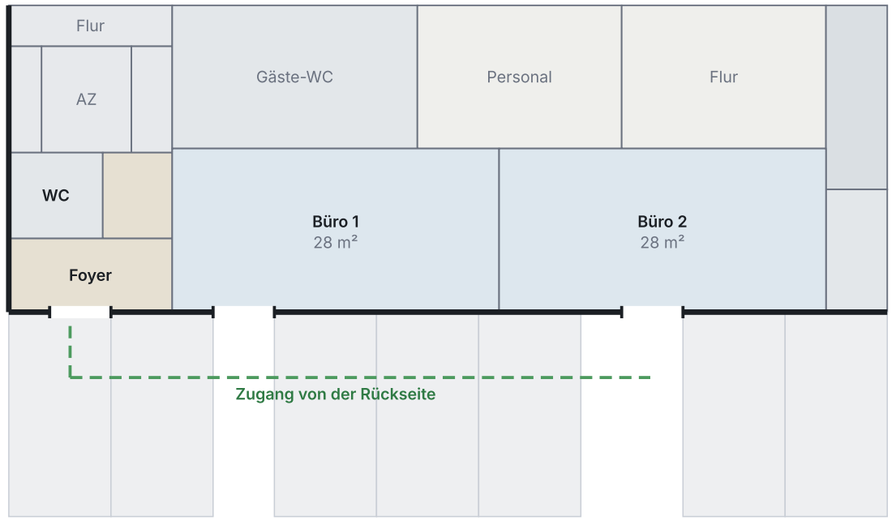


### Alternative F: Flur und WC zwischen den Büros

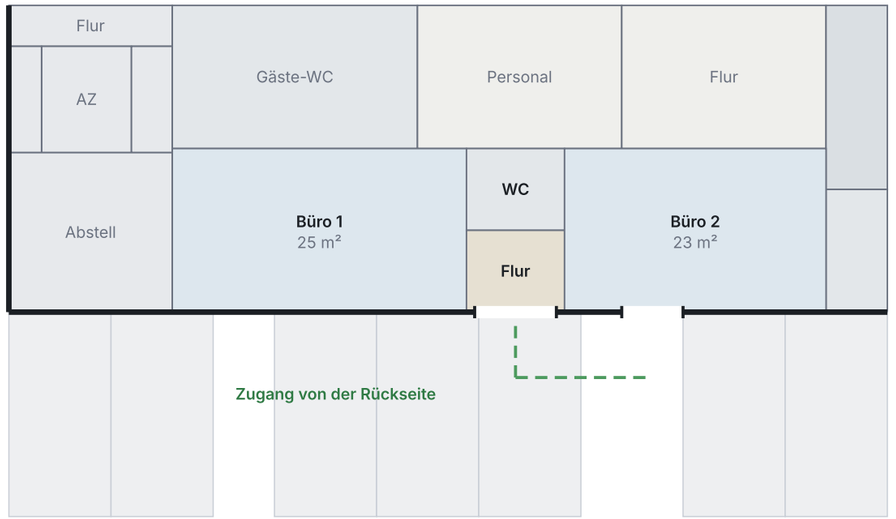


### Alternative M: Mitbenutzung des Gäste-WC

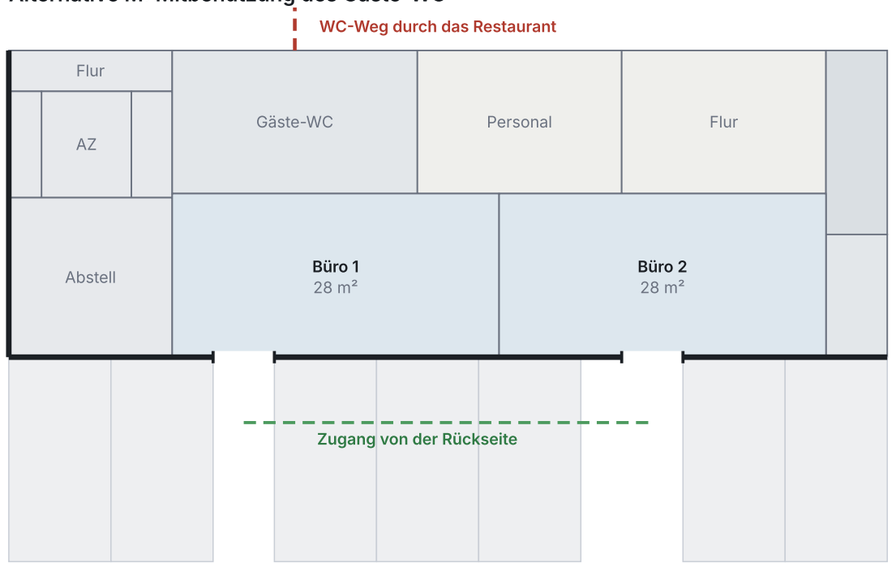


### Vergleich der Alternativen

| | K | F | M |
|---|---|---|---|
| **Gastronomie** | 440 m² | 440 m² | 440 m² |
| **Büros netto** | 56 m² | 48 m² | 56 m² |
| **Büro-WC** | im Foyer, 5 m² | zwischen Büros, 5 m² | Gäste-WC |
| **WC von beiden Büros erreichbar** | nur über außen | ja, innen | nur durch Restaurant |
| **unabhängig vom Restaurant** | ja (Rückseite) | ja (Rückseite) | nein (WC) |
| **Barrierefreier Zugang** | ja, eben | ja, eben | ja, eben |
| **Verlust** | Abstell Wohnen 16 m² | Bürofläche −8 m² | keiner |

Arbeitsstand: Alternative K (Büros bleiben je 28 m², Gastronomie unverändert). Sie kostet den Abstellraum Wohnen im Erdgeschoss; ein neuer Ort für Fahrrad und Abstell ist offen (C-38). Alternative F löst die Wege innen, verkleinert die Büros auf 25 und 22 m².

## KENNZAHLEN

| | |
|---|---|
| Büro 1 und 2 (K) | **je ca. 28 m² netto** |
| Foyer mit Büro-WC (K) | **ca. 16 m² brutto** |

## LEGENDE

- Büro
- Büro-Foyer, Büro-Flur
- WC
- Weg von der Rückseite
- Weg durch das Restaurant

## OFFENE PUNKTE (NICHT GELÖST)

- C-32 Büros nur rückseitig belichtet und erschlossen; Büro-WC jetzt in drei Alternativen geprüft.
- C-29 Fußweg vom Platz zur Rückseite und Grundstückszuschnitt unbekannt: unabhängige Erreichbarkeit nur unter dieser Voraussetzung.
- C-38 Abstell- und Fahrradraum Wohnen: neuer Ort offen.
- C-36 Fluchtwege der Büros: Rücktüren, nicht geprüft.

## HINWEISE

Gastronomie bleibt bei 440 m²; keine Fläche wird ohne Alternativen abgegeben.

Flächen netto = Brutto × 0,88 (Annahme). Türen und Wandstärken nicht festgelegt.

**Neue Mitte Werlte · Baufeld 3**

Bauvorhaben: Restaurant und Bar, Büros, Wohnungen

## Büros – Zugang, WC und Flur

Maßstab 1:150 (A3)

Stand 22.10.2026 · Arbeitsgrundlage B3 (Variante B, nicht festgelegt)

VORLÄUFIGER ARBEITSSTAND – nicht freigegeben